PROJEKT 01 / REFERENCIA

Rodinný dom Slivník (RD Imričko)

Vykurovanie (ÚK) | Projekt stavby (PSP) | Slivník, okr. Trebišov

Moderný návrh ústredného kúrenia pre novostavbu rodinného domu. Projekt v sebe spája detailný výpočet tepelných strát a ziskov podľa STN EN 12831 s optimalizovaným návrhom zdroja tepla a precíznym dimenzovaním rozvodných potrubí a podlahových vykurovacích okruhov.


TECHNICKÉ PARAMETRE

Vykurovací systém	**Teplovodné podlahové**
Výpočtová tepelná strata	**11,50 kW**
Tepelné zisky objektu	**5,40 kW**
Vonkajšia výpočt. teplota	**-13 °C**
Ročná spotreba tepla	**21,52 MWh/rok**
Normový rámec	**STN EN 12831, 12828**

VÝKRESOVÁ DOKUMENTÁCIA

- Pôdorys rozvodov podlahového vykurovania 1.NP
- Hydraulická schéma zapojenia a rozdeľovačov
- Podrobná technická správa a dimenzovanie

VÝKRES Č. 01: PÔDORYS ROZVODOV VYKUROVANIA 1.NP — MIERKA 1:50

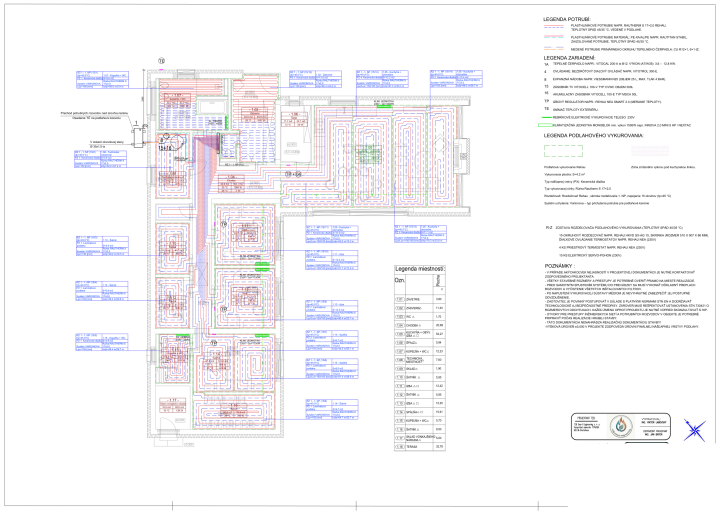

VÝKRES Č. 02: HYDRAULICKÁ SCHÉMA ROZVODOV A ZAPOJENIA ÚK — SCHÉMA

