LEGENDA PODLAHOVÉHO VYKUROVANIA:

PODLAHOVÉ KÚRENIE REHAU

Lpz=100 [mm]	ROZOSTUP VYK. RÚROK
S=8,6 m2	VYKUROVACIA PLOCHA
PX: Keramická dlažba	TYP NÁŠLAPNEJ VRSTVY
Rúrka RAUTHERM S 17x2,0	TYP VYKUROVACEJ RÚRKY
Nast.=0,63 (48 kg/h)	NASTAVENIE REG. OKRUHU(PRIETOK)
lo/lp=12.7 m/1.6 m	Dĺžka okruhu / dĺžka prípojky
RZ 1. NP-1/9 (tp=45°C)	rozdelovač na 1.NP 1. napojenie a
VARIONOVA	9 vetiev (tp - teplota prívodu)
PZ:21°C	typ prichytenia potrubi pre podlahove kurenie maximálna povrchová teplota podlahovej zóny

RZ 1 - 1. NP (9)

ROZDELOVACIA STANICA PRE PODLAHOVÉ VYKUROVANIE 45/35°C
NAPR. FY. REHAU HKV-D 9, SKRINKA ROZDELOVAČA NA STENU AP 130/805 (805x730x130mm)
REGULAČNÝ ROZVÁDZAČ REHAU NEA (230V) (1ks)
PRIESTOROVÝ TERMOSTAT REHAU NEA (230V) (2ks)
ELEKTRICKÝ SERVOPOHON REHAU (230V) (9ks)


RZ 2 - 1. NP (4)

ROZDELOVACIA STANICA PRE PODLAHOVÉ VYKUROVANIE 45/35°C
NAPR. FY. REHAU HKV-D 4, SKRINKA ROZDELOVAČA NA STENU AP 130/605 (605x730x130mm)
REGULAČNÝ ROZVÁDZAČ REHAU NEA (230V) (1ks)
ELEKTRICKÝ SERVOPOHON REHAU (230V) (4ks)

- 1.01 -	
Vstup	
2.0 m2	5.8 m3
20 °C	136 W
- 1.02 -	
Kancelária	
38.4 m2	109.2 m3
22 °C	1467 W
- 1.03 -	
Kuchynka	
6.0 m2	17.1 m3
22 °C	327 W
- 1.04 -	
WC	
2.5 m2	7.1 m3
22 °C	129 W
- 1.05 -	
Sklad	
69.9 m2	198.6 m3
20 °C	3195 W
- 1.06 -	
Školiaca miestnosť	
45.7 m2	129.9 m3
22 °C	1701 W
- 1.07 -	
Technická miestnosť	
7.3 m2	20.8 m3
24 °C	541 W
- 1.08 -	
Sprcha	
1.8 m2	5.1 m3
24 °C	132 W

LEGENDA MIESTNOSTÍ

Č.MIEST.	POPIS MIESTNOSTI	PLOCHA	PODLAHA	STENY	STROP
1.01	VSTUP	2,04 m2	P1 VINYL	INT. NÁTER	PLNÝ SDK PODHLAD
1.02	KANCELÁRIA	38,44 m2	P1 VINYL	INT. NÁTER	PLNÝ SDK PODHLAD
1.03	KUCHYNKA	6,03 m2	P1 VINYL	INT. NÁTER	PLNÝ SDK PODHLAD
1.04	WC	2,50 m2	P3 KERAM. DLAŽBA	KERAM. OBKLAD	PLNÝ SDK PODHLAD
1.05	SKLAD	70,68 m2	P3 EPOXIDOVÁ PODL.	INT. NÁTER	BEZ PODHLADU
1.06	ŠKOLIACA MIESTNOSŤ	45,74 m2	P1 VINYL	INT. NÁTER	PLNÝ SDK PODHLAD
1.07	TECHNICKÁ MIESTNOSŤ	7,33 m2	P3 EPOXIDOVÁ PODL.	INT. NÁTER	PLNÝ SDK PODHLAD
1.08	SPRCHA	1,80 m2	P3 KERAM. DLAŽBA	KERAM. OBKLAD	PLNÝ SDK PODHLAD
	CELKOVÁ PLOCHA / TOTAL AREA	174,56 m2			
1.09	TERASA	29,15 m2	DREVENÁ TERASA	–	–

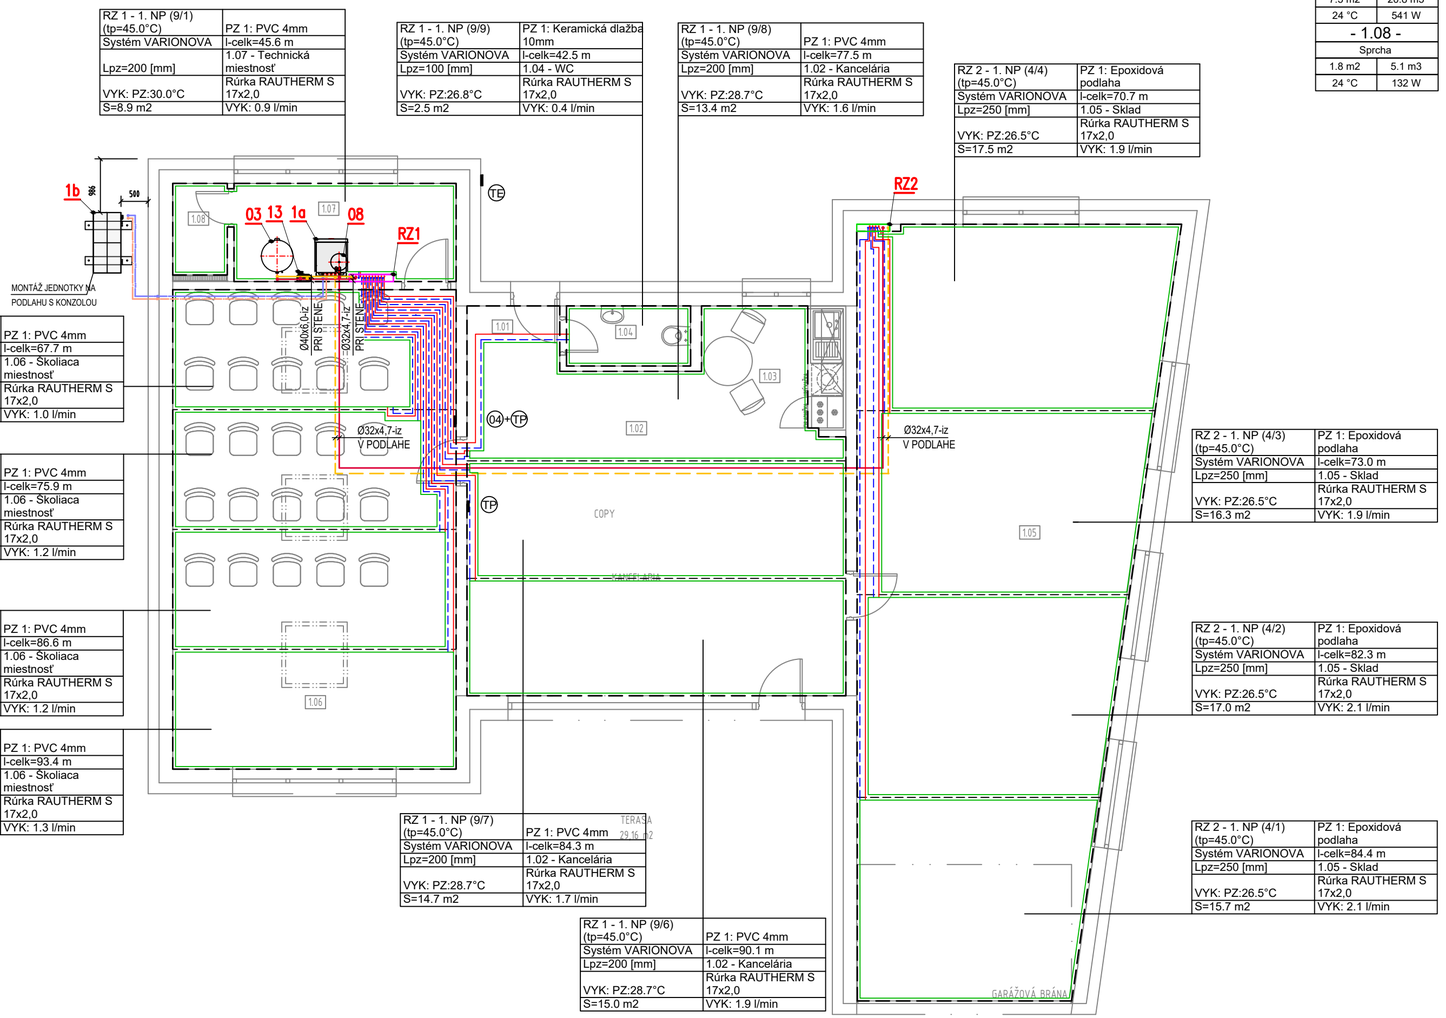

RZ 1 - 1. NP (9/1) (tp=45.0°C)	PZ 1: PVC 4mm
Systém VARIONOVA	l-celk=45.6 m
Lpz=200 [mm]	1.07 - Technická miestnosť
VYK: PZ:30.0°C	Rúrka RAUTHERM S 17x2,0
S=8.9 m2	VYK: 0.9 l/min

RZ 1 - 1. NP (9/2) (tp=45.0°C)	PZ 1: PVC 4mm
Systém VARIONOVA	l-celk=67.7 m
Lpz=150 [mm]	1.06 - Školiaca miestnosť
VYK: PZ:28.3°C	Rúrka RAUTHERM S 17x2,0
S=8.9 m2	VYK: 1.0 l/min

RZ 1 - 1. NP (9/3) (tp=45.0°C)	PZ 1: PVC 4mm
Systém VARIONOVA	l-celk=75.9 m
Lpz=150 [mm]	1.06 - Školiaca miestnosť
VYK: PZ:28.3°C	Rúrka RAUTHERM S 17x2,0
S=10.2 m2	VYK: 1.2 l/min

RZ 1 - 1. NP (9/4) (tp=45.0°C)	PZ 1: PVC 4mm
Systém VARIONOVA	l-celk=86.6 m
Lpz=150 [mm]	1.06 - Školiaca miestnosť
VYK: PZ:28.3°C	Rúrka RAUTHERM S 17x2,0
S=11.1 m2	VYK: 1.2 l/min

RZ 1 - 1. NP (9/5) (tp=45.0°C)	PZ 1: PVC 4mm
Systém VARIONOVA	l-celk=93.4 m
Lpz=150 [mm]	1.06 - Školiaca miestnosť
VYK: PZ:28.3°C	Rúrka RAUTHERM S 17x2,0
S=11.4 m2	VYK: 1.3 l/min

RZ 1 - 1. NP (9/9) (tp=45.0°C)	PZ 1: Keramická dlažba 10mm
Systém VARIONOVA	l-celk=42.5 m
Lpz=100 [mm]	1.04 - WC
VYK: PZ:26.8°C	Rúrka RAUTHERM S 17x2,0
S=2.5 m2	VYK: 0.4 l/min

RZ 1 - 1. NP (9/8) (tp=45.0°C)	PZ 1: PVC 4mm
Systém VARIONOVA	l-celk=77.5 m
Lpz=200 [mm]	1.02 - Kancelária
VYK: PZ:28.7°C	Rúrka RAUTHERM S 17x2,0
S=13.4 m2	VYK: 1.6 l/min

RZ 1 - 1. NP (9/7) (tp=45.0°C)	PZ 1: PVC 4mm
Systém VARIONOVA	l-celk=84.3 m
Lpz=200 [mm]	1.02 - Kancelária
VYK: PZ:28.7°C	Rúrka RAUTHERM S 17x2,0
S=14.7 m2	VYK: 1.7 l/min

RZ 1 - 1. NP (9/6) (tp=45.0°C)	PZ 1: PVC 4mm
Systém VARIONOVA	l-celk=90.1 m
Lpz=200 [mm]	1.02 - Kancelária
VYK: PZ:28.7°C	Rúrka RAUTHERM S 17x2,0
S=15.0 m2	VYK: 1.9 l/min

RZ 2 - 1. NP (4/4) (tp=45.0°C)	PZ 1: Epoxidová podlaha
Systém VARIONOVA	l-celk=70.7 m
Lpz=250 [mm]	1.05 - Sklad
VYK: PZ:26.5°C	Rúrka RAUTHERM S 17x2,0
S=17.5 m2	VYK: 1.9 l/min

RZ 2 - 1. NP (4/3) (tp=45.0°C)	PZ 1: Epoxidová podlaha
Systém VARIONOVA	l-celk=73.0 m
Lpz=250 [mm]	1.05 - Sklad
VYK: PZ:26.5°C	Rúrka RAUTHERM S 17x2,0
S=16.3 m2	VYK: 1.9 l/min

RZ 2 - 1. NP (4/2) (tp=45.0°C)	PZ 1: Epoxidová podlaha
Systém VARIONOVA	l-celk=82.3 m
Lpz=250 [mm]	1.05 - Sklad
VYK: PZ:26.5°C	Rúrka RAUTHERM S 17x2,0
S=17.0 m2	VYK: 2.1 l/min

RZ 2 - 1. NP (4/1) (tp=45.0°C)	PZ 1: Epoxidová podlaha
Systém VARIONOVA	l-celk=84.4 m
Lpz=250 [mm]	1.05 - Sklad
VYK: PZ:26.5°C	Rúrka RAUTHERM S 17x2,0
S=15.7 m2	VYK: 2.1 l/min

LEGENDA POTRUBIA:

POTRUBIE - PLASTHLINNÍKOVÁ RÚRKA RAUTHERM S 17x2,0, fy. REHAU
PRE OKRUHY PODLAHOVÉHO VYKUROVANIA, TEPLOTNÝ SPÁD 45/35°C

POTRUBIE - PLASTHLINNÍKOVÁ RÚRKA PE-Xa/AL/PE napr. RAUTITAN STABIL
SPÁJANÉ LISOVANÍM, IZOLOVANÉ POTRUBIE, TEPLOTNÝ SPÁD 45/35°C
POTRUBIE VEDENÉ V PODLAHE, PRE PODLAHOVÉ VYKUROVANIE

ROZVOD ÚK PRE PRIMÁRNY OKRUH TEPELNÉHO ČERPADLA
MATERIÁL MEĎ

LEGENDA ZARIADENÍ A ARMATÚR :

1a	KOMPAKTNÁ VNÚTORNÁ JEDNOTKA TEPELNÉHO ČERPADLA VITOCAL 222-S AWBT-M-E 221.E08
1b	VONKAJ.JEDNOTKA VITOCAL 222-S AWBT-M-E 221.E08 (230V)
	MAX.VÝSTUPNÁ TEPLOTA 60°C,TEPELNY VYKON 2,6-9kW A7/W35
	EKOLOGICKE CHLADIVO R32, REGULÁCIA ONE-BASE,WIFI (Z022722)
03	AKUMULACNY ZASOBNIK VITOCELL 100-W TYP SVWA 200L
04	BEZDRÔDOTVÉ DIAĽKOVÉ OVLÁDANIE VITOTROL 300-E
08	UZAVRETÁ TLAKOVÁ EXPANZNÁ NÁDOBA VIESSMANN N25 OBJEM 25L, 3bar
	ROZMERY : Ø=308 mm, VÝŠKA 477 mm , HMOTNOSŤ 4,3 kg + NASTENNY DRZIAK PRE N25 (9572216)
TP	PRIESTOROVÝ REGULÁTOR NEA SMART 2.0 PRE MERANIE TEPLOTY V MIESTNOSTI, FY. REHAU
TE	SNÍMAČ VONKAJŠEJ TEPLOTY
13	RYCHLOMONT.SADA SO ZMIESAVACOM M32 DN25 ALPHA2+(7741079)
	UPEVNENIE NA STENU PRE RMS DN25 (7741097)

POZNÁMKA :

- V PRÍPADE NEJASNOSTÍ VO VÝKRESOVEJ DOKUMENTÁCII KONTAKTOVAŤ ZODPOVEDNÉHO PROJEKTANTA
- VŠETKY ROZMERY STAVEBNÝCH PRÁC KONTROLOVAŤ NA MIESTE STAVBY
- PRED UVEDENÍM SYSTÉMU DO PREVÁDZKY JE POTREBNÉ VYKONAŤ DÔKLADNÝ PREPLACH SYSTÉMU S VYČISTENÍM VŠETKÝCH FILTROV NA ROZVODE
- PO NAPUSTENÍ SYSTÉMU JE POTREBNÉ VYKONAŤ JEHO ODVZDUŠNENIE
- DODÁVATEL STAVBY JE POVINNÝ REALIZOVAŤ VŠETKY PRÁCE V ZMYSLE PLATNÝCH STN EN S DODRŽANÍM TECHNOLOGICKÝCH A BEZPEČNOSTNÝCH POSTUPOV. ĎALEJ JE POVINNÝ REŠPEKTOVAŤ USTANOVENIÁ STN 730421 O PRÍSLUŠNÝCH ROZMEROVÝCH ODCHÝLKACH REALIZOVANÝCH KONŠTRUKCIÍ PROTI PROJEKTOVANÉMU STAVU. KAŽDÚ ODCHÝLKU OD PROJEKTU JE POTREBNÉ PREROKOVAŤ S GP.

±0,000 = úroveň 1.N.P. = 126,40 m.n.m.