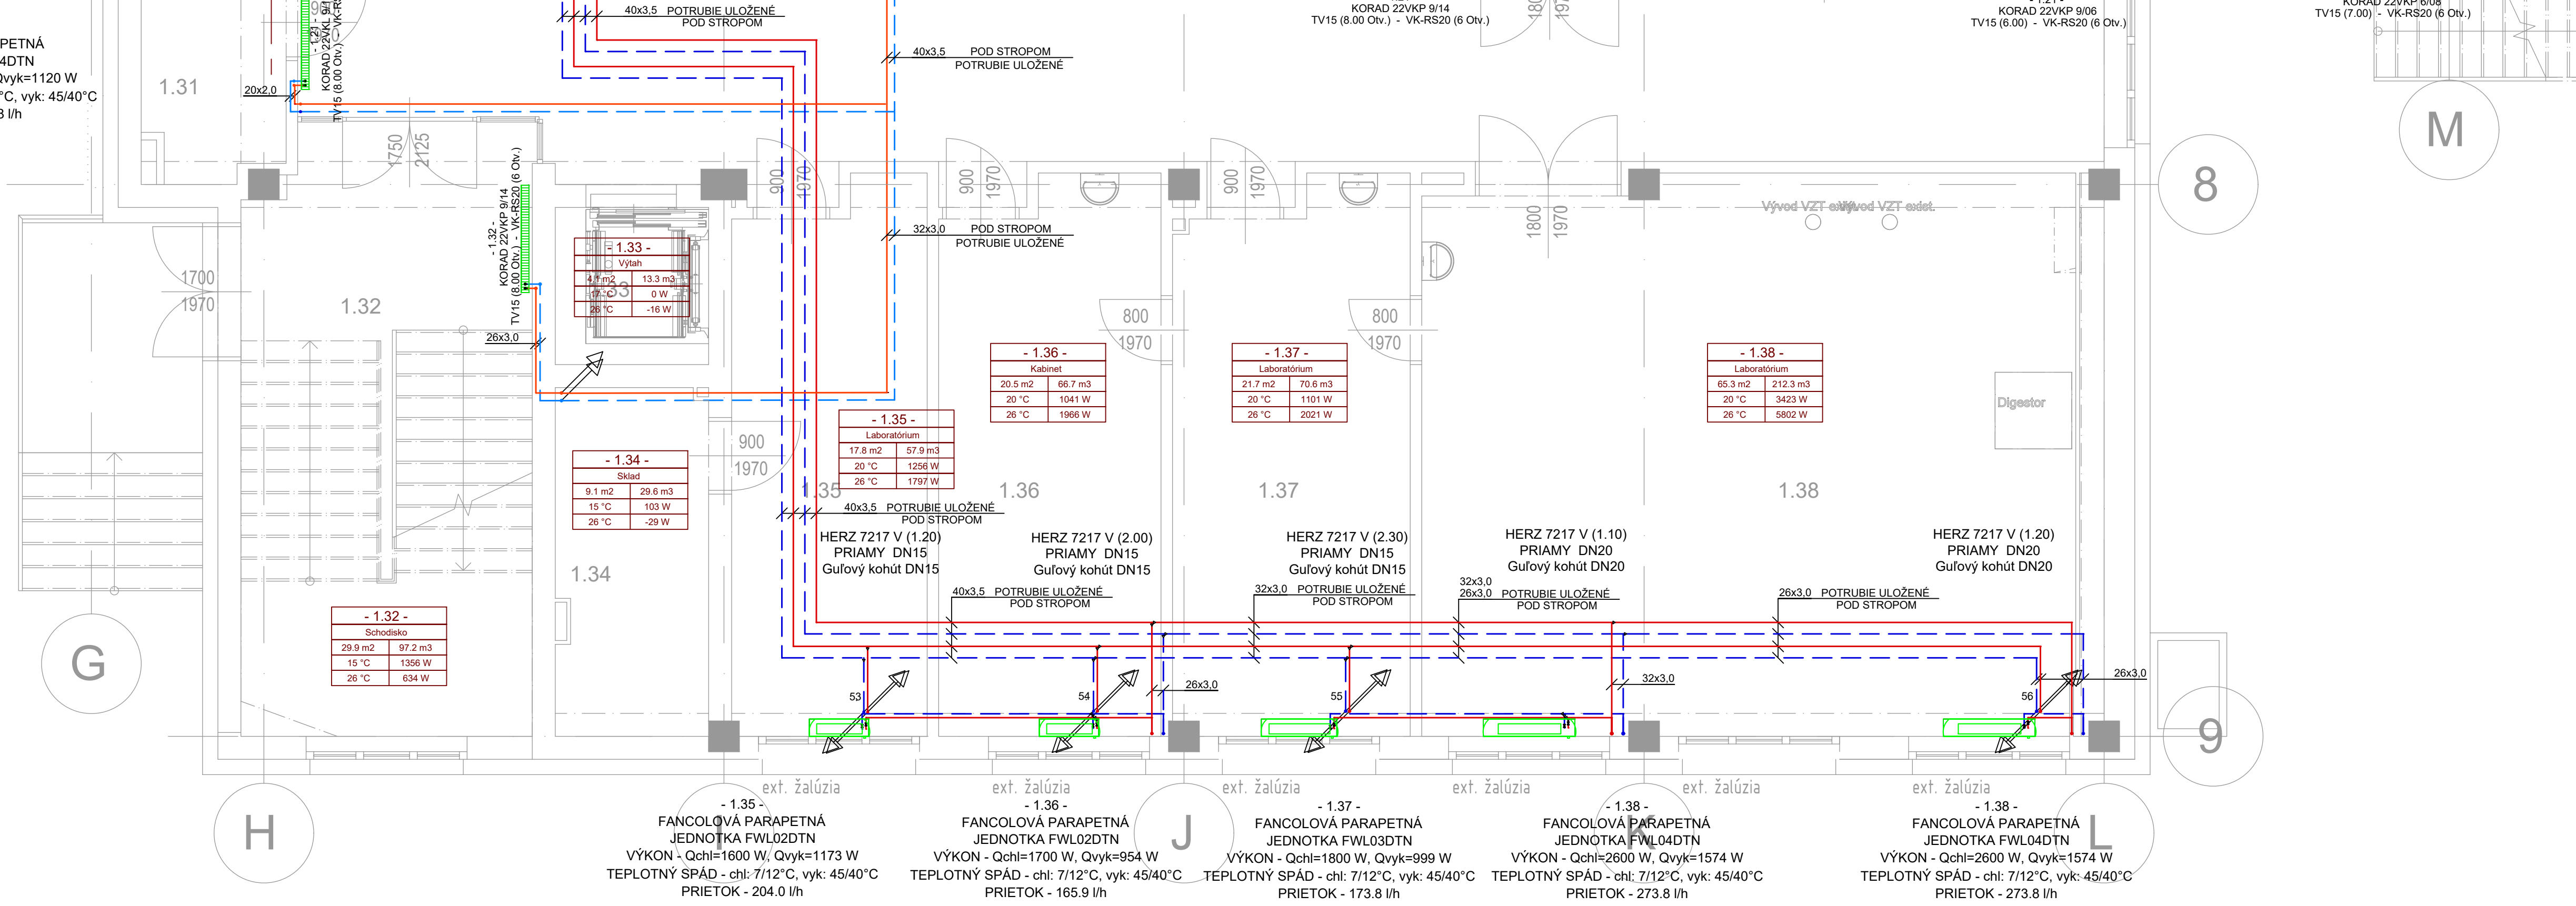

DOSKOVÉ VYKUROVACIE TELESO

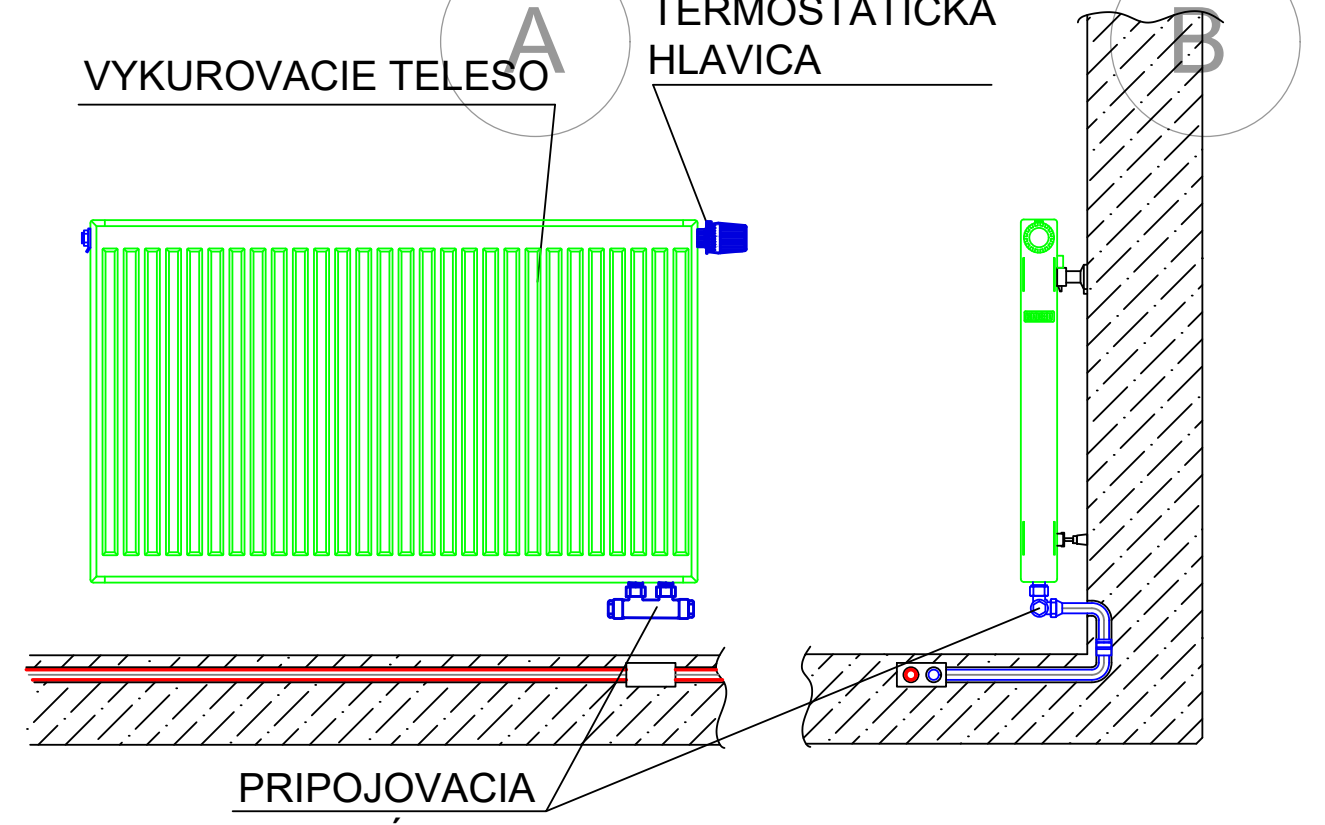

L.M. 1.NP - fakulta		
Č.M.	Názov	Plocha
1.01	Vstupná hala	55.20 m²
1.02	Bufet + kaviareň	64.16 m²
1.04	Výťah	3.47 m²
1.05	Recepcia	9.71 m²
1.06	Zázemie - recepcia	4.72 m²
1.07	Chodba	60.04 m²
1.08	Schodisko	21.20 m²
1.09	Chodba	15.79 m²
1.10	Bezbarier. záchodová kabína	3.56 m²
1.11	WC ženy	13.56 m²
1.12	WC muži	11.20 m²
1.13	Sklad pre učebňu 3D	4.50 m²
1.14	Učebňa 3D modelovania	67.70 m²
1.15	Kabinet	22.56 m²
1.16	Kabinet	23.80 m²
1.17	Učebňa	54.25 m²
1.18	Učebňa	59.15 m²
1.19	Kabinet	24.07 m²
1.20	Učebňa	54.86 m²
1.21	Spojovacia chodba	203.54 m²
1.22	Zádverie	17.48 m²
1.23	Vrátnica	9.77 m²
1.24	Sklad	9.72 m²
1.25	Laboratórium	42.20 m²
1.26	Laboratórium	65.08 m²
1.27a	Strojovňa tepelného čerp.	35.33 m²
1.27b	Sklad	38.53 m²
1.28	Bezbarier. záchodová kabína	3.16 m²
1.29	WC ženy	9.86 m²
1.30	WC muži	10.63 m²
1.31	Rozvodňa NN	5.39 m²
1.32	Schodisko	29.95 m²
1.33	Výťah	4.10 m²
1.34	Sklad	8.95 m²
1.35	Laboratórium	17.79 m²
1.36	Kabinet	20.54 m²
1.37	Laboratórium	21.62 m²
1.38	Laboratórium	61.60 m²
1.39	Chodba	20.33 m²
1.40	Schodisko	18.80 m²
1.41	Chodba	13.62 m²
1.42	Dielňa	62.02 m²
1.43	Garáž	32.06 m²
1.44	Spojovacia chodba	25.04 m²
1.45	Sklad	14.71 m²
1.46	Sklad	20.24 m²
1.47	Sklad	12.92 m²
1.48	Sklad	23.84 m²
1.49	Upratovačka	5.65 m²
1.50	Miestnosť CBS	4.89 m²
		1442.82 m²

LEGENDA OSADENIA REGULÁCIE NA PÄTE STÚPAČKY:

GK - Guľový kohút
VK - Vypúšťací kohút DN15
RTD - Regulátor tlakovej diferencie
PTV - Partnerský vyvažovací ventil Herz Stromax GM 2013 - závit Rp

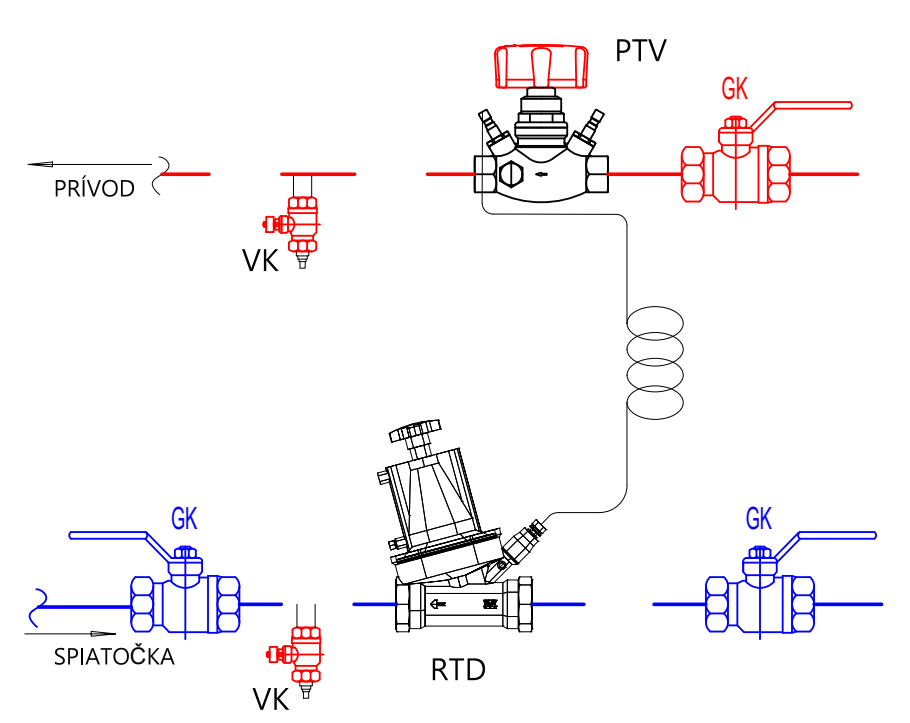

DETAIL NAPOJENIA KAZETOVÉHO FANCOILU:

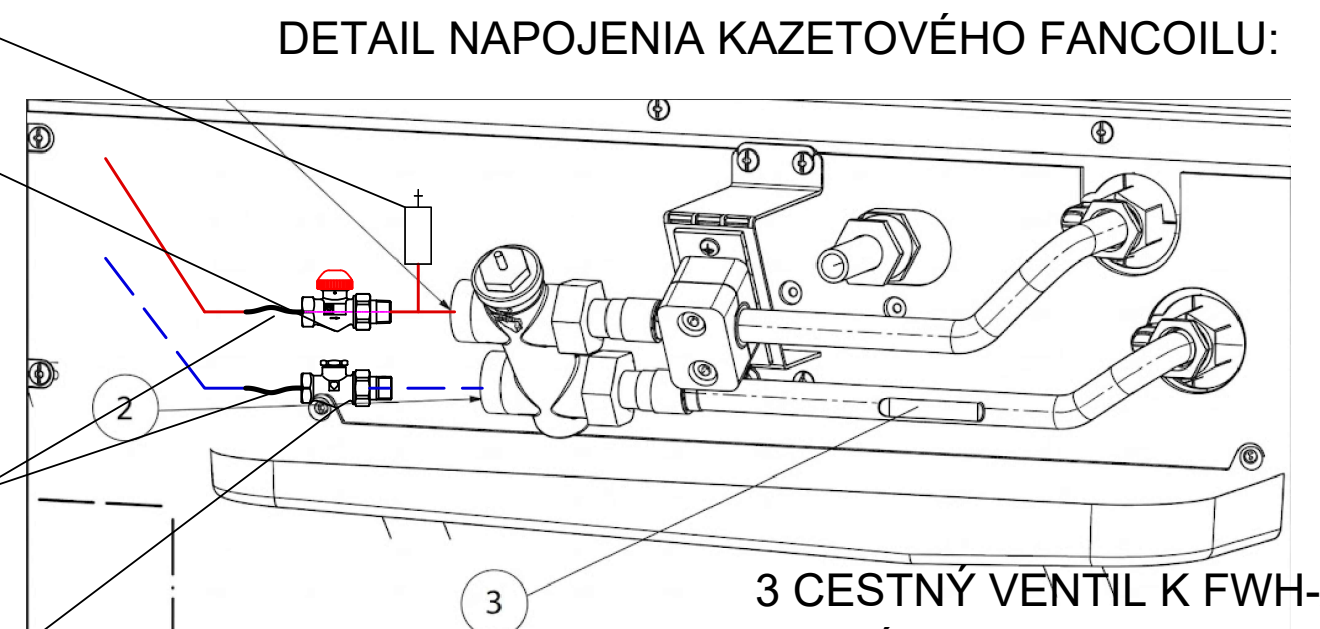

3 CESTNÝ VENTIL K FWH-AT
(DODÁVKA VZT S FANCOILOM)
230V on/off
VEĽKOSŤ 1-35 = 1/2" (kvs=1,7)
VEĽKOSŤ 4-10 = 3/4" (kvs=2,8)

DETAIL NAPOJENIA KANÁLOVÉHO FANCOILU:

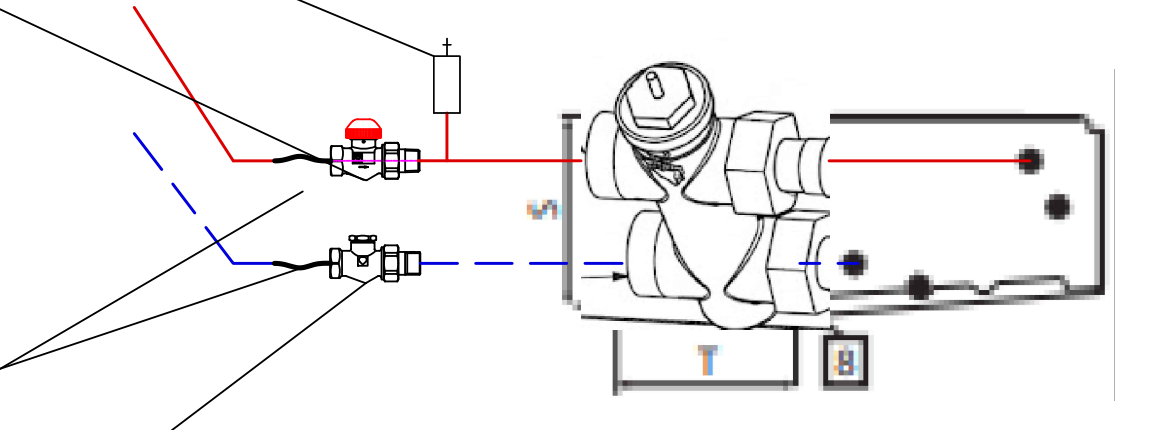

3 CESTNÝ VENTIL K FWM-AT
(DODÁVKA VZT S FANCOILOM)
230V on/off
VEĽKOSŤ 1-35 = 1/2" (kvs=1,7)
VEĽKOSŤ 4-10 = 3/4" (kvs=2,8)

DETAIL NAPOJENIA PARAPETNÉHO FANCOILU:

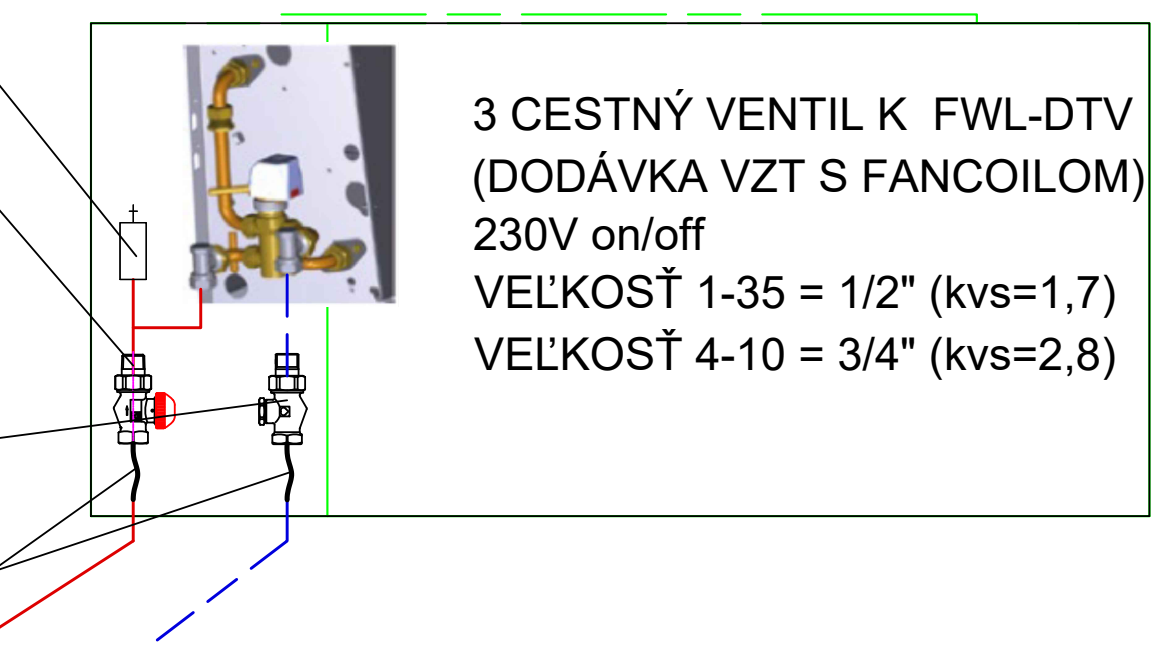

3 CESTNÝ VENTIL K FWL-DTV
(DODÁVKA VZT S FANCOILOM)
230V on/off
VEĽKOSŤ 1-35 = 1/2" (kvs=1,7)
VEĽKOSŤ 4-10 = 3/4" (kvs=2,8)

LEGENDA:

VYKUROVACIE POTRUBIE - NÍZKOUHLÍKOVÉ OCELOVÉ POTRUBIE TEPLOTNÝ SPÁD 60/50 °C HLAVNÝ ROZVOD Z TEPELNÉHO ČERPADLA

VYKUROVACIE POTRUBIE - NÍZKOUHLÍKOVÉ OCELOVÉ POTRUBIE TEPLOTNÝ SPÁD 60/50 °C HLAVNÝ ROZVOD Z AKUMULAČNEJ NÁDRŽE

VYKUROVACIE POTRUBIE - PLASTOHLÍKOVÉ/NÍZKOUHLÍKOVÉ OCELOVÉ POTRUBIE TEPLOTNÝ SPÁD 45/40 °C PRE NAPOJENIE RADIATOROV

VYKUROVACIE POTRUBIE - PLASTOHLÍKOVÉ POTRUBIE/NÍZKOUHLÍKOVÉ OCELOVÉ POTRUBIE TEPLOTNÝ SPÁD 45/40 °C

EXPANZNÉ POTRUBIE

DOSKOVÉ VYKUROVACIE TELESO

STÚPANIE/KLESANIE POTRUBIA

PARAPETNÁ FANCOIL JEDNOTKA

KANÁLOVÁ VZDUCHOVÁ JEDNOTKA

KAZETOVÁ STROPNÁ FANCOIL JEDNOTKA

LEGENDA VYKUROVACÍCH OKRUHOV:

UK1 - Prevádzka kancelárie 4.NP Fancoil
UK2 - Prevádzka Aula Fancoil
UK3 - Prevádzka škola Sever Fancoil
UK4 - Prevádzka škola Juh Fancoil
UK5 - Prevádzka škola Radiatory

LEGENDA POPISOVÝCH TABULIEK:

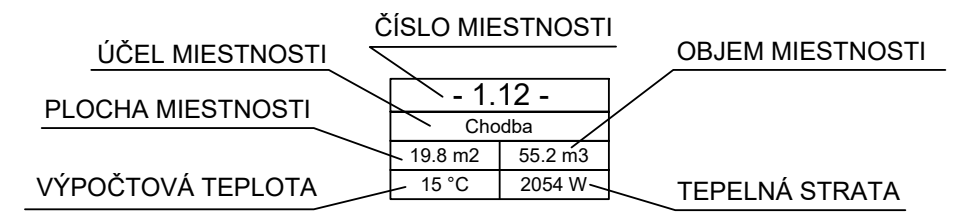

±0,000 = ÚROVEŇ PODLAHY 1.NP

SADA ČÍSLO

Objednávateľ: Trenčiansky samosprávny kraj, K dolnej stanici 7282/20A, 911 01 Trenčín,
Tre
Generálny projekt
Kontroloval: Ing.
Kraj: Trenčiansky
Investor: Trenčian
Trenčian
Miesto stavby: k.ú
15
Stupeň PD:
Akcia:
Objekt: SO 20
Obsah: Pôdory