1
2
3
4
5
6
7
8
9
A
B
C
D
E
F
G
H
I
J
K
L
M
N
O
POTRUBIE ULOŽENÉ V PODLAHE
POTRUBIE ULOŽENÉ POD STROPOM
PRÍSTUP K VENTILOM CEZ REVÍZNE VRÁTKA
ext. žalúzia
tieniaca roleta
HERZ 7217 V (1.30) PRIAMY DN20 Guľový kohút DN20
HERZ 7217 V (1.20) PRIAMY DN20 Guľový kohút DN20
HERZ 7217 V (0.10) PRIAMY DN20 Guľový kohút DN20
HERZ 7217 V (1.10) PRIAMY DN20 Guľový kohút DN20
- 4.03 - FANCOLOVÁ PARAPETNÁ JEDNOTKA VSTAVANÁ FWL08DTN VÝKON - Qchl=4420 W, Qvyk=1946 W TEPLOTNÝ SPÁD - chl: 7/12°C, vyk: 45/40°C PRIETOK - 338.51 kg/h
- 4.03 - FANCOLOVÁ PARAPETNÁ JEDNOTKA VSTAVANÁ FWL08DTN VÝKON - Qchl=4420 W, Qvyk=1946 W TEPLOTNÝ SPÁD - chl: 7/12°C, vyk: 45/40°C PRIETOK - chl: 338.51 l/h
- 4.03 - FANCOLOVÁ PARAPETNÁ JEDNOTKA VSTAVANÁ FWL01DTN VÝKON - Qchl=1400 W, Qvyk=458 W TEPLOTNÝ SPÁD - chl: 7/12°C, vyk: 45/40°C PRIETOK - chl: 79.67 l/h
- 4.03 - FANCOLOVÁ PARAPETNÁ JEDNOTKA VSTAVANÁ FWL04DTN VÝKON - Qchl=3000 W, Qvyk=1760 W TEPLOTNÝ SPÁD - chl: 7/12°C, vyk: 45/40°C PRIETOK - chl: 306.15 l/h
- 4.03 - Knižnica 54.8 m2 170.4 m3 20 °C 4115 W 26 °C 8003 W
- 4.04 - Sklad kníh 17.6 m2 53.9 m3 15 °C 513 W 26 °C 906 W
- 4.01 - FANCOLOVÁ PODSTROPNÁ JEDNOTKA FVH04AT VÝKON - Qchl=4300 W, Qvyk=744 W TEPLOTNÝ SPÁD - chl: 7/12°C, vyk: 45/40°C PRIETOK - chl: 740 l/h,vyk: 128 l/h
HERZ 7217 V (1.00) PRIAMY DN20 Guľový kohút DN20
- 4.01 - Vstupná hala 71.6 m2 219.2 m3 20 °C 3014 W 26 °C 12801 W
69
40x3,5
20x2,0
32x3,0
26x3,0
galéria
-1.500
+9.300
+7.500
+9.000
+10.800
- 4.03 - FANCOLOVÁ PARAPETNÁ JEDNOTKA FWL04DTN VÝKON - Qchl=3000 W, Qvyk=1760 W TEPLOTNÝ SPÁD - chl: 7/12°C, vyk: 45/40°C PRIETOK - 306.15 kg/h
27
- 4.09 - FWL04DTN
- 4.09 - Seminárna miestnosť 73.5 m2 224.9 m3 20 °C 3646 W 26 °C 4327 W
HERZ 7217 V (2.30) PRIAMY DN15 Guľový kohút DN15
HERZ 7217 V (1.90) PRIAMY DN15 Guľový kohút DN15
HERZ 7217 V (1.40) PRIAMY DN15 Guľový kohút DN15
HERZ 7217 V (3.10) PRIAMY DN15 Guľový kohút DN15
HERZ 7217 V (3.00) PRIAMY DN15 Guľový kohút DN15
- 4.10 - FANCOLOVÁ PARAPETNÁ JEDNOTKA FWL02DTN VÝKON - Qchl=1660 W, Qvyk=1200 W TEPLOTNÝ SPÁD - chl: 7/12°C, vyk: 45/40°C PRIETOK - 208.74 l/h
- 4.11 - FANCOLOVÁ PARAPETNÁ JEDNOTKA FWL02DTN VÝKON - Qchl=1500 W, Qvyk=1138 W TEPLOTNÝ SPÁD - chl: 7/12°C, vyk: 45/40°C PRIETOK - 197.95 l/h
- 4.12 - FANCOLOVÁ PARAPETNÁ JEDNOTKA FWL01DTN VÝKON - Qchl=1100 W, Qvyk=921 W TEPLOTNÝ SPÁD - chl: 7/12°C, vyk: 45/40°C PRIETOK - 160.21 l/h
- 4.13 - FANCOLOVÁ PARAPETNÁ JEDNOTKA FWL02DTN VÝKON - Qchl=1850 W, Qvyk=1418 W TEPLOTNÝ SPÁD - chl: 7/12°C, vyk: 45/40°C PRIETOK - 246.66 l/h
- 4.10 - Kancelária 22.5 m2 68.9 m3 20 °C 1224 W 26 °C 1166 W
- 4.11 - Kancelária 20.5 m2 62.8 m3 20 °C 1135 W 26 °C 1062 W
- 4.12 - Kancelária 16.1 m2 49.2 m3 20 °C 943 W 26 °C 854 W
- 4.13 - Jazyková učebňa 54.9 m2 168.0 m3 20 °C 2898 W 26 °C 2760 W
HERZ 7217 V (3.40) PRIAMY DN15 Guľový kohút DN15
HERZ 7217 V (1.00) PRIAMY DN20 Guľový kohút DN15
HERZ 7217 V (3.70) PRIAMY DN15 Guľový kohút DN15
HERZ 7217 V (3.80) PRIAMY DN15 Guľový kohút DN15
HERZ 7217 V (1.20) PRIAMY DN20 Guľový kohút DN20
10
11
12
13
14
15
- 4.23 - FANCOLOVÁ PARAPETNÁ JEDNOTKA FWL03DTN VÝKON - Qchl=2000 W, Qvyk=1499 W TEPLOTNÝ SPÁD - chl: 7/12°C, vyk: 45/40°C PRIETOK - 260.75 l/h
- 4.24 - FANCOLOVÁ PARAPETNÁ JEDNOTKA FWL03DTN VÝKON - Qchl=2050 W, Qvyk=1510 W TEPLOTNÝ SPÁD - chl: 7/12°C, vyk: 45/40°C PRIETOK - 262.66 l/h
- 4.25 - FANCOLOVÁ PARAPETNÁ JEDNOTKA FWL04DTN VÝKON - Qchl=2400 W, Qvyk=1775 W TEPLOTNÝ SPÁD - chl: 7/12°C, vyk: 45/40°C PRIETOK - 308.76 l/h
- 4.26 - FANCOLOVÁ PARAPETNÁ JEDNOTKA FWL03DTN VÝKON - Qchl=2100 W, Qvyk=1569 W TEPLOTNÝ SPÁD - chl: 7/12°C, vyk: 45/40°C PRIETOK - 272.93 l/h
- 4.27 - FANCOLOVÁ PARAPETNÁ JEDNOTKA FWL03DTN VÝKON - Qchl=2100 W, Qvyk=1584 W TEPLOTNÝ SPÁD - chl: 7/12°C, vyk: 45/40°C PRIETOK - 275.54 l/h
- 4.28 - FANCOLOVÁ PARAPETNÁ JEDNOTKA FWL04DTN VÝKON - Qchl=2470 W, Qvyk=1998 W TEPLOTNÝ SPÁD - chl: 7/12°C, vyk: 45/40°C PRIETOK - 347.55 l/h
- 4.27 - Kancelária 31.1 m2 95.1 m3 20 °C 1624 W 26 °C 1586 W
- 4.28 - Kancelária 36.2 m2 110.6 m3 20 °C 1943 W 26 °C 1843 W
75x4,6
DN125-iz
29
TČ1
TČ1
UP
- 4.42 - Schodisko 18.9 m2 57.9 m3 18 °C 0 W 26 °C 24 W
28
HERZ 7217 V (1.10) PRIAMY DN15 Guľový kohút DN15
- 4.44 - FANCOLOVÁ PARAPETNÁ JEDNOTKA FWL03DTN VÝKON - Qchl=1350 W, Qvyk=976 W TEPLOTNÝ SPÁD - chl: 7/12°C, vyk: 45/40°C PRIETOK - 168.77 l/h
- 4.44 - Sklad dizajn 20.2 m2 61.8 m3 15 °C 1055 W 26 °C 1092 W
HERZ 7217 V (2.30) PRIAMY DN20 Guľový kohút DN20
HERZ 7217 V (2.00) PRIAMY DN20 Guľový kohút DN20
- 4.45 - FANCOLOVÁ PODSTROPNÁ JEDNOTKA FWH04AT VÝKON - Qchl=4500 W, Qvyk=3136 W TEPLOTNÝ SPÁD - chl: 7/12°C, vyk: 45/40°C PRIETOK - 545.51 l/h
- 4.45 - Seminárna miestnosť 111.3 m2 340.7 m3 20 °C 6386 W 26 °C 7337 W
- 4.15- FANCOLOVÁ PARAPETNÁ JEDNOTKA FWL03DTN VÝKON - Qchl=2600 W, Qvyk=1791 W TEPLOTNÝ SPÁD - chl: 7/12°C, vyk: 45/40°C PRIETOK - 311.54 l/h
- 4.16 - FANCOLOVÁ PARAPETNÁ JEDNOTKA FWL02DTN VÝKON - Qchl=1600 W, Qvyk=937 W TEPLOTNÝ SPÁD - chl: 7/12°C, vyk: 45/40°C PRIETOK - 162.99 l/h
- 4.17- FANCOLOVÁ PARAPETNÁ JEDNOTKA FWL04DTN VÝKON - Qchl=2470 W, Qvyk=1389 W TEPLOTNÝ SPÁD - chl: 7/12°C, vyk: 45/40°C PRIETOK - 241.62 l/h
- 4.18 - FANCOLOVÁ PARAPETNÁ JEDNOTKA FWL02DTN VÝKON - Qchl=1660 W, Qvyk=965 W TEPLOTNÝ SPÁD - chl: 7/12°C, vyk: 45/40°C PRIETOK - 167.86 l/h
- 4.19 - FANCOLOVÁ PARAPETNÁ JEDNOTKA FWL02DTN VÝKON - Qchl=1750 W, Qvyk=1024 W TEPLOTNÝ SPÁD - chl: 7/12°C, vyk: 45/40°C PRIETOK - 178.12 l/h
- 4.20 - FANCOLOVÁ PARAPETNÁ JEDNOTKA FWL04DTN VÝKON - Qchl=2470 W, Qvyk=1387 W TEPLOTNÝ SPÁD - chl: 7/12°C, vyk: 45/40°C PRIETOK - 241.27 l/h
- 4.21 - FANCOLOVÁ PARAPETNÁ JEDNOTKA FWL04DTN VÝKON - Qchl=3000 W, Qvyk=1711 W TEPLOTNÝ SPÁD - chl: 7/12°C, vyk: 45/40°C PRIETOK - 308.06 l/h
- 4.15 - Kancelária 28.0 m2 85.7 m3 20 °C 1749 W 26 °C 2133 W
- 4.16 - Kancelária 16.4 m2 50.2 m3 20 °C 961 W 26 °C 1296 W
- 4.17 - Kancelária 25.5 m2 77.9 m3 20 °C 1418 W 26 °C 1987 W
- 4.18 - Kancelária 17.1 m2 52.5 m3 20 °C 985 W 26 °C 1362 W
- 4.19 - Kancelária 18.7 m2 57.1 m3 20 °C 1045 W 26 °C 1440 W
- 4.20 - Kancelária 25.4 m2 77.8 m3 20 °C 1415 W 26 °C 1987 W
- 4.21 - Kancelária 32.0 m2 97.9 m3 20 °C 1748 W 26 °C 2460 W
68
25
24
26
23
22
21b
HERZ 7217 V (1.10) PRIAMY DN20 Guľový kohút DN20
HERZ 7217 V (1.40) PRIAMY DN15 Guľový kohút DN15
HERZ 7217 V (0.70) PRIAMY DN20 Guľový kohút DN20
HERZ 7217 V (1.40) PRIAMY DN15 Guľový kohút DN15
HERZ 7217 V (1.60) PRIAMY DN15 Guľový kohút DN15
HERZ 7217 V (0.70) PRIAMY DN20 Guľový kohút DN20
HERZ 7217 V (1.00) PRIAMY DN20 Guľový kohút DN20
- 4.22 - Spojovacia chodba 105.9 m2 324.1 m3 18 °C 3248 W 26 °C 6861 W
HERZ 7217 V (1.90) PRIAMY DN20 Guľový kohút DN20
HERZ 7217 V (1.80) PRIAMY DN20 Guľový kohút DN20
- 4.29 - FANCOLOVÁ PODSTROPNÁ JEDNOTKA FWH04AT VÝKON - Qchl=4000 W, Qvyk=3017W TEPLOTNÝ SPÁD - chl: 7/12°C, vyk: 45/40°C PRIETOK - 524.81 l/h
- 4.29 - Multifunčný priestor 194.5 m2 595.3 m3 20 °C 7641 W
63x4,5
50x4,0
- 4.46 - FANCOLOVÁ PODSTROPNÁ JEDNOTKA FWH04AT VÝKON - Qchl=4100 W, Qvyk=3080W TEPLOTNÝ SPÁD - chl: 7/12°C, vyk: 45/40°C PRIETOK - 535.77 l/h
- 4.47 - FANCOLOVÁ PODSTROPNÁ JEDNOTKA FWH04AT VÝKON - Qchl=3000 W, Qvyk=1899 W TEPLOTNÝ SPÁD - chl: 7/12°C, vyk: 45/40°C PRIETOK - 521.85 l/h
- 4.46 - Ateliér II 49.4 m2 151.1 m3 20 °C 3091 W 26 °C 3582 W
- 4.47 - Kancelária 30.5 m2 93.3 m3 20 °C 1952 W 26 °C 2518 W
- 4.47 - Chodba
4.48
- 4.36 - FANCOLOVÁ PARAPETNÁ JEDNOTKA FWL04DTN VÝKON - Qchl=3000 W, Qvyk=2497 W TEPLOTNÝ SPÁD - chl: 7/12°C, vyk: 45/40°C PRIETOK - 434.35 l/h
- 4.37 - FANCOLOVÁ PARAPETNÁ JEDNOTKA FWL03DTN VÝKON - Qchl=2200 W, Qvyk=1057 W TEPLOTNÝ SPÁD - chl: 7/12°C, vyk: 45/40°C PRIETOK - 183.86 l/h
- 4.38 - FANCOLOVÁ PARAPETNÁ JEDNOTKA FWL03DTN VÝKON - Qchl=2200 W, Qvyk=1064 W TEPLOTNÝ SPÁD - chl: 7/12°C, vyk: 45/40°C PRIETOK - 185.08 l/h
- 4.39 - FANCOLOVÁ PARAPETNÁ JEDNOTKA FWL03DTN VÝKON - Qchl=2200 W, Qvyk=1057 W TEPLOTNÝ SPÁD - chl: 7/12°C, vyk: 45/40°C PRIETOK - 183.86 l/h
- 4.41 - FANCOLOVÁ PARAPETNÁ JEDNOTKA FWL03DTN VÝKON - Qchl=2300 W, Qvyk=1110W TEPLOTNÝ SPÁD - chl: 7/12°C, vyk: 45/40°C PRIETOK - 272.93 l/h
- 4.42 - FANCOLOVÁ PARAPETNÁ JEDNOTKA FWL03DTN VÝKON - Qchl=2200 W, Qvyk=1322 W TEPLOTNÝ SPÁD - chl: 7/12°C, vyk: 45/40°C PRIETOK - 229.96 l/h
- 4.36 - Kancelária 32.2 m2 98.5 m3 20 °C 2420 W 26 °C 2475 W
- 4.37 - Kancelária 21.6 m2 66.2 m3 20 °C 1121 W 26 °C 1648 W
- 4.38 - Kancelária 21.7 m2 66.3 m3 20 °C 1128 W 26 °C 1655 W
- 4.39 - Kancelária 21.7 m2 66.3 m3 20 °C 1121 W 26 °C 1648 W
- 4.41 - Kancelária 22.5 m2 68.9 m3 20 °C 1178 W 26 °C 1735 W
- 4.42 - Kancelária 23.6 m2 72.1 m3 20 °C 1402 W 26 °C 1680 W
21a
20
19
18
17
16
HERZ 7217 V (1.40) PRIAMY DN20 Guľový kohút DN20
HERZ 7217 V (1.40) PRIAMY DN15 Guľový kohút DN15
HERZ 7217 V (3.70) PRIAMY DN15 Guľový kohút DN15
HERZ 7217 V (2.50) PRIAMY DN15 Guľový kohút DN15

LEGENDA:

	VYKUROVACIE POTRUBIE - NÍZKOUHLÍKOVÉ OCELOVÉ POTRUBIE TEPLOTNÝ SPÁD 60/50 °C HLAVNÝ ROZVOD Z TEPELNÉHO ČERPADLA
	VYKUROVACIE POTRUBIE - NÍZKOUHLÍKOVÉ OCELOVÉ POTRUBIE TEPLOTNÝ SPÁD 60/50 °C HLAVNÝ ROZVOD Z AKUMULAČNEJ NÁDRŽE
	VYKUROVACIE POTRUBIE - PLASTOHLÍKOVÉ/NÍZKOUHLÍKOVÉ OCELOVÉ POTRUBIE TEPLOTNÝ SPÁD 45/40 °C PRE NAPOJENIE RADIATOROV
	VYKUROVACIE POTRUBIE - PLASTOHLÍKOVÉ POTRUBIE/NÍZKOUHLÍKOVÉ OCELOVÉ POTRUBIE TEPLOTNÝ SPÁD 45/40 °C
	EXPANZNÉ POTRUBIE
	DOSKOVÉ VYKUROVACIE TELESO
	STÚPANIE/KLESANIE POTRUBIA
	PARAPETNÁ FANCOIL JEDNOTKA
	KANÁLOVÁ VZDUCHOVÁ JEDNOTKA
	KAZETOVÁ STROPNÁ FANCOIL JEDNOTKA

LEGENDA VYKUROVACÍCH OKRUHOV:

- UK1 - Prevádzka kancelárie 4.NP Fancoil
- UK2 - Prevádzka Aula Fancoil
- UK3 - Prevádzka škola Sever Fancoil
- UK4 - Prevádzka škola Juh Fancoil
- UK5 - Prevádzka škola Radiatory

LEGENDA POPISOVÝCH TABULIEK:

ČÍSLO MIESTNOSTI
ÚČEL MIESTNOSTI
OBJEM MIESTNOSTI
PLOCHA MIESTNOSTI
VÝPOČTOVÁ TEPLOTA
TEPELNÁ STRATA

- 1.12 -	
Chodba	
19.8 m2	55.2 m3
15 °C	2054 W

L.M. 4.NP - PBS		
Č.M.	Názov	Plocha
4.01	Vstupná hala	52.75
4.02	Výťah	3.47
4.03	Študovňa	44.85
4.04	Sklad kníh	17.09
4.05	Bezbarier. záchodová kabína	3.71
4.06	WC ženy	5.62
4.07	WC personál	1.97
4.08	WC muži	13.03
4.09	Seminárna miestnosť	67.28
4.10	Kancelária	21.00
4.11	Kancelária	19.47
4.12	Kancelária	16.26
4.13	Jazyková učebňa	48.19
4.14	Schodisko	21.56
4.15	Kancelária	26.52
4.16	Kancelária	16.03
4.17	Kancelária	24.69
4.18	Kancelária	16.84
4.19	Kancelária	17.04
4.20	Kancelária	24.64
4.21	Kancelária	27.91
4.22	Spojovacia chodba	220.43
4.23	Kancelária	26.85
4.24	Kancelária	26.34
4.25	Kancelária	33.03
4.26	Kancelária	29.12
4.27	Kancelária	29.64
4.28	Kancelária	31.93
4.29	Multifunkčný priestor	75.60
4.30	Bezbarier. záchodová kabína	3.46
4.31	WC ženy	10.38
4.32	WC muži	11.27
4.33	Upratovačka	4.90
4.34	Schodisko	29.94
4.35	Výťah	4.10
4.36	Kancelária	31.11
4.37	Kancelária	19.20
4.38	Kancelária	19.61
4.39	Kancelária	19.60
4.41	Kancelária	19.61
4.42	Kancelária	19.33
4.43	Schodisko	18.02
4.44	Sklad dizajn	19.74
4.45	Seminárna miestnosť	111.65
4.46	Ateliér II	48.46
4.47	Kancelária	26.43
4.48	Chodba	53.88

DETAIL NAPOJENIA KAZETOVÉHO FANCOILU:

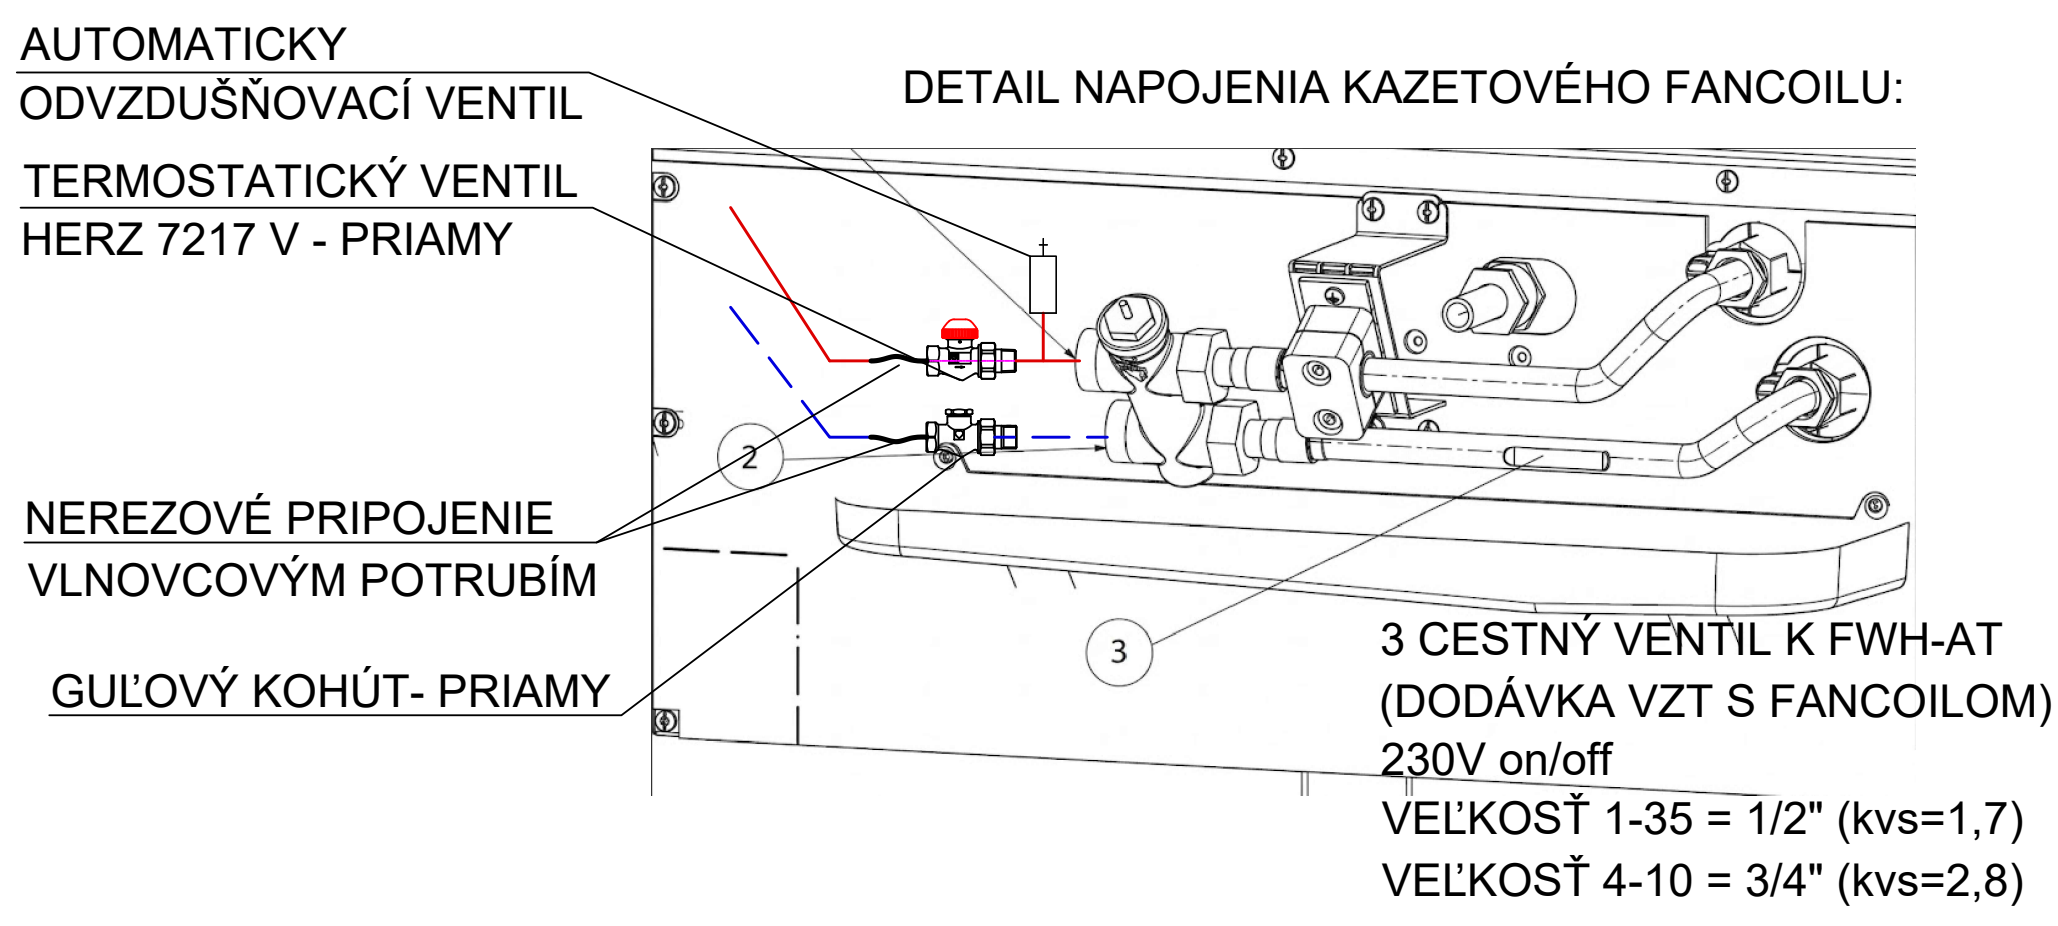
AUTOMATICKY ODVZDUŠŇOVACÍ VENTIL
TERMOSTATICKÝ VENTIL HERZ 7217 V - PRIAMY
NEREZOVÉ PRIPOJENIE VLNOVCOVÝM POTRUBÍM
GUĽOVÝ KOHÚT- PRIAMY
3 CESTNÝ VENTIL K FWH-AT (DODÁVKA VZT S FANCOILOM) 230V on/off VEĽKOSŤ 1-35 = 1/2" (kvs=1,7) VEĽKOSŤ 4-10 = 3/4" (kvs=2,8)

DETAIL NAPOJENIA KANÁLOVÉHO FANCOILU:

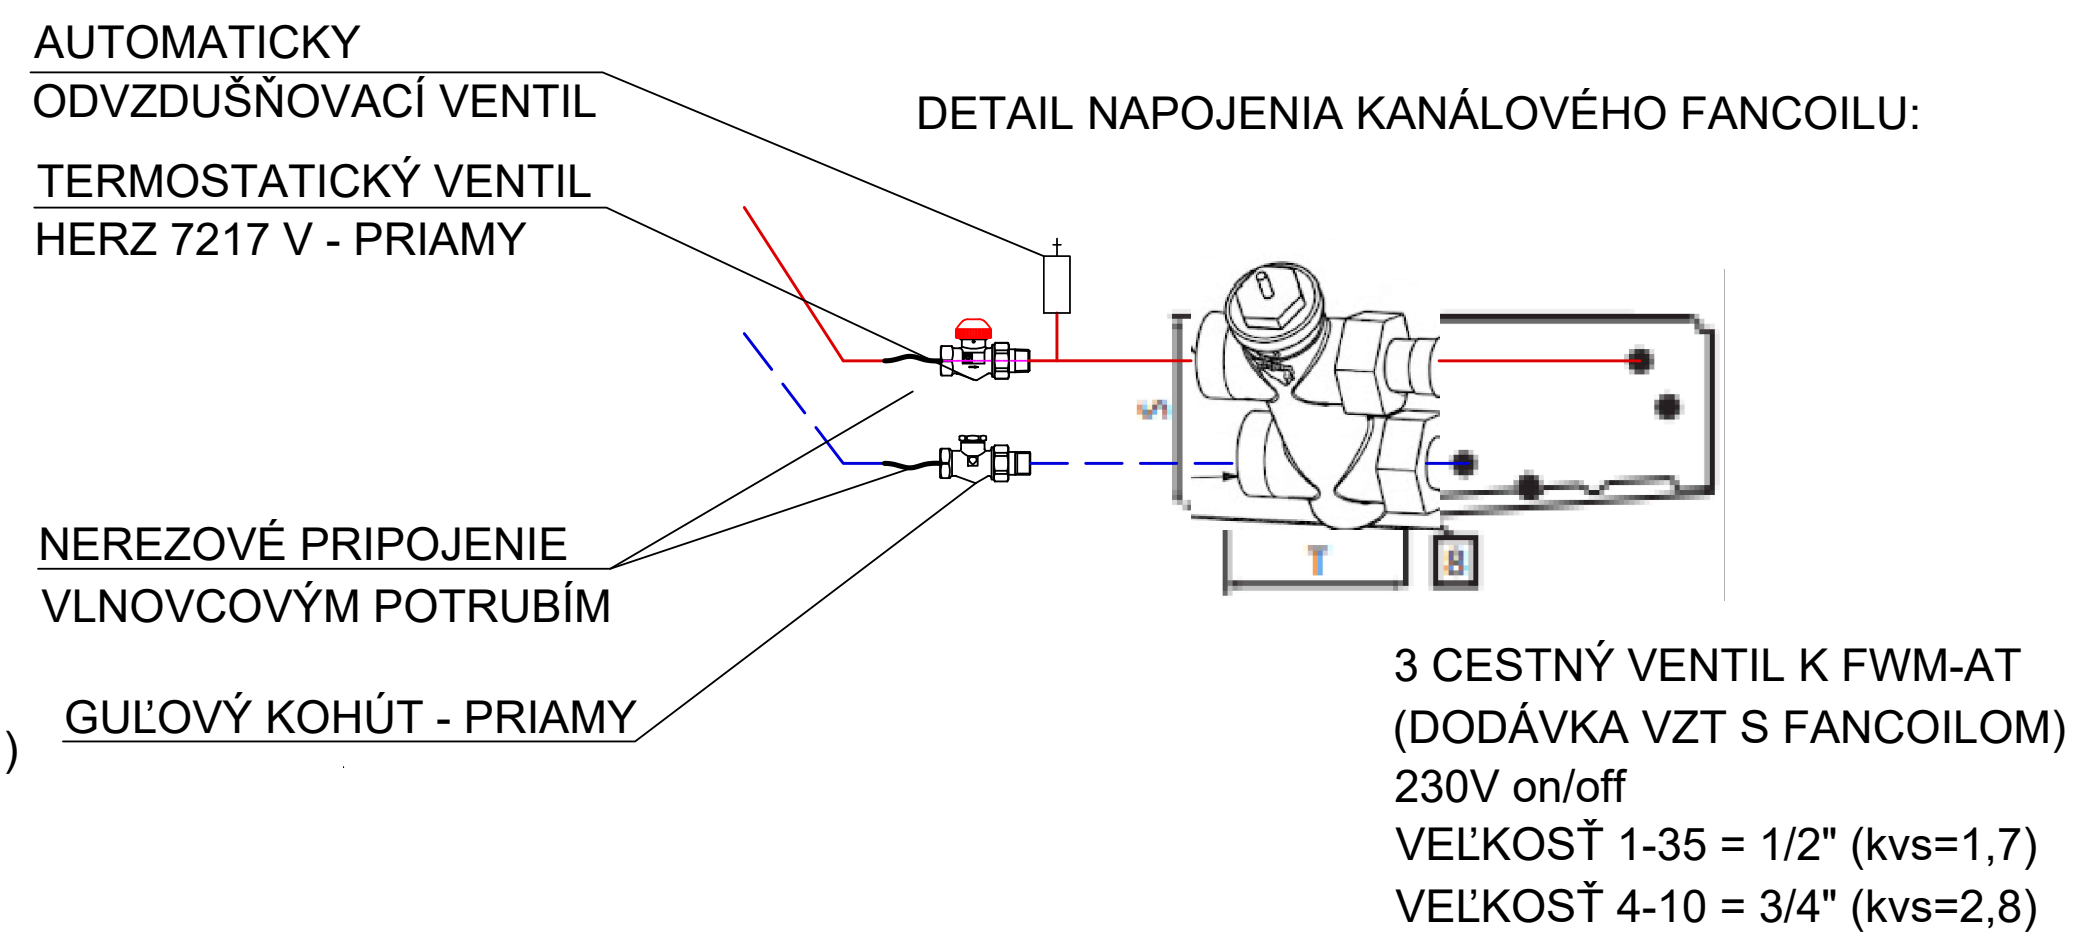
AUTOMATICKY ODVZDUŠŇOVACÍ VENTIL
TERMOSTATICKÝ VENTIL HERZ 7217 V - PRIAMY
NEREZOVÉ PRIPOJENIE VLNOVCOVÝM POTRUBÍM
GUĽOVÝ KOHÚT - PRIAMY
3 CESTNÝ VENTIL K FWM-AT (DODÁVKA VZT S FANCOILOM) 230V on/off VEĽKOSŤ 1-35 = 1/2" (kvs=1,7) VEĽKOSŤ 4-10 = 3/4" (kvs=2,8)

DETAIL NAPOJENIA PARAPETNÉHO FANCOILU:

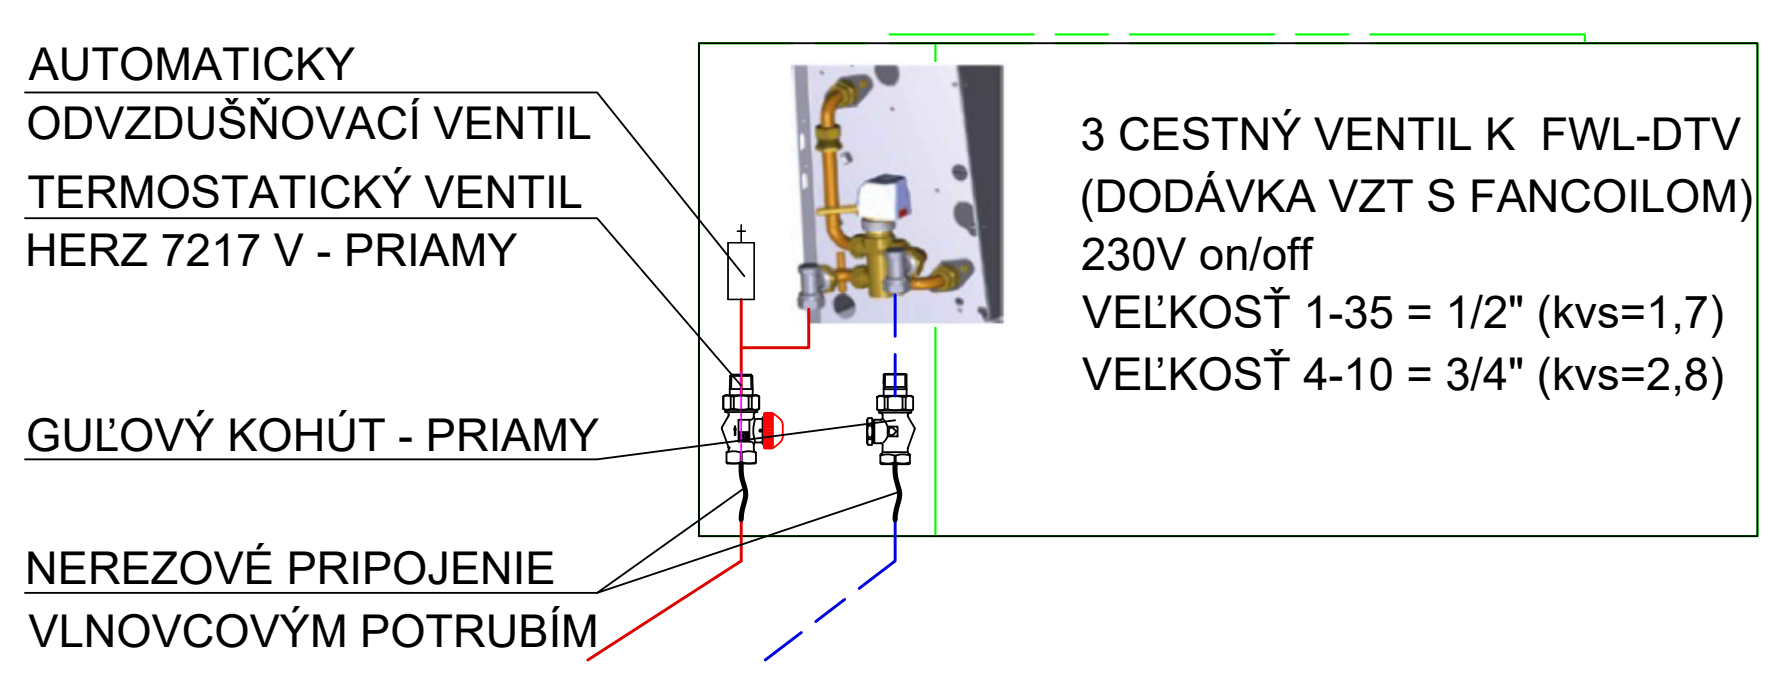
AUTOMATICKY ODVZDUŠŇOVACÍ VENTIL
TERMOSTATICKÝ VENTIL HERZ 7217 V - PRIAMY
GUĽOVÝ KOHÚT - PRIAMY
NEREZOVÉ PRIPOJENIE VLNOVCOVÝM POTRUBÍM
3 CESTNÝ VENTIL K FWL-DTV (DODÁVKA VZT S FANCOILOM) 230V on/off VEĽKOSŤ 1-35 = 1/2" (kvs=1,7) VEĽKOSŤ 4-10 = 3/4" (kvs=2,8)

±0,000 = ÚROVEŇ PODLAHY 1.NP

SADA ČÍSLO

Objednávateľ: Trenčiansky samosprávny kraj, K dolnej stanici 7282/20A, 911 01 Trenčín,
Tre
Generálny projekt
Kontroloval: Ing.
Kraj: Trenčiansky
Investor: Trenčian
Trenčian
Miesto stavby: k.ú
15
Stupeň PD:
Akcia:
Objekt: SO 20
Obsah: Pôdory