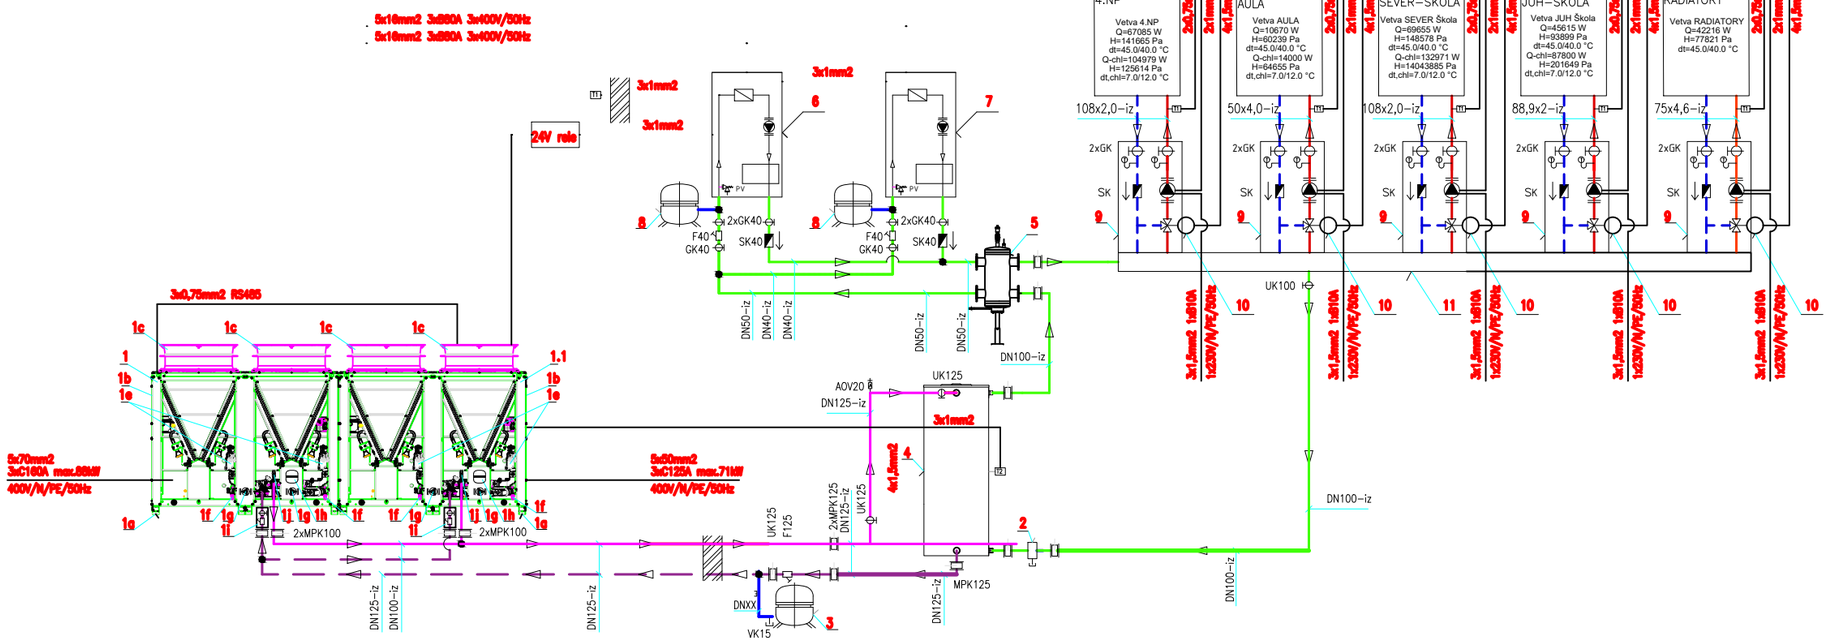


LEGENDA ZARIADENÍ:

POZ.	NÁZOV, ROZMER	P. KS
	TEPELNÉ ČERPADLO CARRIER 61AQ 260P skladá sa z dvoch modulov:	1
1	TEPELNÉ ČERPADLO CARRIER 61AQ 160P	
1.1	TEPELNÉ ČERPADLO CARRIER 61AQ 100P	
	MAX. VÝSTUPNÁ TEPLOTA 75°C, CHLADIVO R290 GWP3	
	VYK.VÝKON 30,5–197kW (A–7/W45)	
	CHLAD.VÝKON 26,9–105kW (A35/W7)	
1a	ANTIVIBRAČNE BLOKY – SILENT BLOKY – SADA opcia 308	–
1b	REGULÁCIA TEP.ČERPADLA SmartVu – v rozsahu dodávky pol.1	–
1c	EC–ELEKTRONICKY RIADENY VENTILÁTOR – v rozsahu dodávky pol.1	–
1d	SNÍMAČ VONKAJŠEJ TEPLOTY – opcia 312	–
1e	ODLUČOVAČ CHLADIVA PROPÁN S ODVZDUŠNOVACÍM VENTILOM – v rozsahu dodávky pol.1	–
1f	TERMOSTATICKÝ VENTIL PROTI ZAMRZNUTIU – v rozsahu dodávky pol.1	–
1g	OBEHOVÉ ČERPADLO S REGULÁCIOU OTÁČOK – opcia 116V	–
1h	EXPANZNÁ NÁDOBA OBJEM 8L – opcia 116V	–
1i	SADA FILTRA NA SYSTÉM (treba namontovať) – v rozsahu dodávky pol.1	–
1j	POISTNÝ VENTIL PRE SYSTÉM 4bar – v rozsahu dodávky pol.1	–
2	ODLUČOVAČ SPIROTRAP S MAGNETOM DN100 PRÍRUBOVÝ (7784181)	3
3	EXPANZNÁ NÁDOBA N300, OBJEM 300L, 6bar STRIEBORNÁ	1
4	AKUM.ZÁSOBNÍK PRE UK VITOCELL 050–HC EC PRO SH2010HA OBJEM 2010L (Z028042)	1
5	HYDRAULIC.VYROVNÁVAČ TLAKOV S IZOLÁCIOU	1
6	ZÁVESNÝ ELEKTROKOTOL TYP EKCO.TM 16–48 kW (Z021557)	1
7	ZÁVESNÝ ELEKTROKOTOL TYP EKCO.T 16–48 kW (Z021561)	2
8	EXPANZNÁ NÁDOBA H25, OBJEM 25, 3bar BIELA (7938082)	1
9	RÝCHLOMONTÁŽNA SADA M32 SO ZMIEŠAVACOM DN50 MAGNA3 50–80F (ZK01668)	1
10	SERVOPOHON SR10 230V/50Hz (7199567)	1
11	MODULÁRNY ROZDEĽOVAČ PRE 5 OKRUHOV DN100	1
15		2
16		1
17		2
T1	SNÍMAČ VÝSTUPNEJ TEPLOTY (7426463)	5
T2	SNÍMAČ TEPLOTY ZÁSOBNÍKA – dodávka kaskádovej regulácie tep.čerpadiel	1
T3	SNÍMAČ TEPLOTY ZÁSOBNÍKA – opcia 312A	1
T4	SNÍMAČ VONKAJŠEJ TEPLOTY – v rozsahu dodávky pol.17	1
T5	SNÍMAČ TEPLOTY HYDRAULICKEJ VÝHYBKY – existujúci	1
T6	PONORNÝ SNÍMAČ TEPLOTY (7438702)	1

LEGENDA:

- VYKUROVACIE POTRUBIE - NÍZKOUHLÍKOVÉ OCELOVÉ POTRUBIE TEPLOTNÝ SPÁD 60/50 °C -VETVA TEPELNÉ ČERPADLO
- VYKUROVACIE POTRUBIE - NÍZKOUHLÍKOVÉ OCELOVÉ POTRUBIE TEPLOTNÝ SPÁD 60/50 °C -VETVA TEPELNÉ ČERPADLO Z AKUMULÁCIE
- VYKUROVACIE POTRUBIE - NÍZKOUHLÍKOVÉ OCELOVÉ POTRUBIE TEPLOTNÝ SPÁD 42/35 °C
- EXPANZNÉ POTRUBIE

±0,000 = ÚROVEŇ PODLAHY 1.NP

SADA ČÍSLO

Objednávateľ: Trenčiansky samosprávny kraj, K dolnej stanici 7282/20A, 911 01 Trenčín,
Trenčianska univerzita Alexandra Dubčeka v Trenčíne, Študentská 2, 911 50 Trenčín

Generálny projekta

Kontroloval: Ing. Já

Kraj: Trenčiansky

Investor: Trenčiansk
Trenčiansk

Miesto stavby: k.ú h
1548

Stupeň PD:

Akcia:

Objekt: SO 201

Obsah: Schéma