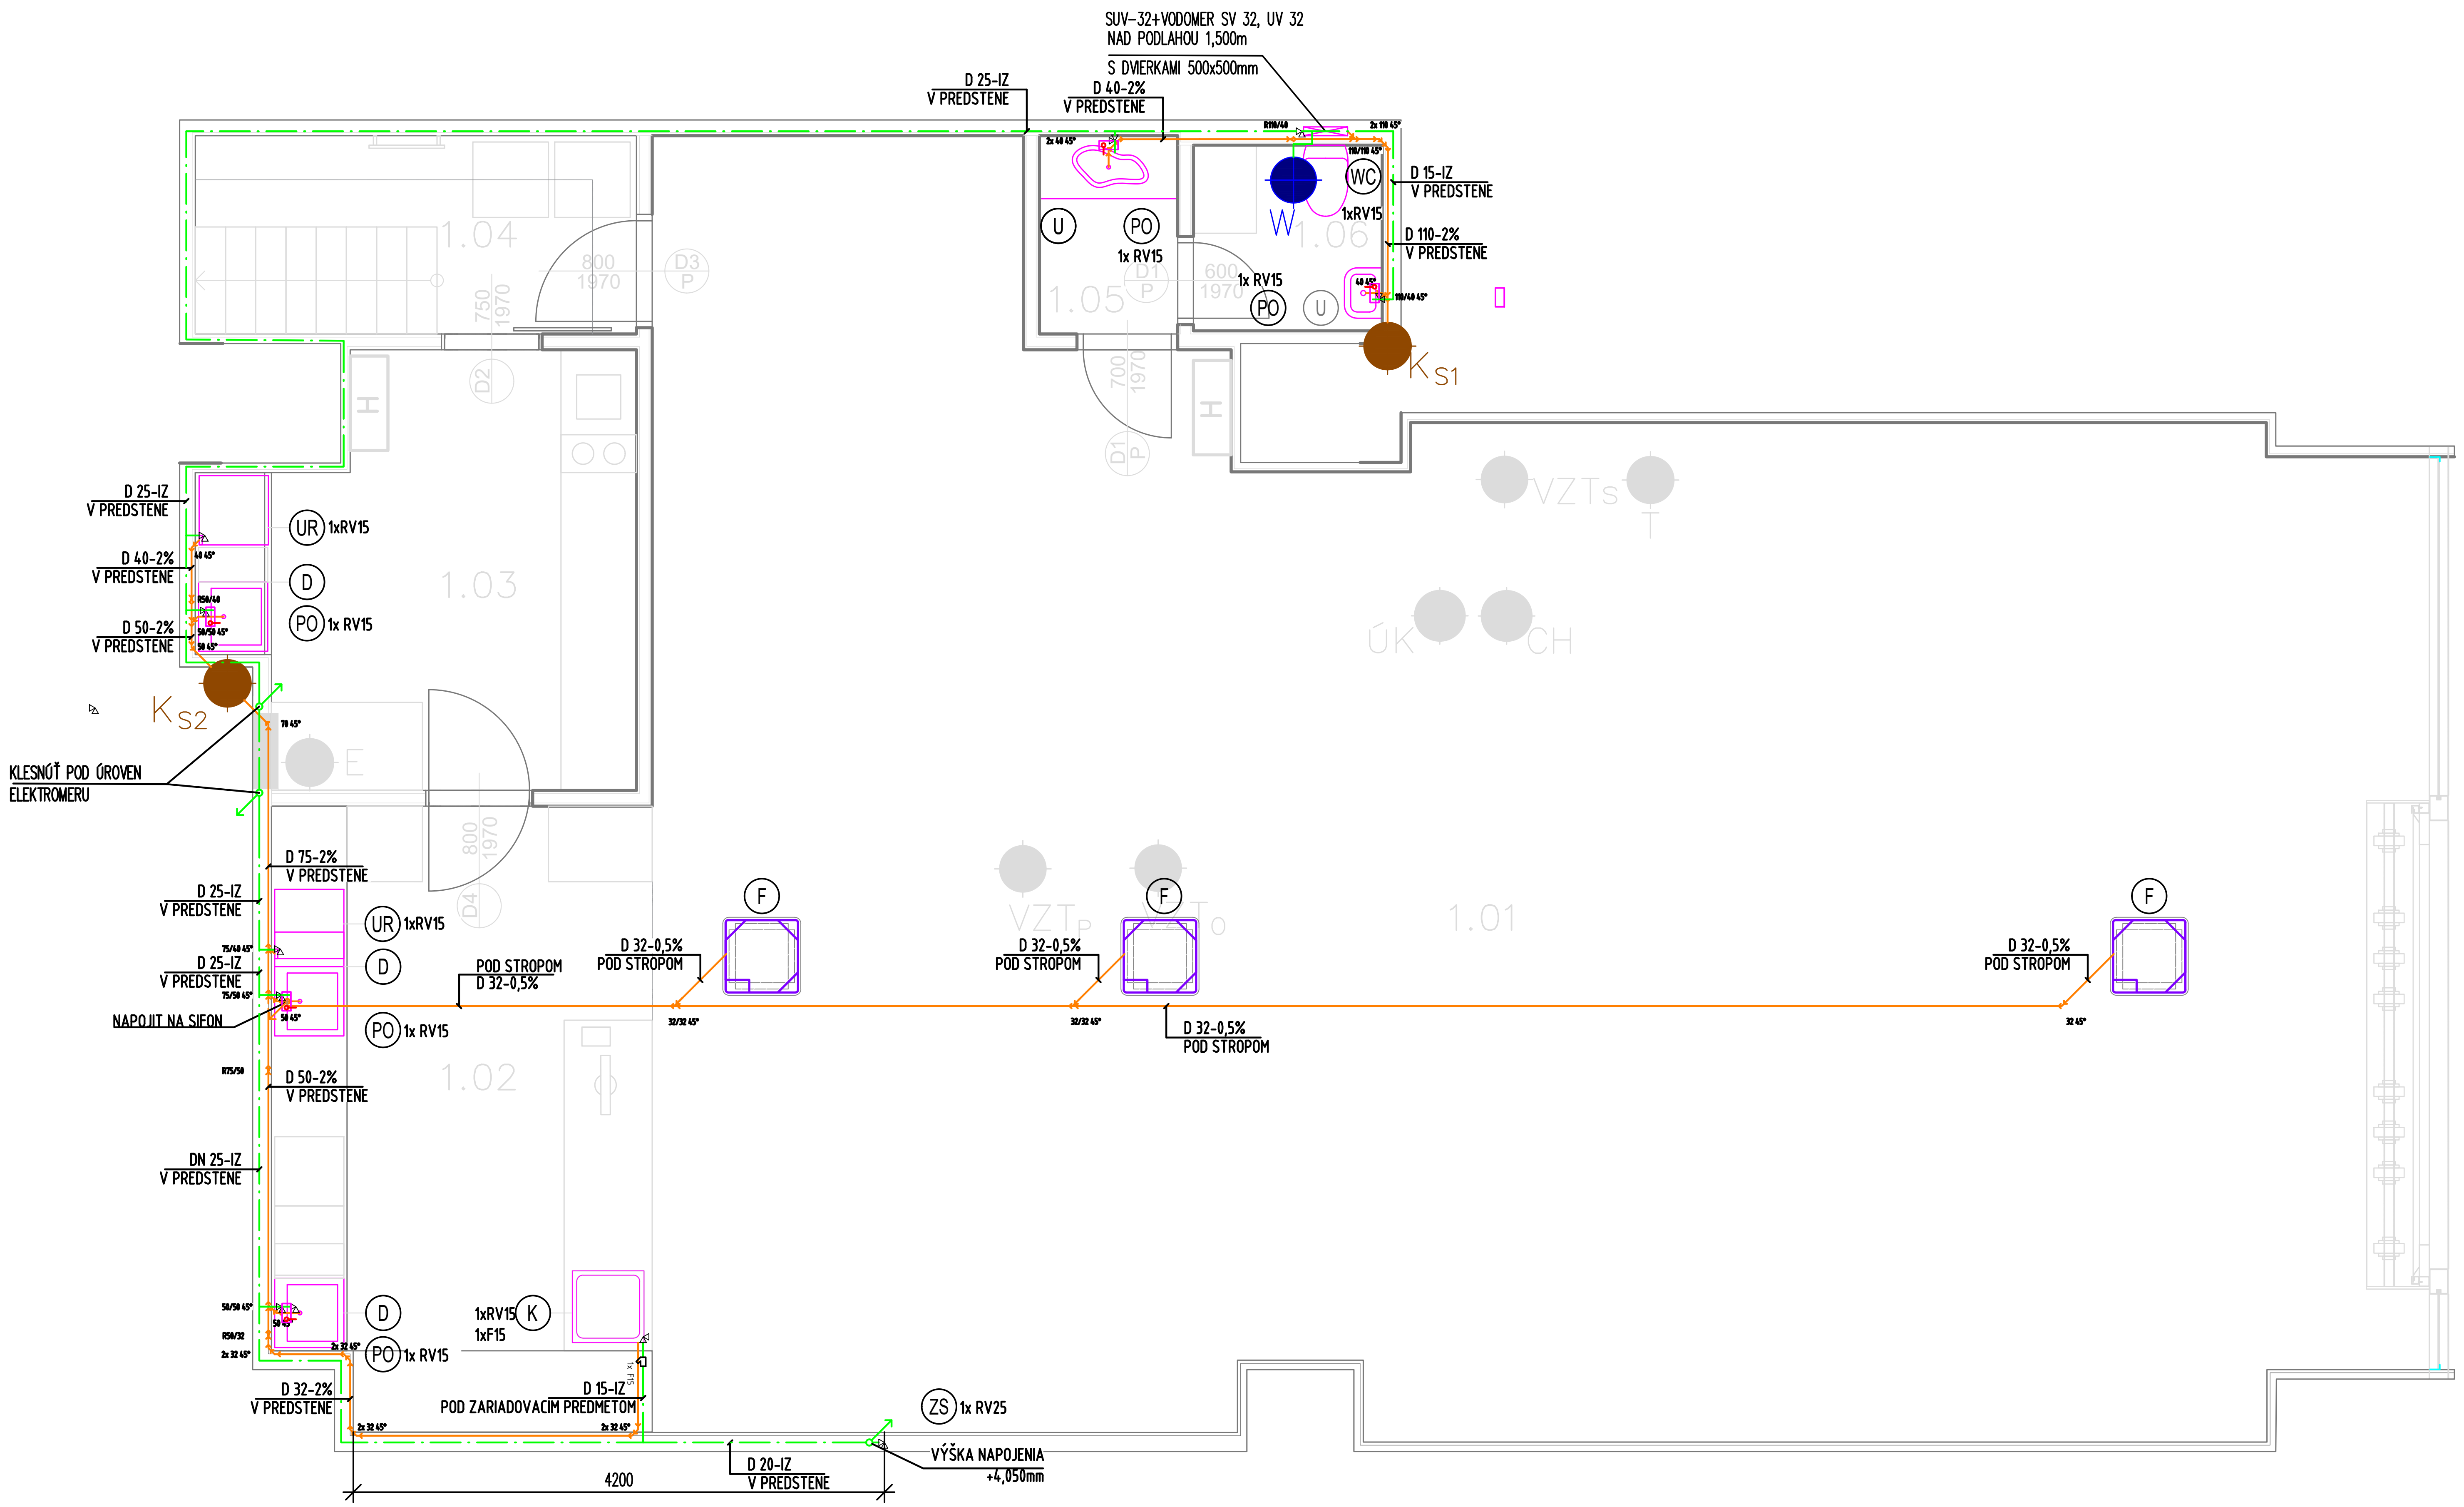
SUV–32+VODOMER SV 32, UV 32
NAD PODLAHOU 1,500m
S DVIERKAMI 500x500mm
D 25-IZ
V PREDSTENE
D 40-2%
V PREDSTENE
D 15-IZ
V PREDSTENE
D 110-2%
V PREDSTENE
U
PO
1x RV15
WC
1xRV15
W
1x RV15
PO
U
K_{S1}
1.05
1.06
1.04
1.03
1.02
1.01
D 25-IZ
V PREDSTENE
D 40-2%
V PREDSTENE
D 50-2%
V PREDSTENE
UR 1xRV15
D
PO 1x RV15
K_{S2}
KLESNÚŤ POD ÚROVEN
ELEKTROMERU
E
VZT
ÚK
CH
D 75-2%
V PREDSTENE
D 25-IZ
V PREDSTENE
D 25-IZ
V PREDSTENE
NAPOJIT NA SIFON
UR 1xRV15
D
PO 1x RV15
POD STROPOM
D 32-0,5%
D 32-0,5%
POD STROPOM
F
D 32-0,5%
POD STROPOM
D 32-0,5%
POD STROPOM
D 50-2%
V PREDSTENE
DN 25-IZ
V PREDSTENE
D
PO 1x RV15
1xRV15 K
1xF15
D 32-2%
V PREDSTENE
D 15-IZ
POD ZARIADOVACÍM PREDMETOM
ZS 1x RV25
D 20-IZ
V PREDSTENE
VÝŠKA NAPOJENIA
+4,050mm
4200

LEGENDA POTRUBIA

——— KANALIZAČNÉ ZVODOVÉ POTRUBIE HRDLOVÉ Z RÚR A TVAROVIEK S GUMOVÝM TESNENÍM
MATERIÁL: WAVIN AS PRE VNÚTORNÉ ROZVODY

—·— POTRUBIE ROZVODU STUDENEJ PITNEJ VODY – IZOLOVANÝ TEPELNOU IZOLÁCIOU TUBOLIT DG HR. 9mm
MATERIAL: PEX/Al/PEX

—··— POTRUBIE ROZVODU TEPLEJ VODY – PRIPOJOVACIA FLEXI HADICA

W EXISTUJÚCI VODOVOD, BOD NAPOJENIA D32

K_{S1} , K_{S2} EXISTUJÚCE ODPADOVÉ POTRUBIE SPLAŠKOVEJ KANALIZÁCIE, BOD NAPOJENIA D110

POZNÁMKY

Všetky kóty a rozmery PREMERAŤ NA STAVBE pred zahájením prác. Zvlášť preveriť polohy pripojenia technologických zariadení.
Montážne trasy potrubí koordinovať s profesiami VZT a EL.
Práce realizovať striktne podľa platných STN/EN noriem. Kanalizačné potrubia osadiť v požadovanom spáde (min. 2%).
Zhotoviteľ je POVINNÝ pred zakrytím vykonať tlakovú skúšku vody a skúšku tesnosti kanalizácie. O skúškach vyhotoviť PROTOKOL.
Rozvody TÚV a SV izolovať izoláciou typu TUBOLIT (alebo ekvivalentom) v normou požadovanej hrúbke.
Projektant nenesie zodpovednosť za funkčnosť systému v prípade, že montáž nebola vykonaná v súlade s touto PD, platnými normami a technologickými postupmi výrobcu.

LEGENDA MIESTNOSTÍ 02.OP.05 / SU – A 102:

Č.M.	NÁZOV MIESTNOSTI	PLOCHA (m²)	POPIS POVRCHOVÝCH ÚPRAV					
			STENY		STROPY		PODLAHA	
			DRUH	OBKLAD	DRUH	PODHĽAD	DRUH	SOKEL
1.01	PRIESTOR KAVIARNE	119.60	DVOJNÁSOBNÝ NÁTER	–	NÁSTREK EXISTUJÚCEHO PODHĽADU	–	KERAMICKÁ DLAŽBA	–
1.02	PRIESTOR BARU	14.62	DVOJNÁSOBNÝ NÁTER	NAD PRACOVNOU DOSKOU		–	KERAMICKÁ DLAŽBA	KERAMICKÁ DLAŽBA V. 70 mm
1.03	KUCHYNKA	10.41	DVOJNÁSOBNÝ NÁTER	NAD PRACOVNOU DOSKOU		SDK PODHĽAD S.V. 2800 mm	KERAMICKÁ DLAŽBA	KERAMICKÁ DLAŽBA V. 70 mm
1.04	SKLAD	5.53	DVOJNÁSOBNÝ NÁTER	–		SDK PODHĽAD S.V. 3800 mm	KERAMICKÁ DLAŽBA	KERAMICKÁ DLAŽBA V. 70 mm
1.05	UMYVÁRKA	1.68	DVOJNÁSOBNÝ NÁTER	KERAMICKÝ OBKLAD V. 1,2 m		SDK PODHĽAD S.V. 2800 mm	KERAMICKÁ DLAŽBA	KERAMICKÝ OBKLAD V. 1,2 m
1.06	TOALETA	2.21	DVOJNÁSOBNÝ NÁTER	KERAMICKÝ OBKLAD V. 1,2 m		SDK PODHĽAD S.V. 2800 mm	KERAMICKÁ DLAŽBA	KERAMICKÝ OBKLAD V. 1,2 m
CELKOVÁ ÚŽITKOVÁ PLOCHA		154.05						

LEGENDA ZARIAĎOVACÍCH PREDMETOV A ARMATÚR

WC	ZÁVESNÉ WC, INŠTALAČNÝ PRVOK PRE ZÁVESNÉ WC SO ZABUDOVANOU SPLACHOVACOU NÁDRŽKOU A ZÁPACHOVOU UZÁVIERKOU, S REDUKCIOU NA D 110
U	UMÝVADLO, INŠTALAČNÝ PRVOK PRE UMÝVADLO, ZÁPACHOVÁ UZÁVIERKA D 40
D	KUCHYNSKÝ DREZ, DREZOVÁ ZÁPACHOVÁ UZÁVIERKA D 50
K	KÁVOVAR, ZÁPACHOVÁ UZÁVIERKA D 32
UR	UMÝVAČKA RIADU S INTEGROVANOU PODOMIETKOVOU ZÁPACHOVOU UZÁVIERKOU D 40
F	FANCOIL
PO	PRIETOKOVÝ OHRIEVAČ ESH 5 U-N Trend (2kW)
ZS	ZELENÁ STENA, VÝŠKA NAPOJENIA +4,050mm NAD PODLAHOU

SU – A 102	
Plocha nájmu (Leasing):	171,80 m²
Podlahová plocha:	154,05 m²

0,000 = 137,50 m n.m., B.p.v.

ZODP. PROJEKTANT	HIP	VYPRACOVAL
Ing. Norber		

STAVBA
Č. OBCHOD
INVESTOR
NÁZOV OB
PROFESIA
AUTORI PR
KONTAKTN. NÁJOMCU
OBSAH VÝ

Obsah tohto výkr