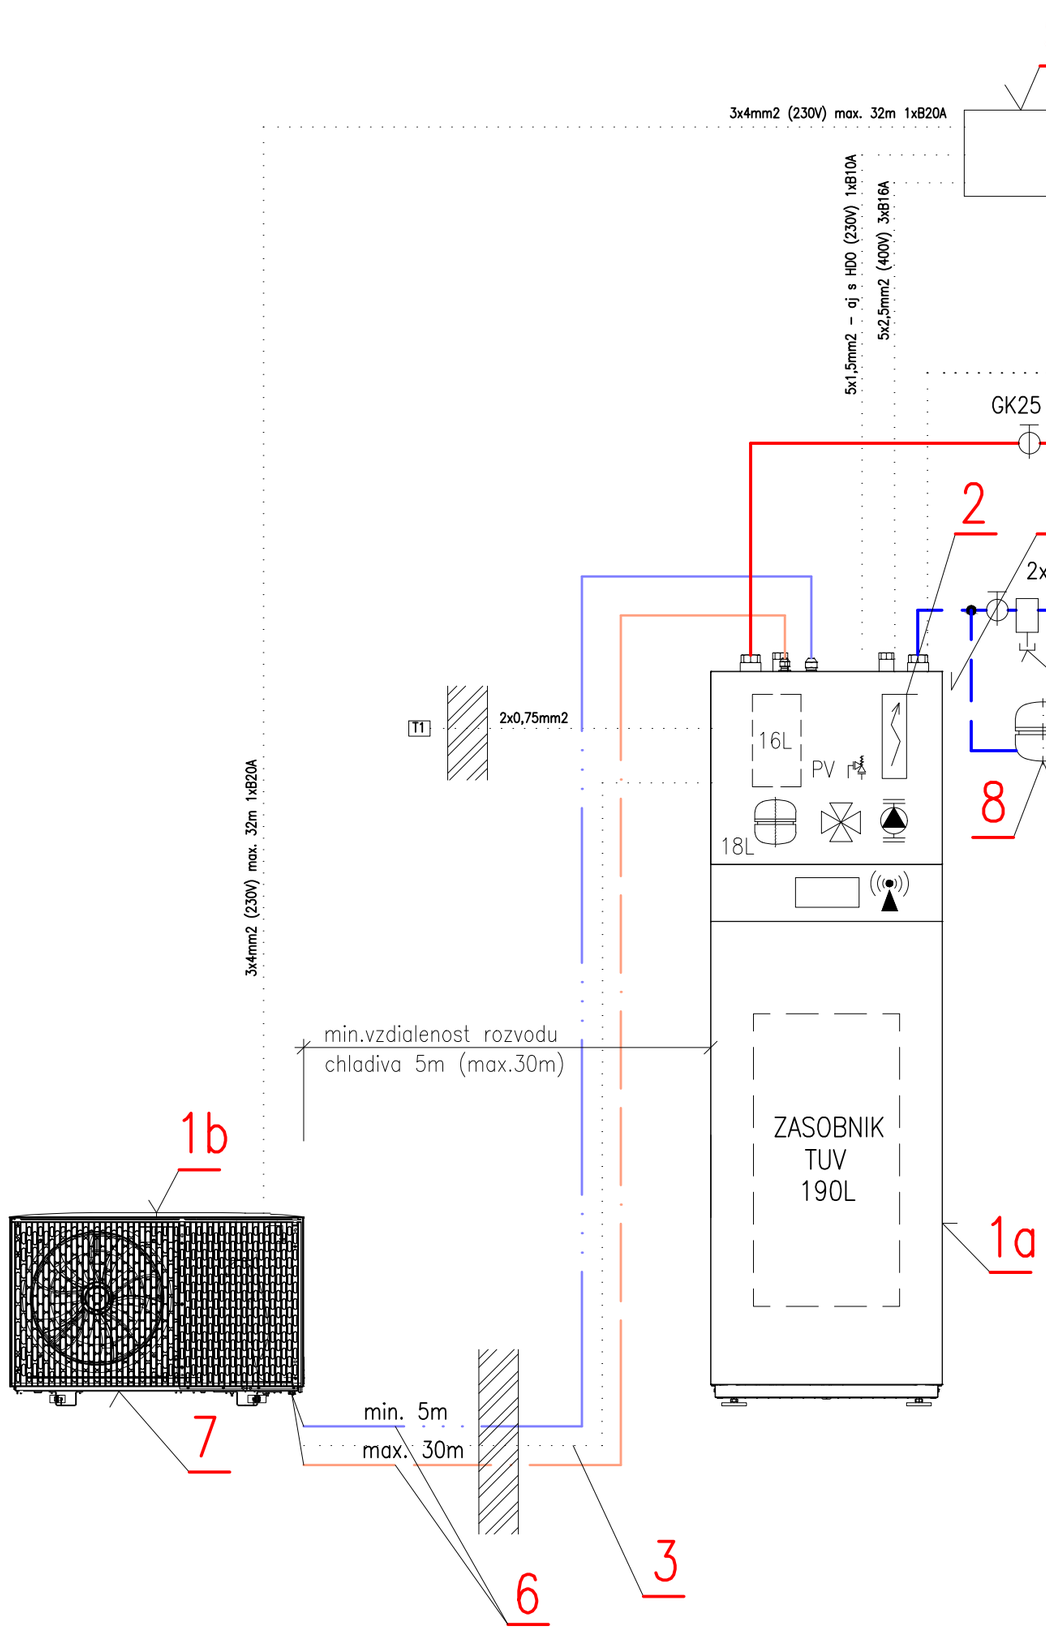


LEGENDA ZARIADENÍ:

POZ.	NÁZOV, ROZMER	P. KS
1a	VNUTORNA JEDNOTKA VITOCAL 222-S AWBT-M-E-AC 221.E10	1
1b	VONKAJ.JEDNOTKA VITOCAL 222-S AWBT-M-E-AC 221.E10 (230V)	1
	MAX.VÝSTUPNÁ TEPLOTA 60°C,TEPELNY VYKON 2,6-10,4kW A7/W35	
	EKOLOGICKE CHLADIVO R32, REGULÁCIA ONE-BASE,WIFI (Z022724)	
2	ELEKTRIC.PRIETOKOVY OHRIEVAC 8kW -v rozsahu dodavky pol.1a	1
3	CANBUS KOMUNIKACNY KABEL MEDZI JEDNOTKY 15m (ZK06217)	1
4	BEZDRATOVÉ DIALKOVE OVLADANIE VITOTROL 300-E (7959522)	1
5	ELEKTRICKY ROZVADZAC OBJEKTU	1
6	INSTALAC.SADA 16/6 NA ZEM+KONZOLA - 12,5M RURY (ZK06313)	1
7	ELEKTRIC.VYHREVNY PAS PRE VANU KONDENZATU 2,5m (ZK04098)	1
8	EXPANZNA NADOBA N25 OBJEM 25L, 3bar BIELA (7938081)	1
	NASTENNY DRZIAK PRE N25 (9572216)	1
9	ODKALOVAC S MAGNETOM A IZOLACIOU VITOTRAP 28mm (ZK04654)	1
10	PRIPOJOVACIA SADA NA OMIETKU-ZHORA	1
T1	SNIMAC VONKAJSEJ TEPLOTY - v rozsahu dodavky tep.cerpadla	1
T2	SNIMAC ROSNEHO BODU - VLHKOSTI (7181418)	1

LEGENDA POTRUBIA:

POTRUBIE - PLASTHLINNÍKOVÁ RÚRKA NAPR. GEBERIT MEPLA
PRE OKRUH PODLAHOVÉHO VYKUROVANIA, TEPLOTNÝ SPÁD 45/35°C, PRÍVOD A SPATOČKA

ROZVOD ÚK PRE PRIMÁRNY OKRUH TEPELNÉHO ČERPADLA
MATERIÁL MEĎ

LEGENDA ARMATÚR :

GK	GUĽOVÝ KOHÚT ZÁVITOVÝ , PN 16/120°C
UK	UZATVÁRACIA KLAPKA BEZPRÍRUBOVÁ , PN 16/120°C
AOV	AUTOMATICKÝ ODVZDUŠŇOVACÍ VENTIL S UZATVÁRACÍM VENTILOM , PN 16/120°C
VK	VYPÚŠŤACÍ KOHÚT , PN 16/120°C
SK	SPÄTNÁ KLAPKA ZÁVITOVÁ CELOKOVOVÁ ŤAŽKÁ , PN 16/120°C
F	FILTER ZÁVITOVÝ , SITO S OKOM 0,40mm , PN 16/120°C
OV	ODVZDUŠŇOVACÍ VENTIL , PN 16/120°C
PV	POISTNÝ VENTIL ZÁVITOVÝ PN 16/120°C

VYKUROVANIE

A-DESIG
ARCHITEKTONICKÝ ATEL
HABURSKÁ 20 ; 821 01 BRATIS

GENERÁLNY PROJEKTANT:	A-DESIGN s.r BRATISLAVA
HIP:	Ing.arch.I.POI
ZODPOVEDNÝ PROJEKTANT:	Ing. N. JÓKA
VYPRACOVAL:	Bc. Viktor Lab