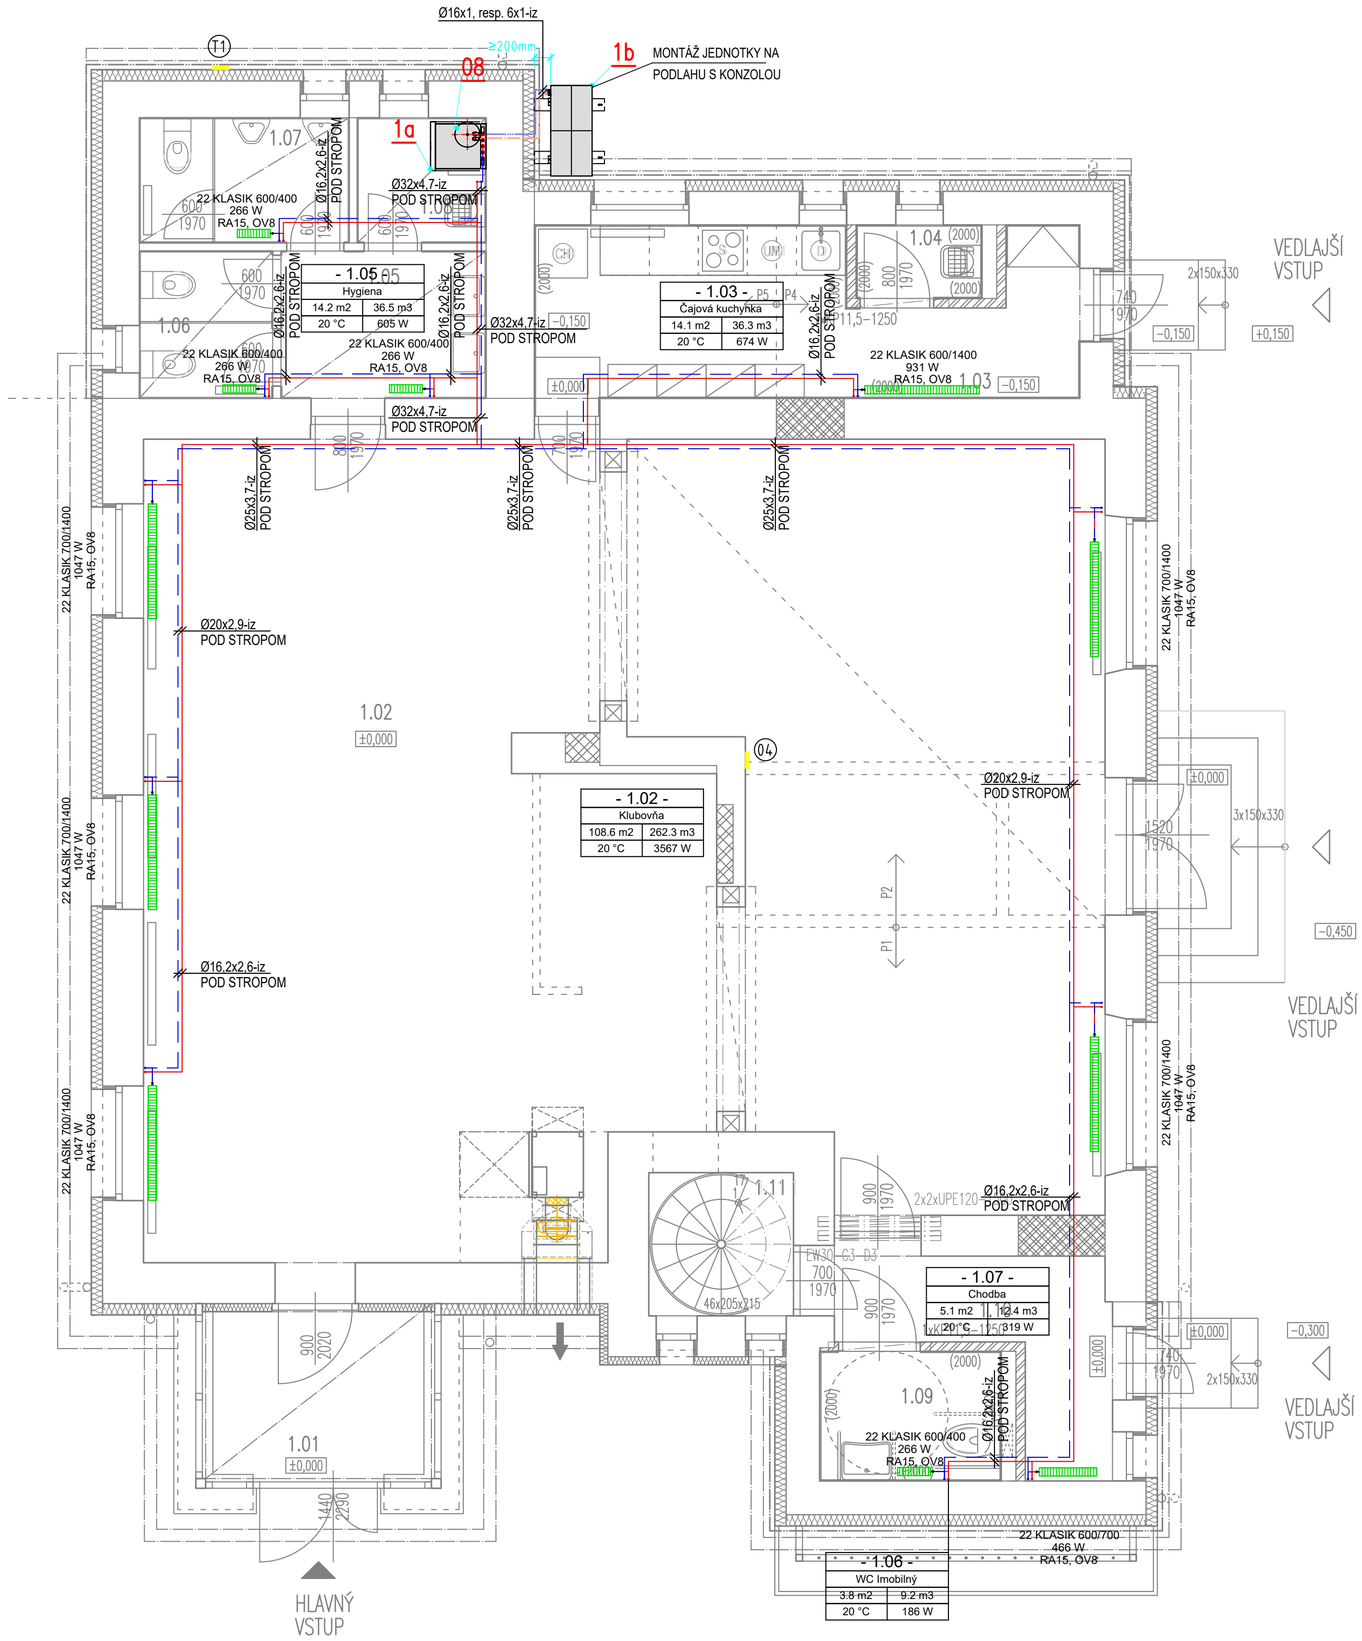



## LEGENDA MIESTNOSTÍ:

| ČÍSLO MIEST. | MIESTNOSŤ | PLOCHA M2 | POD-LAHA | PODLAHA / SOKEL | STROP / STENY |
|---|---|---|---|---|---|
| 1.01 | ZÁDVERIE | 5,18 | P1 | KERAMICKÁ DLAŽBA<br>KERAMICKÝ SOKEL, V=100MM | SADROKARTÓNOVÝ PODHLAD KAZETOVÝ<br>VNÚTORNÁ OMIETKA + VNÚTORNÁ FARBA BIELA<br>KONTAKTNÝ ZATEPLOVACÍ SYSTÉM |
| 1.02 | KLUBOVŇA | 109,80 | P1,P2 | KERAMICKÁ DLAŽBA PROTIŠMYKOVÁ<br>KERAMICKÝ SOKEL, V=100MM | SADROKARTÓNOVÝ PODHLAD + MALBA (BIELA)<br>VNÚTORNÁ OMIETKA + VNÚTORNÁ FARBA BIELA<br>VNÚTORNÁ OMIETKA + VNÚTORNÁ FARBA BIELA |
| 1.03 | ČAJOVÁ KUCHYNKA | 12,16 | P4,P5 | KERAMICKÁ DLAŽBA PROTIŠMYKOVÁ<br>– | SADROKARTÓNOVÝ PODHLAD + MALBA (BIELA)<br>VNÚTORNÁ OMIETKA + VNÚTORNÁ FARBA BIELA<br>KERAMICKÝ OBKLAD, V=2,0m<br>VNÚTORNÁ OMIETKA + VNÚTORNÁ FARBA BIELA |
| 1.04 | UPRATOVACIA MIESTNOSŤ | 1,39 | P4 | KERAMICKÁ DLAŽBA PROTIŠMYKOVÁ<br>– | SADROKARTÓNOVÝ PODHLAD + MALBA (BIELA)<br>VNÚTORNÁ OMIETKA + VNÚTORNÁ FARBA BIELA<br>KERAMICKÝ OBKLAD, V=2,0m<br>VNÚTORNÁ OMIETKA + VNÚTORNÁ FARBA BIELA |
| 1.05 | PREDSIEŇ WC | 4,52 | P1 | KERAMICKÁ DLAŽBA<br>– | SADROKARTÓNOVÝ PODHLAD KAZETOVÝ<br>KERAMICKÝ OBKLAD, V=PO STROP |
| 1.06 | WC ŽENY | 2,93 | P1 | KERAMICKÁ DLAŽBA<br>– | SADROKARTÓNOVÝ PODHLAD KAZETOVÝ<br>KERAMICKÝ OBKLAD, V=PO STROP |
| 1.07 | WC MUŽI | 3,92 | P1 | KERAMICKÁ DLAŽBA<br>– | SADROKARTÓNOVÝ PODHLAD KAZETOVÝ<br>KERAMICKÝ OBKLAD, V=PO STROP |
| 1.08 | TECHNICKÁ MIESTNOSŤ +UPRATOVACIA MIESTNOSŤ | 2,41 | P1 | KERAMICKÁ DLAŽBA<br>– | SADROKARTÓNOVÝ PODHLAD KAZETOVÝ<br>KERAMICKÝ OBKLAD, V=PO STROP |
| 1.09 | WC IMOBILNÍ | 3,52 | P1 | KERAMICKÁ DLAŽBA PROTIŠMYKOVÁ<br>– | SADROKARTÓNOVÝ PODHLAD + MALBA (BIELA)<br>VNÚTORNÁ OMIETKA + VNÚTORNÁ FARBA BIELA<br>KERAMICKÝ OBKLAD, V=2,0m<br>VNÚTORNÁ OMIETKA + VNÚTORNÁ FARBA BIELA |
| 1.10 | CHODBA | 5,33 | P1 | KERAMICKÁ DLAŽBA PROTIŠMYKOVÁ<br>KERAMICKÝ SOKEL, V=100MM | SADROKARTÓNOVÝ PODHLAD + MALBA (BIELA)<br>VNÚTORNÁ OMIETKA + VNÚTORNÁ FARBA BIELA<br>KERAMICKÝ OBKLAD, V=2,0m<br>VNÚTORNÁ OMIETKA + VNÚTORNÁ FARBA BIELA |
| 1.11 | SCHODISKO | 3,10 | P1,P3 | KERAMICKÁ DLAŽBA PROTIŠMYKOVÁ<br>KERAMICKÝ SOKEL, V=100MM | –<br>VNÚTORNÁ OMIETKA + VNÚTORNÁ FARBA BIELA |
| | 1.NP SPOLU | 154,26 | | | |

## LEGENDA VYKUROVACÍCH TELIES:

SPÔSOB ZNAČENIA — OCEĽOVÉ DOSKOVÉ VYKUROVACIE TELESO KLASIK
TYP KLASIK, S BOČNÝM PRIPOJENÍM

22 KLASIK 600/1200
- 22 — TYP DVOJRADOVÝ
- KLASIK — PREVEDENIE KLASIK - S BOČNÝM PRIPOJENÍM
- 600 — STAVEBNÁ VÝŠKA V MILIMETROCH
- 1200 — STAVEBNÁ DĹŽKA V MILIMETROCH

## LEGENDA POTRUBIA:

POTRUBIE - PLASTHLINNÍKOVÁ RÚRKA RAUTITAN STABIL, fy. REHAU
PRE OKRUHY KONVEKČNÉHO VYKUROVANIA, TEPLOTNÝ SPÁD 50/40°C, PRÍVOD A SPATOČKA
ROZVOD ÚK PRE PRIMÁRNY OKRUH TEPELNÉHO ČERPADLA
MATERIÁL MEĎ


## LEGENDA ZARIADENÍ A ARMATÚR :

| | |
|---|---|
| 1a | KOMPAKTNÁ VNÚTORNÁ JEDNOTKA TEPELNÉHO ČERPADLA VITOCAL 222-S AWBT-M-E 221.E06 |
| 1b | VONKAJ.JEDNOTKA VITOCAL 222-S AWBT-M-E 221.E06 (230V)<br>MAX.VÝSTUPNÁ TEPLOTA 60°C,TEPELNY VYKON 2,6-7,5kW A7/W35<br>EKOLOGICKE CHLADIVO R32, REGULÁCIA ONE-BASE,WIFI (Z022722) |
| 04 | BEZDRÔTOVÉ DIAĽKOVÉ OVLÁDANIE VITOTROL 300-E |
| 08 | UZAVRETÁ TLAKOVÁ EXPANZNÁ NÁDOBA VIESSMANN N25 OBJEM 25L, 3bar<br>ROZMERY : Ø=308 mm, VÝŠKA 477 mm , HMOTNOSŤ 4,3 kg + NASTENNY DRZIAK PRE N25 (9572216) |
| T1 | SNÍMAČ VONKAJŠEJ TEPLOTY |
| RA | RADIATOROVÝ VENTIL NAPR. VERAFIX-VKE, UZATVÁRACIE ŠRÓBENIE H-BLOK S VONKAJŠÍM ZÁVITOM<br>EUROKONUS PRE VYKUROVACIE TELESÁ TYPU VENTIL-KOMPAKT, ROHOVÝ, DN15<br>PRIPOJENIE RADIÁTORA VONKAJŠÍ ZÁVIT 1/2", PRIPOJENIE RÚRKY VONKAJŠÍ ZÁVIT 3/4"<br>TERMOSTATICKÁ HLAVICA SO VSTAVANÝM KVAPALINOVÝM SNÍMAČOM, ROZSAH 6-28°C |
| OV | ODVZDUŠŇOVACÍ VENTIL , PN 16/120°C |

## POZNÁMKA :

- V PRÍPADE NEJASNOSTÍ VO VÝKRESOVEJ DOKUMENTÁCII KONTAKTOVAŤ ZODPOVEDNÉHO PROJEKTANTA
- VŠETKY ROZMERY STAVEBNÝCH PRÁC KONTROLOVAŤ NA MIESTE STAVBY
- PRED UVEDENÍM SYSTÉMU DO PREVÁDZKY JE POTREBNÉ VYKONAŤ DÔKLADNÝ PREPLACH SYSTÉMU S VYČISTENÍM VŠETKÝCH FILTROV NA ROZVODE
- PO NAPUSTENÍ SYSTÉMU JE POTREBNÉ VYKONAŤ JEHO ODVZDUŠNENIE
- DODÁVATEL STAVBY JE POVINNÝ REALIZOVAŤ VŠETKY PRÁCE V ZMYSLE PLATNÝCH STN EN S DODRŽANÍM TECHNOLOGICKÝCH A BEZPEČNOSTNÝCH POSTUPOV. ĎALEJ JE POVINNÝ REŠPEKTOVAŤ USTANOVENIÁ STN 730421 O PRÍSLUŠNÝCH ROZMEROVÝCH ODCHÝLKACH REALIZOVANÝCH KONŠTRUKCIÍ PROTI PROJEKTOVANÉMU STAVU. KAŽDÚ ODCHÝLKU OD PROJEKTU JE POTREBNÉ PREROKOVAŤ S GP.

## DETAIL OSADENIA VONKAJŠEJ JEDNOTKY NA STENE NA KONZOLE

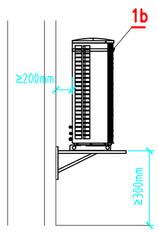


Autorom projektu a výhradným vlastníkom autorských a majetkových práv je spoločnosť M PRO s.r.o, Ing. Andrej Marcík. Projektová dokumentácia, ako aj samotné architektonické dielo podlieha autorskej ochrane podľa zákona 185/2015 Z. z. - Autorský zákon v znení neskorších predpisov. Vyhotovenie napodobenín, rozmnožovanie a akékoľvek úpravy bez písomného súhlasu autora je trestné.

Výškové osadenie: ±0,000= 130,875 m.n.m. (BPV)
Súradnicový systém: JTSK

Generálny projektant: **M PRO s.r.o.**
Kadnárova 23, 831 52 Bratislava
mprosro@gmail.com +421 905 489 533
Ing. Andej Marcík

Projektant časti: **JOPRO group s.r.o.**
Trnavská cesta 67, 821 04 Bratislava
@jopro.sk +421 905 549 978
Ing.

Autor/Spoluautor:
Ing. Andrej Marcík
Ing. Daniela Marcíková
Ing. Miroslav Greguš
Ing.Ing.arch.Mgr.art.J.Kuráň,PhD.

Zodpovedný projektant: Ing.
Vypracoval: Bc. Viktor Labovský

Orientácia na svetové strany:

Názov projektu / stavby:

# OBECNÝ DOM LIMBACH