RZ 1 - 1. NP (7)

ROZDEĽOVACIA STANICA PRE PODLAHOVÉ VYKUROVANIE 45/35°C
NAPR. FY. REHAU HKV-D 7, SKRINKA ROZDEĽOVAČA NA STENU 130/805 (805x730x130mm)
REGULAČNÝ ROZVÁDZAČ REHAU NEA (230V) (1ks)
PRIESTOROVÝ TERMOSTAT REHAU NEA (230V) (2ks)
ELEKTRICKÝ SERVOPOHON REHAU (230V) (7ks)

RZ 1 – 1. NP (7/7) (tp=45.0°C)	1.08 – Kupelna
PZ 1: Keramická dlažba 10 mm	VYK: PZ:33.4°C
Systém VARIONOVA	Rúrka RAUTHERM S 17x2,0
lo/lp=37.2 m/11.8 m	S=3.7 m2
Lpz=100 [mm]	VYK: 0.6 l/min

RZ 1 – 1. NP (7/1) (tp=45.0°C)	1.10 – Technicka miestnost
PZ 1: Keramická dlažba 10 mm	VYK: PZ:31.7°C
Systém VARIONOVA	Rúrka RAUTHERM S 17x2,0
lo/lp=19.4 m/13.9 m	S=1.9 m2
Lpz=100 [mm]	VYK: 0.4 l/min

RZ 1 – 1. NP (7/2) (tp=45.0°C)	1.12 – Obývačka + jedalen
PZ 1: PVC 5 mm	VYK: PZ:28.0°C [OZ:28.6°C]
Systém VARIONOVA	Rúrka RAUTHERM S 17x2,0
lo/lp=82.1 m/18.7 m	S=10.5 m2
Lpz/Loz=150/100 [mm]	VYK: 1.2 l/min

RZ 1 – 1. NP (7/6) (tp=45.0°C)	1.07 – Spálňa
PZ 1: PVC 5 mm	VYK: PZ:29.4°C
Systém VARIONOVA	Rúrka RAUTHERM S 17x2,0
lo/lp=74.3 m/7.7 m	S=11.2 m2
Lpz=150 [mm]	VYK: 1.0 l/min

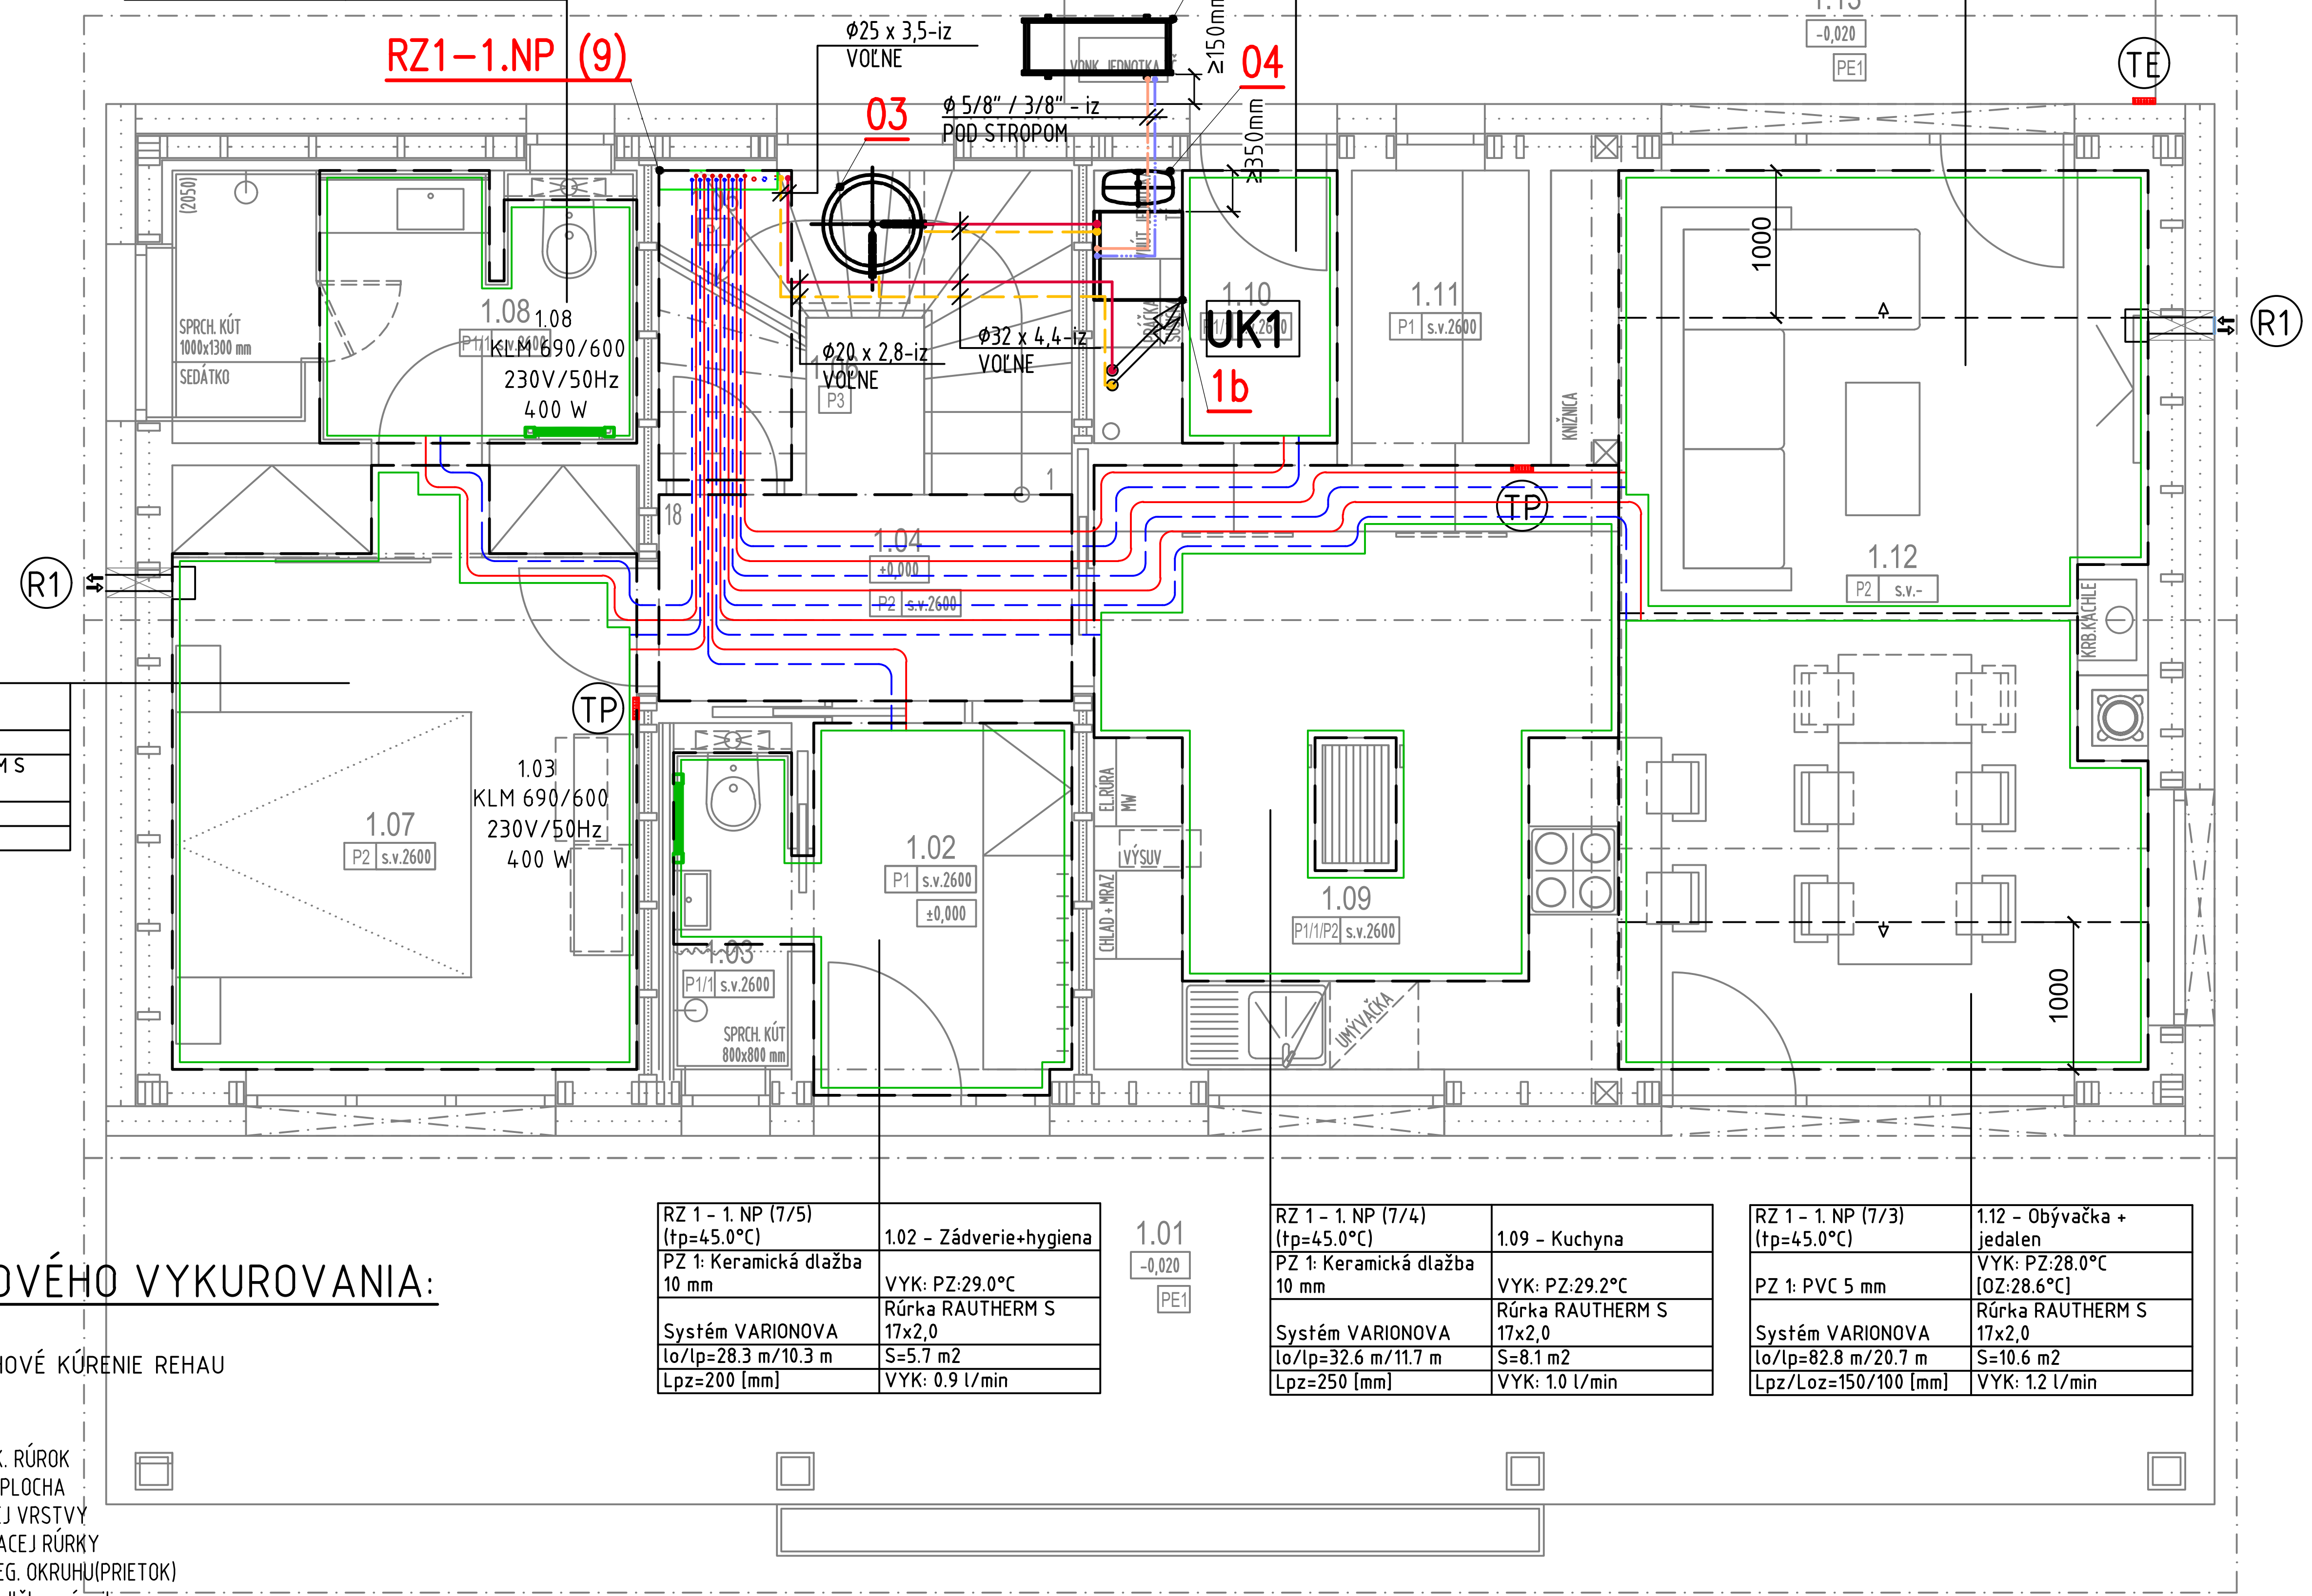

RZ 1 – 1. NP (7/5) (tp=45.0°C)	1.02 – Zádverie+hygiena
PZ 1: Keramická dlažba 10 mm	VYK: PZ:29.0°C
Systém VARIONOVA	Rúrka RAUTHERM S 17x2,0
lo/lp=28.3 m/10.3 m	S=5.7 m2
Lpz=200 [mm]	VYK: 0.9 l/min

RZ 1 – 1. NP (7/4) (tp=45.0°C)	1.09 – Kuchyna
PZ 1: Keramická dlažba 10 mm	VYK: PZ:29.2°C
Systém VARIONOVA	Rúrka RAUTHERM S 17x2,0
lo/lp=32.6 m/11.7 m	S=8.1 m2
Lpz=250 [mm]	VYK: 1.0 l/min

RZ 1 – 1. NP (7/3) (tp=45.0°C)	1.12 – Obývačka + jedalen
PZ 1: PVC 5 mm	VYK: PZ:28.0°C [OZ:28.6°C]
Systém VARIONOVA	Rúrka RAUTHERM S 17x2,0
lo/lp=82.8 m/20.7 m	S=10.6 m2
Lpz/Loz=150/100 [mm]	VYK: 1.2 l/min

LEGENDA PODLAHOVÉHO VYKUROVANIA:

🟩 PODLAHOVÉ KÚRENIE REHAU

Lpz=100 [mm]	ROZOSTUP VYK. RÚROK
S=8,6 m2	VYKUROVACIA PLOCHA
PZ: Keramická dlažba	TYP NÁŠLAPNEJ VRSTVY
Rúrka RAUTHERM S 17x2,0	TYP VYKUROVACEJ RÚRKY
Nast.=0,63 (48 kg/h)	NASTAVENIE REG. OKRUHU(PRIETOK)
lo/lp=12.7 m/1.6 m	Dlžka okruhu / dlžka prípojky
RZ 1. NP-1/9 (tp=45°C)	rozdelovač na 1 .NP 1. napojenie a 9 vetiev (tp - teplota prívodu)
VARIONOVA	typ prichytenia potrubi pre podlahove kurenie
PZ:21°C	maximálna povrchová teplota podlahovej zóny

- 1.02 -		- 1.03 -		- 1.04 -		- 1.07 -		- 1.08 -		- 1.09 -		- 1.10 -		- 1.12 -	
Zádverie		WC + Sprcha		Chodba		Spálňa		Kupelna		Kuchyna		Technicka miestnost		Obývačka + jedalen	
4.1 m2	10.7 m3	2.1 m2	5.5 m3	4.9 m2	12.7 m3	12.9 m2	33.6 m3	5.6 m2	15.7 m3	15.5 m2	40.2 m3	3.1 m2	7.9 m3	21.8 m2	56.6 m3
20 °C	234 W	24 °C	108 W	20 °C	82 W	24 °C	596 W	24 °C	334 W	22 °C	524 W	20 °C	206 W	22 °C	1585 W

LEGENDA VYKUROVACÍCH TELIES:

▥ OCEĽOVÉ DOSKOVÉ VYKUROVACIE TELESO RADIK
SPÔSOB ZNAČENIA TYP RADIK, SO SPODNÝM PRIPOJENÍM

33 VK 900 /900
- 900 (druhé) – STAVEBNÁ DĹŽKA V MILIMETROCH
- 900 (prvé) – STAVEBNÁ VÝŠKA V MILIMETROCH
- VK – PREVEDENIE VENTIL KOMPAKT - SO SPODNÝM PRIPOJENÍM
- 33 – TYP DVOJRADOVÝ

🟩 ELEKTRICKÉ PRIAMOVÝHREVNÉ REBRÍKOVÉ VYKUROVACIE TELESO
TYP KORALUX LINEAR MAX-ERA, FY. KORADO

🟥 FÓLIOVÁ TECHNOLÓGIA SYSTÉMU VYHRIEVANIA NA ZÁKLADE DLHOVLNNÉHO INFRAČERVENÉHO ŽIARENIA

LEGENDA POTRUBIA:

POTRUBIE - PLASTHLINNÍKOVÁ RURKA PE-Xa/AL/PE napr. RAUTITAN Stabil REHAU
SPÁJANÉ LISOVANÍM, IZOLOVANÉ POTRUBIE, TEPLOTNÝ SPÁD 45/35°C. PRE PODLAHOVÉ VYKUROVANIE

🟥 POTRUBIE - PLASTHLINNÍKOVÁ RURKA PE-Xa/AL/PE napr. RAUTITAN Stabil REHAU
SPÁJANÉ LISOVANÍM, IZOLOVANÉ POTRUBIE, TEPLOTNÝ SPÁD 45/35°C.

🟦 ROZVOD ÚK PRE PRIMÁRNY OKRUH TEPELNÉHO ČERPADLA
PRE OKRUHY KONVEKČNÉHO VYKUROVANIA, PRÍVOD A SPATOČKA
MATERIÁL MEĎ

LEGENDA ZARIADENÍ A ARMATÚR :

1a	VNÚTORNÁ JEDNOTKA TEPELNÉHO ČERPADLA BRILON ELCO AEROTOP SPLIT 08.2 M-CR 1Z
1b	VONKAJ.JEDNOTKA BRILON ELCO AEROTOP SPLIT 08.2 M-CR 1Z MAX.VÝSTUPNÁ TEPLOTA 60°C,TEPELNY VYKON 8kW A7/W35, 3f-400V
03	AKUMULAČNÍ ZÁSOBNÍK VYKUROVACEJ VODY WPPS 130, Objem 130l
04	UZAVRETÁ TLAKOVÁ EXPANZNÁ NÁDOBA VIESSMANN C35 OBJEM 35L, 3bar
TP	TERMOSTAT PRIESTOROVÝ REMOCON PLUS 2
TE	SNÍMAČ VONKAJŠEJ TEPLOTY
R1	LOKÁLNA REKUPERAČNÁ JEDNOTKA TYPU NAPR. VIESSMANN VITOVENT 100-D

- PRÍPADNÉ ZMENY PROJEKTU JE NUTNÉ PRED ICH REALIZÁCIOU PREKONZULTOVAŤ S AUTOROM PROJEKTU, ICH REALIZÁCIA JE MOŽNÁ NA ZÁKLADE JEHO PÍSOMNÉHO SÚHLASU !
- PRÍPADNÉ NEJASNOSTI V PROJEKTE JE NUTNÉ BEZODKLADNE OZNÁMIŤ ZODPOVEDNÉMU PROJEKTANTOVI !
- PROJEKTOVANÉ ROZMERY STAVEBNÝCH VÝROBKOV A KONŠTRUKCIÍ JE NUTNÉ PRED ICH ZADANÍM DO VÝROBY OVERIŤ PREMERANÍM PRIAMO NA STAVBE !

±0,000 = 300 mm nad U.T.

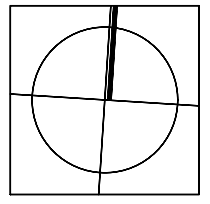

AUTOR PROJEKTU
ZODPOVEDNÝ PRO
INVESTOR
MIESTO STAVBY
PROFESIA
DRUH STAVBY
NÁZOV VÝKRESU
OZNAČENIE VÝKRE