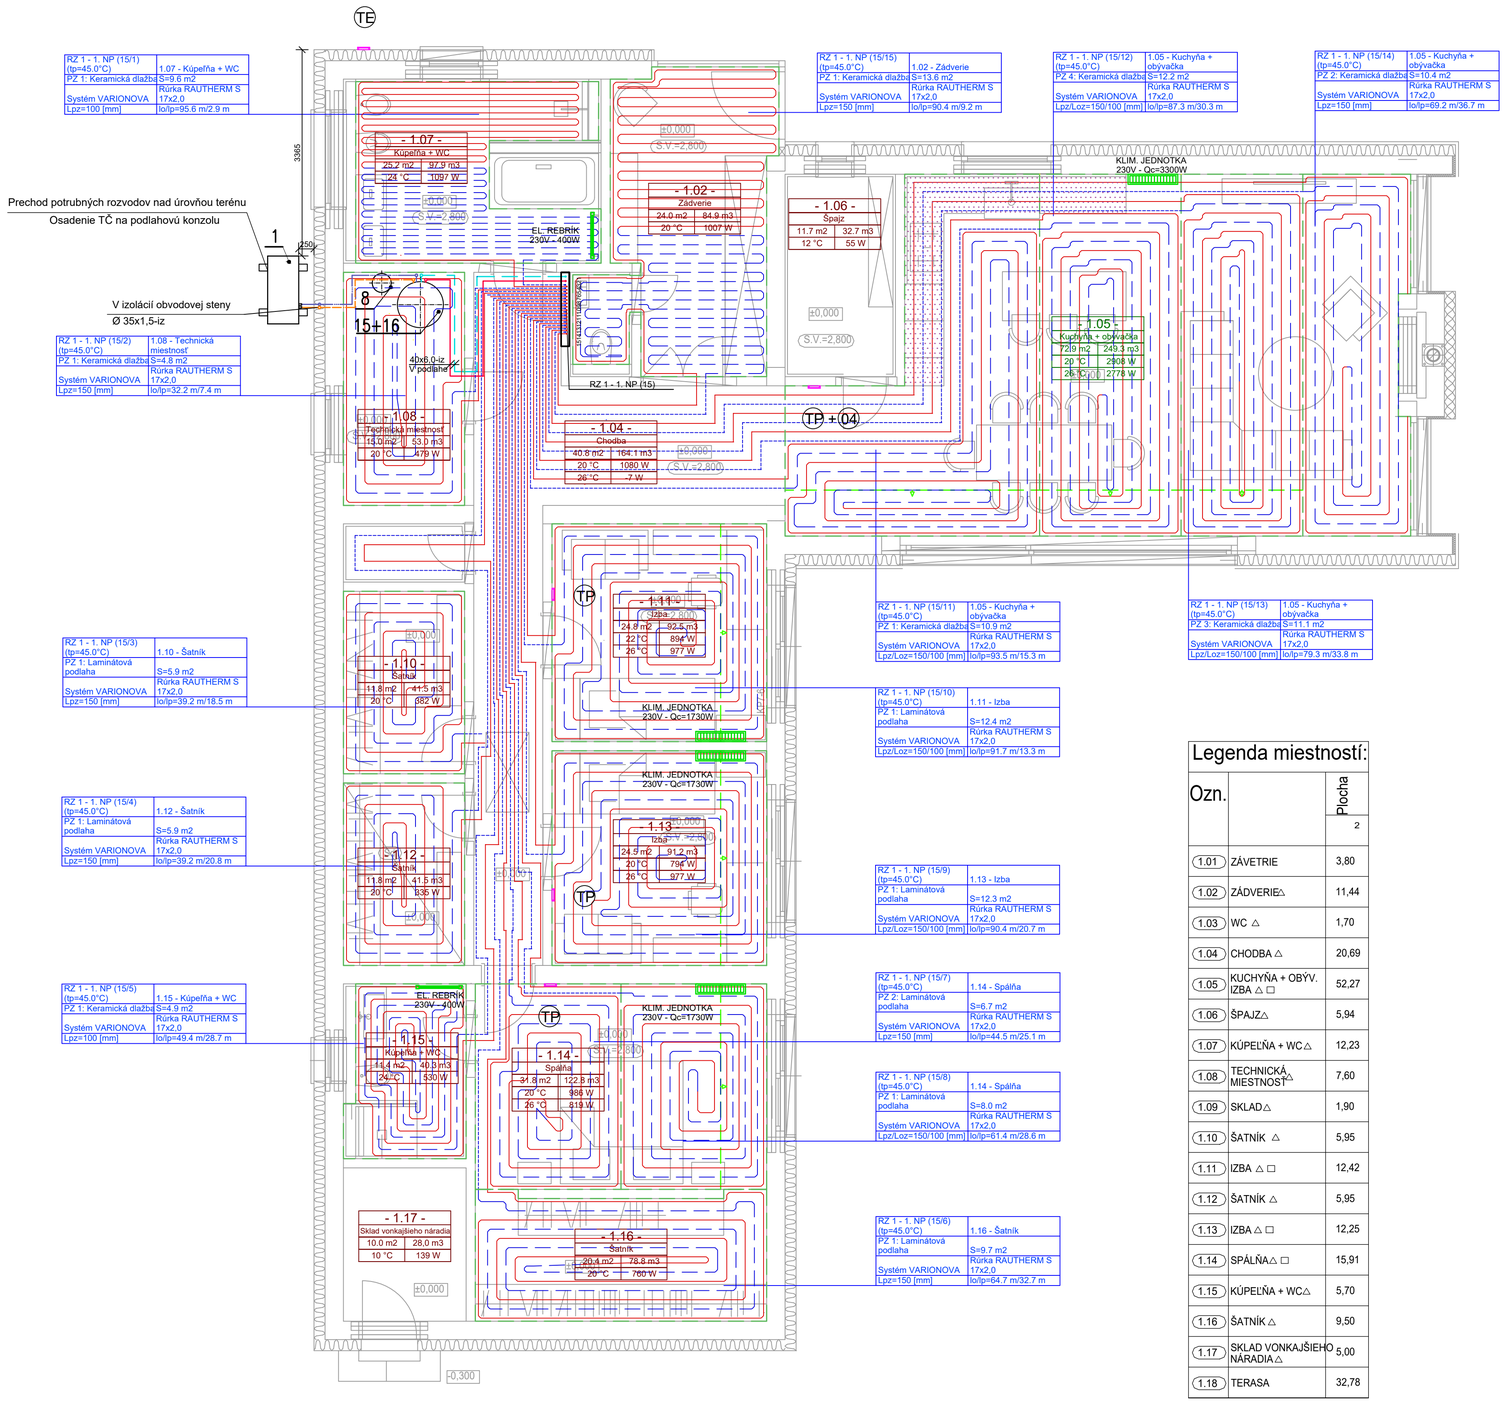


LEGENDA POTRUBÍ:

PLASTHLINÍKOVÉ POTRUBIE NAPR. RAUTHERM S 17×2,0 REHAU, TEPLOTNÝ SPÁD 45/35 °C, VEDENÉ V PODLAHE.

PLASTHLINÍKOVÉ POTRUBIE MATERIÁL: PE-XA/AL/PE NAPR. RAUTITAN STABIL, ZAIZOLOVANÉ POTRUBIE, TEPLOTNÝ SPÁD 45/35 °C.

MEDENÉ POTRUBIE PRIMÁRNEHO OKRUHU TEPELNÉHO ČERPADLA: CU Φ12×1, 6×1-IZ.

LEGENDA ZARIADENÍ:

1A TEPELNÉ ČERPADLO NAPR.: VITOCAL 200-A ie B12. VÝKON (A7/W35): 3,6 – 12,8 KW.

4 OVLÁDANIE: BEZDRÔTOVÝ DIAĽOVÝ OVLÁDAČ NAPR. VITOTROL 300-E.

8 EXPANZNÁ NÁDOBA NAPR: VIESSMANN N25 (OBJEM 25 L, MAX. TLAK 4 BAR).

15 ZÁSOBNÍK TV VITOCELL 100-V TYP CVWC OBJEM 300L

16 AKUMULACNY ZASOBNIK VITOCELL 100-E TYP MSCA 50L

TP IZBOVÝ REGULÁTOR NAPR.: REHAU NEA SMART 2.0 (MERANIE TEPLOTY).

TE SNÍMAČ TEPLOTY EXTERIÉRU.

REBRÍKOVÉ ELEKTRICKÉ VYKUROVACIE TELESO 230V

KLIMATIZAČNÁ JEDNOTKA MONOBLOK min. výkon 1500W napr. INNOVA 2.0 MINI 9 HP / NEXTAC

LEGENDA PODLAHOVÉHO VYKUROVANIA:

Podlahové vykurovanie Rehau

Zóna zníženého výkonu pod kuchynskou linkou.

Vykurovacia plocha: S=4.2 m²

Typ nášľapnej vrstvy (PX): Keramická dlažba

Typ vykurovacej rúrky: Rúrka Rautherm S 17×2,0

Rozdeľovač: Rozdeľovač Rehau , skrinka rozdeľovača 1. NP, napojenie 15 okruhov (tp=45 °C)

Systém uchytenia: Varionova – typ prichytenia potrubia pre podlahové kúrenie

R-Z ZOSTAVA ROZDEĽOVAČA PODLAHOVÉHO VYKUROVANIA (TEPLOTNÝ SPÁD 45/35 °C)

15-OKRUHOVÝ ROZDEĽOVAČ NAPR. REHAU HKVD SX-AG 15, SKRINKA (ROZMER 510 X 907 X 86 MM). ĎIALKOVÉ OVLÁDANIE TERMOSTATOV NAPR. REHAU NEA (230V)

4 KS PRIESTROVÝ TERMOSTAT NAPR. REHAU NEA (230V)

15 KS ELEKTRICKÝ SERVO-POHON (230V)

POZNÁMKY :

- V PRÍPADE AKÝCHKOĽVEK NEJASNOSTÍ V PROJEKTOVEJ DOKUMENTÁCII JE NUTNÉ KONTAKTOVAŤ ZODPOVEDNÉHO PROJEKTANTA.
- VŠETKY STAVEBNÉ ROZMERY A PRESTUPY JE POTREBNÉ OVERIŤ PRIAMO NA MIESTE REALIZÁCIE.
- PRED SAMOTNÝM SPUSTENÍM SYSTÉMU DO PREVÁDZKY SA MUSÍ VYKONAŤ DÔKLADNÝ PREPLACH ROZVODOV A VYČISTENIE VŠETKÝCH INŠTALOVANÝCH FILTROV.
- PO NAPUSTENÍ VYKUROVACEJ SÚSTAVY MÉDIOM JE NEVYHNUTNÉ ZABEZPEČIŤ JEJ POSTUPNÉ ODVZDUŠNENIE.
- ZHOTOVITEĽ JE POVINNÝ POSTUPOVAŤ V SÚLADE S PLATNÝMI NORMAMI STN EN A DODRŽIAVAŤ TECHNOLOGICKÉ AJ BEZPEČNOSTNÉ PREDPISY. ZÁROVEŇ MUSÍ REŠPEKTOVAŤ USTANOVENIA STN 730421 O ROZMEROVÝCH ODCHÝLKACH. KAŽDÚ ZMENU OPROTI PROJEKTU JE NUTNÉ VOPRED SKONZULTOVAŤ S HIP.
- OTVORY PRE PRESTUPY INŽINIERSKYCH SIETÍ A POTRUBNÝCH ROZVODOV V OBJEKTE JE POTREBNÉ PRIPRAVIŤ POČAS REALIZÁCIE HRUBEJ STAVBY.
- TÁTO DOKUMENTÁCIA NENAHRÁDZA REALIZAČNÚ DOKUMENTÁCIU STAVBY!
-VÝŠKOVÁ ÚROVEŇ ±0,000 V PROJEKTE ZODPOVEDÁ ÚROVNI FINÁLNEJ NÁŠĽAPNEJ VRSTVY PODLAHY.

Legenda miestností:

Ozn.		Plocha [m2]
1.01	ZÁVETRIE	3,80
1.02	ZÁDVERIE△	11,44
1.03	WC △	1,70
1.04	CHODBA △	20,69
1.05	KUCHYŇA + OBÝV. IZBA △ ☐	52,27
1.06	ŠPAJZ△	5,94
1.07	KÚPEĽŇA + WC△	12,23
1.08	TECHNICKÁ MIESTNOSŤ△	7,60
1.09	SKLAD△	1,90
1.10	ŠATNÍK △	5,95
1.11	IZBA △ ☐	12,42
1.12	ŠATNÍK △	5,95
1.13	IZBA △ ☐	12,25
1.14	SPÁLŇA△ ☐	15,91
1.15	KÚPEĽŇA + WC△	5,70
1.16	ŠATNÍK △	9,50
1.17	SKLAD VONKAJŠIEHO NÁRADIA△	5,00
1.18	TERASA	32,78

PROJEKTANT TZB:
TZB Smart Engineering s. r. o.
Karpatské námestie 7770/10A
831 06 Bratislava

VYPRACOVAL:
ING. VIKTOR LABOVSKÝ

ZODPOVEDNÝ PROJEKTANT
ING. JÁN BÁTOR