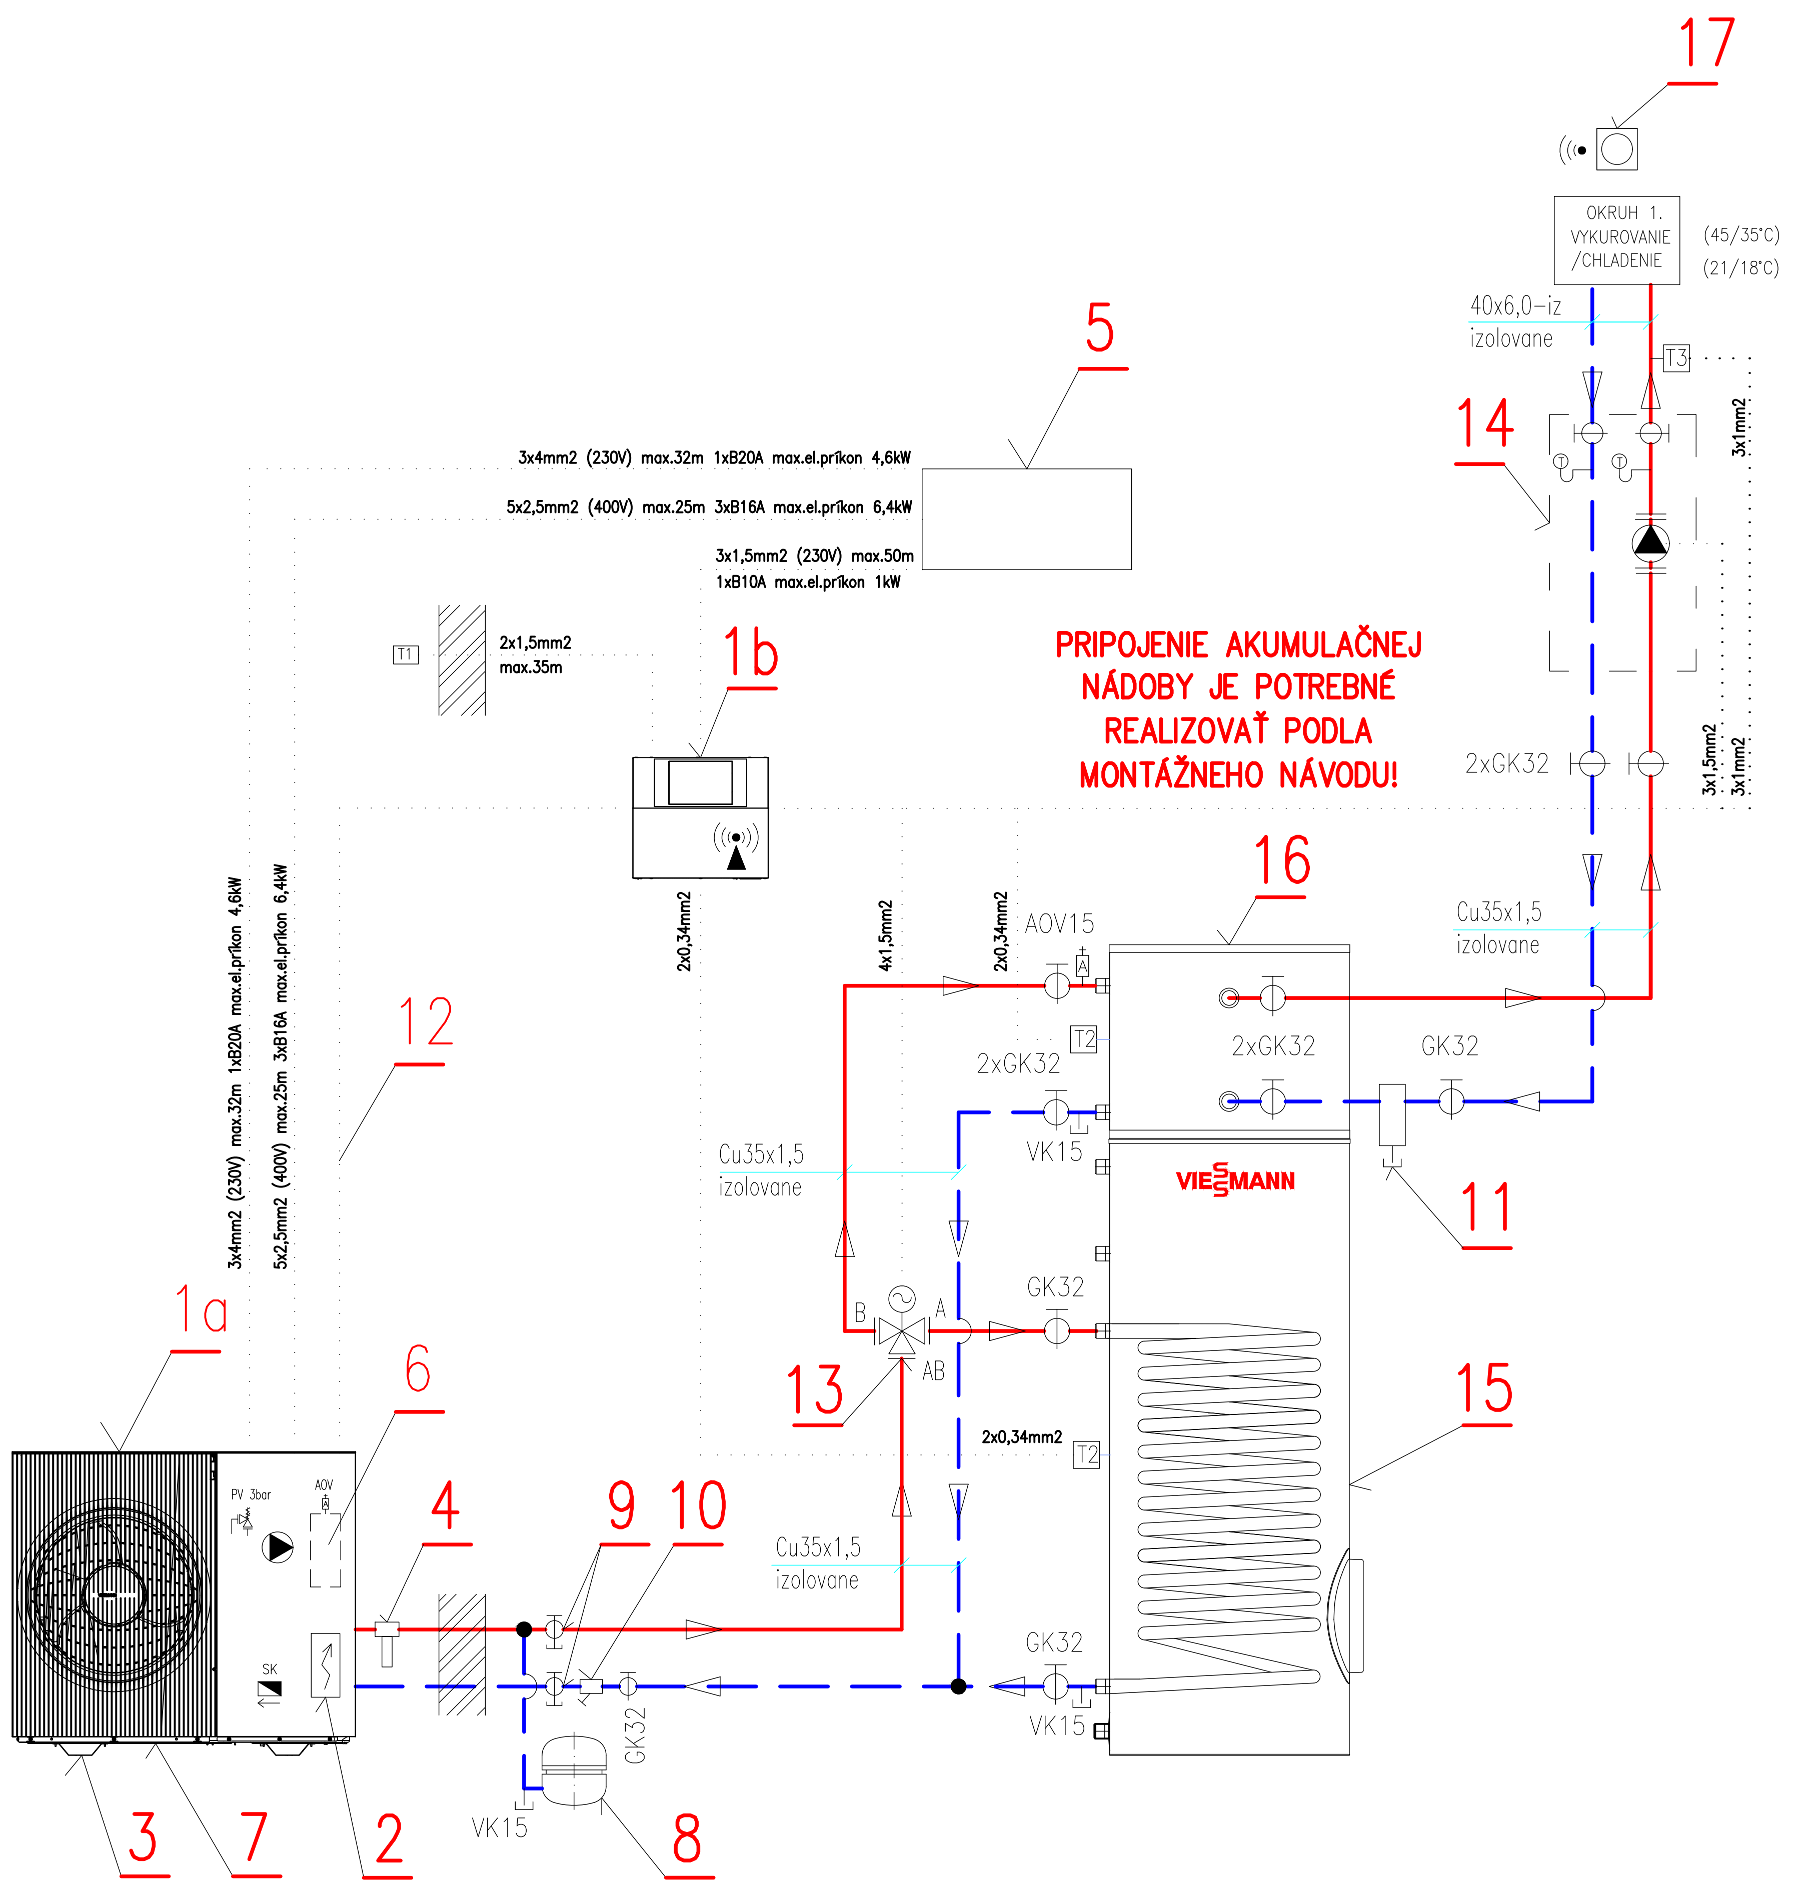

PRIPOJENIE AKUMULAČNEJ NÁDOBY JE POTREBNÉ REALIZOVAŤ PODLA MONTÁŽNEHO NÁVODU!

LEGENDA ZARIADENÍ:

POZ.	NÁZOV, ROZMER	P. KS
1a	VONKAJŠIA JEDNOTKA VITOCAL 200-A ie B12 230 V123	1
	MAX.VÝSTUPNÁ TEPLOTA 75°C, TEPELNÝ VÝKON 3,6-12,8kW A7/W35	1
	CHLADIVO R290 GWP3, ONE-BASE INTELIGENCE, WIFI (Z034465)	
1b	VNÚTORNÁ NÁSTENNÁ REGULÁCIA IDU-Controller - dodávka pol.1a	1
2	ELEKTRICKÝ PRIETOKOVÝ OHRIEVAČ 6,4kW - dodávka pol.1a	1
3	KONZOLA POD VONKAJŠIU JEDNOTKU-MONTÁŽ NA ZEM (3210409)	1
4	TERMOSTATICKÝ VENTIL PROTI ZAMRZNUTIU DN25 (ZR00220)	1
5	ELEKTRICKÝ ROZVÁDZAČ OBJEKTU	1
6	BEZPEČNOSTNÝ PLAVÁKOVÝ ODVZDUŠŇOVACÍ VENTIL-dodávka pol.1a	1
7	ELEKTRICKÝ VYHREVNÝ PÁS + VAŇA KONDENZÁTU (3210415)	1
8	EXPANZNA NADOBA N35 OBJEM 35L, 3bar BIELA (7938083)	1
	PRIPOJOVACI VENTIL PRE N35 (9572213)	1
9	SADA GULOV.KOHUTOV PRE PLNENIE A ODVZDUSNENIE (ZK06057)	1
10	GULOVY KOHUT S MAGNETICKYM FILTROM DN32 - dodávka pol.1a	1
11	ODKALOVAC S MAGNETOM A IZOLACIOU VITOTRAP 5/4" (ZK04657)	1
12	CANBUS KOMUNIKACNY KABEL MEDZI JEDNOTKY 15m (7973123)	1
13	TROJCESTNY PREPINACI VENTIL DN25 230V (7814924)	1
14	RMS BEZ ZMIESAVACA GDA211 DN32 Wilo Para 25/8 (7140702)	1
15	ZÁSOBNÍK TV VITOCELL 100-V TYP CVWC OBJEM 300L (Z026456)	1
16	AKUMULACNY ZASOBNIK VITOCELL 100-E TYP MSCA 50L 1(Z026457)	1
17	BEZDRATOVÉ DIALKOVE OVLADANIE VITOTROL 100-EH (7979559)	1
T1	SNIMAC VONKAJSEJ TEPLOTY - dodávka pol.1b	1
T2	SNIMAC TEPLOTY ZASOBNIKA - ponorny (7438702)	2
T3	SNIMAC ROSNEHO BODU 230V - VLHKOSTI (7452646)	1

LEGENDA POTRUBÍ:

PLASTHLINÍKOVÉ POTRUBIE MATERIÁL: PE-XA/AL/PE NAPR. RAUTITAN STABIL, ZAIZOLOVANÉ POTRUBIE, TEPLOTNÝ SPÁD 45/35 °C.

MEDENÉ POTRUBIE PRIMÁRNEHO OKRUHU TEPELNÉHO ČERPADLA: CU Φ12×1, 6×1-IZ.

LEGENDA ARMATÚR :

GK	GUĽOVÝ KOHÚT SO ZÁVITOM
AOV	AUTOMATICKÝ ODVZDUŠŇOVACÍ VENTIL S UZATVÁRACOU ARMATÚROU
PV	POISTNÝ VENTIL SO ZÁVITOM

POZNÁMKY :

- V PRÍPADE AKÝCHKOĽVEK NEJASNOSTÍ V PROJEKTOVEJ DOKUMENTÁCII JE NUTNÉ KONTAKTOVAŤ ZODPOVEDNÉHO PROJEKTANTA.
- VŠETKY STAVEBNÉ ROZMERY A PRESTUPY JE POTREBNÉ OVERIŤ PRIAMO NA MIESTE REALIZÁCIE.
- PRED SAMOTNÝM SPUSTENÍM SYSTÉMU DO PREVÁDZKY SA MUSÍ VYKONAŤ DÔKLADNÝ PREPLACH ROZVODOV A VYČISTENIE VŠETKÝCH INŠTALOVANÝCH FILTROV.
- PO NAPUSTENÍ VYKUROVACEJ SÚSTAVY MÉDIOM JE NEVYHNUTNÉ ZABEZPEČIŤ JEJ POSTUPNÉ ODVZDUŠNENIE.
- ZHOTOVITEĽ JE POVINNÝ POSTUPOVAŤ V SÚLADE S PLATNÝMI NORMAMI STN EN A DODRŽIAVAŤ TECHNOLOGICKÉ AJ BEZPEČNOSTNÉ PREDPISY. ZÁROVEŇ MUSÍ REŠPEKTOVAŤ USTANOVENIA STN 730421 O ROZMEROVÝCH ODCHÝLKACH. KAŽDÚ ZMENU OPROTI PROJEKTU JE NUTNÉ VOPRED SKONZULTOVAŤ S HIP.
- OTVORY PRE PRESTUPY INŽINIERSKYCH SIETÍ A POTRUBNÝCH ROZVODOV V OBJEKTE JE POTREBNÉ PRIPRAVIŤ POČAS REALIZÁCIE HRUBEJ STAVBY.
- TÁTO DOKUMENTÁCIA NENAHRÁDZA REALIZAČNÚ DOKUMENTÁCIU STAVBY!
-VÝŠKOVÁ ÚROVEŇ ±0,000 V PROJEKTE ZODPOVEDÁ ÚROVNI FINÁLNEJ NÁŠĽAPNEJ VRSTVY PODLAHY.

PROJEKTANT TZB:

TZB Smart Engineering s. r. o.
Karpatské námestie 7770/10A
831 06 Bratislava

VYPRACOVAL:
ING. VIKTOR Labovský

ZODPOVEDNÝ PROJEKTANT
ING. JÁN BÁTOR

±0,000 = 170,90 m n.m. - ÚROVEŇ 1. NP

PROJEKTANT: