R-Z ZOSTAVA ROZDEĽOVAČA PODLAHOVÉHO VYKUROVANIA (TEPLOTNÝ SPÁD 45/35 °C)

10-OKRUHOVÝ ROZDEĽOVAČ NAPR. REHAU HKVD SX-AG 10, SKRINKA (ROZMER 577 X 510 X 80 MM).
ĎIAĽKOVÉ OVLÁDANIE TERMOSTATOV NAPR. REHAU NEA (230V)

4 KS PRIESTROVÝ TERMOSTAT NAPR. REHAU NEA (230V)

10 KS ELEKTRICKÝ SERVO-POHON (230V)

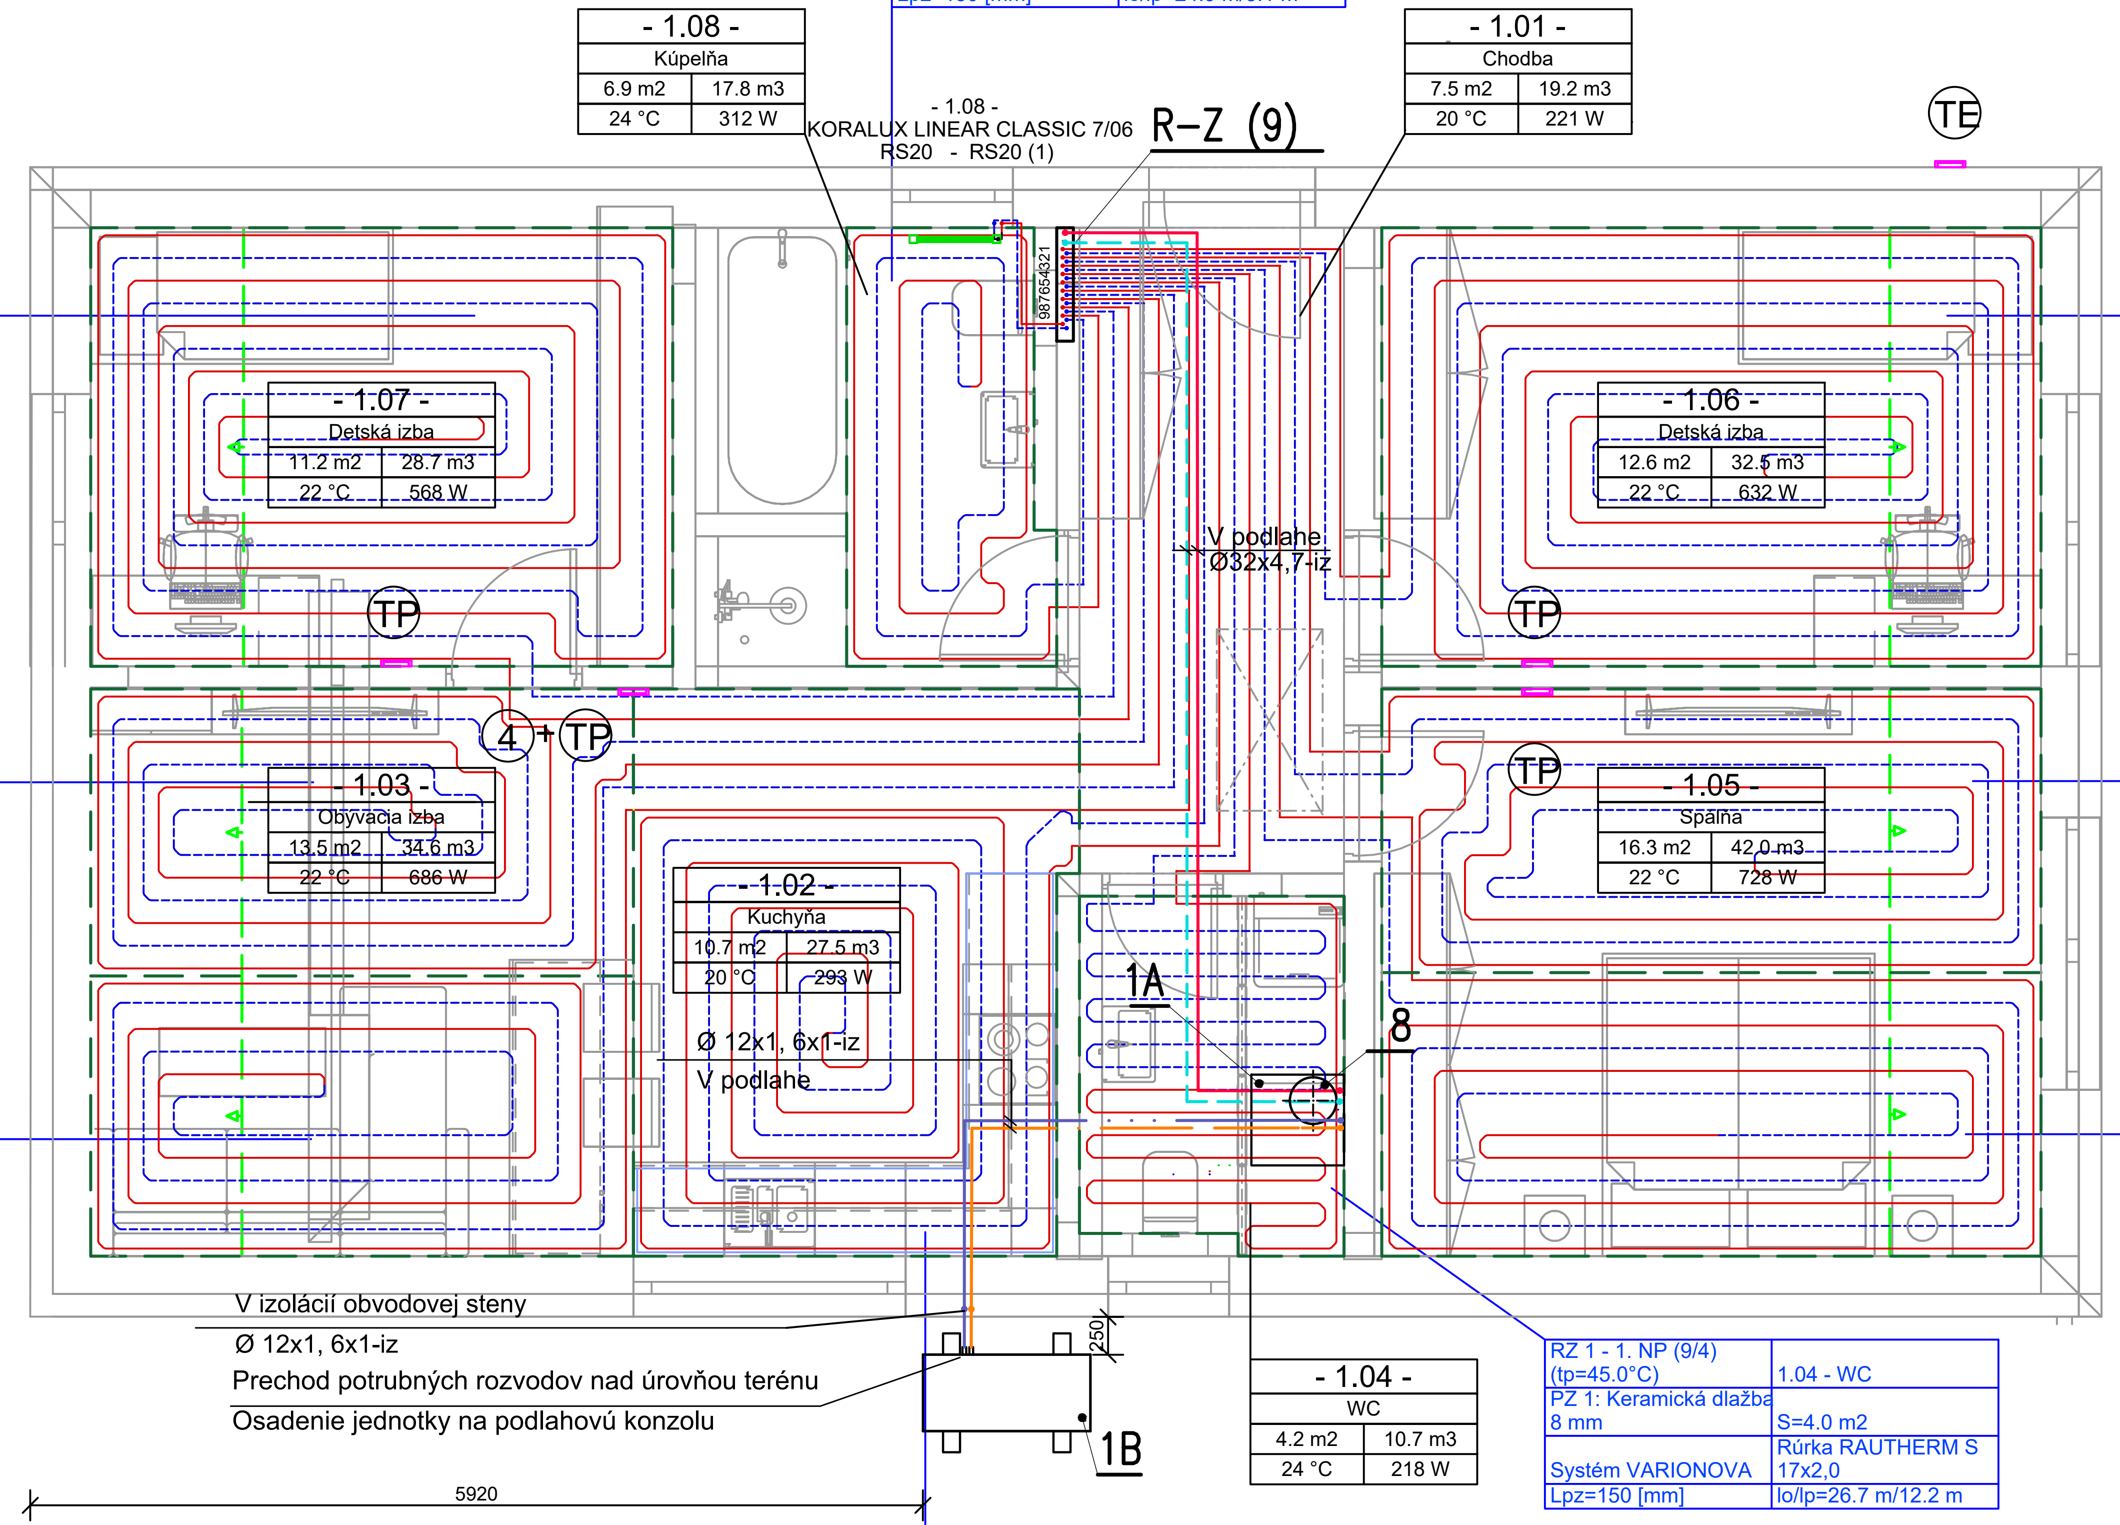
RZ 1 - 1. NP (9/9) (tp=45.0°C) | 1.08 - Kúpeľňa | PZ 1: Keramická dlažba 8 mm | S=3.7 m2 | Systém VARIONOVA | Rúrka RAUTHERM S 17x2,0 | Lpz=150 [mm] | lo/lp=24.9 m/5.1 m
- 1.08 - Kúpeľňa 6.9 m2 17.8 m3 24 °C 312 W
- 1.08 - KORALUX LINEAR CLASSIC 7/06 RS20 - RS20 (1)
R-Z (9)
- 1.01 - Chodba 7.5 m2 19.2 m3 20 °C 221 W
TE
RZ 1 - 1. NP (9/8) (tp=45.0°C) | 1.07 - Detská izba | PZ 1: Laminátová podlaha 10 mm | S=11.2 m2 | Systém VARIONOVA | Rúrka RAUTHERM S 17x2,0 | Lpz/Loz=150/100 [mm] | lo/lp=84.2 m/15.1 m
- 1.07 - Detská izba 11.2 m2 28.7 m3 22 °C 568 W
RZ 1 - 1. NP (9/1) (tp=45.0°C) | 1.06 - Detská izba | PZ 1: Laminátová podlaha 10 mm | S=12.6 m2 | Systém VARIONOVA | Rúrka RAUTHERM S 17x2,0 | Lpz/Loz=150/100 [mm] | lo/lp=94.0 m/9.3 m
- 1.06 - Detská izba 12.6 m2 32.5 m3 22 °C 632 W
987654321
V podlahe Ø32x4,7-iz
TP
RZ 1 - 1. NP (9/7) (tp=45.0°C) | 1.03 - Obývacia izba | PZ 1: Laminátová podlaha 10 mm | S=6.4 m2 | Systém VARIONOVA | Rúrka RAUTHERM S 17x2,0 | Lpz/Loz=150/100 [mm] | lo/lp=49.0 m/14.6 m
4 + TP
- 1.03 - Obývacia izba 13.5 m2 34.6 m3 22 °C 686 W
RZ 1 - 1. NP (9/2) (tp=45.0°C) | 1.05 - Spálňa | PZ 1: Laminátová podlaha 10 mm | S=8.0 m2 | Systém VARIONOVA | Rúrka RAUTHERM S 17x2,0 | Lpz/Loz=150/100 [mm] | lo/lp=59.4 m/11.5 m
TP
- 1.05 - Spálňa 16.3 m2 42.0 m3 22 °C 728 W
- 1.02 - Kuchyňa 10.7 m2 27.5 m3 20 °C 293 W
Ø 12x1, 6x1-iz
V podlahe
1A
8
RZ 1 - 1. NP (9/6) (tp=45.0°C) | 1.03 - Obývacia izba | PZ 1: Laminátová podlaha 10 mm | S=6.6 m2 | Systém VARIONOVA | Rúrka RAUTHERM S 17x2,0 | Lpz/Loz=150/100 [mm] | lo/lp=50.5 m/18.7 m
RZ 1 - 1. NP (9/3) (tp=45.0°C) | 1.05 - Spálňa | PZ 1: Laminátová podlaha 10 mm | S=8.2 m2 | Systém VARIONOVA | Rúrka RAUTHERM S 17x2,0 | Lpz/Loz=150/100 [mm] | lo/lp=60.7 m/14.4 m
V izolácií obvodovej steny
Ø 12x1, 6x1-iz
Prechod potrubných rozvodov nad úrovňou terénu
Osadenie jednotky na podlahovú konzolu
250
1B
5920
- 1.04 - WC 4.2 m2 10.7 m3 24 °C 218 W
RZ 1 - 1. NP (9/4) (tp=45.0°C) | 1.04 - WC | PZ 1: Keramická dlažba 8 mm | S=4.0 m2 | Systém VARIONOVA | Rúrka RAUTHERM S 17x2,0 | Lpz=150 [mm] | lo/lp=26.7 m/12.2 m
RZ 1 - 1. NP (9/5) (tp=45.0°C) | 1.02 - Kuchyňa | PZ 1: Laminátová podlaha 10 mm | S=8.3 m2 | Systém VARIONOVA | Rúrka RAUTHERM S 17x2,0 | Lpz=150 [mm] | lo/lp=55.5 m/11.6 m

⬚

Podlahové vykurovanie Rehau

Vykurovacia plocha: S=4.2 m²

Typ nášľapnej vrstvy (PX): Keramická dlažba

Typ vykurovacej rúrky: Rúrka Rautherm S 17×2,0

Rozdeľovač: Rozdeľovač Rehau , skrinka rozdeľovača . 1. NP, napojenie 9 okruhov (tp=45 °C)

Systém uchytenia: Varionova – typ prichytenia potrubia pre podlahové kúrenie

TABUĽKA MIESTNOSTÍ 1.NP

Č. MIESTNOSTI	NÁZOV MIESTNOSTI	PLOCHA (m2)
1.01	Chodba	7,66
1.02	Kuchyňa	14,34
1.03	Obývacia izba	13,78
1.04	WC	4,28
1.05	Spálňa	19,18
1.06	Detská izba	15,22
1.07	Detská izba	11,70
1.08	WC	7,27
		93,43 m²

DETAIL NAPOJENIA VYKUROVACÍCH TELIES

REBRÍKOVÉ VYKUROVACIE TELESO

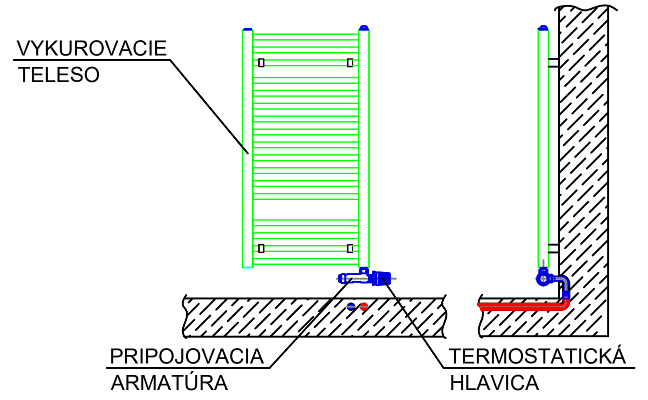
VYKUROVACIE TELESO
PRIPOJOVACIA ARMATÚRA
TERMOSTATICKÁ HLAVICA

POZNÁMKY :

- V PRÍPADE AKÝCHKOĽVEK NEJASNOSTÍ V PROJEKTOVEJ DOKUMENTÁCII JE NUTNÉ KONTAKTOVAŤ ZODPOVEDNÉHO PROJEKTANTA.
- VŠETKY STAVEBNÉ ROZMERY A PRESTUPY JE POTREBNÉ OVERIŤ PRIAMO NA MIESTE REALIZÁCIE.
- PRED SAMOTNÝM SPUSTENÍM SYSTÉMU DO PREVÁDZKY SA MUSÍ VYKONAŤ DÔKLADNÝ PREPLACH ROZVODOV A VYČISTENIE VŠETKÝCH INŠTALOVANÝCH FILTROV.
- PO NAPUSTENÍ VYKUROVACEJ SÚSTAVY MÉDIOM JE NEVYHNUTNÉ ZABEZPEČIŤ JEJ POSTUPNÉ ODVZDUŠNENIE.
- ZHOTOVITEĽ JE POVINNÝ POSTUPOVAŤ V SÚLADE S PLATNÝMI NORMAMI STN EN A DODRŽIAVAŤ TECHNOLOGICKÉ AJ BEZPEČNOSTNÉ PREDPISY. ZÁROVEŇ MUSÍ REŠPEKTOVAŤ USTANOVENIA STN 730421 O ROZMEROVÝCH ODCHÝLKACH. KAŽDÚ ZMENU OPROTI PROJEKTU JE NUTNÉ VOPRED SKONZULTOVAŤ S HIP.
- OTVORY PRE PRESTUPY INŽINIERSKYCH SIETÍ A POTRUBNÝCH ROZVODOV V OBJEKTE JE POTREBNÉ PRIPRAVIŤ POČAS REALIZÁCIE HRUBEJ STAVBY.
- TÁTO DOKUMENTÁCIA NENAHRÁDZA REALIZAČNÚ DOKUMENTÁCIU STAVBY!
-VÝŠKOVÁ ÚROVEŇ ±0,000 V PROJEKTE ZODPOVEDÁ ÚROVNI FINÁLNEJ NÁŠĽAPNEJ VRSTVY PODLAHY.

LEGENDA POTRUBÍ:

🟥 – – –	PLASTHLINÍKOVÉ POTRUBIE NAPR. RAUTHERM S 17×2,0 REHAU, TEPLOTNÝ SPÁD 45/35 °C, VEDENÉ V PODLAHE.
🟥 – – –	PLASTHLINÍKOVÉ POTRUBIE MATERIÁL: PE-XA/AL/PE NAPR. RAUTITAN STABIL, ZAIZOLOVANÉ POTRUBIE, TEPLOTNÝ SPÁD 45/35 °C.
—·· —	MEDENÉ POTRUBIE PRIMÁRNEHO OKRUHU TEPELNÉHO ČERPADLA: CU Φ12×1, 6×1-IZ.

LEGENDA ZARIADENÍ:

1A	TEPELNÉ ČERPADLO (VNÚTORNÁ JEDNOTKA) NAPR.: VIESSMANN VITOCAL 222-S. INTEGROVANÝ ZÁSOBNÍK NA TV (190 L), NAPÁJANIE 230V/50HZ.
1B	TEPELNÉ ČERPADLO (VONKAJŠIA JEDNOTKA) NAPR.: VITOCAL 222-S. VÝKON (A7/W35): 2,6 – 7,5 KW.
4	OVLÁDANIE: BEZDRÔTOVÝ DIAĽOVÝ OVLÁDAČ NAPR. VITOTROL 300-E.
8	EXPANZNÁ NÁDOBA NAPR: VIESSMANN N25 (OBJEM 25 L, MAX. TLAK 3 BAR).
TP	IZBOVÝ REGULÁTOR NAPR.: REHAU NEA SMART 2.0 (MERANIE TEPLOTY).
TE	SNÍMAČ TEPLOTY EXTERIÉRU.
🟩	REBRÍKOVÉ VYKUROVACIE TELESO KORALUX LINEAR CLASSIC DOPLNENÉ O EL. VYKUROVACIU VLOŽKU 230V

TABUĽKA REVÍZIÍ

ČÍSLO REVÍZIE	DÁTUM	POPIS ZMENY	VYPRACOVAL

0,000=223,560 m n. m.

AUTOR PROJEKTU:	Ing. arch. Ivor Mečiar, Matúš Sorokáč	GENERÁLNY PROJEKTANT: Alla s.r.o. Riazanská 70/683 831 02 Bratislava tel.: +421 907 693 679 email: ateliar@alla.sk
H.I.P.:	Ing. arch. Ivor Mečiar, ArtD.	
ZODP. PROJEKTANT:	Ing. Ján Bátor	
VYPRACOVAL:	Ing. Viktor Labovský	

INVESTOR:	Sy
NÁZOV PROJEKTU:	I
MIESTO STAVBY:	K
OBSAH VÝKRESU:	F
STAVEBNÝ OBJEKT:	S
ID STAVBY: ---	STUPEŇ PD: PSP
NÁZOV VÝKRESU V ELEKTRONICKEJ F	