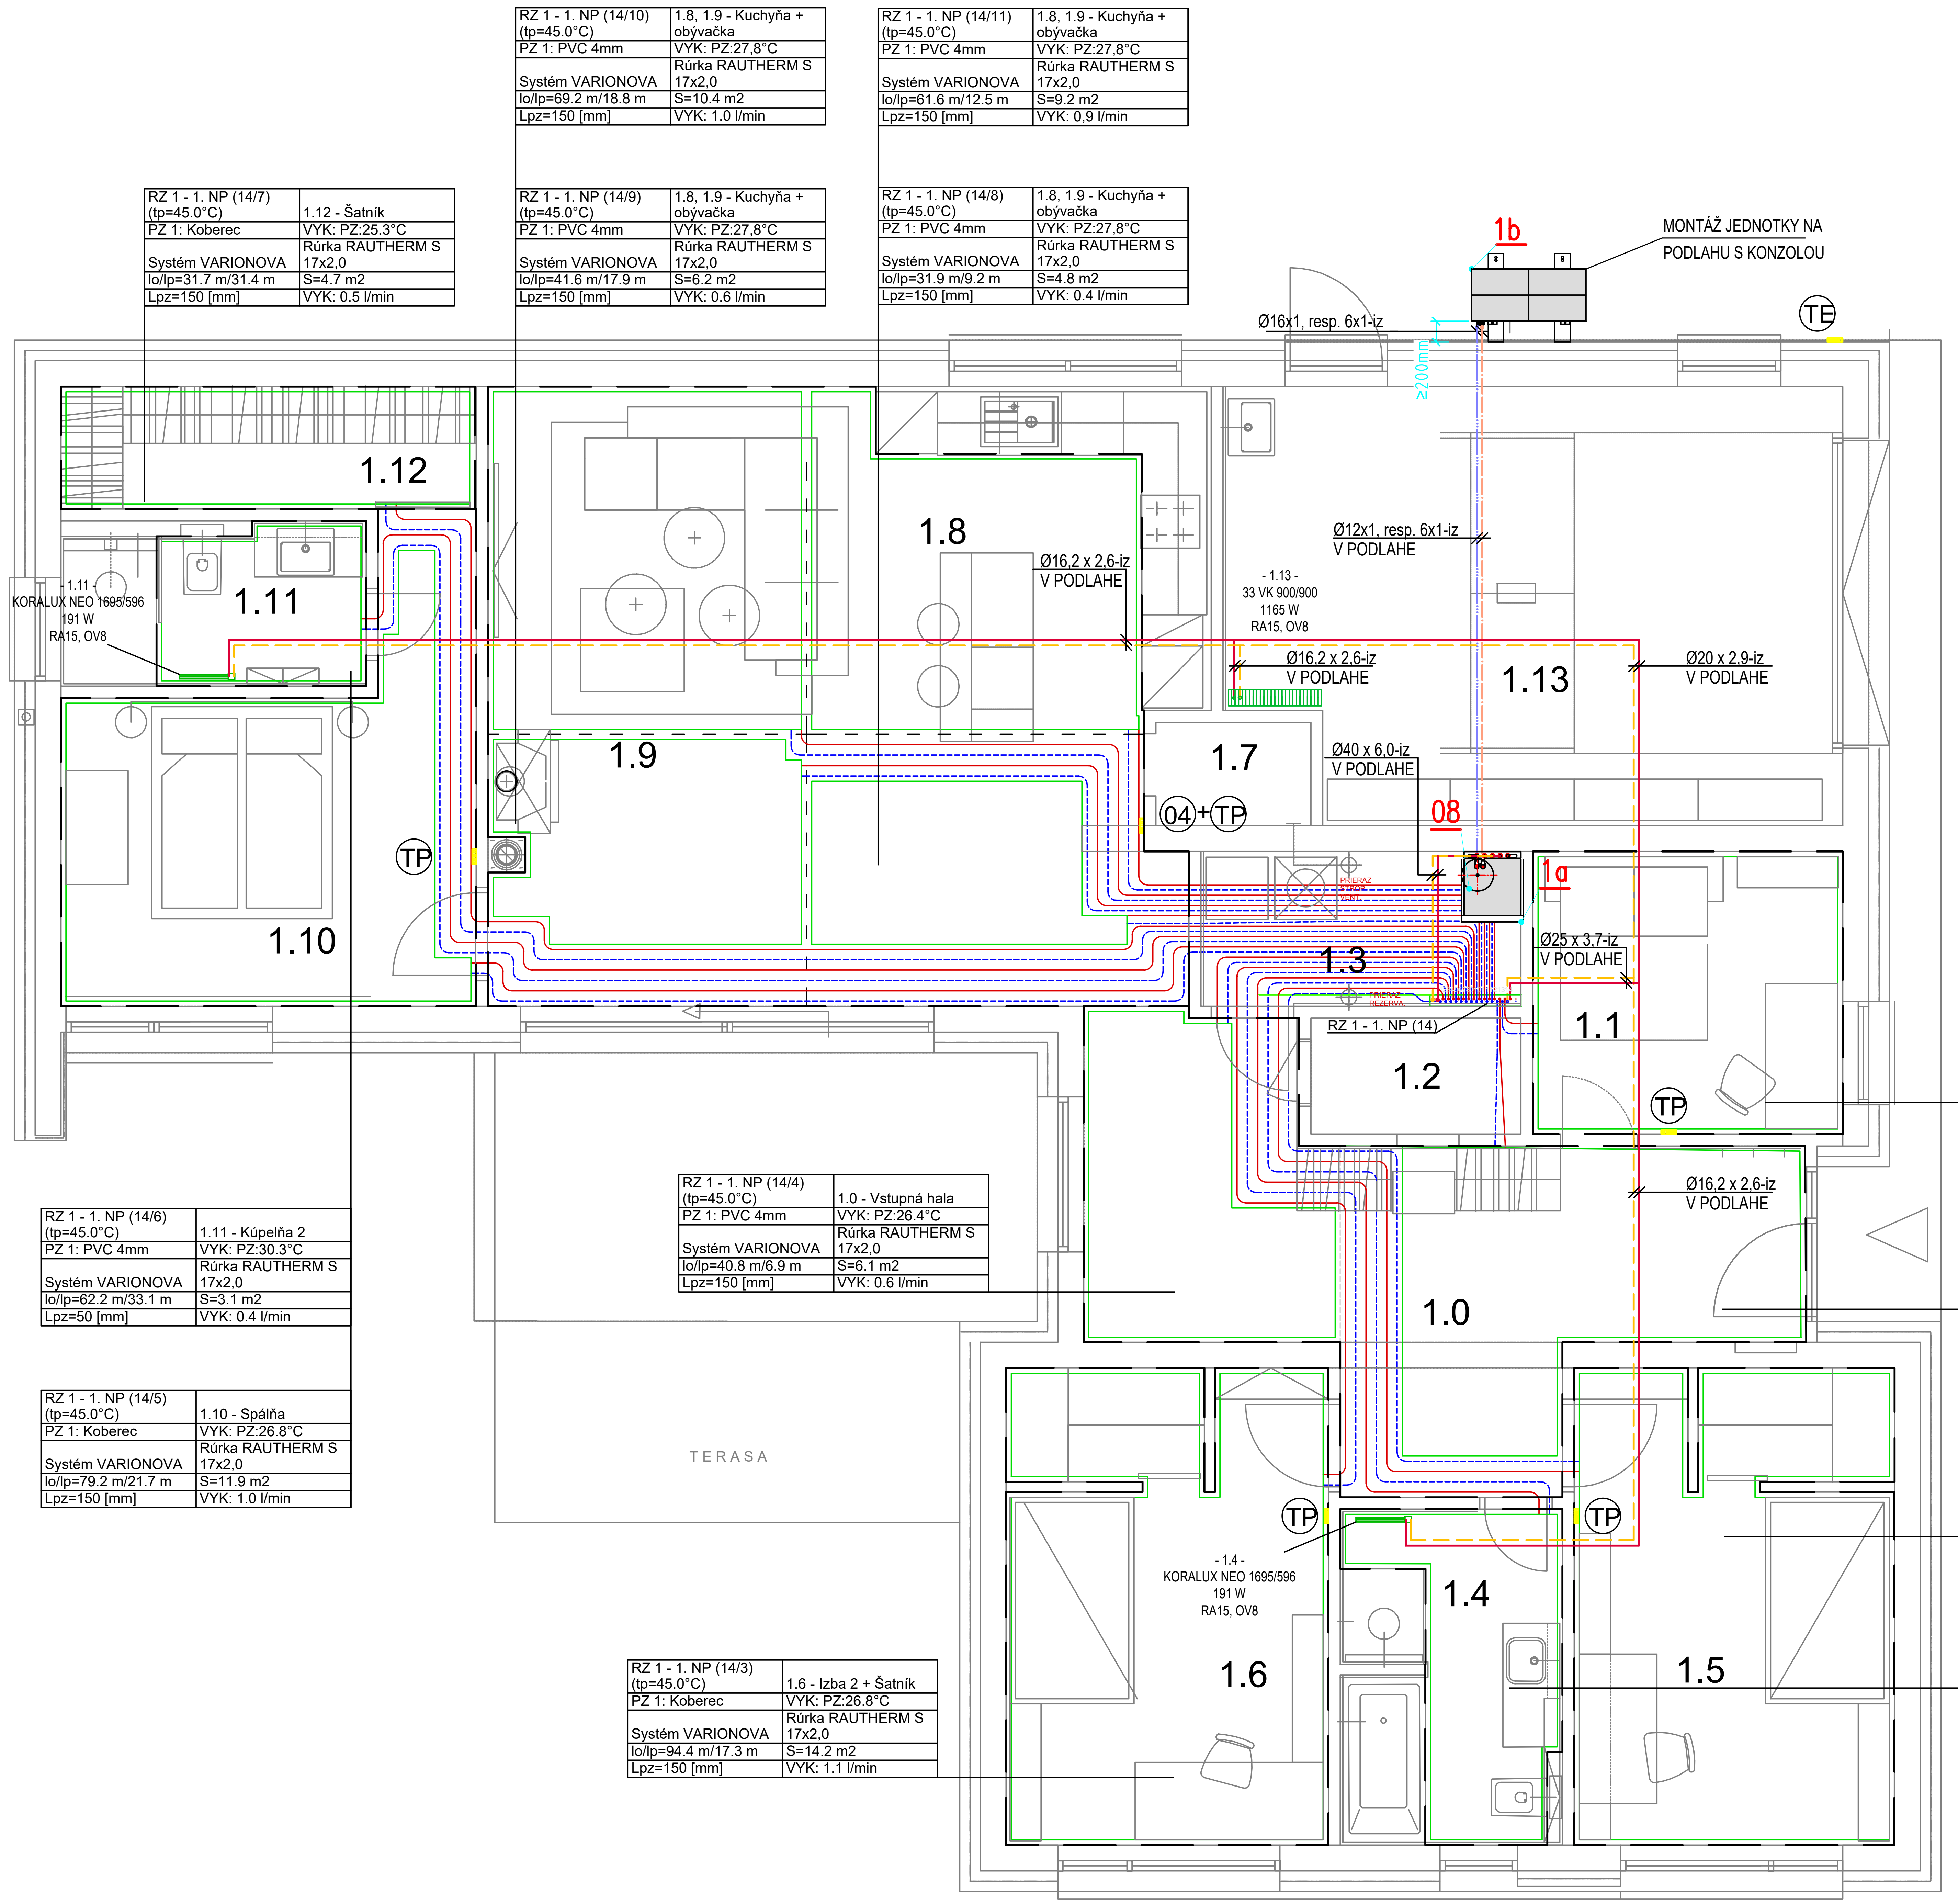

RZ 1 - 1. NP (14/7) (tp=45.0°C)	1.12 - Šatník
PZ 1: Koberec	VYK: PZ:25.3°C
Systém VARIONOVA	Rúrka RAUTHERM S 17x2,0
lo/lp=31.7 m/31.4 m	S=4.7 m2
Lpz=150 [mm]	VYK: 0.5 l/min

RZ 1 - 1. NP (14/10) (tp=45.0°C)	1.8, 1.9 - Kuchyňa + obývačka
PZ 1: PVC 4mm	VYK: PZ:27,8°C
Systém VARIONOVA	Rúrka RAUTHERM S 17x2,0
lo/lp=69.2 m/18.8 m	S=10.4 m2
Lpz=150 [mm]	VYK: 1.0 l/min

RZ 1 - 1. NP (14/9) (tp=45.0°C)	1.8, 1.9 - Kuchyňa + obývačka
PZ 1: PVC 4mm	VYK: PZ:27,8°C
Systém VARIONOVA	Rúrka RAUTHERM S 17x2,0
lo/lp=41.6 m/17.9 m	S=6.2 m2
Lpz=150 [mm]	VYK: 0.6 l/min

RZ 1 - 1. NP (14/11) (tp=45.0°C)	1.8, 1.9 - Kuchyňa + obývačka
PZ 1: PVC 4mm	VYK: PZ:27,8°C
Systém VARIONOVA	Rúrka RAUTHERM S 17x2,0
lo/lp=61.6 m/12.5 m	S=9.2 m2
Lpz=150 [mm]	VYK: 0,9 l/min

RZ 1 - 1. NP (14/8) (tp=45.0°C)	1.8, 1.9 - Kuchyňa + obývačka
PZ 1: PVC 4mm	VYK: PZ:27,8°C
Systém VARIONOVA	Rúrka RAUTHERM S 17x2,0
lo/lp=31.9 m/9.2 m	S=4.8 m2
Lpz=150 [mm]	VYK: 0.4 l/min

RZ 1 - 1. NP (14/6) (tp=45.0°C)	1.11 - Kúpelňa 2
PZ 1: PVC 4mm	VYK: PZ:30.3°C
Systém VARIONOVA	Rúrka RAUTHERM S 17x2,0
lo/lp=62.2 m/33.1 m	S=3.1 m2
Lpz=50 [mm]	VYK: 0.4 l/min

RZ 1 - 1. NP (14/5) (tp=45.0°C)	1.10 - Spálňa
PZ 1: Koberec	VYK: PZ:26.8°C
Systém VARIONOVA	Rúrka RAUTHERM S 17x2,0
lo/lp=79.2 m/21.7 m	S=11.9 m2
Lpz=150 [mm]	VYK: 1.0 l/min

RZ 1 - 1. NP (14/4) (tp=45.0°C)	1.0 - Vstupná hala
PZ 1: PVC 4mm	VYK: PZ:26.4°C
Systém VARIONOVA	Rúrka RAUTHERM S 17x2,0
lo/lp=40.8 m/6.9 m	S=6.1 m2
Lpz=150 [mm]	VYK: 0.6 l/min

RZ 1 - 1. NP (14/3) (tp=45.0°C)	1.6 - Izba 2 + Šatník
PZ 1: Koberec	VYK: PZ:26.8°C
Systém VARIONOVA	Rúrka RAUTHERM S 17x2,0
lo/lp=94.4 m/17.3 m	S=14.2 m2
Lpz=150 [mm]	VYK: 1.1 l/min

RZ 1 - 1. NP (14/12) (tp=45.0°C)	1.0 - Vstupná hala
PZ 1: PVC 4mm	VYK: PZ:27.8°C
Systém VARIONOVA	Rúrka RAUTHERM S 17x2,0
lo/lp=62.5 m/3.3 m	S=9.4 m2
Lpz=150 [mm]	VYK: 0.8 l/min

RZ 1 - 1. NP (14/12) (tp=45.0°C)	1.0 - Vstupná hala
PZ 1: PVC 4mm	VYK: PZ:26.4°C
Systém VARIONOVA	Rúrka RAUTHERM S 17x2,0
lo/lp=62.5 m/3.3 m	S=9.4 m2
Lpz=150 [mm]	VYK: 1.0 l/min

RZ 1 - 1. NP (14/1) (tp=45.0°C)	1.5 - Izba 1 + Šatník
PZ 1: Koberec	VYK: PZ:26.8°C
Systém VARIONOVA	Rúrka RAUTHERM S 17x2,0
lo/lp=93.7 m/18.3 m	S=14.1 m2
Lpz=150 [mm]	VYK: 1.1 l/min

RZ 1 - 1. NP (14/2) (tp=45.0°C)	1.4 - Kúpeľna
PZ 1: PVC 4mm	VYK: PZ:30,3°C
Systém VARIONOVA	Rúrka RAUTHERM S 17x2,0
lo/lp=93.1 m/19.7 m	S=4.7 m2
Lpz=50 [mm]	VYK: 0.5 l/min

LEGENDA MIESTNOSTÍ:

ozn	NÁZOV MIESTNOSTI	plocha m²
1.0	VSTUP HALA	19,20
1.1	PRACOVŇA	8,20
1.2	SKLAD	2,28
1.3	TECHNIKA	4,64
1.4	KÚPELŇA	7,00
1.5	IZBA + ŠATNÍK	14,31
1.6	IZBA + ŠATNÍK	14,40
1.7	KOMORA	1,50
1.8	KUCHYŇA	11,20
1.9	OBÝVACIA IZBA	29,60
1.10	SPÁLŇA	13,74
1.11	KÚPELŇA	4,72
1.12	ŠATNÍK	4,76
1.13	GARÁŽ	24,42
1.14	KRYTÁ TERASA	22,42
	CELKOVÁ ÚŽITKOVÁ PLOCHA PODLAŽIA /BEZ TERASY, VR. GARÁžE/ 159.97 m2	

DETAIL ZAPOJENIA VYKUROVACIEHO TELIESA:

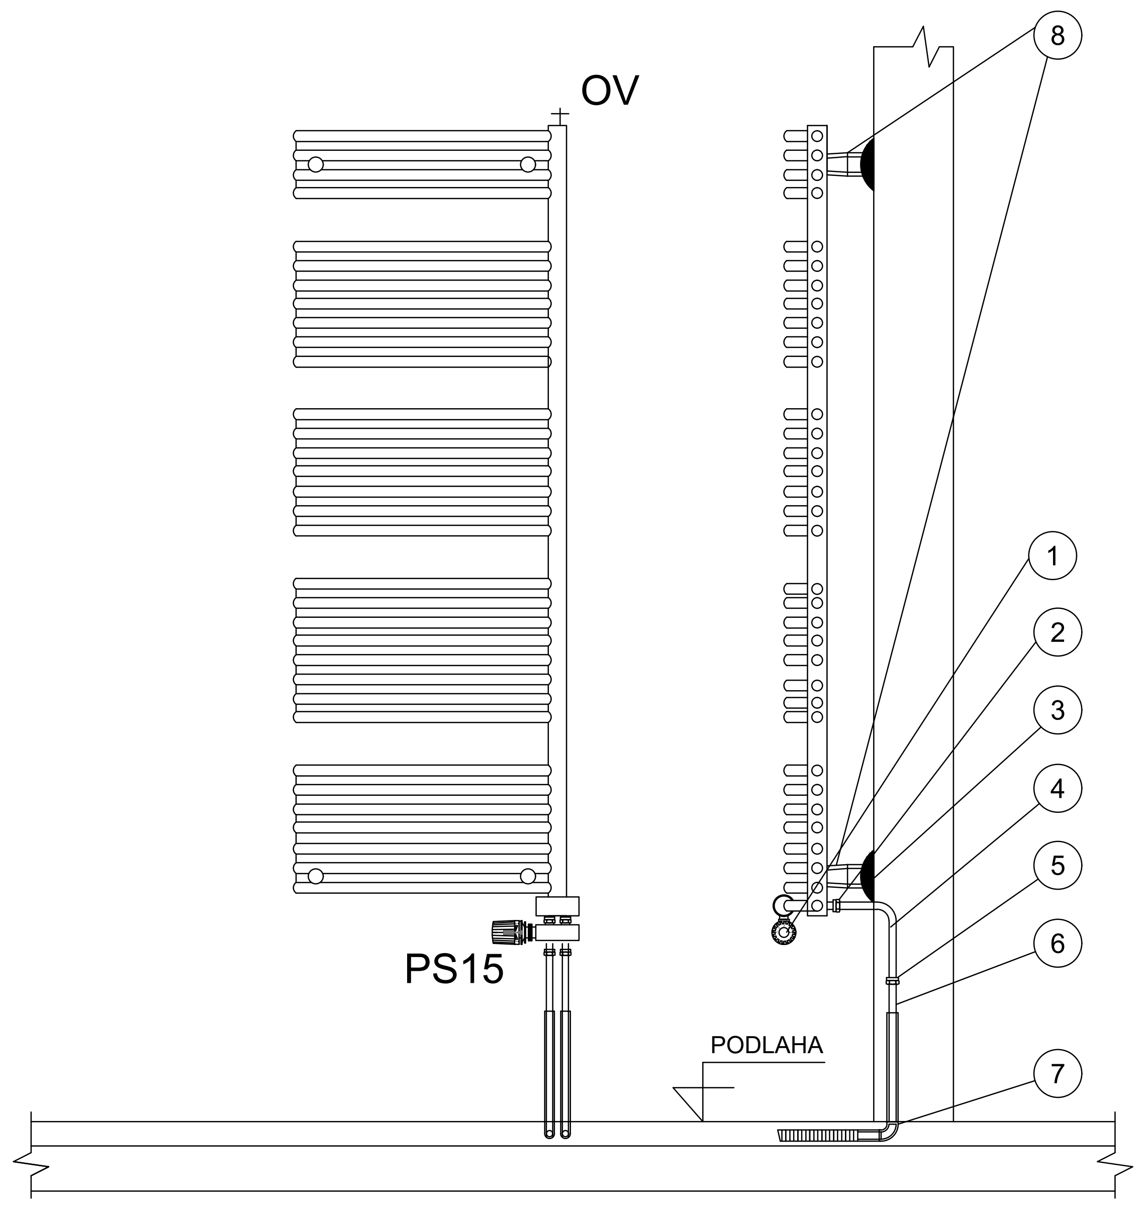

1	Pripojenie vykurovacieho telesa, rozteč H=50mm	5	Násuvná objímka
2	Svorková spojka	6	Vykurovacia rúrka
3	Krycia rozeta	7	Vodiaci oblúk 90°
4	Pripojovacia garnitúra s upevňovacím	8	Stenová konzola

LEGENDA PODLAHOVÉHO VYKUROVANIA:

🟩 PODLAHOVÉ KÚRENIE REHAU

Lpz=100 [mm]	ROZOSTUP VYK. RÚROK
S=8,6 m2	VYKUROVACIA PLOCHA
PZ: Keramická dlažba	TYP NÁŠLAPNEJ VRSTVY
Rúrka RAUTHERM S 17x2,0	TYP VYKUROVACEJ RÚRKY
Nast.=0,63 (48 kg/h)	NASTAVENIE REG. OKRUHU(PRIETOK)
lo/lp=12.7 m/1.6 m	Dlžka okruhu / dlžka prípojky
RZ 1. NP-1/9 (tp=45°C)	rozdelovač na 1 .NP 1. napojenie a
VARIONOVA	9 vetiev (tp - teplota prívodu)
PZ:21°C	typ prichytenia potrubi pre podlahove kurenie
	maximálna povrchová teplota podlahovej zóny

- 1.0 -		- 1.1 -		- 1.4 -		- 1.5 -		- 1.6 -	
Vstupná hala		Pracovňa		Kúpeľna		Izba 1 + Šatník		Izba 2 + Šatník	
19.2 m2	48.6 m3	8.2 m2	20.8 m3	7.0 m2	17.7 m3	14.3 m2	36.1 m3	14.3 m2	36.2 m3
22 °C	633 W	22 °C	370 W	24 °C	357 W	22 °C	575 W	22 °C	578 W

- 1.8, 1.9 -		- 1.10 -		- 1.11 -		- 1.12 -		- 1.13 -	
Kuchyňa + obývačka		Spálňa		Kúpelňa 2		Šatník		Garáž	
40.8 m2	103.1 m3	13.7 m2	34.6 m3	4.7 m2	11.8 m3	4.8 m2	12.0 m3	24.4 m2	61.6 m3
22 °C	1552 W	22 °C	575 W	24 °C	251 W	22 °C	152 W	15 °C	810 W

LEGENDA VYKUROVACÍCH TELIES:

▨ OCEĽOVÉ DOSKOVÉ VYKUROVACIE TELESO KLASIK

SPÔSOB ZNAČENIA TYP KLASIK, S BOČNÝM PRIPOJENÍM

33 VK 900/900
- 900 (druhé) – STAVEBNÁ DĹŽKA V MILIMETROCH
- 900 (prvé) – STAVEBNÁ VÝŠKA V MILIMETROCH
- VK – PREVEDENIE VENTIL KOMPAKT - SO SPODNÝM PRIPOJENÍM
- 33 – TYP DVOJRADOVÝ

🟩 REBRÍKOVÉ VYKUROVACIE TELESO
TYP KORALUX NEO, FY. KORADO

LEGENDA POTRUBIA:

🟥 POTRUBIE - PLASTHLINNÍKOVÁ RURKA PE-Xa/AL/PE napr. RAUTITAN Stabil REHAU
SPÁJANÉ LISOVANÍM, IZOLOVANÉ POTRUBIE, TEPLOTNÝ SPÁD 45/35°C. PRE PODLAHOVÉ VYKUROVANIE

🟥 POTRUBIE - PLASTHLINNÍKOVÁ RURKA PE-Xa/AL/PE napr. RAUTITAN Stabil REHAU
SPÁJANÉ LISOVANÍM, IZOLOVANÉ POTRUBIE, TEPLOTNÝ SPÁD 45/35°C.

ROZVOD ÚK PRE PRIMÁRNY OKRUH TEPELNÉHO ČERPADLA
PRE OKRUHY KONVEKČNÉHO VYKUROVANIA, PRÍVOD A SPATOČKA
MATERIÁL MEĎ

LEGENDA ZARIADENÍ A ARMATÚR :

1a	KOMPAKTNÁ VNÚTORNÁ JEDNOTKA TEPELNÉHO ČERPADLA VITOCAL 222-S AWBT-M-E 221.E06
1b	VONKAJ.JEDNOTKA VITOCAL 222-S AWBT-M-E 221.E06 (230V) MAX.VÝSTUPNÁ TEPLOTA 60°C,TEPELNY VYKON 2,6-7,5kW A7/W35 EKOLOGICKE CHLADIVO R32, REGULÁCIA ONE-BASE,WIFI (Z022722)
04	BEZDRÔDOTVÉ DIAĽKOVÉ OVLÁDANIE VITOTROL 300-E
08	UZAVRETÁ TLAKOVÁ EXPANZNÁ NÁDOBA VIESSMANN N25 OBJEM 25L, 3bar ROZMERY : Ø=308 mm, VÝŠKA 477 mm , HMOTNOSŤ 4,3 kg + NASTENNY DRZIAK PRE N25 (9572216)
TP	PRIESTOROVÝ REGULÁTOR NEA SMART 2.0 PRE MERANIE TEPLOTY V MIESTNOSTI, FY. REHAU
TE	SNÍMAČ VONKAJŠEJ TEPLOTY
RA	RADIATOROVÝ VENTIL NAPR. VERAFIX-VKE, UZATVÁRACIE ŠRÓBENIE H-BLOK S VONKAJŠÍM ZÁVITOM EUROKONUS PRE VYKUROVACIE TELESÁ TYPU VENTIL-KOMPAKT, ROHOVÝ, DN15 PRIPOJENIE RADIÁTORA VONKAJŠÍ ZÁVIT 1/2", PRIPOJENIE RÚRKY VONKAJŠÍ ZÁVIT 3/4" TERMOSTATICKÁ HLAVICA SO VSTAVANÝM KVAPALINOVÝM SNÍMAČOM, ROZSAH 6-28°C
OV	ODVZDUŠŇOVACÍ VENTIL , PN 16/120°C

POZNÁMKA :

- V PRÍPADE NEJASNOSTÍ VO VÝKRESOVEJ DOKUMENTÁCIÍ KONTAKTOVAŤ ZODPOVEDNÉHO PROJEKTANTA
- VŠETKY ROZMERY STAVEBNÝCH PRÁC KONTROLOVAŤ NA MIESTE STAVBY
- PRED UVEDENÍM SYSTÉMU DO PREVÁDZKY JE POTREBNÉ VYKONAŤ DÔKLADNÝ PREPLACH SYSTÉMU S VYČISTENÍM VŠETKÝCH FILTROV NA ROZVODE
- PO NAPUSTENÍ SYSTÉMU JE POTREBNÉ VYKONAŤ JEHO ODVZDUŠNENIE
- DODÁVATEL STAVBY JE POVINNÝ REALIZOVAŤ VŠETKY PRÁCE V ZMYSLE PLATNÝCH STN EN S DODRŽANÍM TECHNOLOGICKÝCH A BEZPEČNOSTNÝCH POSTUPOV. ĎALEJ JE POVINNÝ REŠPEKTOVAŤ USTANOVENIÁ STN 730421 O PRÍSLUŠNÝCH ROZMEROVÝCH ODCHÝLKACH REALIZOVANÝCH KONŠTRUKCIÍ PROTI PROJEKTOVANÉMU STAVU. KAŽDÚ ODCHÝLKU OD PROJEKTU JE POTREBNÉ PREROKOVAŤ S GP.

Doršic Doršicová
Architektonická Kancelária

OPRÁVNEN
VYPRACOV
INVESTOR:
NÁZOV ST
MIESTO:
PROFESIA:
NÁZOV VÝ