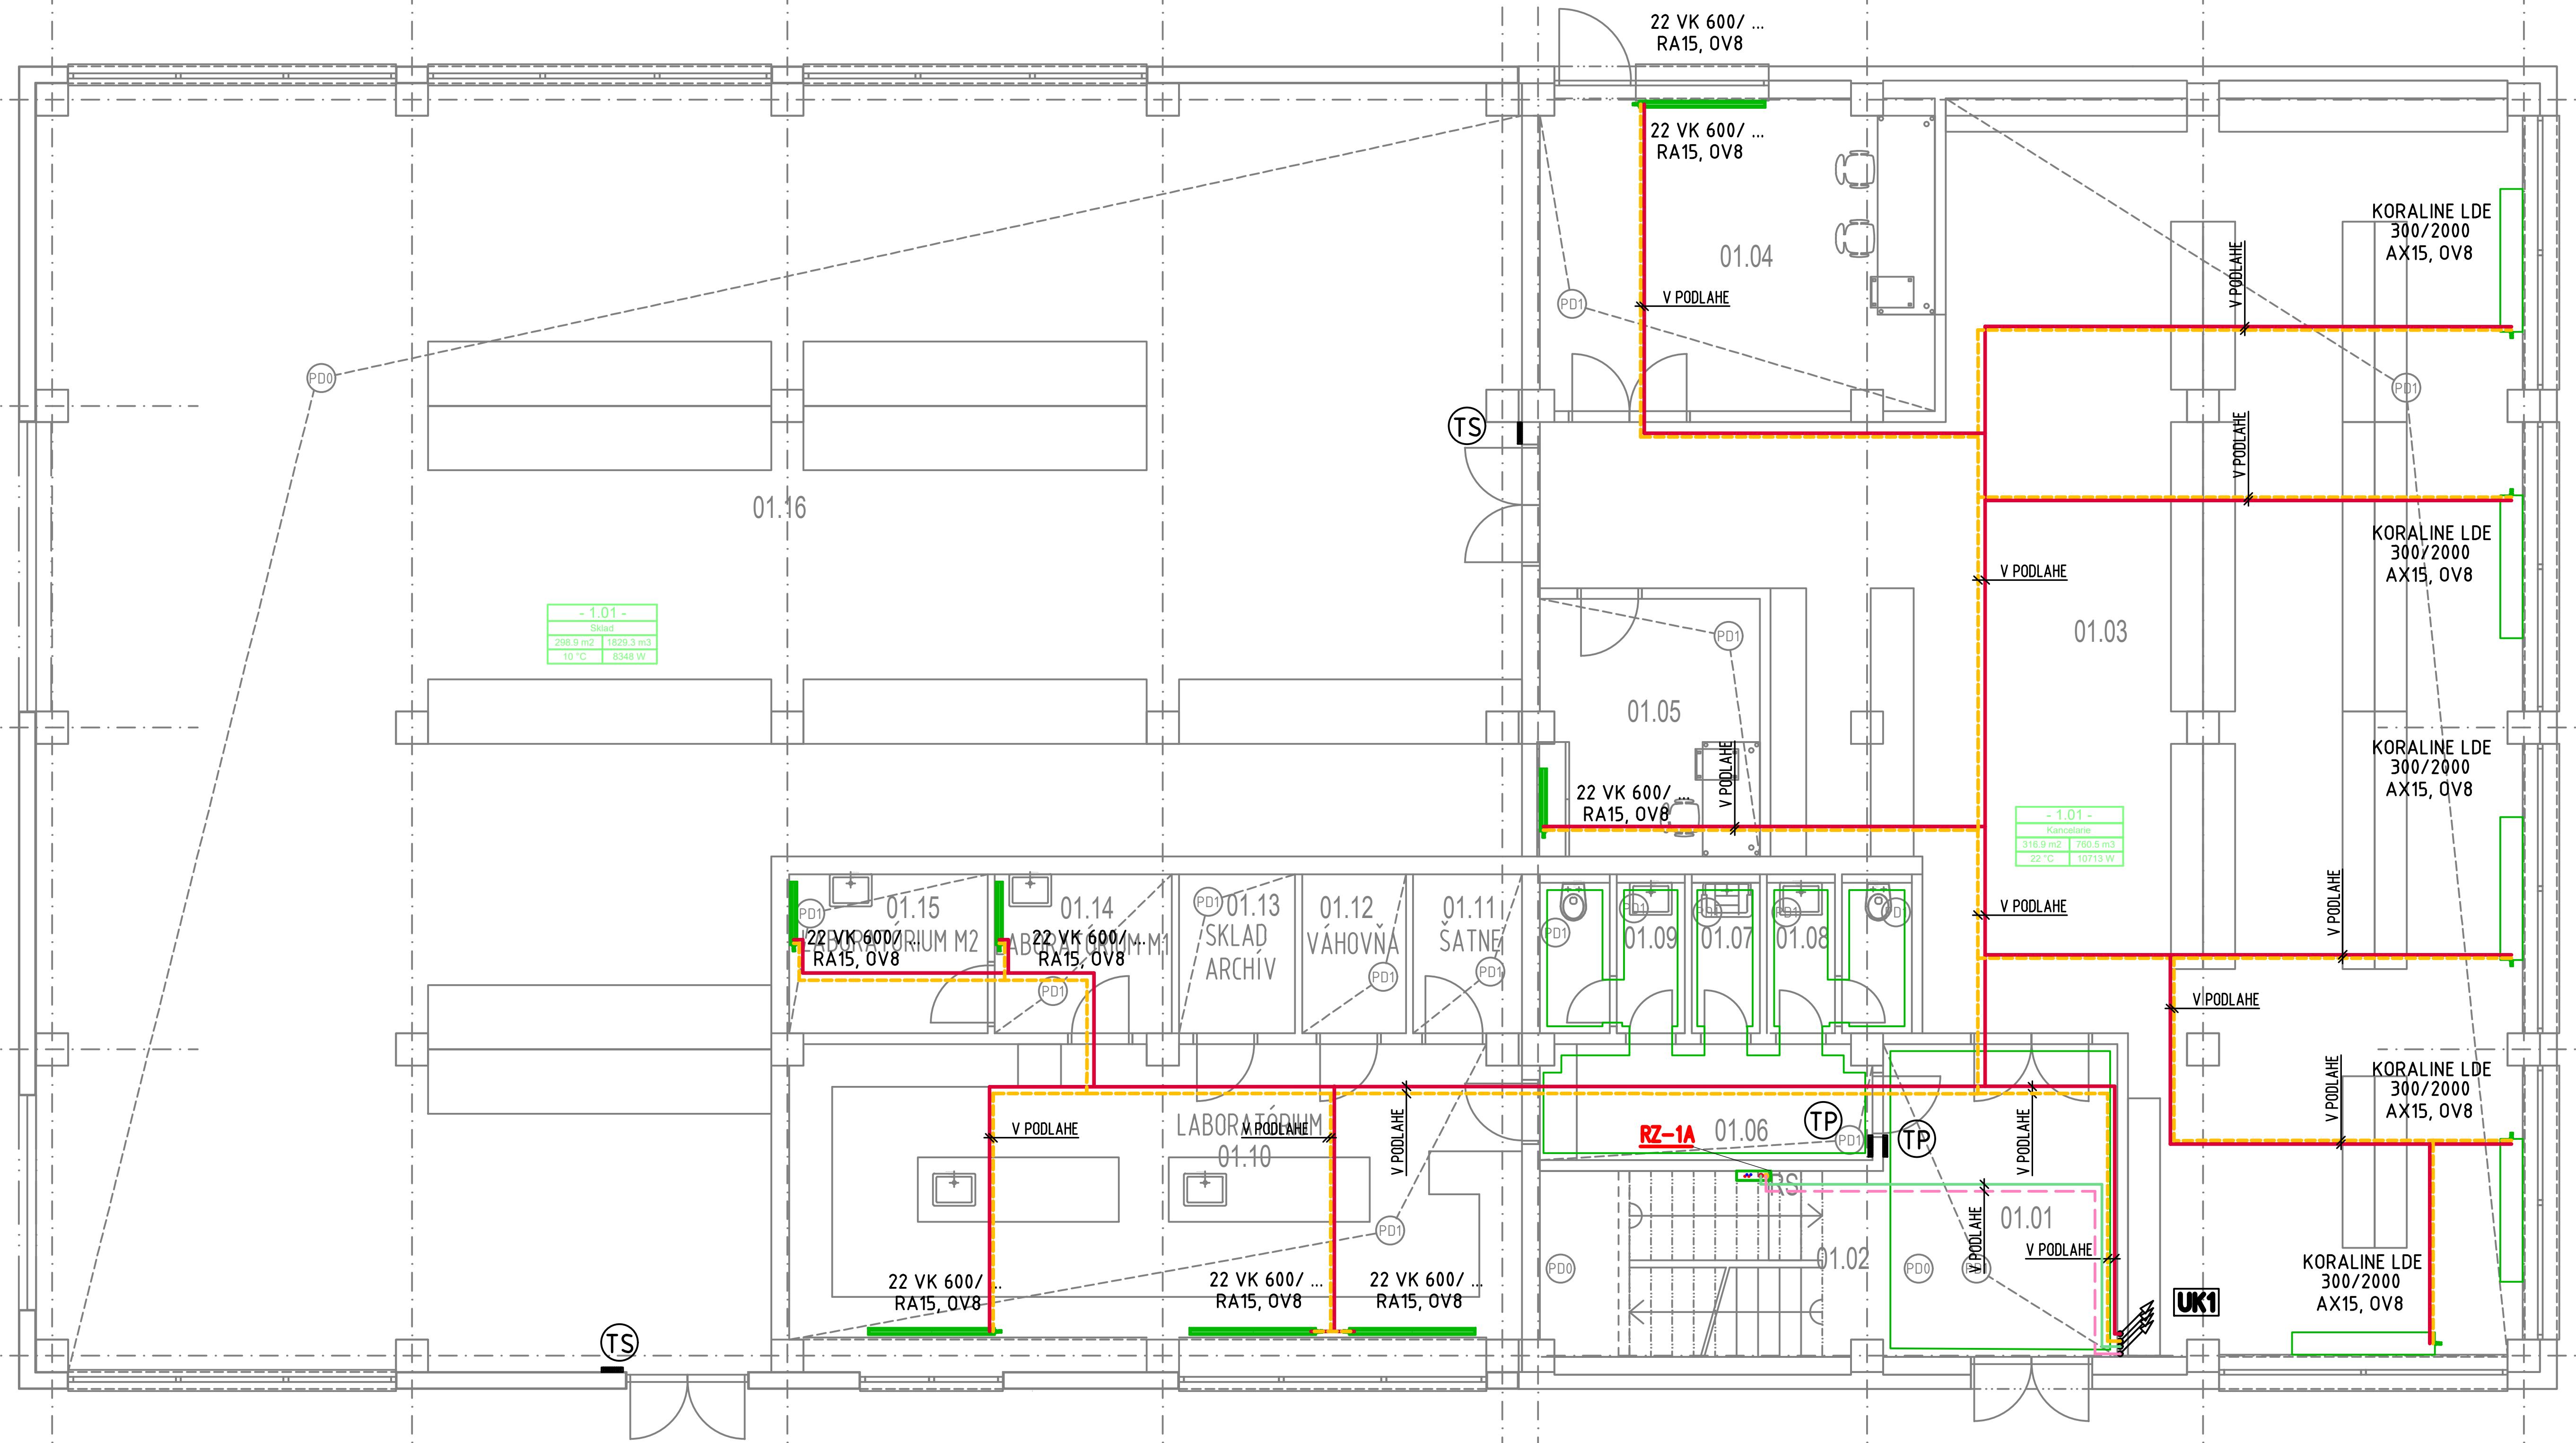

LEGENDA ZARIADENÍ A ARMATÚR :

RA	RADIATOROVÝ VENTIL NAPR. VERAFIX-VKE, UZATVÁRACIE ŠRÓBENIE H-BLOK S VONKAJŠÍM ZÁVITOM EUROKONUS PRE VYKUROVACIE TELESÁ TYPU VENTIL-KOMPAKT, ROHOVÝ, DN15 PRIPOJENIE RADIÁTORA VONKAJŠÍ ZÁVIT 1/2", PRIPOJENIE RÚRKY VONKAJŠÍ ZÁVIT 3/4" TERMOSTATICKÁ HLAVICA ZOSILNENÁ 2080 FL SO VSTAVANÝM KVAPALINOVÝM SNÍMAČOM, ROZSAH 6-28°C
AX	AXIÁLNY TERMOSTATICKÝ VENTIL (SÚČASŤ DODÁVKY TELESA)
GV	GUĽOVÝ VENTIL ZÁVITOVÝ
RV	PREDNASTAVITEĽNÝ REGULAČNÝ VENTIL PRIAMY - STAD
VK	VYPÚŠŤACÍ KOHÚT
OV	ODVZDUŠŇOVACÍ VENTIL
TP	PRIESTOROVÝ REGULÁTOR NEA SMART 2.0 PRE MERANIE TEPLOTY V MIESTNOSTI, FY. REHAU
UK1	STÚPAČKA VYKUROVANIA
TS	Termostat SALUS týdenní programovatelný, 0-230V, 0,5°C, 5A, pro ALFA, SIGMA, ZETA, COMPACT
RZ	ROZDELOVACIA STANICA PRE VYKUROVACIE TELESÁ A PODLAHOVĚ VYKUROVANIE

LAVICOVÉ VYKUROVACIE TELESO KORALINE LDE 300/2000
PRIPOJENIE CEZ AXIÁLNY TERMOSTATICKÝ VENTIL (SÚČASŤ DODÁVKY TELESA)

OCEĽOVÉ DOSKOVÉ VYKUROVACIE TELESO RADIK VK
TYP VENTIL KOMPAKT, S PRAVÝM SPODNÝM PRIPOJENÍM

SPÔSOB ZNAČENIA
22 VK 600/ ...

- STAVEBNÁ DĹŽKA V MILIMETROCH
- STAVEBNÁ VÝŠKA V MILIMETROCH
- PREVEDENIE VENTIL-KOMAPKT
- TYP DVOJRADOVÝ

LEGENDA PODLAHOVÉHO VYKUROVANIA:

PODLAHOVÉ KÚRENIE REHAU

Rúrka RAUTHERM S 17x2,0	TYP VYKUROVACEJ RÚRKY
VARIONOVA	SYSTÉM PODLAHOVÉHO VYKUROVANIA

DETAIL ZAPOJENIA VYKUROVACÍCH TELIES
DOSKOVÉ VYKUROVACIE TELESO

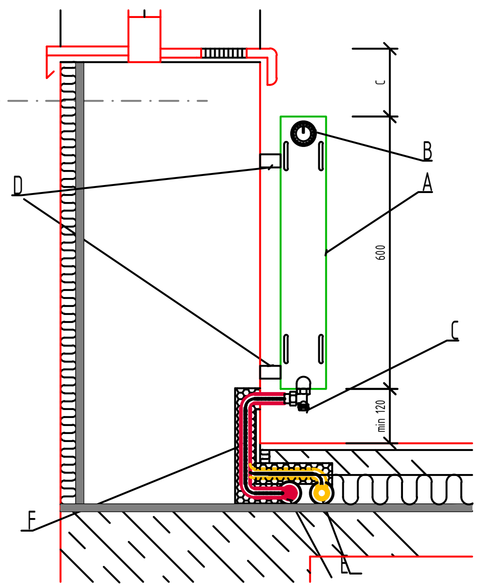

DETAIL OSADENIA VYK. TELESA
NA ROZVODY ÚK, M = 1:25

- A OCEĽOVÉ VYKUROVACIE TELESO TYP VK
- B TERMOSTATICKÁ HLAVICA
- C ROHOVÁ PRIPOJOVACIA ARMATÚRA PRE DVOJTRUBKOVÉ SYSTÉMY
- D DRŽIAK
- E ROZVODY ÚSTREDNÉHO KÚRENIA
- F TRUBICOVÁ IZOLÁCIA

DETAIL ZAPOJENIA VYKUROVACÍCH TELIES
REBRÍKOVÉ VYKUROVACIE TELESO

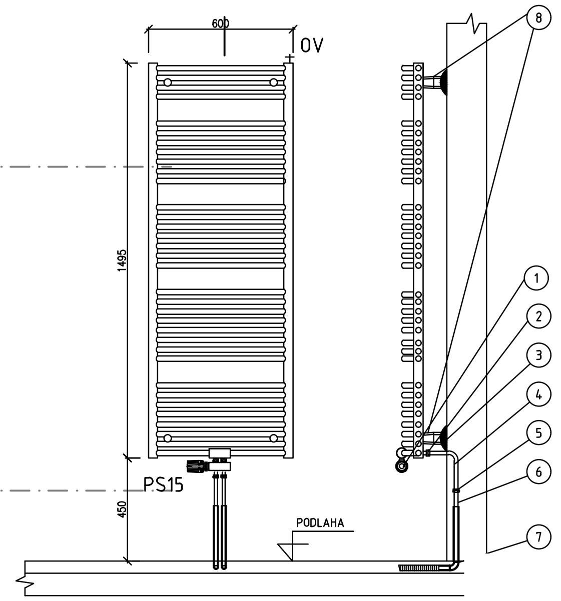

LEGENDA:

1 Stredové pripojenie vykurovacieho telesa, roz
rohové, farbia biela
2 Svorková spojka
3 Krycia rozeta
4 Pripojovacia garnitúra s upevňovacím
5 Násuvná objímka
6 Vykurovacia rúrka
7 Vodiaci oblúk 90°
8 Stenová konzola

LEGENDA MIESTNOSTÍ 1.N.P

Č.M.	ÚČEL MIESTNOSTI	PLOCHA (m2)	POPIS POVRCHOVÝCH ÚPRAV		
			PODLAHA	STENY	STROPY
01.01	VSTUP - CHODBA	10,50	KERAMICKÁ DLAŽBA	SÁDROVÁ OMIETKA	SDK PODHĽAD - PLNÝ
01.02	SCHODISKO	14,60	KERAMICKÁ DLAŽBA	SÁDROVÁ OMIETKA	SDK PODHĽAD - PLNÝ
01.03	PREDAJŇA	153,55	VINYL	SÁDROVÁ OMIETKA	SDK PODHĽAD - PLNÝ
01.04	BALIAREŇ - E-SHOP	23,82	VINYL	SÁDROVÁ OMIETKA	SDK PODHĽAD - PLNÝ
01.05	KANCELÁRIA VEDÚCEHO	11,04	VINYL	SÁDROVÁ OMIETKA	SDK PODHĽAD - PLNÝ
01.06	CHODBA	8,78	VINYL	KERAM. OBKLAD	SDK PODHĽAD - PLNÝ
01.07	UPRATOVAČKA	2,11	KERAMICKÁ DLAŽBA	SÁDROVÁ OMIETKA	SDK PODHĽAD - PLNÝ
01.08	WC MUŽI	4,27	KERAMICKÁ DLAŽBA	SÁDROVÁ OMIETKA	SDK PODHĽAD - PLNÝ
01.09	WC ŽENY	4,27	KERAMICKÁ DLAŽBA	SÁDROVÁ OMIETKA	SDK PODHĽAD - PLNÝ
01.10	LABORATÓRIUM	42,03	VINYL	SÁDROVÁ OMIETKA	SDK PODHĽAD - PLNÝ
01.11	ŠATNE	3,39	VINYL	SÁDROVÁ OMIETKA	SDK PODHĽAD - PLNÝ
01.12	VÁHOVŇA	3,22	VINYL	SÁDROVÁ OMIETKA	SDK PODHĽAD - PLNÝ
01.13	SKLAD	3,61	VINYL	SÁDROVÁ OMIETKA	SDK PODHĽAD - PLNÝ
01.14	LABORATÓRIUM M1	5,51	VINYL	SÁDROVÁ OMIETKA	SDK PODHĽAD - PLNÝ
01.15	LABORATÓRIUM M2	6,17	VINYL	SÁDROVÁ OMIETKA	SDK PODHĽAD - PLNÝ
01.16	SKLAD	296,34	LIATA PODLAHA	SÁDROVÁ OMIETKA	BEZ PODHĽADU

CELKOM	593,27

LEGENDA POTRUBIA:

POTRUBIE - PLASTHLINNÍKOVÁ RÚRKA NAPR. GEBERIT MEPLA
SPÁJANÉ LISOVANÍM, IZOLOVANÉ POTRUBIE, TEPLOTNÝ SPÁD 70/50°C
POTRUBIE VEDENÉ POD STROPOM, PRE RADIATORI, PRÍVOD A SPIATOČKA

POTRUBIE - PLASTHLINNÍKOVÁ RÚRKA NAPR. GEBERIT MEPLA
SPÁJANÉ LISOVANÍM, IZOLOVANÉ POTRUBIE, TEPLOTNÝ SPÁD 45/35°C
POTRUBIE VEDENÉ V PODLAHE, V ŠACHTE, PRE PODLAHOVÉ VYKUROVANIE, PRÍVOD A SPIATOČKA

POZNÁMKA :

- V PRÍPADE NEJASNOSTÍ VO VÝKRESOVEJ DOKUMENTÁCIÍ KONTAKTOVAŤ ZODPOVEDNÉHO PROJEKTANTA
- VŠETKY ROZMERY STAVEBNÝCH PRÁC KONTROLOVAŤ NA MIESTE STAVBY
- PRED UVEDENÍM SYSTÉMU DO PREVÁDZKY JE POTREBNÉ VYKONAŤ DÔKLADNÝ PREPLACH SYSTÉMU S VYČISTENÍM VŠETKÝCH FILTROV NA ROZVODE
- PO NAPUSTENÍ SYSTÉMU JE POTREBNÉ VYKONAŤ JEHO ODVZDUŠNENIE
- DODÁVATEL STAVBY JE POVINNÝ REALIZOVAŤ VŠETKY PRÁCE V ZMYSLE PLATNÝCH STN EN S DODRŽANÍM TECHNOLOGICKÝCH A BEZPEČNOSTNÝCH POSTUPOV. ĎALEJ JE POVINNÝ REŠPEKTOVAŤ USTANOVENIÁ STN 730421 O PRÍSLUŠNÝCH ROZMEROVÝCH ODCHÝLKACH REALIZOVANÝCH KONŠTRUKCIÍ PROTI PROJEKTOVANÉMU STAVU. KAŽDÚ ODCHÝLKU OD PROJEKTU JE POTREBNÉ PREROKOVAŤ S GP.
- PRESTUPY INŽINIERSKYCH SIETÍ A ROZVODOV V OBJEKTE JE POTREBNÉ VYNECHAŤ PRI REALIZÁCII STAVBY.
- PROJEKTOVÁ DOKUMENTÁCIA JE SPRACOVANÁ PRE ÚČEL VYDANIA STAVEBNÉHO POVOLENIA A NENAHRÁDZA REALIZAČNÝ PROJEKT