
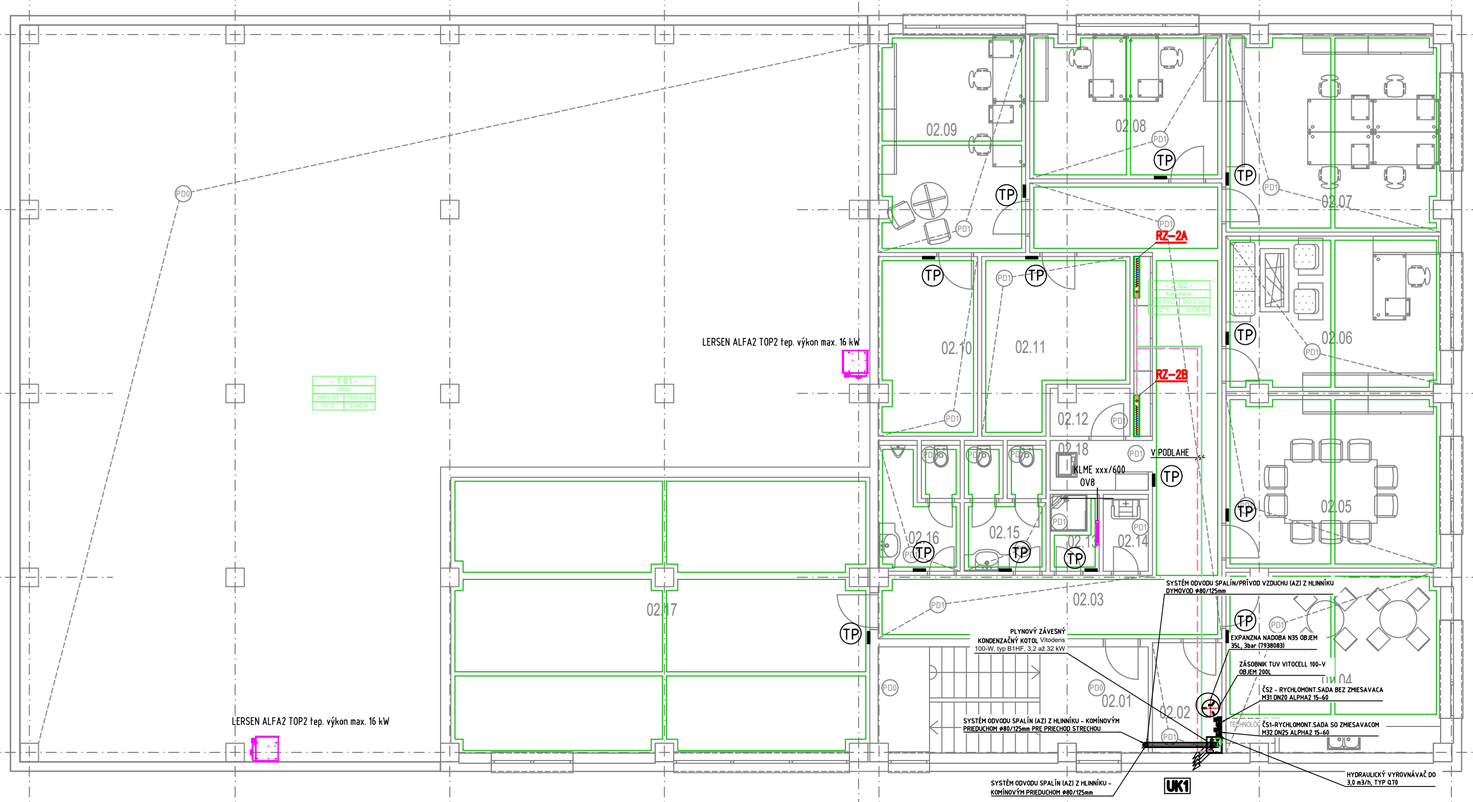



DETAIL ZAPOJENIA VYKUROVACÍCH TELIES DOSKOVÉ VYKUROVACIE TELESO

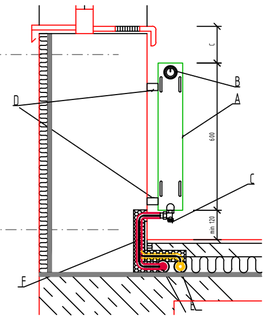

DETAIL OSADENIA VYK. TELESA NA ROZVODY ÚK, M = 1:25

A OCEĽOVÉ VYKUROVACIE TELESO TYP VK
B TERMOSTATICKÁ HLAVICA
C ROHOVÁ PRIPOJOVACIA ARMATÚRA PRE DVOJTRUBKOVÉ SYSTÉMY
D DRŽIAK
E ROZVODY ÚSTREDNÉHO KÚRENIA
F TRUBICOVÁ IZOLÁCIA

DETAIL ZAPOJENIA VYKUROVACÍCH TELIES REBRÍKOVÉ VYKUROVACIE TELESO

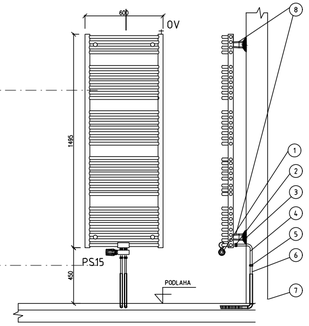

LEGENDA:

1 Stredové pripojenie vykurovacieho telesa, ro:
rohové, farbia biela
2 Svorková spojka
3 Krycia rozeta
4 Pripojovacia garnitúra s upevňovacím
5 Násuvná objímka
6 Vykurovacia rúrka
7 Vodiaci oblúk 90°
8 Stenová konzola

LEGENDA MIESTNOSTÍ 2.N.P

Č.M.	ÚČEL MIESTNOSTI	PLOCHA [m2]	POPIS POVRCHOVÝCH ÚPRAV		
			PODLAHA	STENY	STROPY
02.01	SCHODISKO	17,00	KERAMICKÁ DLAŽBA	SÁDROVÁ OMIETKA	SDK PODHĽAD - PLNÝ
02.02	ARCHÍV	4,59	VINYL	SÁDROVÁ OMIETKA	SDK PODHĽAD - PLNÝ
02.03	CHODBA	36,36	VINYL	SÁDROVÁ OMIETKA	SDK PODHĽAD - PLNÝ
02.04	KUCHYNKA	22,78	VINYL	SÁDROVÁ OMIETKA	SDK PODHĽAD - PLNÝ
02.05	ZASADAČKA	22,07	VINYL	SÁDROVÁ OMIETKA	SDK PODHĽAD - PLNÝ
02.06	KANCELÁRIA RIADITEĽ	19,84	VINYL	KERAM. OBKLAD	SDK PODHĽAD - PLNÝ
02.07	KANCELÁRIA	25,23	VINYL	SÁDROVÁ OMIETKA	SDK PODHĽAD - PLNÝ
02.08	KANCELÁRIA OBCHOD	16,58	VINYL	SÁDROVÁ OMIETKA	SDK PODHĽAD - PLNÝ
02.09	KANCELÁRIA EKONÓM	19,14	VINYL	SÁDROVÁ OMIETKA	SDK PODHĽAD - PLNÝ
02.10	ARCHÍV	10,60	VINYL	SÁDROVÁ OMIETKA	SDK PODHĽAD - PLNÝ
02.11	SKLAD	13,33	VINYL	SÁDROVÁ OMIETKA	SDK PODHĽAD - PLNÝ
02.12	SERVER	2,13	VINYL	SÁDROVÁ OMIETKA	SDK PODHĽAD - PLNÝ
02.13	SPRCHA	2,26	KERAMICKÁ DLAŽBA	SÁDROVÁ OMIETKA	SDK PODHĽAD - PLNÝ
02.14	UPRATOVAČKA	2,07	KERAMICKÁ DLAŽBA	SÁDROVÁ OMIETKA	SDK PODHĽAD - PLNÝ
02.15	WC ŽENY	6,40	KERAMICKÁ DLAŽBA	SÁDROVÁ OMIETKA	SDK PODHĽAD - PLNÝ
02.16	WC MUŽI	6,40	KERAMICKÁ DLAŽBA	SÁDROVÁ OMIETKA	SDK PODHĽAD - PLNÝ
02.17	VOĽNÝ PRIESTOR	68,60	VINYL	SÁDROVÁ OMIETKA	SDK PODHĽAD - PLNÝ
02.18	COPY POINT	3,00	VINYL	SÁDROVÁ OMIETKA	SDK PODHĽAD - PLNÝ

LEGENDA POTRUBÍ:

POTRUBIE - PLASTHLINNÍKOVÁ RÚRKA NAPR. GEBERIT MEPLA
SPÁJANÉ LISOVANÍM, IZOLOVANÉ POTRUBIE, TEPLOTNÝ SPÁD 70/50°C
POTRUBIE VEDENÉ POD STROPOM, PRE RADIATORI, PRÍVOD A SPIATOČKA

POTRUBIE - PLASTHLINNÍKOVÁ RÚRKA NAPR. GEBERIT MEPLA
SPÁJANÉ LISOVANÍM, IZOLOVANÉ POTRUBIE, TEPLOTNÝ SPÁD 45/35°C
POTRUBIE VEDENÉ V PODLAHE, V ŠACHTE, PRE PODLAHOVÉ VYKUROVANIE, PRÍVOD A SPIATOČKA

POZNÁMKA :

- V PRÍPADE NEJASNOSTÍ VO VÝKRESOVEJ DOKUMENTÁCII KONTAKTOVAŤ ZODPOVEDNÉHO PROJEKTANTA
- VŠETKY ROZMERY STAVEBNÝCH PRÁC KONTROLOVAŤ NA MIESTE STAVBY
- PRED UVEDENÍM SYSTÉMU DO PREVÁDZKY JE POTREBNÉ VYKONAŤ DÔKLADNÝ PREPLACH SYSTÉMU S VYČISTENÍM VŠETKÝCH FILTROV NA ROZVODE
- PO NAPUSTENÍ SYSTÉMU JE POTREBNÉ VYKONAŤ JEHO ODVZDUŠNENIE
- DODÁVATEL STAVBY JE POVINNÝ REALIZOVAŤ VŠETKY PRÁCE V ZMYSLE PLATNÝCH STN EN S DODRŽANÍM TECHNOLOGICKÝCH A BEZPEČNOSTNÝCH POSTUPOV. ĎALEJ JE POVINNÝ REŠPEKTOVAŤ USTANOVENIA STN 730421 O PRÍSLUŠNÝCH ROZMEROVÝCH ODCHÝLKACH REALIZOVANÝCH KONŠTRUKCIÍ PROTI PROJEKTOVANÉMU STAVU. KAŽDÚ ODCHÝLKU OD PROJEKTU JE POTREBNÉ PREROKOVAŤ S GP.
- PRESTUPY INŽINIERSKYCH SIETÍ A ROZVODOV V OBJEKTE JE POTREBNÉ VYNECHAŤ PRI REALIZÁCII STAVBY.
- PROJEKTOVÁ DOKUMENTÁCIA JE SPRACOVANÁ PRE ÚČEL VYDANIA STAVEBNÉHO POVOLENIA A NENAHRÁDZA REALIZAČNÝ PROJEKT

LEGENDA ZARIADENÍ A ARMATÚR :

PS	PRIPÁJACÍ BLOK S INTEGROVANÝM TERMOSTATICKÝM VENTILOM TYP BB PRE VYKUROVACIE TELESÁ SO STREDOVÝM PRIPOJENÍM, ROHOVÉ, DN15, PRIPOJENIE RADIÁTORA VONKAJŠÍ ZÁVIT 1/2", PRIPOJENIE DO STENY VONKAJŠÍ ZÁVIT 3/4" S TERMOSTATICKOU HLAVICOU NAPR. THERA-4 KLASIK S KVAPAL. SNÍMAČOM
GV	GUĽOVÝ VENTIL ZÁVITOVÝ
RV	PREDNASTAVITEĽNÝ REGULAČNÝ VENTIL PRIAMY - STAD
VK	VYPÚŠŤACÍ KOHÚT
OV	ODVZDUŠŇOVACÍ VENTIL
TP	PRIESTOROVÝ REGULÁTOR NEA SMART 2.0 PRE MERANIE TEPLOTY V MIESTNOSTI, FY. REHAU
UK1	STÚPAČKA VYKUROVANIA
TS	Termostat SALUS týdenní programovatelný, 0-230V, 0,5°C, 5A, pro ALFA, SIGMA, ZETA, COMPACT
RZ	ROZDELOVACIA STANICA PRE VYKUROVACIE TELESÁ A PODLAHOVÉ VYKUROVANIE

LAVICOVÉ VYKUROVACIE TELESO KORALINE LDE 300/2000

SPÔSOB ZNAČENIA
22 VK 600/ ...
- STAVEBNÁ DĹŽKA V MILIMETROCH
- STAVEBNÁ VÝŠKA V MILIMETROCH
- PREVEDENIE VENTIL-KOMAPKT
- TYP DVOJRADOVÝ

OCEĽOVÉ DOSKOVÉ VYKUROVACIE TELESO RADIK VK
TYP VENTIL KOMPAKT, S PRAVÝM SPODNÝM PRIPOJENÍM

REBRÍKOVÉ VYKUROVACIE TELESO TYP KORALUX LINEAR MAX-E, FY. KORADO

PLYNOVÝ TEPLOVZDUŠNÝ OHRIEVAČ LERSEN ALFA2 TOP2 tep. výkon max. 16 kW

LEGENDA PODLAHOVÉHO VYKUROVANIA:

PODLAHOVÉ KÚRENIE REHAU

Rúrka RAUTHERM S 17x2,0 VARIONOVA	TYP VYKUROVACEJ RÚRKY SYSTÉM PODLAHOVÉHO VYKUROVANIA