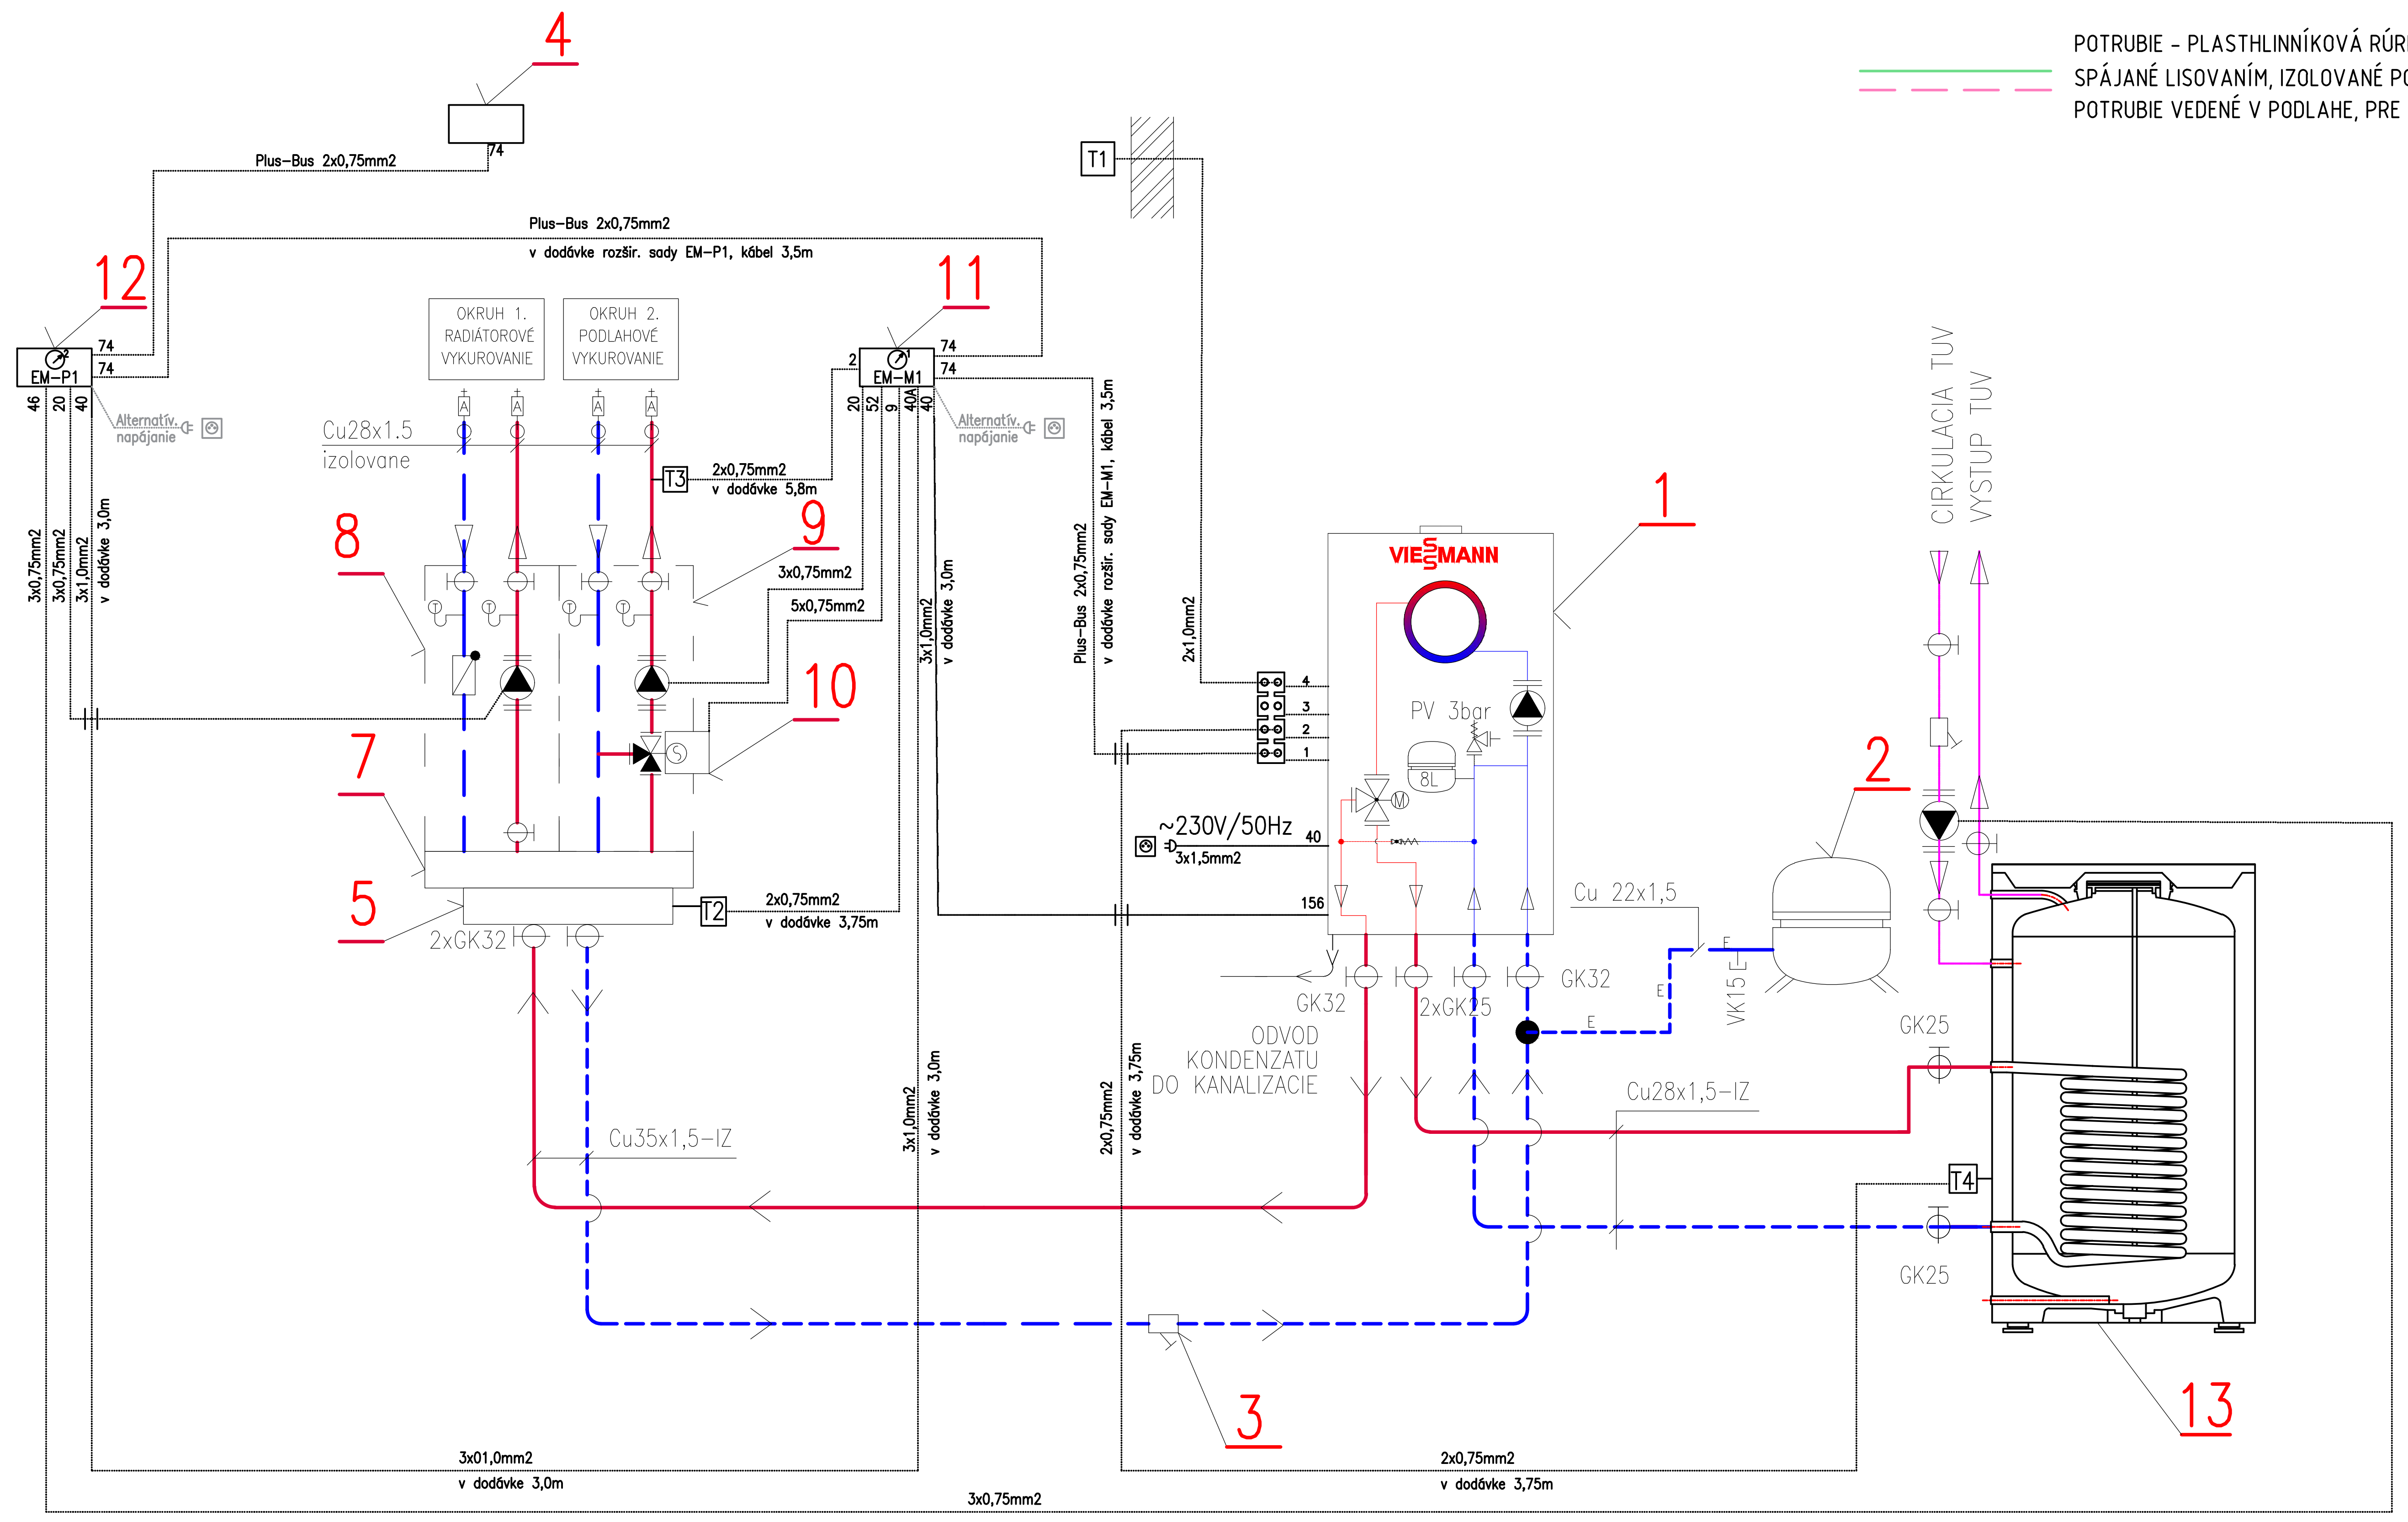
4
Plus-Bus 2x0,75mm2
74
T1
Plus-Bus 2x0,75mm2
v dodávke rozšir. sady EM-P1, kábel 3,5m
12
11
EM-P1
74
74
46
20
40
Alternatív. napájanie
OKRUH 1. RADIÁTOROVÉ VYKUROVANIE
OKRUH 2. PODLAHOVÉ VYKUROVANIE
EM-M1
2
74
74
20
52
9
40A
40
Alternatív. napájanie
Cu28x1.5
izolovane
T3
2x0,75mm2
v dodávke 5,8m
9
8
3x0,75mm2
5x0,75mm2
10
7
5
T2
2x0,75mm2
v dodávke 3,75m
2xGK32
3x0,75mm2
3x0,75mm2
3x1,0mm2
v dodávke 3,0m
3x1,0mm2
v dodávke 3,0m
Plus-Bus 2x0,75mm2
v dodávke rozšir. sady EM-M1, kábel 3,5m
2x1,0mm2
1
VIESSMANN
PV 3bar
8L
4
3
2
1
~230V/50Hz
40
3x1,5mm2
156
GK32
2xGK25
GK32
ODVOD KONDENZATU DO KANALIZACIE
Cu 22x1,5
VK15
E
E
E
2
CIRKULACIA TUV
VYSTUP TUV
GK25
Cu28x1,5-IZ
T4
GK25
13
Cu35x1,5-IZ
3x1,0mm2
v dodávke 3,0m
2x0,75mm2
v dodávke 3,75m
3
3x01,0mm2
v dodávke 3,0m
2x0,75mm2
v dodávke 3,75m
3x0,75mm2

LEGENDA POTRUBIA:

━━━━ POTRUBIE - PLASTHLINNÍKOVÁ RÚRKA NAPR. GEBERIT MEPLA
– – – – SPÁJANÉ LISOVANÍM, IZOLOVANÉ POTRUBIE, TEPLOTNÝ SPÁD 70/50°C
POTRUBIE VEDENÉ V PODLAHE, PRE RADIATORI

━━━━ POTRUBIE - PLASTHLINNÍKOVÁ RÚRKA NAPR. GEBERIT MEPLA
– – – – SPÁJANÉ LISOVANÍM, IZOLOVANÉ POTRUBIE, TEPLOTNÝ SPÁD 45/35°C
POTRUBIE VEDENÉ V PODLAHE, PRE PODLAHOVÉ VYKUROVANIE

LEGENDA ZARIADENÍ:

POZ.	NÁZOV, ROZMER	P. KS
1	KONDENZAČNY KOTOL VIESSMANN VITODENS 100-W, TYP B1HF 3,2-32kW, 7-segment. displej	1
	MONTÁŽNE POMOCKA NA OMIETKU (ZK04307)	1
2	TLAKOVÁ EXPANZNÁ NÁDOBA S MEMBRÁNOU VIESSMANN N 35-BIELA+ BEZP. ARMATÚRA	1
3	ODKALOVAČ VITOTRAP S IZOLÁCIOU 1 1/4" (ZK04657)	1
4	DIALKOVÉ OVLÁDANIE VITOTROL 200-E (Z017415)	1
5	MODULÁRNY HYDRAULICKÝ VYROVNÁVAČ TLAKOV VIESSMANN DN25, DO 3,5 m3/h (7741533)	1
	PÚZDRO PRE PONORNÝ SNÍMAČ (9556119)	1
6	PONORNÝ SNÍMAČ TEPLOTY HVDT (ZK04032)	1
7	MODULÁRNY ROZDELOVAČ PRE 2 OKRUHY DN25 (7741065)	1
	UPEVNENIE NA STENU PRE ROZDELOVAČ DN25 (7011090)	1
8	RÝCHLOMONTÁŽNA SADA BEZ ZMIEŠAVAČA M31 DN20 ALPHA2-60 (7741073)	1
9	RÝCHLOMONTÁŽNA SADA SO ZMIEŠAVAČOM M32 DN25 ALPHA2-60 (7741079)	1
10	SERVOPOHON SR10 (7199567)	1
11	ROZŠIROVACIA SADA PRE JEDEN VYKUR.OKRUH SO ZMIEŠAVAČOM EM-M1 (Z017410)	1
12	ROZŠIROVACIA SADA PRE JEDEN VYKUR.OKRUH BEZ ZMIEŠAVAČA EM-P1 (Z017411)	1
13	ZÁSOBNíKOVÝ OHRIEVAČ PITNEJ VODY VITOCELL 100-W, TYP CVAA 200L-vitopearlwhite(Z018468)	1
T1	SNÍMAČ VONKAJŠEJ TEPLOTY (ZK04306)	1
T2	SNÍMAČ HVDT (ZK04032)	1
T3	SNÍMAČ VÝSTUPNEJ TEPLOTY (v dodávke poz. 11)	1
T4	SNÍMAČ ZÁSOBNIKA TÚV (ZK04671)	1

±0,000 = úroveň 1.N.P. = 126,40 m.n.m.