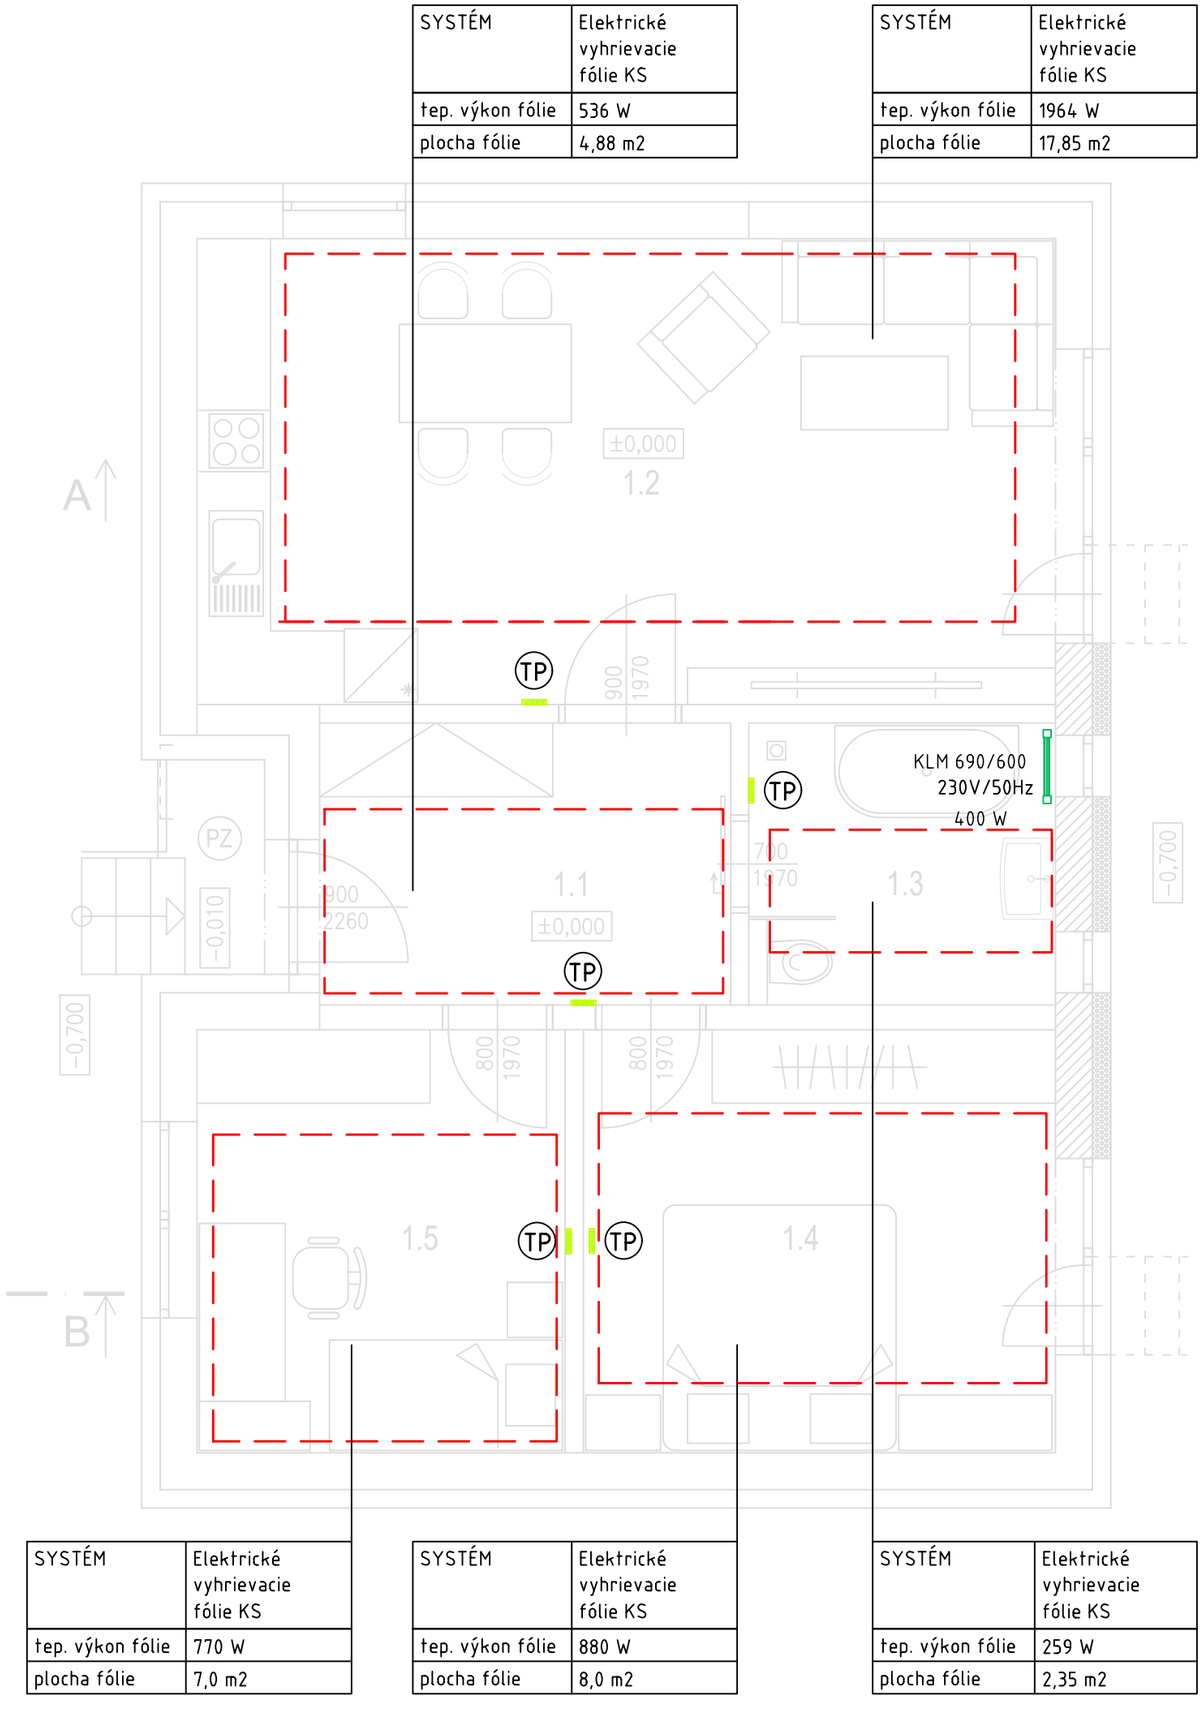


LEGENDA MIESTNOSTÍ 1.NP

Č.M.	NÁZOV MIESTNOSTI	PLOCHA m^2	PODLAHY	ÚPRAVY POVRCHOV		POZNÁMKA
				STENY	STROP	
1.1	PREDSIEŇ	8,40	KERAMICKÁ DLAŽBA	OMIETKA	OMIETKA	KERAM. SOKEL
1.2	OBÝVACIA IZBA + KUCHYŇA	26,60	LAMINÁTOVÉ PARKETY	OMIETKA	OMIETKA	K.OBKLAD PRI KUCH. LINKE
1.3	KÚPELŇA -WC	5,75	KERAMICKÁ DLAŽBA	KER.OBKLAD	OMIETKA	KER.OBKLAD v=2,1m
1.4	IZBA	13,11	LAMINÁTOVÉ PARKETY	OMIETKA	OMIETKA	LEMOVACIA LIŠTA
1.5	IZBA	10,06	LAMINÁTOVÉ PARKETY	OMIETKA	OMIETKA	LEMOVACIA LIŠTA
	SPOLU :	63,92				

LEGENDA:

FÓLIOVÁ TECHNOLÓGIA SYSTÉMU VYHRIEVANIA NA ZÁKLADE DLHOVLNNÉHO INFRAČERVENÉHO ŽIARENIA

TP PRIESTOROVÝ REGULÁTOR TEPLOTY PRE PODLAHOVÉ VYKUROVANIE, napr. Heatflow

ELEKRICKÉ REBRÍKOVÉ VYKUROVACIE TELESO napr. KORALUX LINEAR MAX-ERA

POZNÁMKY:

- VŠETKY ROZMERY STAVEBNÝCH PRÁC KONTROLOVAŤ NA MIESTE STAVBY
- DOPORUČUJEM PREKÁBLOVANIE JEDNOTLIVÝCH TERMOSTATOV PODLAHOVÉHO VYKUROVANIA
- V PRÍPADE NEJASNOSTÍ VO VÝKRESOVEJ DOKUMENTÁCIÍ KONTAKTOVAŤ ZODPOVEDNÉHO PROJEKTANTA S PRISLÚCHAJÚCOU REGULÁCIOU EŠTE PRED ZHOTOVENÍM OMIETOK
- DODÁVATEL STAVBY JE POVINNÝ REALIZOVAŤ VŠETKY PRÁCE V ZMYSLE PLATNÝCH STN EN S DODRŽANÍM TECHNOLOGICKÝCH A BEZPEČNOSTNÝCH POSTUPOV. ĎALEJ JE POVINNÝ REŠPEKTOVAŤ USTANOVENIA STN 730421 O PRÍSLUŠNÝCH ROZMEROVÝCH ODCHÝLKACH REALIZOVANÝCH KONŠTRUKCIÍ PROTI PROJEKTOVANÉMU STAVU. KAŽDÚ ODCHÝLKU OD PROJEKTU JE POTREBNÉ PREROKOVAŤ S GP.
- ±0,000 SA VZŤAHUJE K ÚROVNI FINÁLNEJ ÚPRAVY PODLAHY
- VÝBER VYKUROVACÍCH TELIES PODĽA INVESTORA