LEGENDA MIESTNOSTI

M.č.	NÁZOV	PLOCHA (m2)	Teplota (°C)
A_1.01	Obývačka	41,32 m²	
A_1.02	Vstup	16,25 m²	
A_1.03	Izba	12,58 m²	
A_1.04	Komora	2,83 m²	
A_1.05	Technická miestnosť	3,32 m²	
A_1.06	WC	1,63 m²	
A_1.07	Izba	12,61 m²	
A_1.08	Kúpeľňa	6,86 m²	
A_1.09	Spálňa	13,36 m²	
A_1.10	Izba	12,50 m²	
A_1.11	Kúpeľňa	5,70 m²	

- 1.11 -		- 1.10 -		- 1.09 -		- 1.08 -		- 1.07 -		- 1.05 -		- 1.03 -		- 1.02 -		- 1.01 -	
Kúpeľňa č.2		Izba č.3		Spálňa		Kúpeľňa č.1		Izba č.2		Technická		Izba č. 1		Vstup		Kuchyňa + Obývačka	
5.7 m2		12.5 m2		13.4 m2		6.9 m2		12.6 m2		3.3 m2		12.6 m2		16.0 m2		41.3 m2	
24 °C	396 W	22 °C	665 W	22 °C	535 W	24 °C	467 W	22 °C	601 W	20 °C	136 W	22 °C	738 W	20 °C	519 W	22 °C	2276 W

RZ 1 - 1. NP (11/2) (tp=45.0°C)	1.10 - Izba č.3
PZ 1: Laminátová podlaha	S=12.5 m2
Systém VARIONOVA	Rúrka RAUTHERM S 17x2,0
Lpz=200 [mm]	lo/lp=62.5 m/15.1 m

RZ 1 - 1. NP (11/1) (tp=45.0°C)	1.07 - Izba č.2
PZ 1: Laminátová podlaha	S=12.6 m2
Systém VARIONOVA	Rúrka RAUTHERM S 17x2,0
Lpz=200 [mm]	lo/lp=63.1 m/7.2 m

RZ 1 - 1. NP (11/11) (tp=45.0°C)	1.02 - Vstup
PZ 1: Keramická podlaha	S=7,8 m2
Systém VARIONOVA	Rúrka RAUTHERM S 17x2,0
Lpz=200 [mm]	lo/lp=63.1 m/7.2 m

RZ 1 - 1. NP (11/10) (tp=45.0°C)	1.03 - Izba č. 1
PZ 1: Laminátová podlaha	S=12.6 m2
Systém VARIONOVA	Rúrka RAUTHERM S 17x2,0
Lpz=200 [mm]	lo/lp=62.8 m/11.6 m

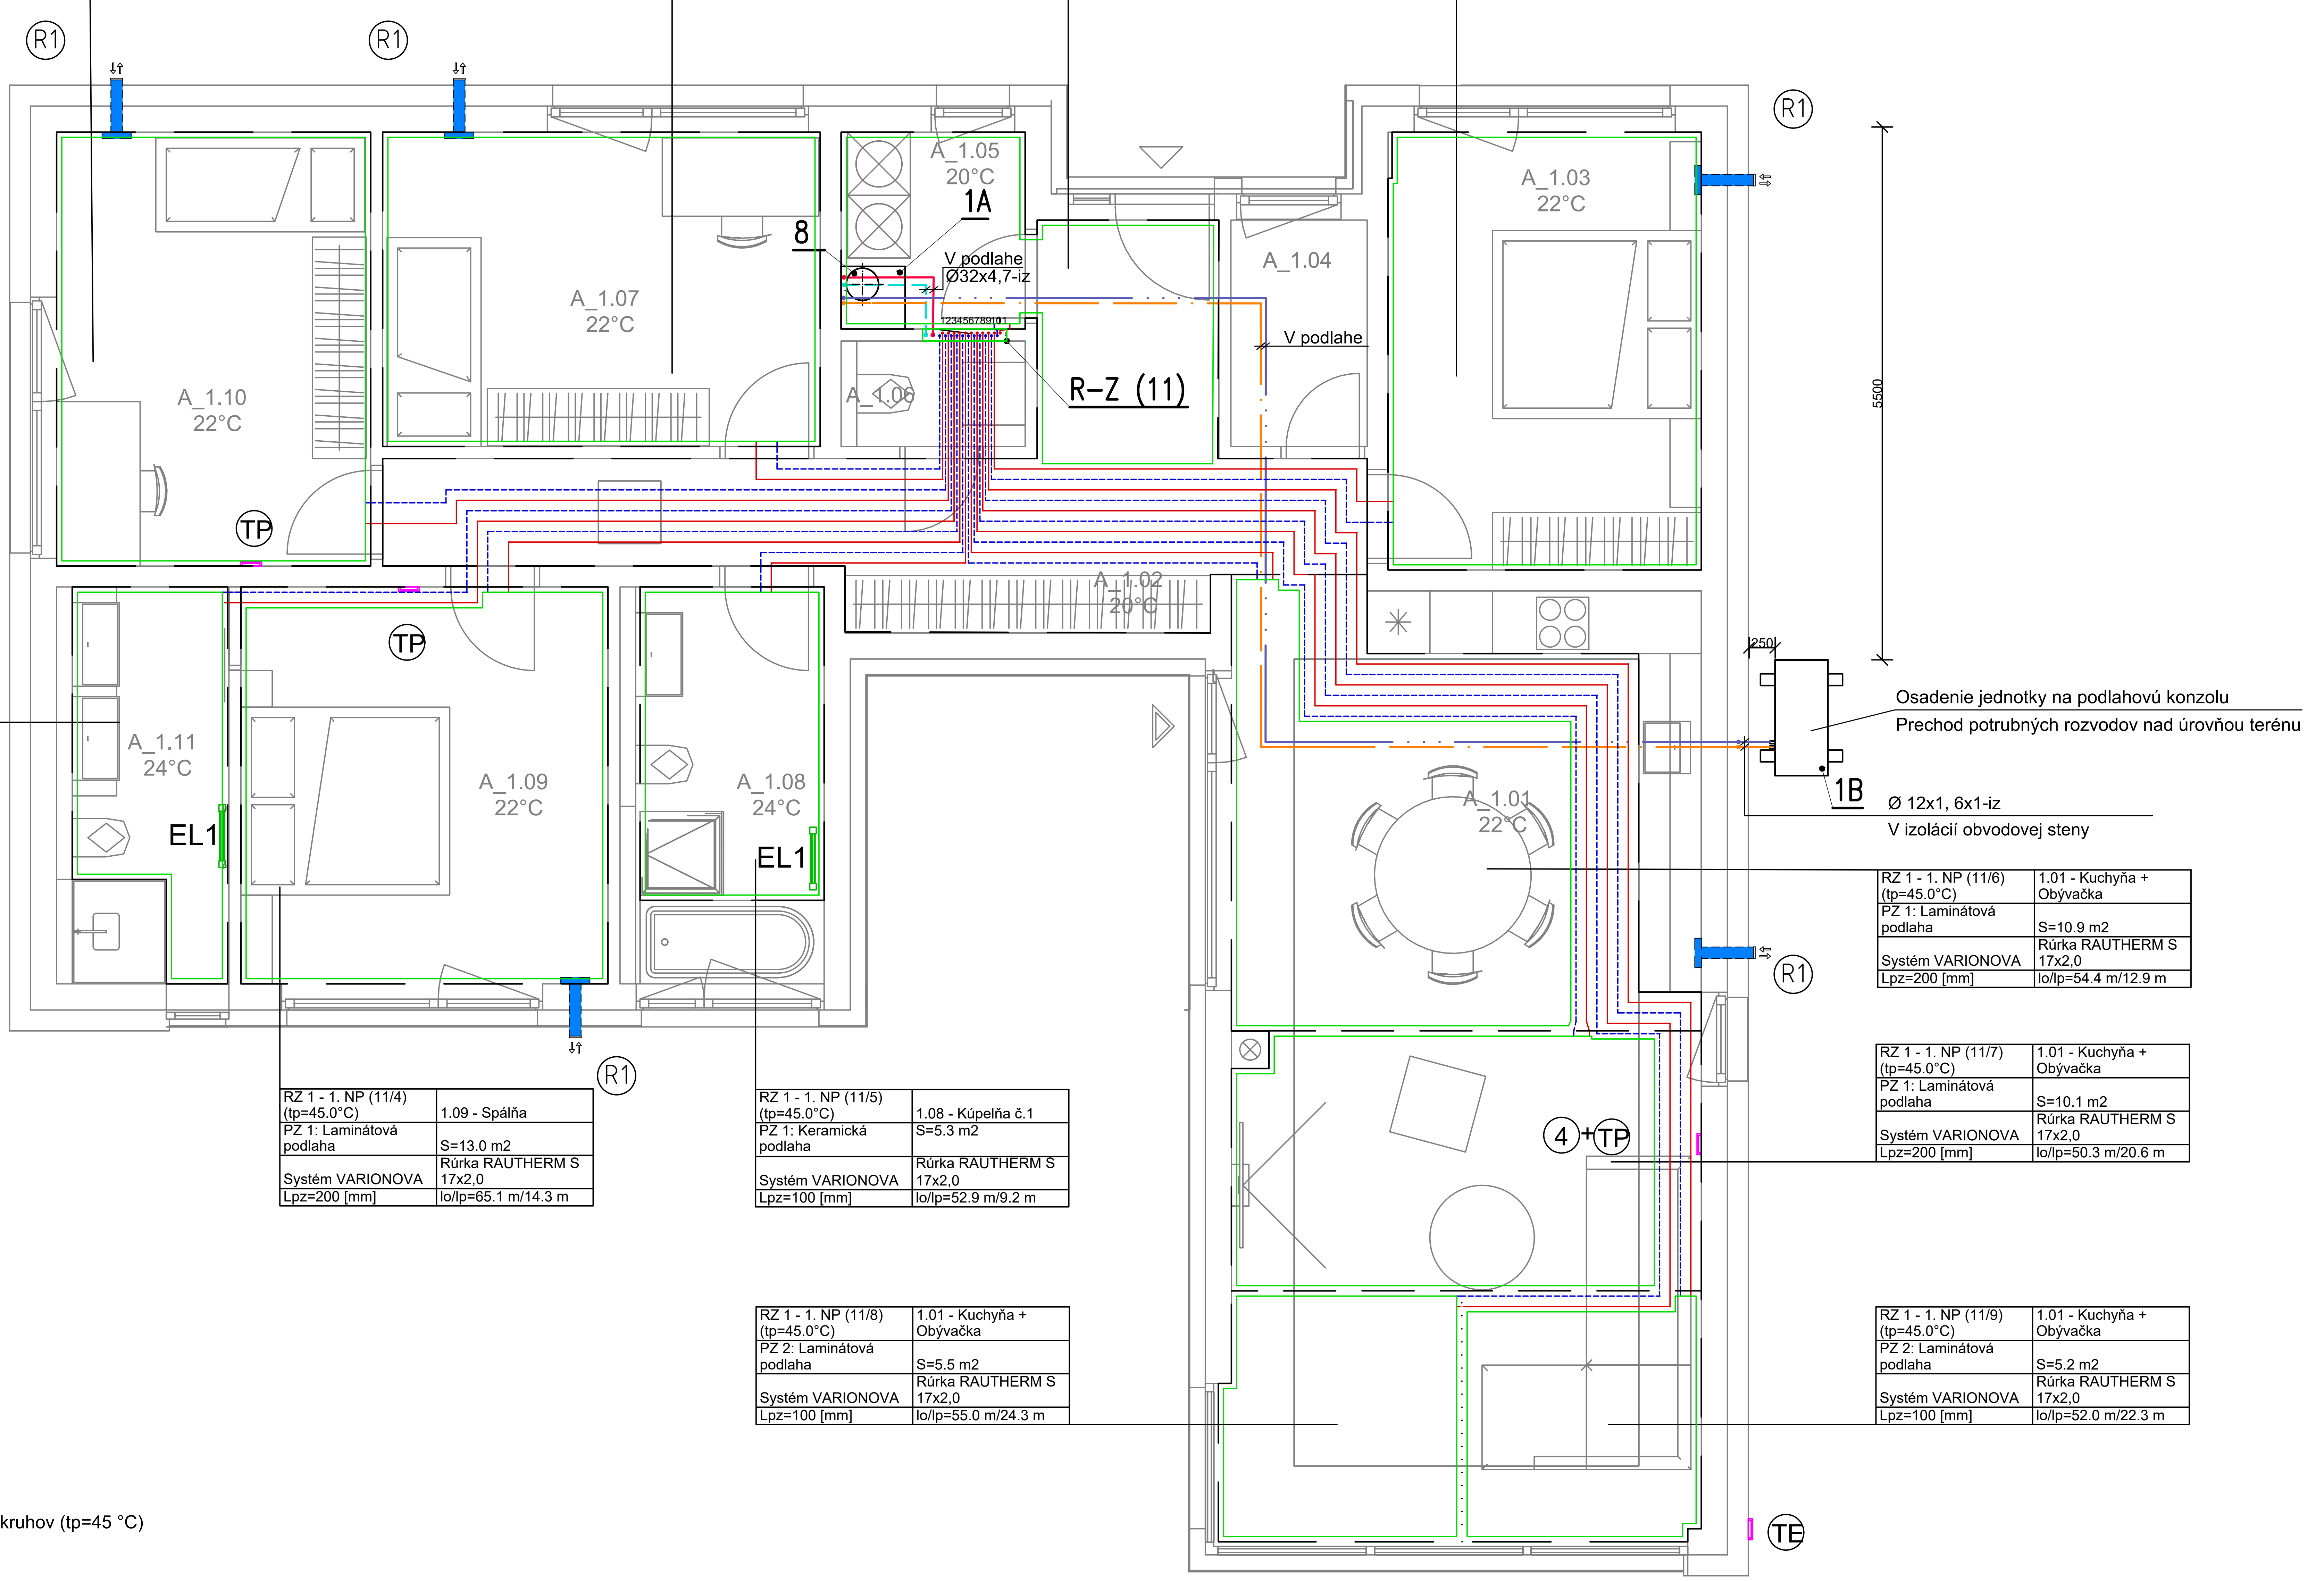

RZ 1 - 1. NP (11/3) (tp=45.0°C)	1.11 - Kúpeľňa č.2
PZ 1: Keramická podlaha	S=4.8 m2
Systém VARIONOVA	Rúrka RAUTHERM S 17x2,0
Lpz=100 [mm]	lo/lp=47.5 m/19.5 m

RZ 1 - 1. NP (11/6) (tp=45.0°C)	1.01 - Kuchyňa + Obývačka
PZ 1: Laminátová podlaha	S=10.9 m2
Systém VARIONOVA	Rúrka RAUTHERM S 17x2,0
Lpz=200 [mm]	lo/lp=54.4 m/12.9 m

RZ 1 - 1. NP (11/4) (tp=45.0°C)	1.09 - Spálňa
PZ 1: Laminátová podlaha	S=13.0 m2
Systém VARIONOVA	Rúrka RAUTHERM S 17x2,0
Lpz=200 [mm]	lo/lp=65.1 m/14.3 m

RZ 1 - 1. NP (11/5) (tp=45.0°C)	1.08 - Kúpeľňa č.1
PZ 1: Keramická podlaha	S=5.3 m2
Systém VARIONOVA	Rúrka RAUTHERM S 17x2,0
Lpz=100 [mm]	lo/lp=52.9 m/9.2 m

RZ 1 - 1. NP (11/7) (tp=45.0°C)	1.01 - Kuchyňa + Obývačka
PZ 1: Laminátová podlaha	S=10.1 m2
Systém VARIONOVA	Rúrka RAUTHERM S 17x2,0
Lpz=200 [mm]	lo/lp=50.3 m/20.6 m

RZ 1 - 1. NP (11/8) (tp=45.0°C)	1.01 - Kuchyňa + Obývačka
PZ 2: Laminátová podlaha	S=5.5 m2
Systém VARIONOVA	Rúrka RAUTHERM S 17x2,0
Lpz=100 [mm]	lo/lp=55.0 m/24.3 m

RZ 1 - 1. NP (11/9) (tp=45.0°C)	1.01 - Kuchyňa + Obývačka
PZ 2: Laminátová podlaha	S=5.2 m2
Systém VARIONOVA	Rúrka RAUTHERM S 17x2,0
Lpz=100 [mm]	lo/lp=52.0 m/22.3 m

Podlahové vykurovanie Rehau

Vykurovacia plocha: S=4.2 m²

Typ nášľapnej vrstvy (PX): Keramická dlažba

Typ vykurovacej rúrky: Rúrka Rautherm S 17×2,0

Rozdeľovač: Rozdeľovač Rehau HKV-D 11, skrinka rozdeľovača . 1. NP, napojenie 11 okruhov (tp=45 °C)

Systém uchytenia: Varionova – typ prichytenia potrubia pre podlahové kúrenie

LEGENDA POTRUBÍ:

— — —	Plasthliníkové potrubie napr. Rautherm S 17×2,0 Rehau pre podlahové vykurovanie, teplotný spád 45/35 °C, vedené v podlahe.
— — —	Plasthliníkové potrubie materiál: PE-Xa/AL/PE napr. Rautitan Stabil, zaizolované potrubie, teplotný spád 45/35 °C.
—·—·—	Medené potrubie primárneho okruhu tepelného čerpadla: Cu ϕ12×1, 6×1-iz.

LEGENDA ZARIADENÍ:

1A	Tepelné čerpadlo (vnútorná jednotka) napr.: Viessmann Vitocal 222-S (AWBT-M-E-AC 221.E06). Integrovaný zásobník na TV (190 l), napájanie 230V/50Hz. Hmotnosť: 188 kg.
1B	Tepelné čerpadlo (vonkajšia jednotka) napr.: Vitocal 222-S (vzduch-voda). Výkon (A7/W35): 2,6 – 7,5 kW, COP 4,95. Chladivo R32.
4	Ovládanie: Bezdrôtový diaľový ovládač napr. Vitotrol 300-E.
8	Expanzná nádoba napr: Viessmann N25 (objem 25 l, max. tlak 3 bar).
TP	Izbový regulátor napr.: REHAU Nea Smart 2.0 (meranie teploty).
TE	Snímač teploty exteriéru.
EL1	Elektrické vykurovacie teleso (rebrík) do kúpeľne, min. výkon 300 W (konkrétny model podľa výberu architekta).
R1	Lokálna rekuperačná jednotka napr.: korado korasmart tube 2400
R-Z	Zostava rozdeľovača podlahového vykurovania (teplotný spád 45/35 °C)

12-okruhový rozdeľovač napr. REHAU HKV-D 11, skrinka (rozmer 805 x 730 x 130 mm).
Ďiaľkové ovládanie termostatov napr. REHAU NEA (230V)

5 ks priestrový termostat napr. REHAU NEA (230V)

12 ks elektrický servo-pohon (230V)

POZNÁMKY :

- V prípade akýchkoľvek nejasností v projektovej dokumentácii je nutné kontaktovať zodpovedného projektanta.

- Všetky stavebné rozmery a prestupy je potrebné overiť priamo na mieste realizácie.

- Pred samotným spustením systému do prevádzky sa musí vykonať dôkladný preplach rozvodov a vyčistenie všetkých inštalovaných filtrov.

- Po napustení vykurovacej sústavy médiom je nevyhnutné zabezpečiť jej postupné odvzdušnenie.

- Zhotoviteľ je povinný postupovať v súlade s platnými normami STN EN a dodržiavať technologické aj bezpečnostné predpisy. Zároveň musí rešpektovať ustanovenia STN 730421 o rozmerových odchýlkach. Každú zmenu oproti projektu je nutné vopred skonzultovať s HIP.

- Otvory pre prestupy inžinierskych sietí a potrubných rozvodov v objekte je potrebné pripraviť počas realizácie hrubej stavby.

- Táto dokumentácia nenahrádza realizačnú dokumentáciu stavby!

-Výšková úroveň ±0,000 v projekte zodpovedá úrovni finálnej nášľapnej vrstvy podlahy.

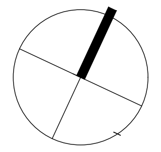

TABUĽKA REVÍZIÍ

ČÍSLO REVÍZIE	DÁTUM	POPIS ZMENY	VYPRACOVAL

0,000=+0,300 nad korunou komunikácie m n. m.

AUTOR PROJEKTU:	Ing. arch. Karol Kallay	GENERÁLNY PROJEKTANT: **Alla s.r.o.** Riazanská 70/683 831 02 Bratislava tel.: +421 907 693 679 email: ateliar@alla.sk
H.I.P.:	Ing. arch Ivor Mečiar, ArtD.	
ZODP. PROJEKTANT:	Ing. Lukáš Skalík, PhD.	
VYPRACOVAL:	Bc. Viktor Labovský	

INVESTOR:	Tomáš Valenta, Bottova 5, 811 09, Bratislava	PEČIATKA:	PARÉ:
NÁZOV PROJEKTU:	**RD V TVARE L**		
MIESTO STAVBY:	Chorvátsky Grob, p. č. 2301/28		ČÍSLO VÝKRESU:
OBSAH VÝKRESU:	**PÔDORYS 1.NP**		**01**
STAVEBNÝ OBJEKT:	SO 01 Rodinný dom v tvare L		

ID STAVBY:	STUPEŇ PD:	URČENIE STAVBY:	IDENTIFIK. KÓD:	ČLENENIE DOK.:	PROFESIE:	ČÍSLO VÝKRESU:	NÁZOV VÝKRESU:	REVÍZIA:
--	PSP	01	1111	S01	VYK	001	N01	00

NÁZOV VÝKRESU V ELEKTRONICKEJ PODOBE: -------_PSP_01_1111_S01_VYK_001_N01_00

DÁTUM:	03/2026	MIERKA:
FORMÁT:	6x A4	1 : 50
KÓD AKCIE:		