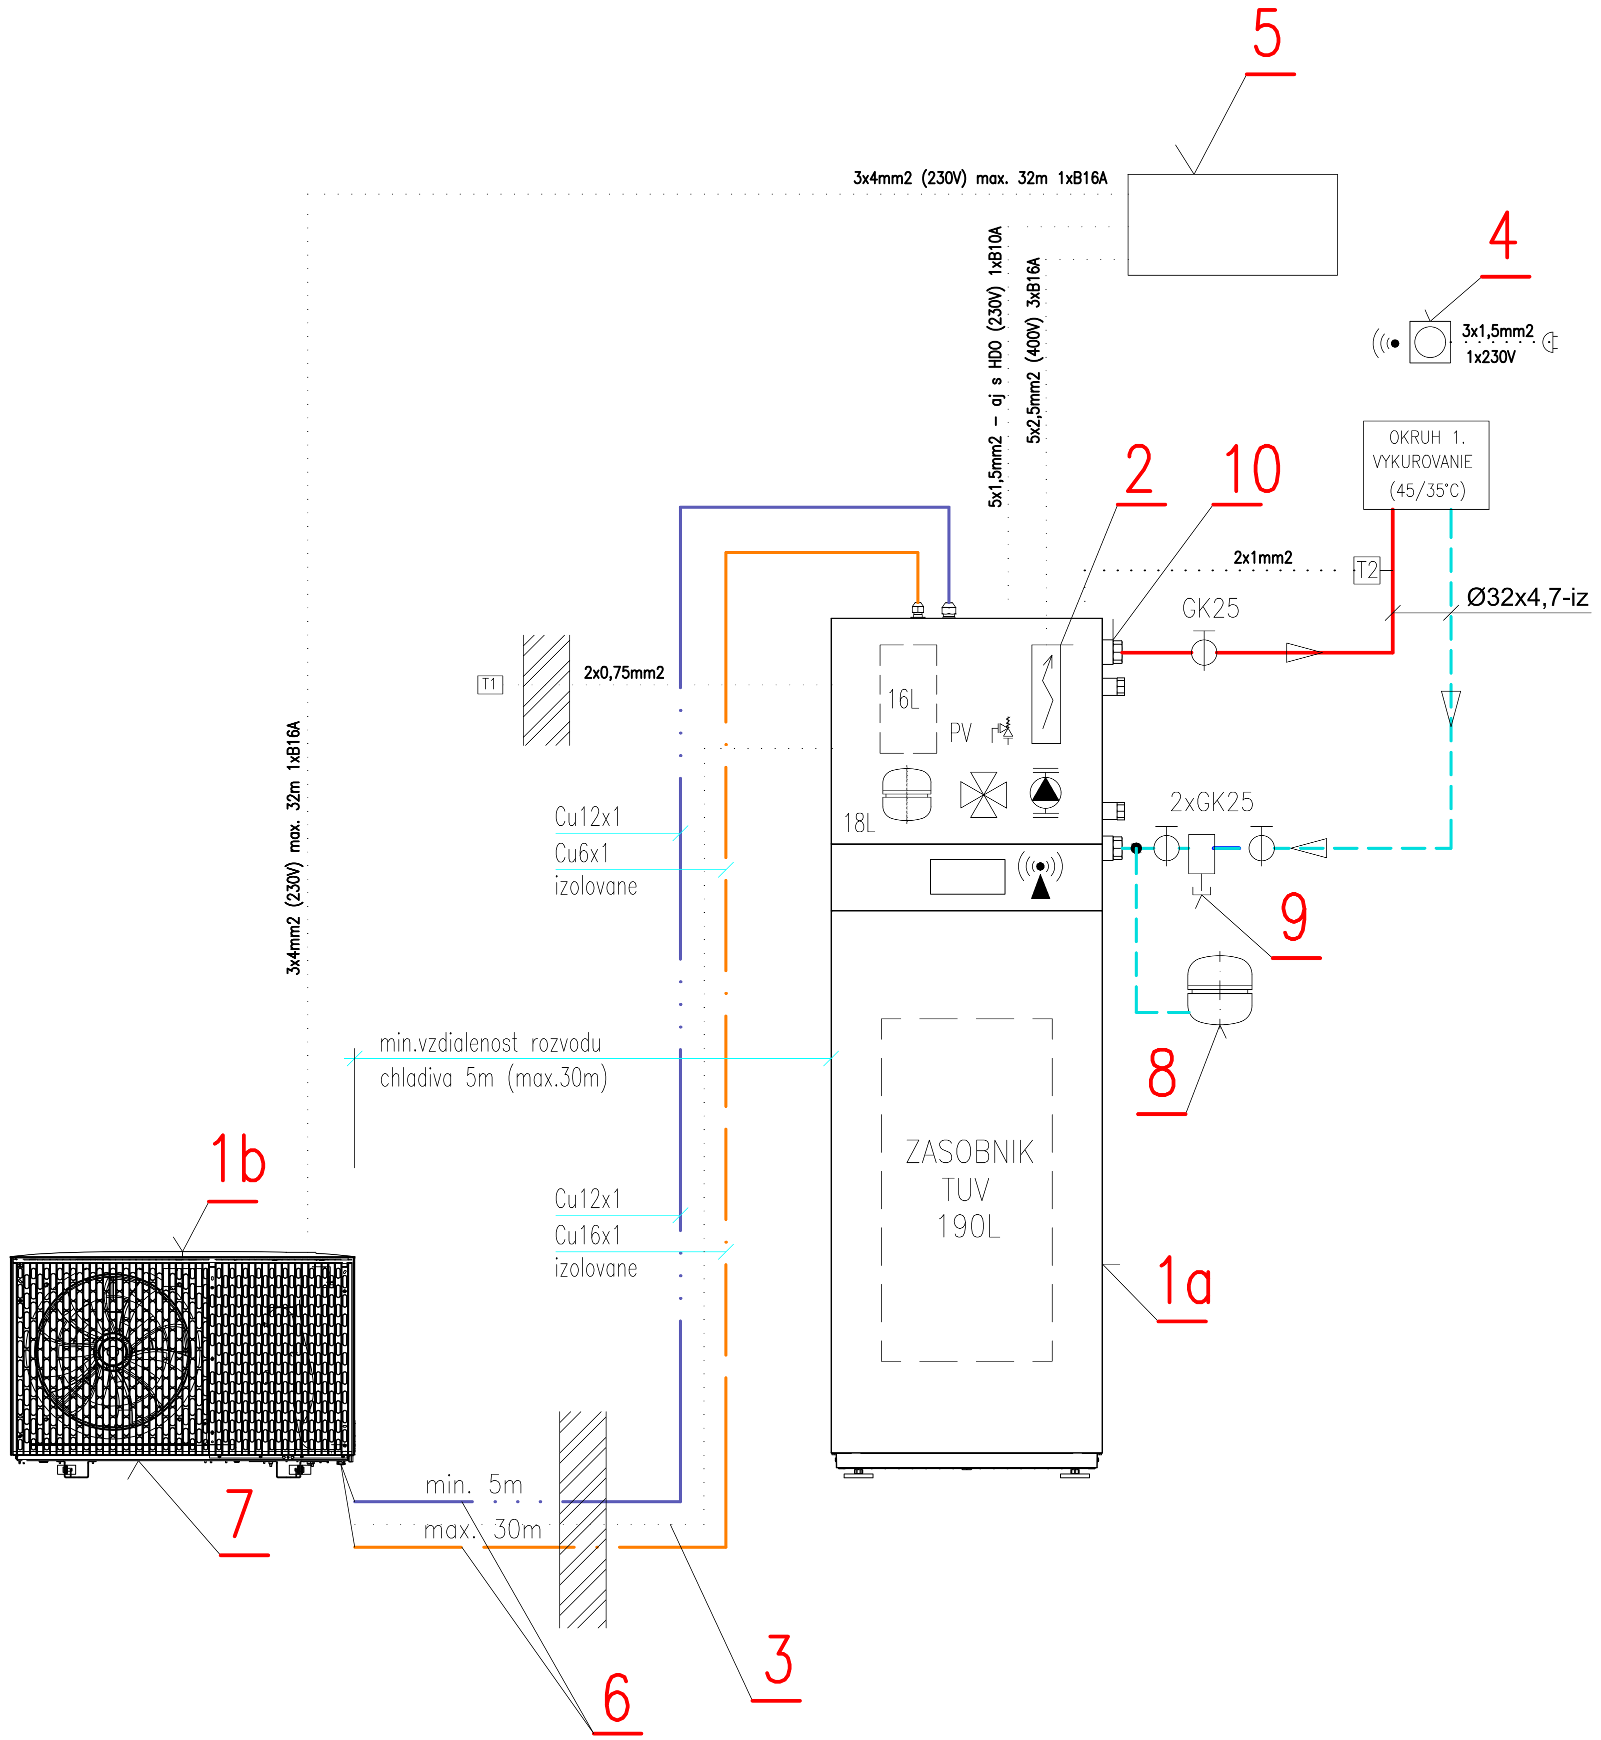

## LEGENDA ZARIADENÍ:

| POZ. | NÁZOV, ROZMER | P. KS |
|---|---|---|
| 1a | VNUT. JEDNOTKA napr. VITOCAL 222–S AWBT–M–E–AC 221.E06 | 1 |
| 1b | VON. JEDNOTKA napr. VITOCAL 222–S AWBT–M–E–AC 221.E06 (230V) | 1 |
|  | MAX.VÝSTUPNÁ TEPLOTA 60°C,TEPELNY VYKON 2,6–7,5kW A7/W35 |  |
|  | EKOLOGICKE CHLADIVO R32, REGULÁCIA ONE–BASE,WIFI (Z022720) |  |
| 2 | ELEKTRIC.PRIETOKOVY OHRIEVAC 8kW –v rozsahu dodavky pol.1a | 1 |
| 3 | CANBUS KOMUNIKACNY KABEL MEDZI JEDNOTKY 15m (ZK06217) | 1 |
| 4 | BEZDROTOVÉ DIALKOVE OVLADANIE VITOTROL 300–E (7959522) | 1 |
| 5 | ELEKTRICKY ROZVADZAC OBJEKTU | 1 |
| 6 | INSTALAC.SADA 12/6 NA ZEM+KONZOLA – 12,5M RURY (ZK06312) | 1 |
| 7 | ELEKTRIC.VYHREVNY PAS PRE VANU KONDENZATU 2,5m (ZK04098) | 1 |
| 8 | EXPANZNA NADOBA N25 OBJEM 25L, 3bar BIELA (7938081) | 1 |
|  | NASTENNY DRZIAK PRE N25 (9572216) | 1 |
| 9 | ODKALOVAC S MAGNETOM A IZOLACIOU VITOTRAP 28mm (ZK04654) | 1 |
| 10 | PRIPOJOVACIA SADA NA OMIETKU–SPRAVA (ZK06403)–treba upresnit | 1 |
|  |  |  |
|  |  |  |
| T1 | SNIMAC VONKAJSEJ TEPLOTY – v rozsahu dodavky tep.cerpadla | 1 |
| T2 | SNIMAC ROSNEHO BODU – VLHKOSTI (7181418) | 1 |
|  |  |  |

## LEGENDA POTRUBÍ:

Plasthliníkové potrubie materiál: PE-Xa/AL/PE napr. Rautitan Stabil, zaizolované potrubie, teplotný spád 45/35 °C.

Medené potrubie primárneho okruhu tepelného čerpadla: Cu ϕ12×1, 6×1-iz.

## LEGENDA ARMATÚR :

| | |
|---|---|
| GK | Guľový kohút so závitom |
| AOV | Automatický odvzdušňovací ventil s uzatváracou armatúrou |
| PV | Poistný ventil so závitom |

## POZNÁMKY :

- V prípade akýchkoľvek nejasností v projektovej dokumentácii je nutné kontaktovať zodpovedného projektanta.

- Všetky stavebné rozmery a prestupy je potrebné overiť priamo na mieste realizácie.

- Pred samotným spustením systému do prevádzky sa musí vykonať dôkladný preplach rozvodov a vyčistenie všetkých inštalovaných filtrov.

- Po napustení vykurovacej sústavy médiom je nevyhnutné zabezpečiť jej postupné odvzdušnenie.

- Zhotoviteľ je povinný postupovať v súlade s platnými normami STN EN a dodržiavať technologické aj bezpečnostné predpisy. Zároveň musí rešpektovať ustanovenia STN 730421 o rozmerových odchýlkach. Každú zmenu oproti projektu je nutné vopred skonzultovať s HIP.

- Otvory pre prestupy inžinierskych sietí a potrubných rozvodov v objekte je potrebné pripraviť počas realizácie hrubej stavby.

- Táto dokumentácia nenahrádza realizačnú dokumentáciu stavby!

-Výšková úroveň ±0,000 v projekte zodpovedá úrovni finálnej nášľapnej vrstvy podlahy.

0,000=+0,300 nad korunou komunikácie m n. m.

| | | |
|---|---|---|
| AUTOR PROJEKTU: | Ing. arch. Karol Kallay | GENERÁLNY PROJEKTANT:<br>**Alla s.r.o.**<br>Riazanská 70/683<br>831 02 Bratislava<br>tel.: +421 907 693 679<br>email: ateliar@alla.sk |
| H.I.P.: | Ing. arch Ivor Mečiar, ArtD. | |
| ZODP. PROJEKTANT: | Ing. Lukáš Skalík, PhD. | |
| VYPRACOVAL: | Bc. Viktor Labovský | |

| | | | |
|---|---|---|---|
| INVESTOR: | Tomáš Valenta, Bottova 5, 811 09, Bratislava | PEČIATKA: | PARÉ: |
| NÁZOV PROJEKTU: | **RD V TVARE L** | | |
| MIESTO STAVBY: | Chorvátsky Grob, p. č. 2301/28 | | ČÍSLO VÝKRESU:<br>**02** |
| OBSAH VÝKRESU: | **SCHÉMA ZAPOJENIA** | | |
| STAVEBNÝ OBJEKT: | SO 01 Rodinný dom v tvare L | | |

| ID STAVBY: | STUPEŇ PD: | URČENIE STAVBY: | IDENTIFIK. KÓD: | ČLENENIE DOK.: | PROFESIE: | ČÍSLO VÝKRESU: | NÁZOV VÝKRESU: | REVÍZIA: |
|---|---|---|---|---|---|---|---|---|
| -- | PSP | 01 | 1111 | S01 | VYK | 02 | SCH | 00 |

NÁZOV VÝKRESU V ELEKTRONICKEJ PODOBE: -------_PSP_01_1111_S01_VYK_002_SCH_00

| | | |
|---|---|---|
| DÁTUM: | 03/2026 | MIERKA:<br>1 : 50 |
| FORMÁT: | 3x A4 | |
| KÓD AKCIE: | | |