- 1.02 -
FANCOLOVÁ PARAPETNÁ
VSTAVANÁ JEDNOTKA FWL02DTN
VÝKON - Qchl=1600 W, Qvyk=1000 W
TEPLOTNÝ SPÁD - chl: 7/12°C, vyk: 45/40°C
PRIETOK - 173.9 l/h
- 1.02 -
FANCOLOVÁ PARAPETNÁ
VSTAVANÁ JEDNOTKA FWL02DTN
VÝKON - Qchl=1600 W, Qvyk=1000 W
TEPLOTNÝ SPÁD - chl: 7/12°C, vyk: 45/40°C
PRIETOK - 173.9 l/h
- 1.02 -
FANCOLOVÁ PARAPETNÁ
VSTAVANÁ JEDNOTKA FWL02DTN
VÝKON - Qchl=1660 W, Qvyk=1000 W
TEPLOTNÝ SPÁD - chl: 7/12°C, vyk: 45/40°C
PRIETOK - 173.9 l/h
- 1.14 -
FANCOLOVÁ PARAPETNÁ
VSTAVANÁ JEDNOTKA FWL04DTN
VÝKON - Qchl=2700 W, Qvyk=1778 W
TEPLOTNÝ SPÁD - chl: 7/12°C, vyk: 45/40°C
PRIETOK - 309.3 l/h
POTRUBIE ULOŽENÉ POD STROPOM
ext. žalúzia
DN125-iz
TČ1
1
2
3
4
5
6
8
9
A
B
C
D
E
F
G
H
J
L
M
N
O

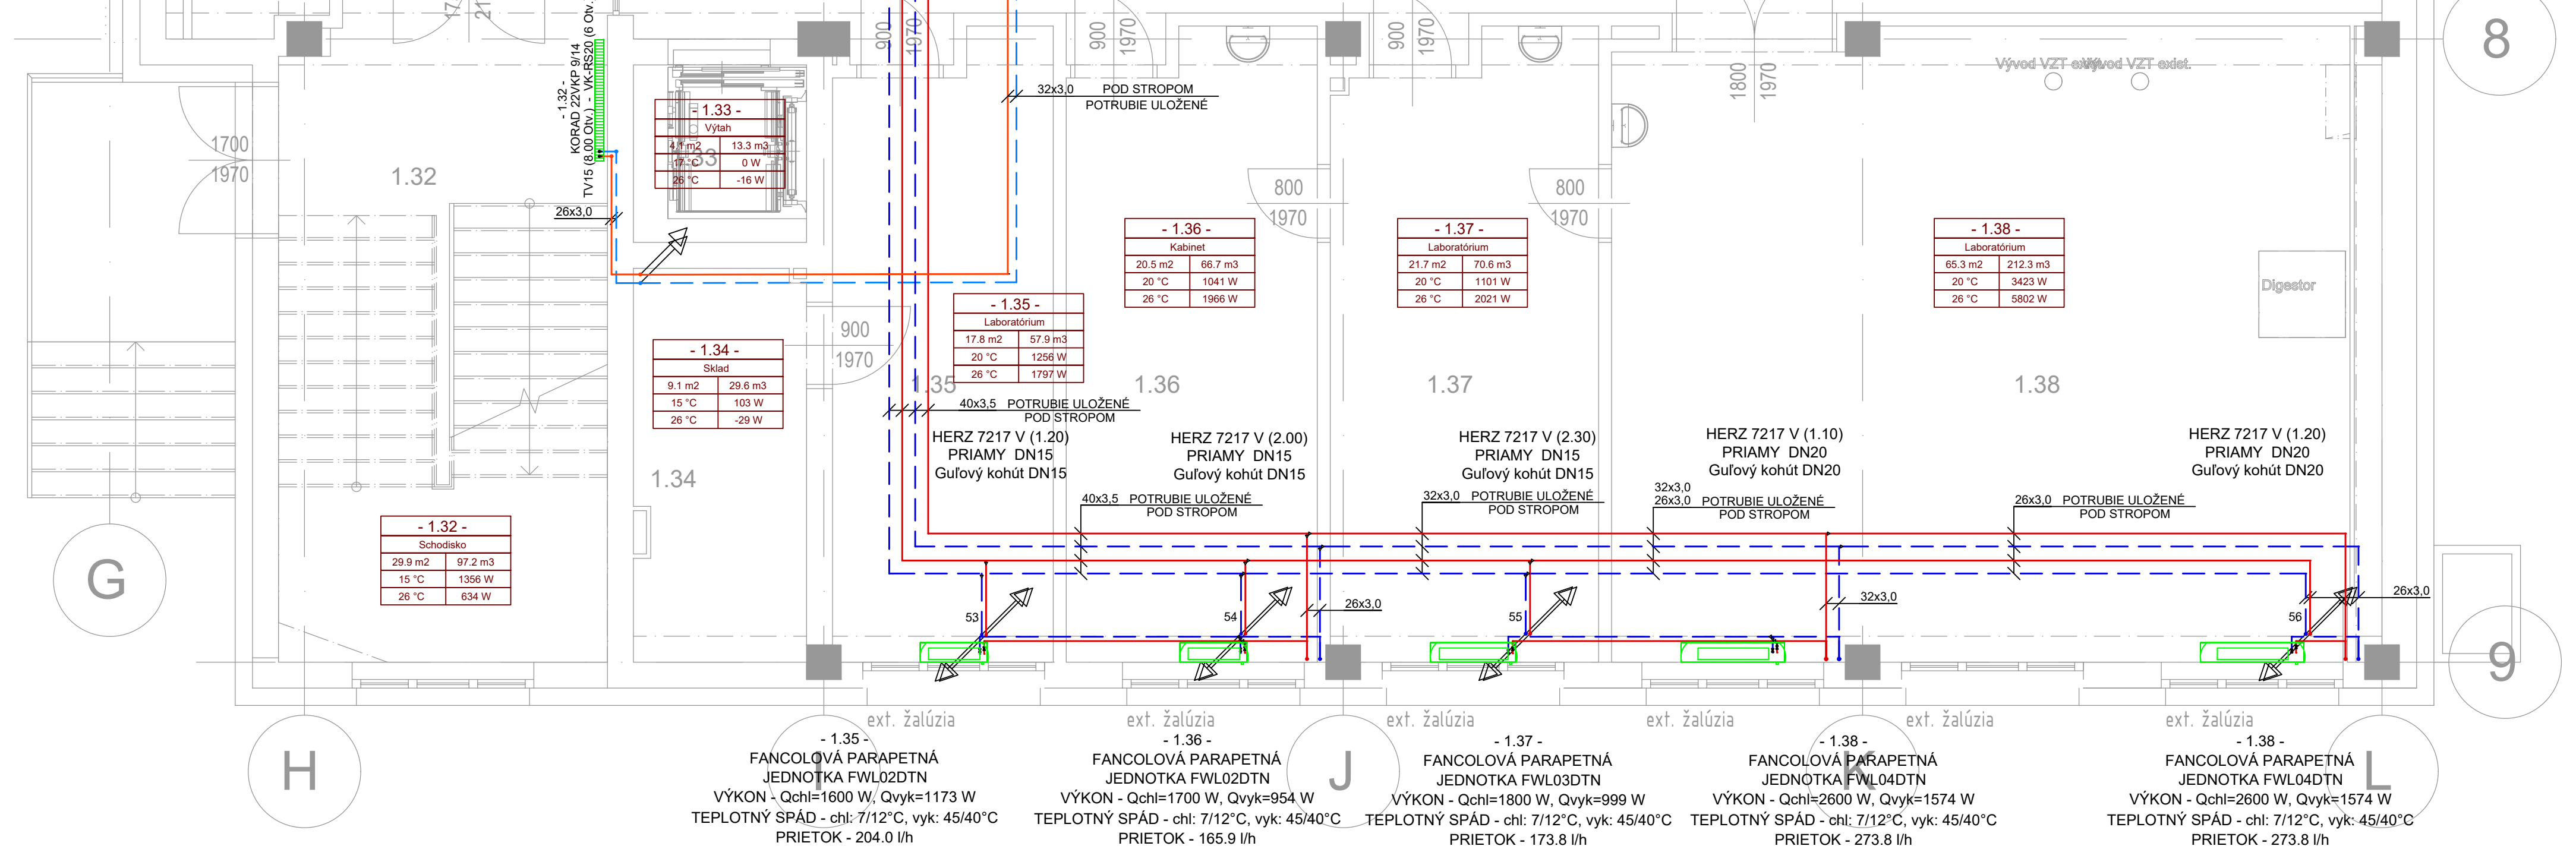

DOSKOVÉ VYKUROVACIE TELESO

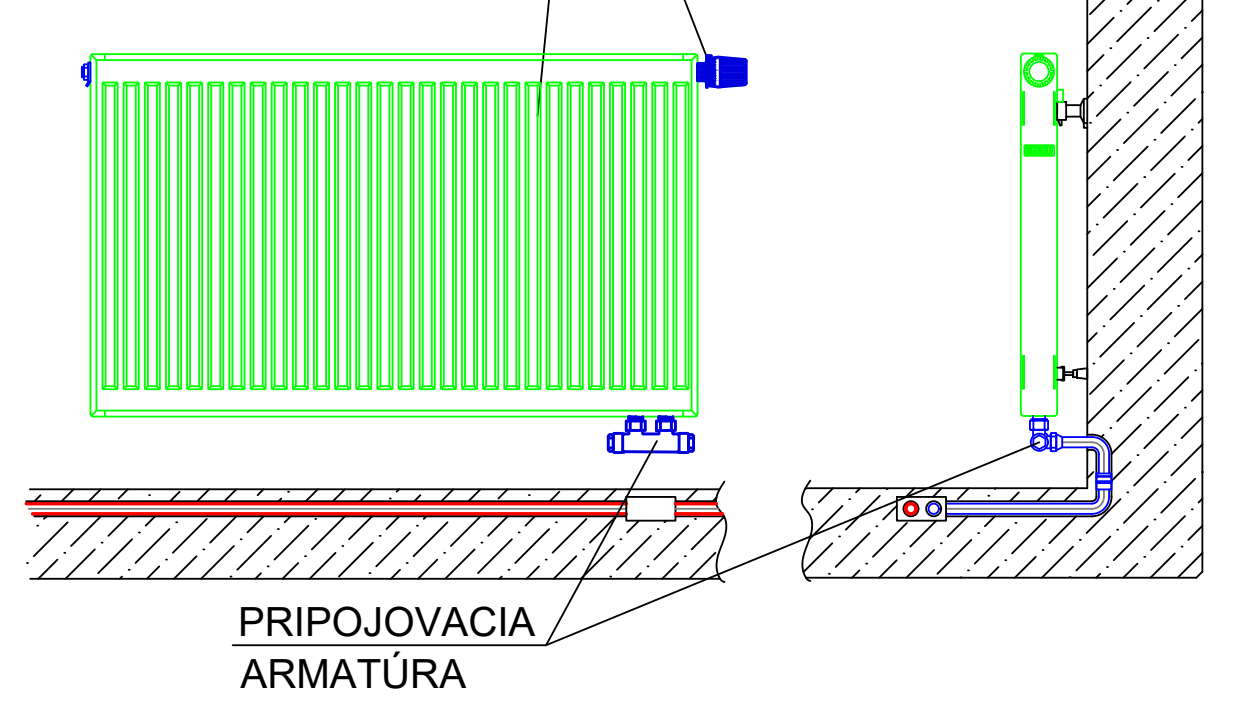

Č.M.	Názov	Plocha
1.01	Vstupná hala	55.20 m^2
1.02	Bufet + kaviareň	64.16 m^2
1.04	Výťah	3.47 m^2
1.05	Recepcia	9.71 m^2
1.06	Zázemie - recepcia	4.72 m^2
1.07	Chodba	60.04 m^2
1.08	Schodisko	21.20 m^2
1.09	Chodba	15.79 m^2
1.10	Bezbarier. záchodová kabína	3.56 m^2
1.11	WC ženy	13.56 m^2
1.12	WC muži	11.20 m^2
1.13	Sklad pre učebňu 3D	4.50 m^2
1.14	Učebňa 3D modelovania	67.70 m^2
1.15	Kabinet	22.56 m^2
1.16	Kabinet	23.80 m^2
1.17	Učebňa	54.25 m^2
1.18	Učebňa	59.15 m^2
1.19	Kabinet	24.07 m^2
1.20	Učebňa	54.86 m^2
1.21	Spojovacia chodba	203.54 m^2
1.22	Zádverie	17.48 m^2
1.23	Vrátnica	9.77 m^2
1.24	Sklad	9.72 m^2
1.25	Laboratórium	42.20 m^2
1.26	Laboratórium	65.08 m^2
1.27a	Strojovňa tepelného čerp.	35.33 m^2
1.27b	Sklad	38.53 m^2
1.28	Bezbarier. záchodová kabína	3.16 m^2
1.29	WC ženy	9.86 m^2
1.30	WC muži	10.63 m^2
1.31	Rozvodňa NN	5.39 m^2
1.32	Schodisko	29.95 m^2
1.33	Výťah	4.10 m^2
1.34	Sklad	8.95 m^2
1.35	Laboratórium	17.79 m^2
1.36	Kabinet	20.54 m^2
1.37	Laboratórium	21.62 m^2
1.38	Laboratórium	61.60 m^2
1.39	Chodba	20.33 m^2
1.40	Schodisko	18.80 m^2
1.41	Chodba	13.62 m^2
1.42	Dielňa	62.02 m^2
1.43	Garáž	32.06 m^2
1.44	Spojovacia chodba	25.04 m^2
1.45	Sklad	14.71 m^2
1.46	Sklad	20.24 m^2
1.47	Sklad	12.92 m^2
1.48	Sklad	23.84 m^2
1.49	Upratovačka	5.65 m^2
1.50	Miestnosť CBS	4.89 m^2
		1442.82 m^2

L.M. 1.NP - fakulta

LEGENDA OSADENIA REGULÁCIE NA PÄTE STÚPAČKY:

GK - Guľový kohút
VK - Vypúšťací kohút DN15
RTD - Regulátor tlakovej diferencie
PTV - Partnerský vyvažovací ventil Herz Stromax GM 2013 - závit Rp

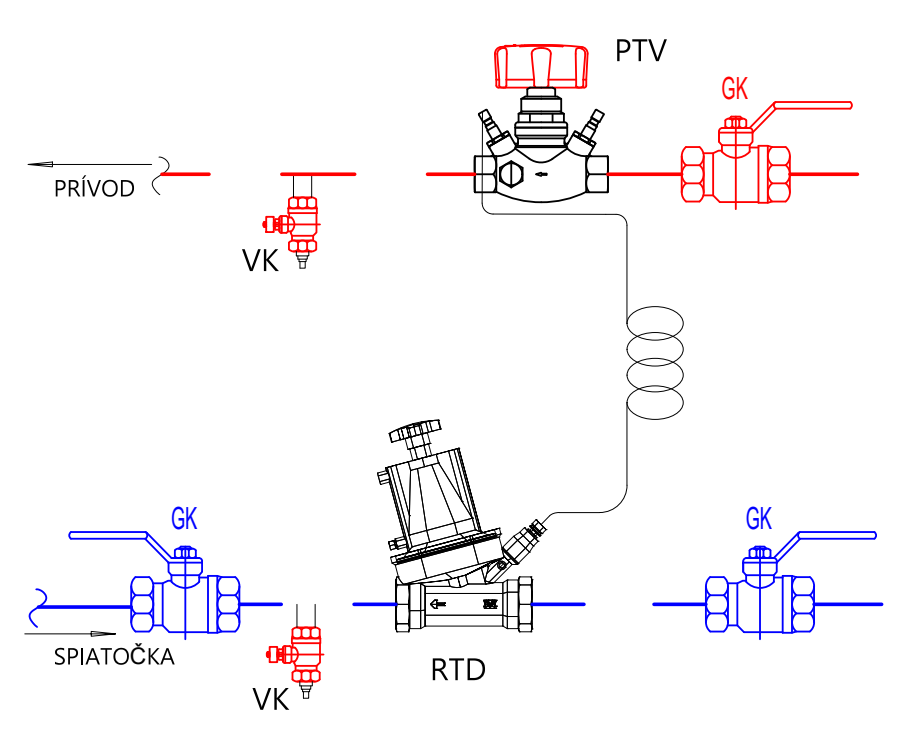

DETAIL NAPOJENIA KAZETOVÉHO FANCOILU:

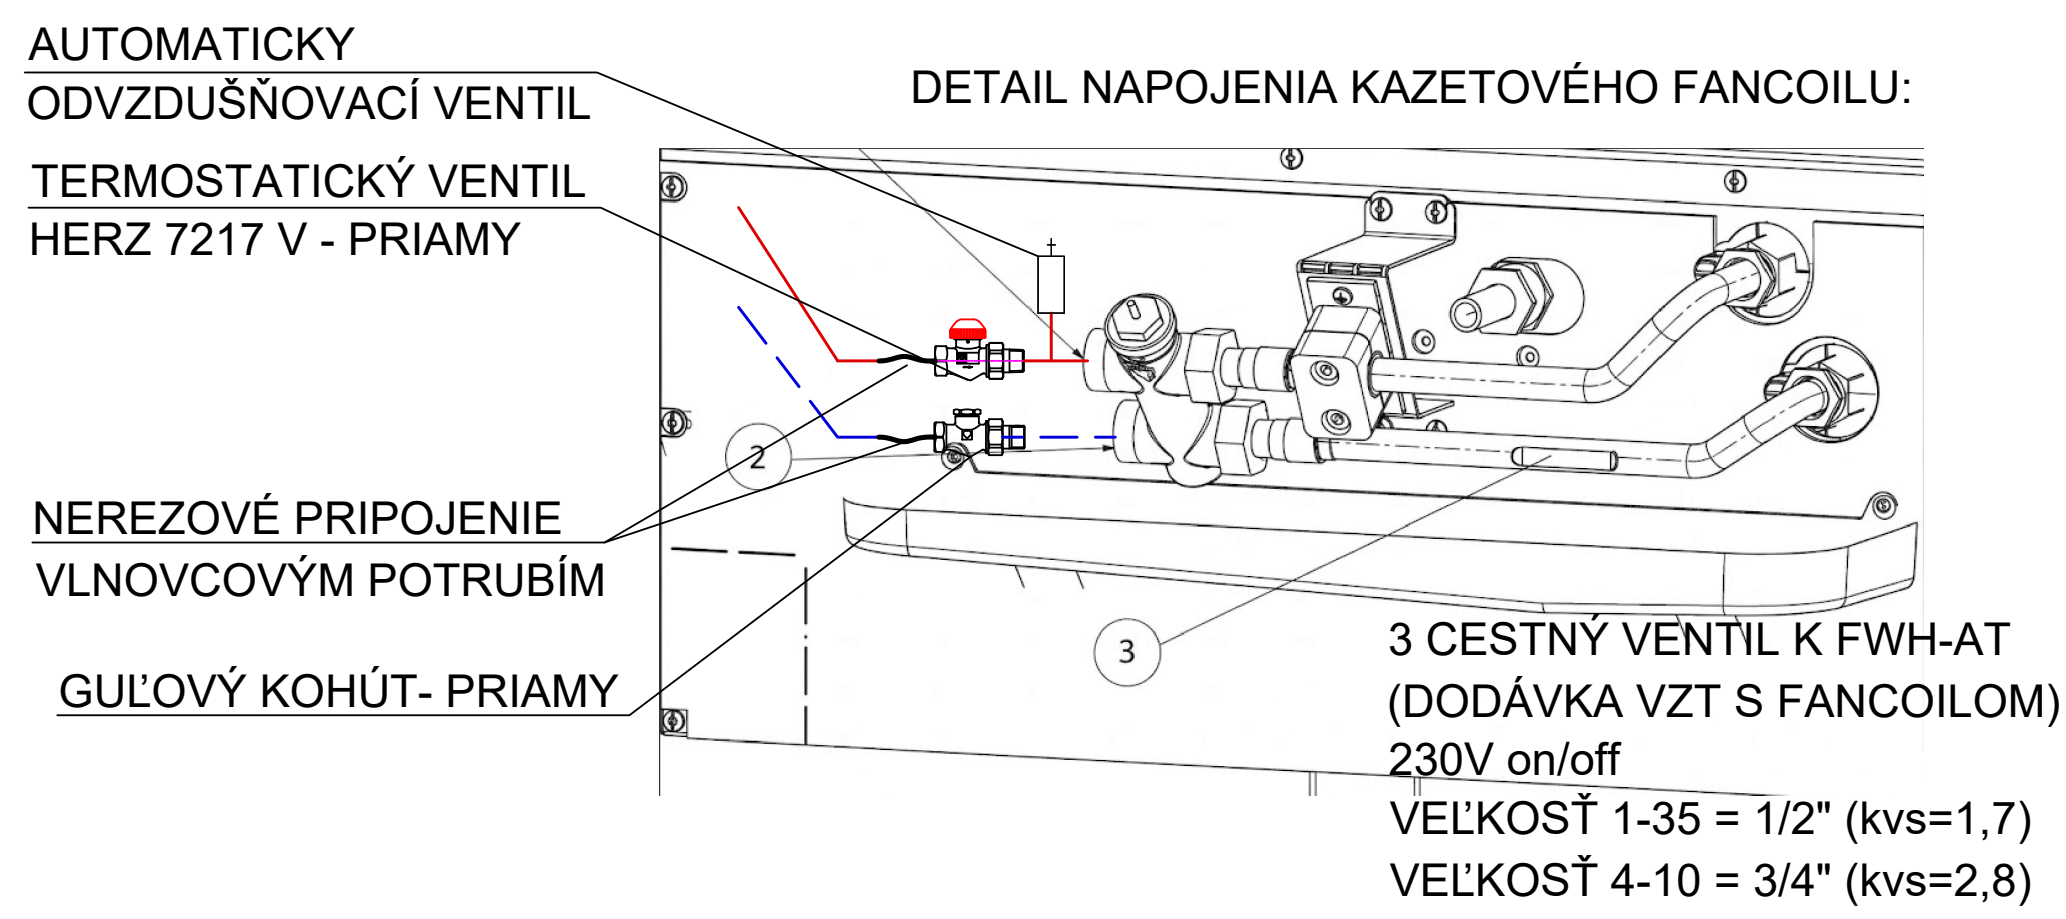
AUTOMATICKY ODVZDUŠŇOVACÍ VENTIL
TERMOSTATICKÝ VENTIL HERZ 7217 V - PRIAMY
NEREZOVÉ PRIPOJENIE VLNOVCOVÝM POTRUBÍM
GUĽOVÝ KOHÚT- PRIAMY
2
3

3 CESTNÝ VENTIL K FWH-AT
(DODÁVKA VZT S FANCOILOM)
230V on/off
VEĽKOSŤ 1-35 = 1/2" (kvs=1,7)
VEĽKOSŤ 4-10 = 3/4" (kvs=2,8)

DETAIL NAPOJENIA KANÁLOVÉHO FANCOILU:

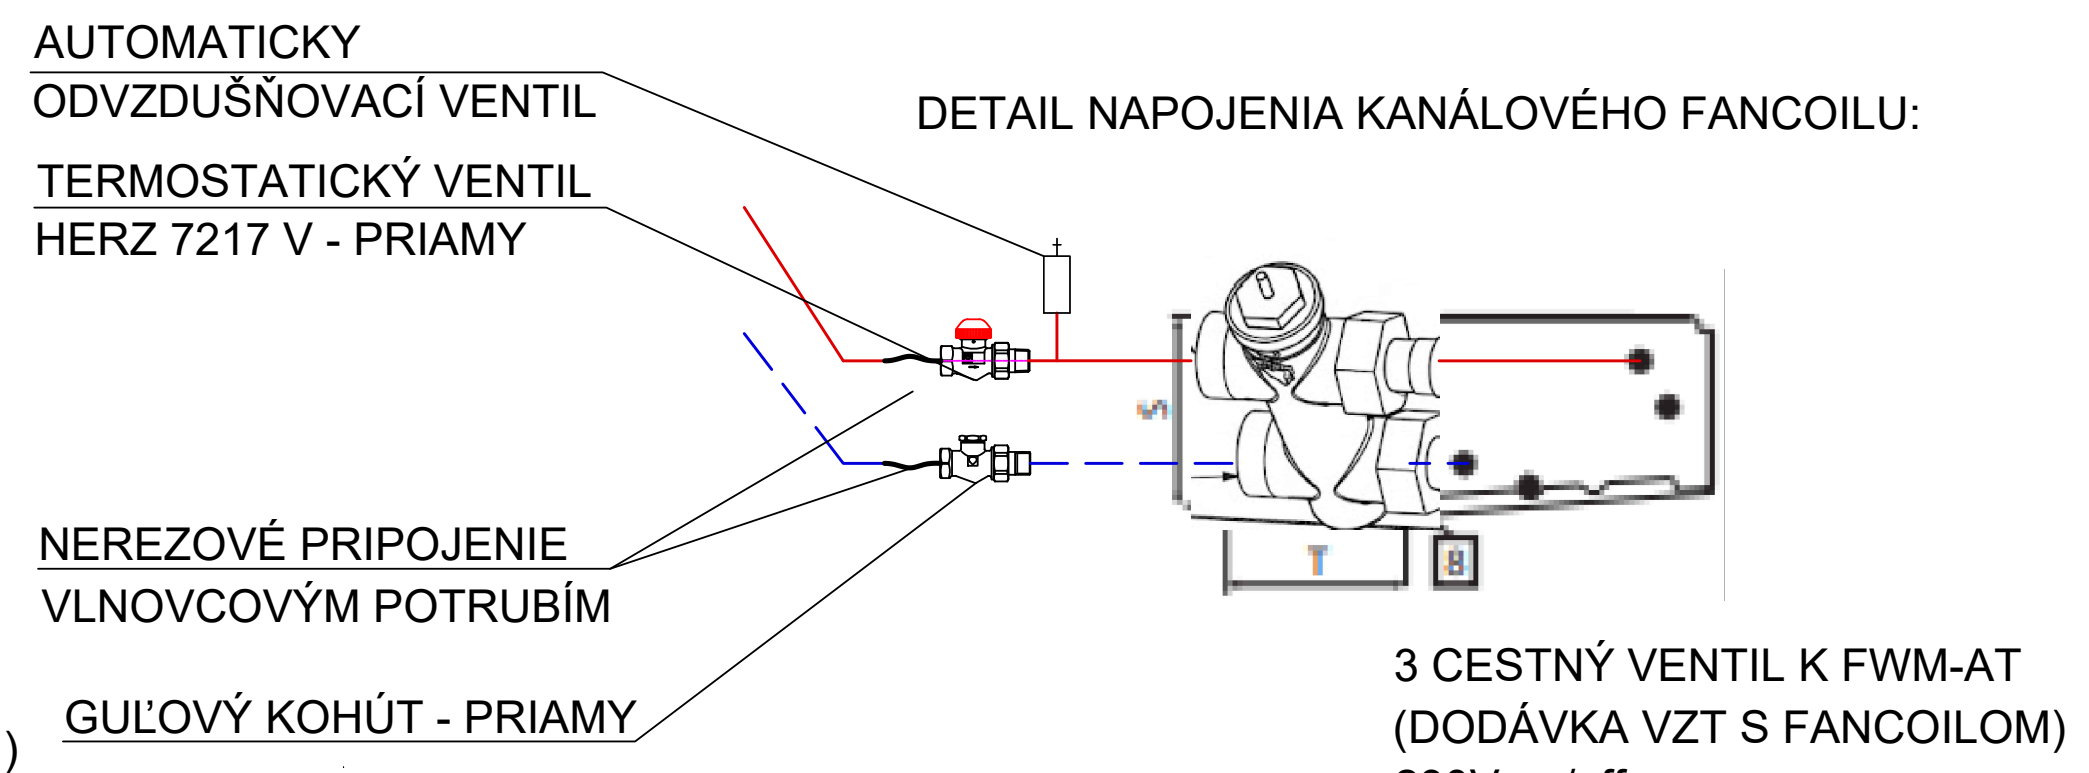
AUTOMATICKY ODVZDUŠŇOVACÍ VENTIL
TERMOSTATICKÝ VENTIL HERZ 7217 V - PRIAMY
NEREZOVÉ PRIPOJENIE VLNOVCOVÝM POTRUBÍM
GUĽOVÝ KOHÚT - PRIAMY

3 CESTNÝ VENTIL K FWM-AT
(DODÁVKA VZT S FANCOILOM)
230V on/off
VEĽKOSŤ 1-35 = 1/2" (kvs=1,7)
VEĽKOSŤ 4-10 = 3/4" (kvs=2,8)

DETAIL NAPOJENIA PARAPETNÉHO FANCOILU:

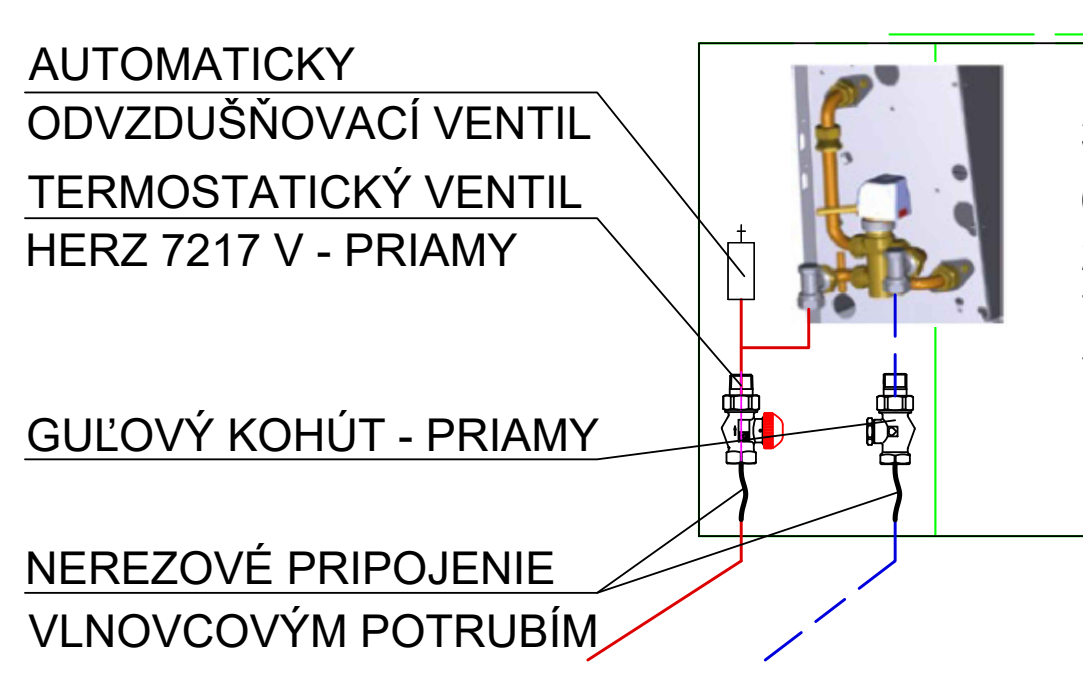
AUTOMATICKY ODVZDUŠŇOVACÍ VENTIL
TERMOSTATICKÝ VENTIL HERZ 7217 V - PRIAMY
GUĽOVÝ KOHÚT - PRIAMY
NEREZOVÉ PRIPOJENIE VLNOVCOVÝM POTRUBÍM

3 CESTNÝ VENTIL K FWL-DTV
(DODÁVKA VZT S FANCOILOM)
230V on/off
VEĽKOSŤ 1-35 = 1/2" (kvs=1,7)
VEĽKOSŤ 4-10 = 3/4" (kvs=2,8)

LEGENDA:

— —	VYKUROVACIE POTRUBIE - NÍZKOUHLÍKOVÉ OCELOVÉ POTRUBIE TEPLOTNÝ SPÁD 60/50 °C HLAVNÝ ROZVOD Z TEPELNÉHO ČERPADLA
— —	VYKUROVACIE POTRUBIE - NÍZKOUHLÍKOVÉ OCELOVÉ POTRUBIE TEPLOTNÝ SPÁD 60/50 °C HLAVNÝ ROZVOD Z AKUMULAČNEJ NÁDRŽE
— —	VYKUROVACIE POTRUBIE - PLASTOHLÍKOVÉ/NÍZKOUHLÍKOVÉ OCELOVÉ POTRUBIE TEPLOTNÝ SPÁD 45/40 °C PRE NAPOJENIE RADIATOROV
— —	VYKUROVACIE POTRUBIE - PLASTOHLÍKOVÉ POTRUBIE/NÍZKOUHLÍKOVÉ OCELOVÉ POTRUBIE TEPLOTNÝ SPÁD 45/40 °C
—	EXPANZNÉ POTRUBIE
▨	DOSKOVÉ VYKUROVACIE TELESO
↗	STÚPANIE/KLESANIE POTRUBIA
▭	PARAPETNÁ FANCOIL JEDNOTKA
▭	KANÁLOVÁ VZDUCHOVÁ JEDNOTKA
▢	KAZETOVÁ STROPNÁ FANCOIL JEDNOTKA

LEGENDA VYKUROVACÍCH OKRUHOV:

UK1 - Prevádzka kancelárie 4.NP Fancoil
UK2 - Prevádzka Aula Fancoil
UK3 - Prevádzka škola Sever Fancoil
UK4 - Prevádzka škola Juh Fancoil
UK5 - Prevádzka škola Radiatory

LEGENDA POPISOVÝCH TABULIEK:

- 1.12 -	
Chodba	
19.8 m2	55.2 m3
15 °C	2054 W

ČÍSLO MIESTNOSTI
ÚČEL MIESTNOSTI
OBJEM MIESTNOSTI
PLOCHA MIESTNOSTI
VÝPOČTOVÁ TEPLOTA
TEPELNÁ STRATA

SADA ČÍSLO

±0,000 = ÚROVEŇ PODLAHY 1.NP

Objednávateľ: Trenčiansky samosprávny kraj, K dolnej stanici 7282/20A, 911 01 Trenčín,
Trenčianska univerzita Alexandra Dubčeka v Trenčíne, Študentská 2, 911 50 Trenčín
Generálny projektant: Arch Konstrukt s.r.o., J. Braneckého 179/14, 911 01 Trenčín
Kontroloval: Ing. Ján Bátor
Vypracoval: Ing. J. Bátor, Ing. V. Labovský
Kraj: Trenčiansky
Okres: Púchov
Obec: Púchov
Investor: Trenčiansky samosprávny kraj, K dolnej stanici 7282/20A, 911 01 Trenčín,
Trenčianska univerzita Alexandra Dubčeka v Trenčíne, Študentská 2, 911 50 Trenčín
Miesto stavby: k.ú Horné Kočkovce, p.č.1509/1, 1510/1, 1527, 1528, 1529/1, 1529/2, 1530/1, 1533, 1535, 1548/2, 1548/4, 1548/5, 1548/6,
Stupeň PD: DOKUMENTÁCIA PRE STAVEBNÉ POVOLENIE
Akcia:
EDU-TECH KAMPUS PÚCHOV
Objekt: SO 201 FPT TnUAD
Obsah: Pôdorys 1.NP

ARCH KONSTRUKT
J. Braneckého 179/14, 911 01 Trenčín
tel. 0907/146 508
www.archkonstrukt.sk
email: filina@archkonstrukt.sk

Dátum: 7/2026
Stupeň: DSP
Vykurovanie
Formát: 30xA4
Mierka: 1 : 50
Výkres: 01