1
2
3
4
5
6
7
8
9
A
B
C
D
E
F
G
H
I
J
K
L
M
N
O
FANCOLOVÁ PARAPETNÁ JEDNOTKA VSTAVANÁ
HERZ 7217 V - PRIAMY
Guľový kohút DN15
Guľový kohút DN20
POTRUBIE ULOŽENÉ POD STROPOM
POTRUBIE ULOŽENÉ V PODLAHE
PRÍSTUP K VENTILOM CEZ REVÍZNE VRÁTKA
FANCOLOVÁ KANÁLOVÁ JEDNOTKA
FANCOLOVÁ PODSTROPNÁ JEDNOTKA
TČ1 DN125-iz
ext. žalúzia
tieniaca roleta
Digestorium
Vývod VZT sobt.

DOSKOVÉ VYKUROVACIE TELESO

L.M. 2.NP - PBS

Č.M.	Názov	Plocha
2.01	Vstupná hala	73.09
2.02	Výťah	3.47
2.03	Študijné oddelenie	24.71
2.04	Archív	13.65
2.05	Chodba	61.99
2.06	Bezbarier. záchodová kabína	3.90
2.07	WC muži	12.01
2.08	WC ženy	14.67
2.09	WC personál	4.24
2.10	Seminárna miestnosť	67.43
2.11	Kabinet	24.00
2.12	Kabinet	25.03
2.13	Laboratórium	57.30
2.14	Schodisko	21.49
2.15	Laboratórium	14.07
2.16	Laboratórium	34.61
2.17	Laboratórium	22.72
2.18	Kabinet	23.45
2.19	Učebňa	56.09
2.20	Spojovacia chodba	199.76
2.21	Laboratórium - PC učebňa	40.89
2.22	Kabinet	19.28
2.23	Kabinet	21.43
2.24	Laboratórium	83.39
2.25	Sklad chemických látok	25.59
2.26	Sklad nebezpečného odpadu	26.81
2.27	Váhovňa	22.44
2.28	Bezbarier. záchodová kabína	3.30
2.29	WC ženy	10.04
2.30	WC muži	10.46
2.31	Upratovačka	4.80
2.32	Schodisko	30.04
2.33	Výťah	4.10
2.34	Sklad	8.86
2.35	Laboratórium	18.06
2.36	Laboratórium	19.43
2.37	Laboratórium	86.71
2.38	Schodisko	18.76
2.39	Schodisko	16.39
2.40	Sklad	3.38
2.41	Aula	186.87
2.42	Šatňa	8.96
2.43	Catering	8.31

LEGENDA:

🟪	VYKUROVACIE POTRUBIE - NÍZKOUHLÍKOVÉ OCELOVÉ POTRUBIE TEPLOTNÝ SPÁD 60/50 °C HLAVNÝ ROZVOD Z TEPELNÉHO ČERPADLA
🟩	VYKUROVACIE POTRUBIE - NÍZKOUHLÍKOVÉ OCELOVÉ POTRUBIE TEPLOTNÝ SPÁD 60/50 °C HLAVNÝ ROZVOD Z AKUMULAČNEJ NÁDRŽE
🟥	VYKUROVACIE POTRUBIE - PLASTOHLÍKOVÉ/NÍZKOUHLÍKOVÉ OCELOVÉ POTRUBIE TEPLOTNÝ SPÁD 45/40 °C PRE NAPOJENIE RADIATOROV
🟥	VYKUROVACIE POTRUBIE - PLASTOHLÍKOVÉ POTRUBIE/NÍZKOUHLÍKOVÉ OCELOVÉ POTRUBIE TEPLOTNÝ SPÁD 45/40 °C
🟦	EXPANZNÉ POTRUBIE
▥	DOSKOVÉ VYKUROVACIE TELESO
↗	STÚPANIE/KLESANIE POTRUBIA
▭	PARAPETNÁ FANCOIL JEDNOTKA
▭	KANÁLOVÁ VZDUCHOVÁ JEDNOTKA
▣	KAZETOVÁ STROPNÁ FANCOIL JEDNOTKA

LEGENDA VYKUROVACÍCH OKRUHOV:

UK1 - Prevádzka kancelárie 4.NP Fancoil
UK2 - Prevádzka Aula Fancoil
UK3 - Prevádzka škola Sever Fancoil
UK4 - Prevádzka škola Juh Fancoil
UK5 - Prevádzka škola Radiatory

LEGENDA POPISOVÝCH TABULIEK:

ČÍSLO MIESTNOSTI	- 1.12 -
ÚČEL MIESTNOSTI	Chodba
PLOCHA MIESTNOSTI	19.8 m2
OBJEM MIESTNOSTI	55.2 m3
VÝPOČTOVÁ TEPLOTA	15 °C
TEPELNÁ STRATA	2054 W

DETAIL NAPOJENIA KAZETOVÉHO FANCOILU:

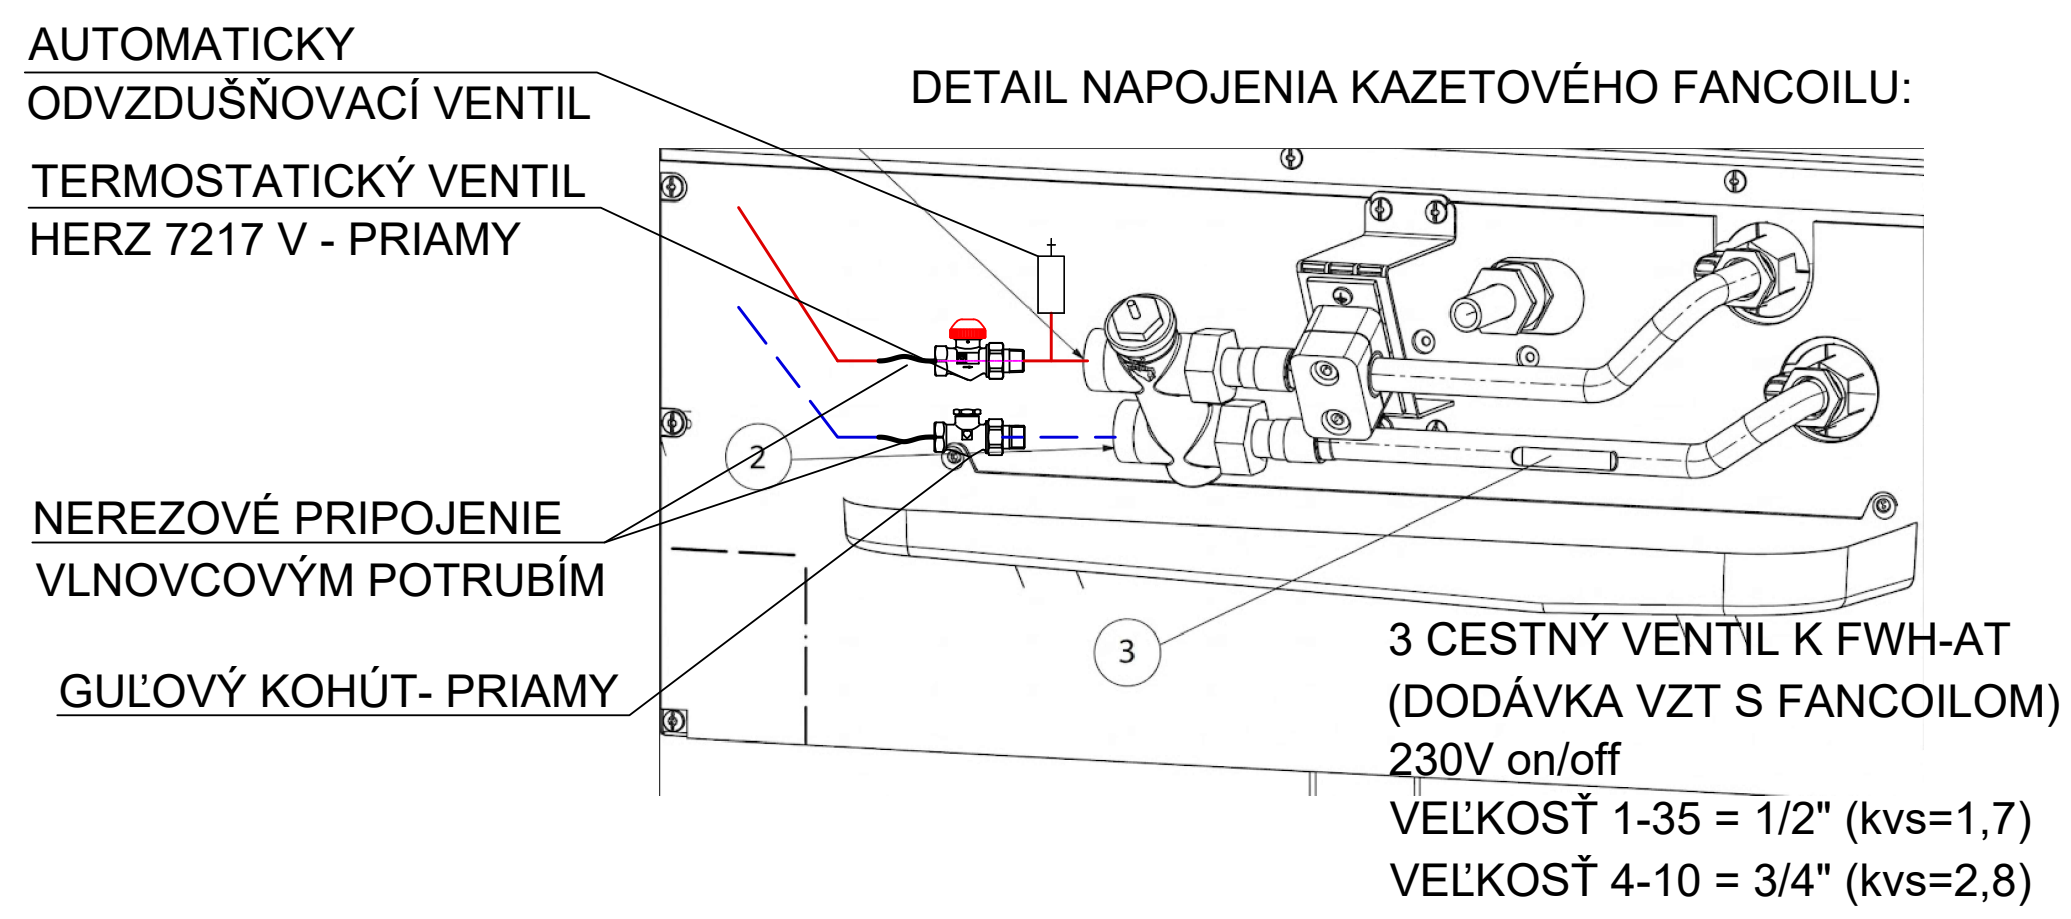
AUTOMATICKY ODVZDUŠŇOVACÍ VENTIL
TERMOSTATICKÝ VENTIL HERZ 7217 V - PRIAMY
NEREZOVÉ PRIPOJENIE VLNOVCOVÝM POTRUBÍM
GUĽOVÝ KOHÚT- PRIAMY
2
3

3 CESTNÝ VENTIL K FWH-AT
(DODÁVKA VZT S FANCOILOM)
230V on/off
VEĽKOSŤ 1-35 = 1/2" (kvs=1,7)
VEĽKOSŤ 4-10 = 3/4" (kvs=2,8)

DETAIL NAPOJENIA KANÁLOVÉHO FANCOILU:

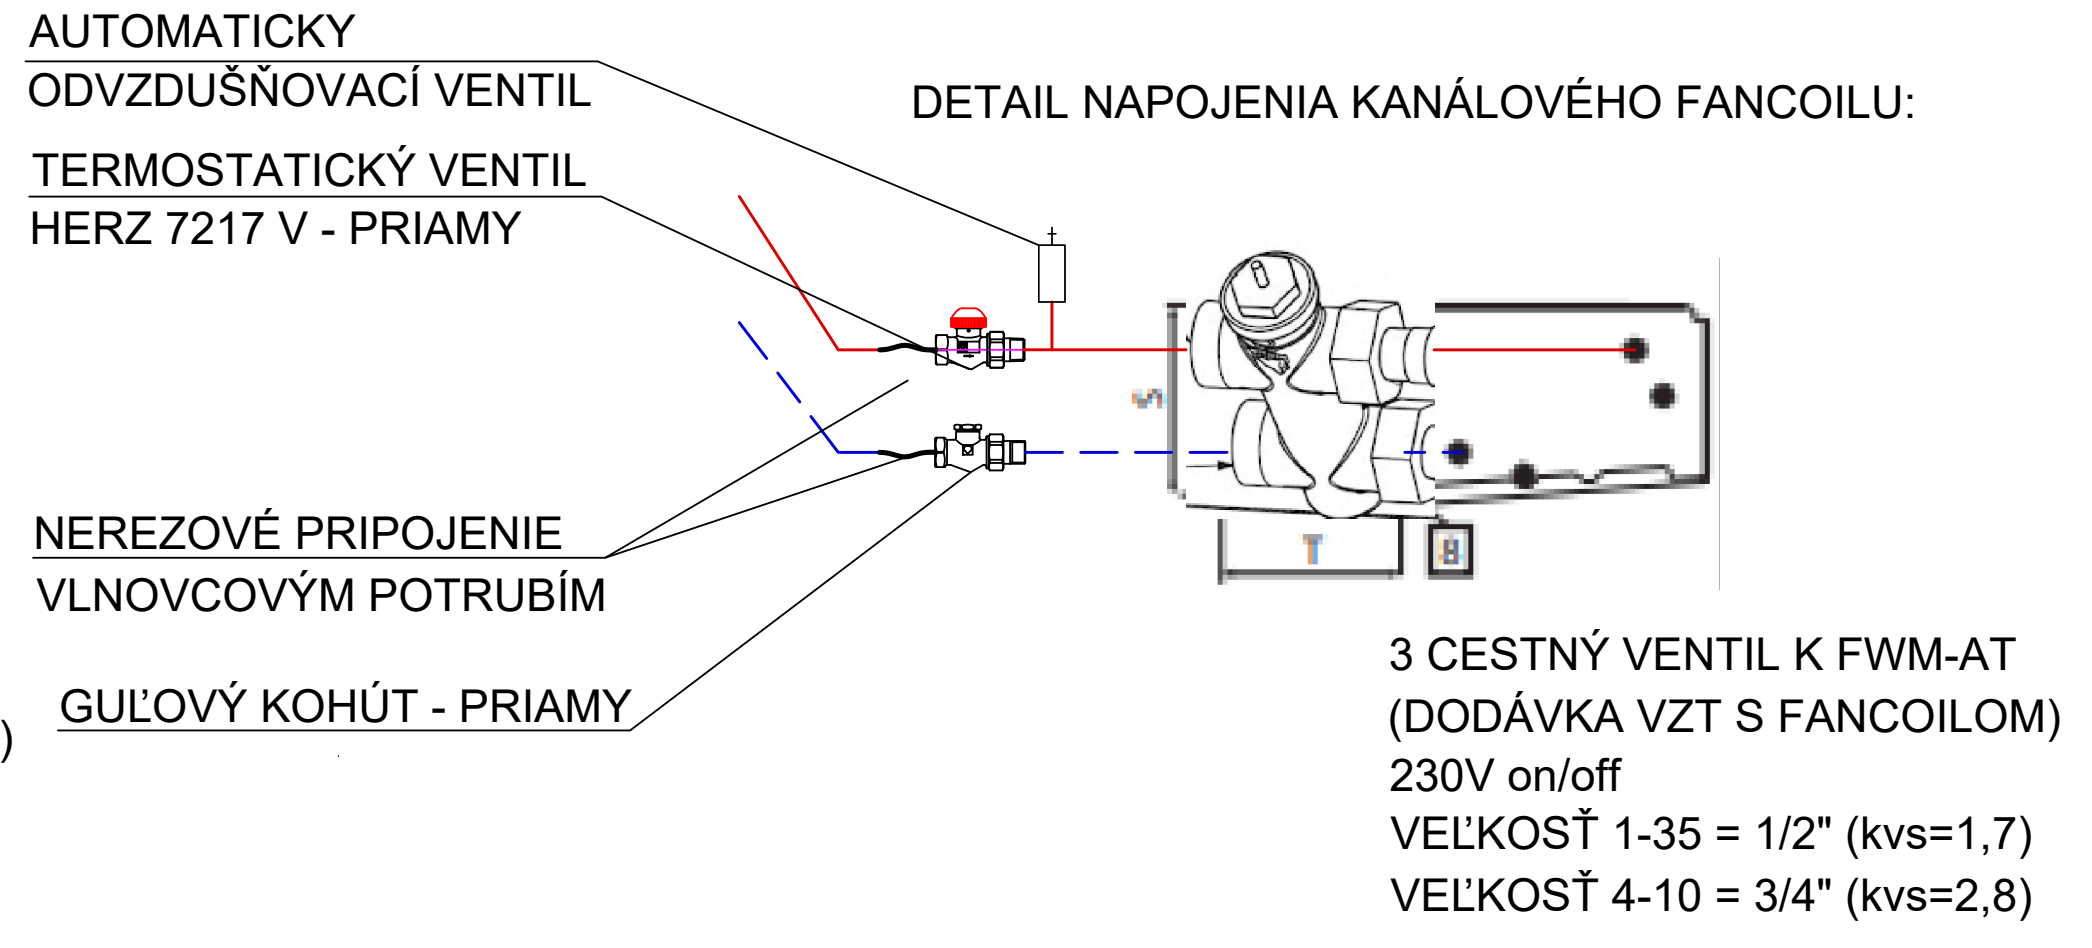
AUTOMATICKY ODVZDUŠŇOVACÍ VENTIL
TERMOSTATICKÝ VENTIL HERZ 7217 V - PRIAMY
NEREZOVÉ PRIPOJENIE VLNOVCOVÝM POTRUBÍM
GUĽOVÝ KOHÚT - PRIAMY
S
T
B

3 CESTNÝ VENTIL K FWM-AT
(DODÁVKA VZT S FANCOILOM)
230V on/off
VEĽKOSŤ 1-35 = 1/2" (kvs=1,7)
VEĽKOSŤ 4-10 = 3/4" (kvs=2,8)

DETAIL NAPOJENIA PARAPETNÉHO FANCOILU:

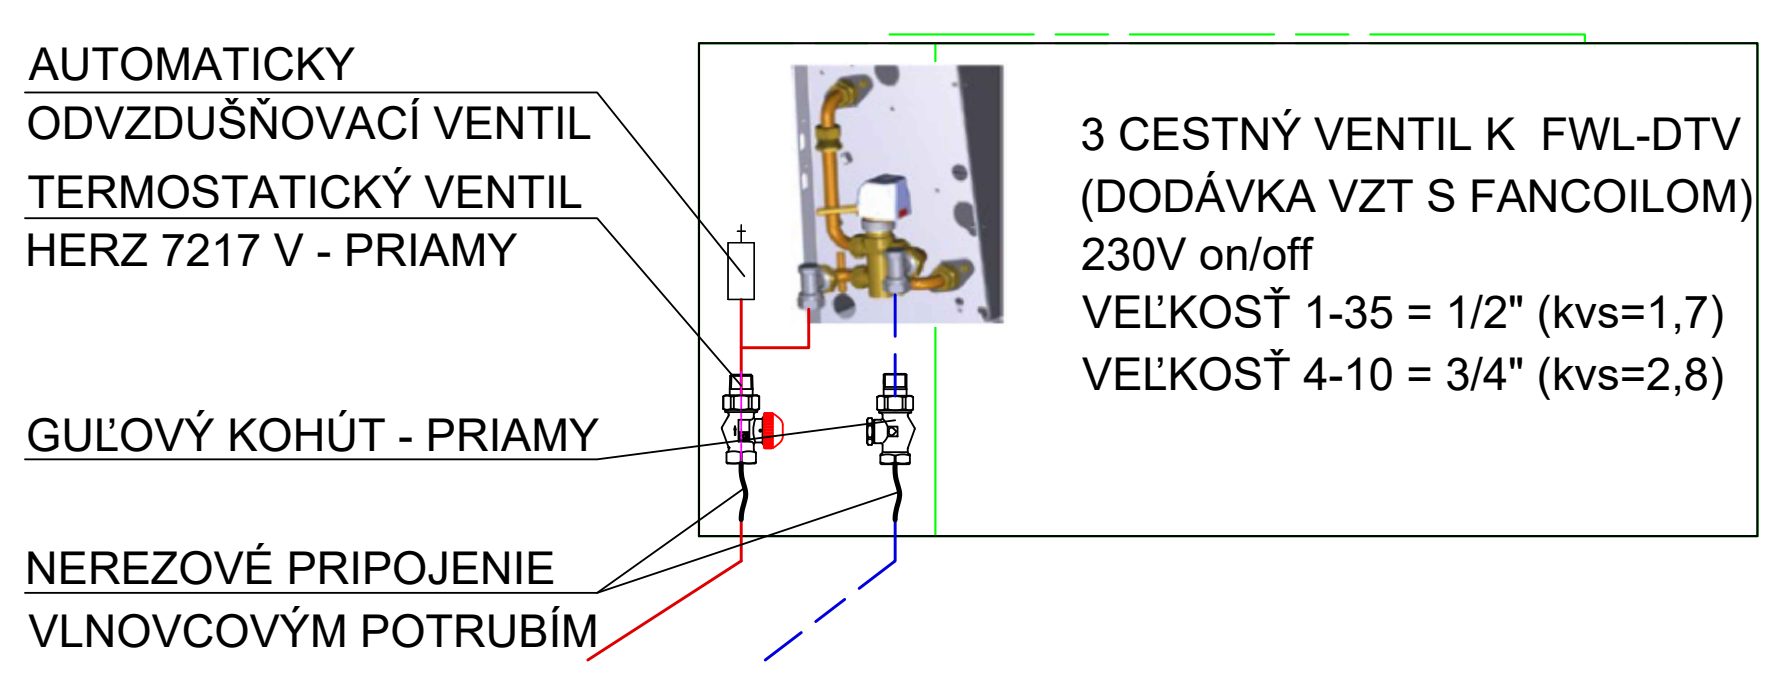
AUTOMATICKY ODVZDUŠŇOVACÍ VENTIL
TERMOSTATICKÝ VENTIL HERZ 7217 V - PRIAMY
GUĽOVÝ KOHÚT - PRIAMY
NEREZOVÉ PRIPOJENIE VLNOVCOVÝM POTRUBÍM

3 CESTNÝ VENTIL K FWL-DTV
(DODÁVKA VZT S FANCOILOM)
230V on/off
VEĽKOSŤ 1-35 = 1/2" (kvs=1,7)
VEĽKOSŤ 4-10 = 3/4" (kvs=2,8)

SADA ČÍSLO

±0,000 = ÚROVEŇ PODLAHY 1.NP

Objednávateľ:	Trenčiansky samosprávny kraj, K dolnej stanici 7282/20A, 911 01 Trenčín, Trenčianska univerzita Alexandra Dubčeka v Trenčíne, Študentská 2, 911 50 Trenčín
Generálny projektant:	Arch Konstrukt s.r.o., J. Braneckého 179/14, 911 01 Trenčín
Kontroloval:	Ing. Ján Bátor
Vypracoval:	Ing. J. Bátor, Ing. V. Labovský
Kraj:	Trenčiansky
Okres:	Púchov
Obec:	Púchov
Investor:	Trenčiansky samosprávny kraj, K dolnej stanici 7282/20A, 911 01 Trenčín, Trenčianska univerzita Alexandra Dubčeka v Trenčíne, Študentská 2, 911 50 Trenčín
Miesto stavby:	k.ú Horné Kočkovce, p.č.1509/1, 1510/1, 1527, 1528, 1529/1, 1529/2, 1530/1, 1533, 1535, 1548/2, 1548/4, 1548/5, 1548/6,
Stupeň PD:	DOKUMENTÁCIA PRE STAVEBNÉ POVOLENIE
Akcia:	EDU-TECH KAMPUS PÚCHOV
Objekt:	SO 201 FPT TnUAD
Obsah:	Pôdorys 2.NP
Dátum:	7/2026
Stupeň:	DSP
	Vykurovanie
Formát:	30xA4
Mierka:	1 : 50
Výkres:	02

ARCH KONSTRUKT
J. Braneckého 179/14, 911 01 Trenčín
tel. 0907/146 508
www.archkonstrukt.sk
email: filina@archkonstrukt.sk