DOSKOVÉ VYKUROVACIE TELESO
VYKUROVACIE TELESO
TERMOSTATICKÁ HLAVICA
PRIPOJOVACIA ARMATÚRA
PRÍSTUP K VENTILOM CEZ REVÍZNE VRÁTKA
POTRUBIE ULOŽENÉ V PODLAHE
POTRUBIE ULOŽENÉ POD STROPOM
HERZ 7217 V (1.10) PRIAMY DN20 Guľový kohút DN20
HERZ 7217 V (2.00) PRIAMY DN15 Guľový kohút DN15
HERZ 7217 V (1.90) PRIAMY DN15 Guľový kohút DN15
ext. žalúzia
tieniaca roleta
- 3.03 - FANCOLOVÁ PARAPETNÁ JEDNOTKA VSTAVANÁ FWL06DTN VÝKON - Qchl=3600 W, Qvyk=1409 W TEPLOTNÝ SPÁD - chl: 7/12°C, vyk: 45/40°C PRIETOK - 245.1 l/h
- 3.04 - FANCOLOVÁ PARAPETNÁ JEDNOTKA VSTAVANÁ FWL02DTN VÝKON - Qchl=1700 W, Qvyk=1047 W TEPLOTNÝ SPÁD - chl: 7/12°C, vyk: 45/40°C PRIETOK - 182.13 l/h
- 3.05 - FANCOLOVÁ PARAPETNÁ JEDNOTKA VSTAVANÁ FWL02DTN VÝKON - Qchl=1600 W, Qvyk=1216 W TEPLOTNÝ SPÁD - chl: 7/12°C, vyk: 45/40°C PRIETOK - 182.13 l/h
- 3.01 - FANCOLOVÁ KANÁLOVÁ JEDNOTKA FVM04AT VÝKON - Qchl=3220 W, Qvyk=1424 W TEPLOTNÝ SPÁD - chl: 7/12°C, vyk: 45/40°C PRIETOK - 247.70 l/h
- 3.01 - FANCOLOVÁ PODSTROPNÁ JEDNOTKA FVH04AT VÝKON - Qchl=4300 W, Qvyk=1424 W TEPLOTNÝ SPÁD - chl: 7/12°C, vyk: 45/40°C PRIETOK - 247.7 l/h
- 3.03 - Zasadačka dekana 47.0 m2 152.9 m3 20 °C 2990 W 26 °C 5946 W
- 3.04 - Sektretariát 24.7 m2 80.3 m3 20 °C 1109 W 26 °C 1433 W
- 3.05 - Kancelária dekana 23.0 m2 74.8 m3 20 °C 1277 W 26 °C 1430 W
- 3.10 - Wc personal 5.3 m2 17.1 m3 15 °C 144 W 26 °C 0 W
- 3.08 - Wc muži 12.1 m2 39.4 m3 15 °C 134 W 26 °C 0 W
- 3.10 - KORAD 11VKP 3/06 TV15 (1) - VK-RS20 (6 Otv.)
- 3.08 - KORAD 11VKP 3/06 TV15 (1) - VK-RS20 (6 Otv.)
HERZ 7217 V (1.80) PRIAMY DN20 Guľový kohút DN20
HERZ 7217 V (1.40) PRIAMY DN20 Guľový kohút DN20
HERZ 7217 V (1.40) PRIAMY DN15 Guľový kohút DN15
HERZ 7217 V (1.70) PRIAMY DN15 Guľový kohút DN15
- 3.21 - FANCOLOVÁ PARAPETNÁ JEDNOTKA FWL04DTN VÝKON - Qchl=2200 W, Qvyk=2526 W TEPLOTNÝ SPÁD - chl: 7/12°C, vyk: 45/40°C PRIETOK - 439.40 l/h
- 3.22 - FANCOLOVÁ PARAPETNÁ JEDNOTKA FWL01DTN VÝKON - Qchl=1000 W, Qvyk=952 W TEPLOTNÝ SPÁD - chl: 7/12°C, vyk: 45/40°C PRIETOK - 165.6 l/h
- 3.23 - FANCOLOVÁ PARAPETNÁ JEDNOTKA FWL01DTN VÝKON - Qchl=1020 W, Qvyk=1033 W TEPLOTNÝ SPÁD - chl: 7/12°C, vyk: 45/40°C PRIETOK - 179.69 l/h
- 3.24 - FANCOLOVÁ PARAPETNÁ JEDNOTKA FWL03DTN VÝKON - Qchl=2200 W, Qvyk=2097 W TEPLOTNÝ SPÁD - chl: 7/12°C, vyk: 45/40°C PRIETOK - 364.77 l/h
- 3.21 - Laboratórium - PC učebňa 42.8 m2 139.1 m3 20 °C 1498 W 26 °C 1435 W
- 3.22 - Dielňa dizajnu 19.8 m2 64.3 m3 20 °C 987 W 26 °C 852 W
- 3.23 - Dielňa dizajnu 21.5 m2 70.0 m3 20 °C 1014 W 26 °C 918 W
- 3.24 - Laboratórium 85.1 m2 276.6 m3 20 °C 4247 W 26 °C 3672 W
DN125-iz
Digestor
Vývod VZT exist.
3.01 3.06 3.07 3.08 3.09 3.10 3.11 3.12 3.15 3.16 3.17 3.18 3.19 3.20 3.21 3.22 3.23 3.24 3.25 3.26 3.27 3.28 3.29 3.32 3.33 3.34 3.36 3.37 3.38 3.39 3.40
A B C D E F G H I J K L M N O
1 2 3 4 5 6 8 9

Č.M.	Názov	Plocha
3.01	Vstupná hala	52.24
3.02	Výťah	3.47
3.03	Zasadačka dekana	41.13
3.04	Sekretáriát	24.72
3.05	kancelária dekana	23.39
3.06	Chodba	74.82
3.07	Bezbarier. záchodová kabína	3.90
3.08	WC muži	11.97
3.09	WC ženy	13.92
3.10	WC personál	4.27
3.11	Kuchynka	11.59
3.12	Archív + sklad	8.05
3.13	Kabinet	22.84
3.14	Učebňa	23.78
3.15	Laboratórium	55.03
3.16	Schodisko	21.49
3.17	Učebňa	73.82
3.18	Kabinet	24.16
3.19	Atelier dizajnu	56.41
3.20	Spojovacia chodba	200.53
3.21	Laboratórium - PC učebňa	40.89
3.22	Dielňa dizajnu	19.46
3.23	Dielňa dizajnu	21.43
3.24	Laboratórium	83.42
3.25	Laboratórium	25.59
3.26	Sklad skla	26.81
3.27	Sklad	22.44
3.28	Bezbarier. záchodová kabína	3.30
3.29	WC ženy	10.03
3.30	WC muži	10.36
3.31	Upratovačka	4.80
3.32	Schodisko	30.04
3.33	Výťah	4.10
3.34	Sklad	8.88
3.35	Laboratórium	18.93
3.36	Pripravovňa	19.07
3.37	Laboratórium	86.36
3.38	Schodisko	18.96
3.39	Schodisko	11.57
3.40	Aula - balkón	57.48
3.41	Technika - ozvučenie	18.64

L.M. 3.NP - PBS

DETAIL NAPOJENIA KAZETOVÉHO FANCOILU:

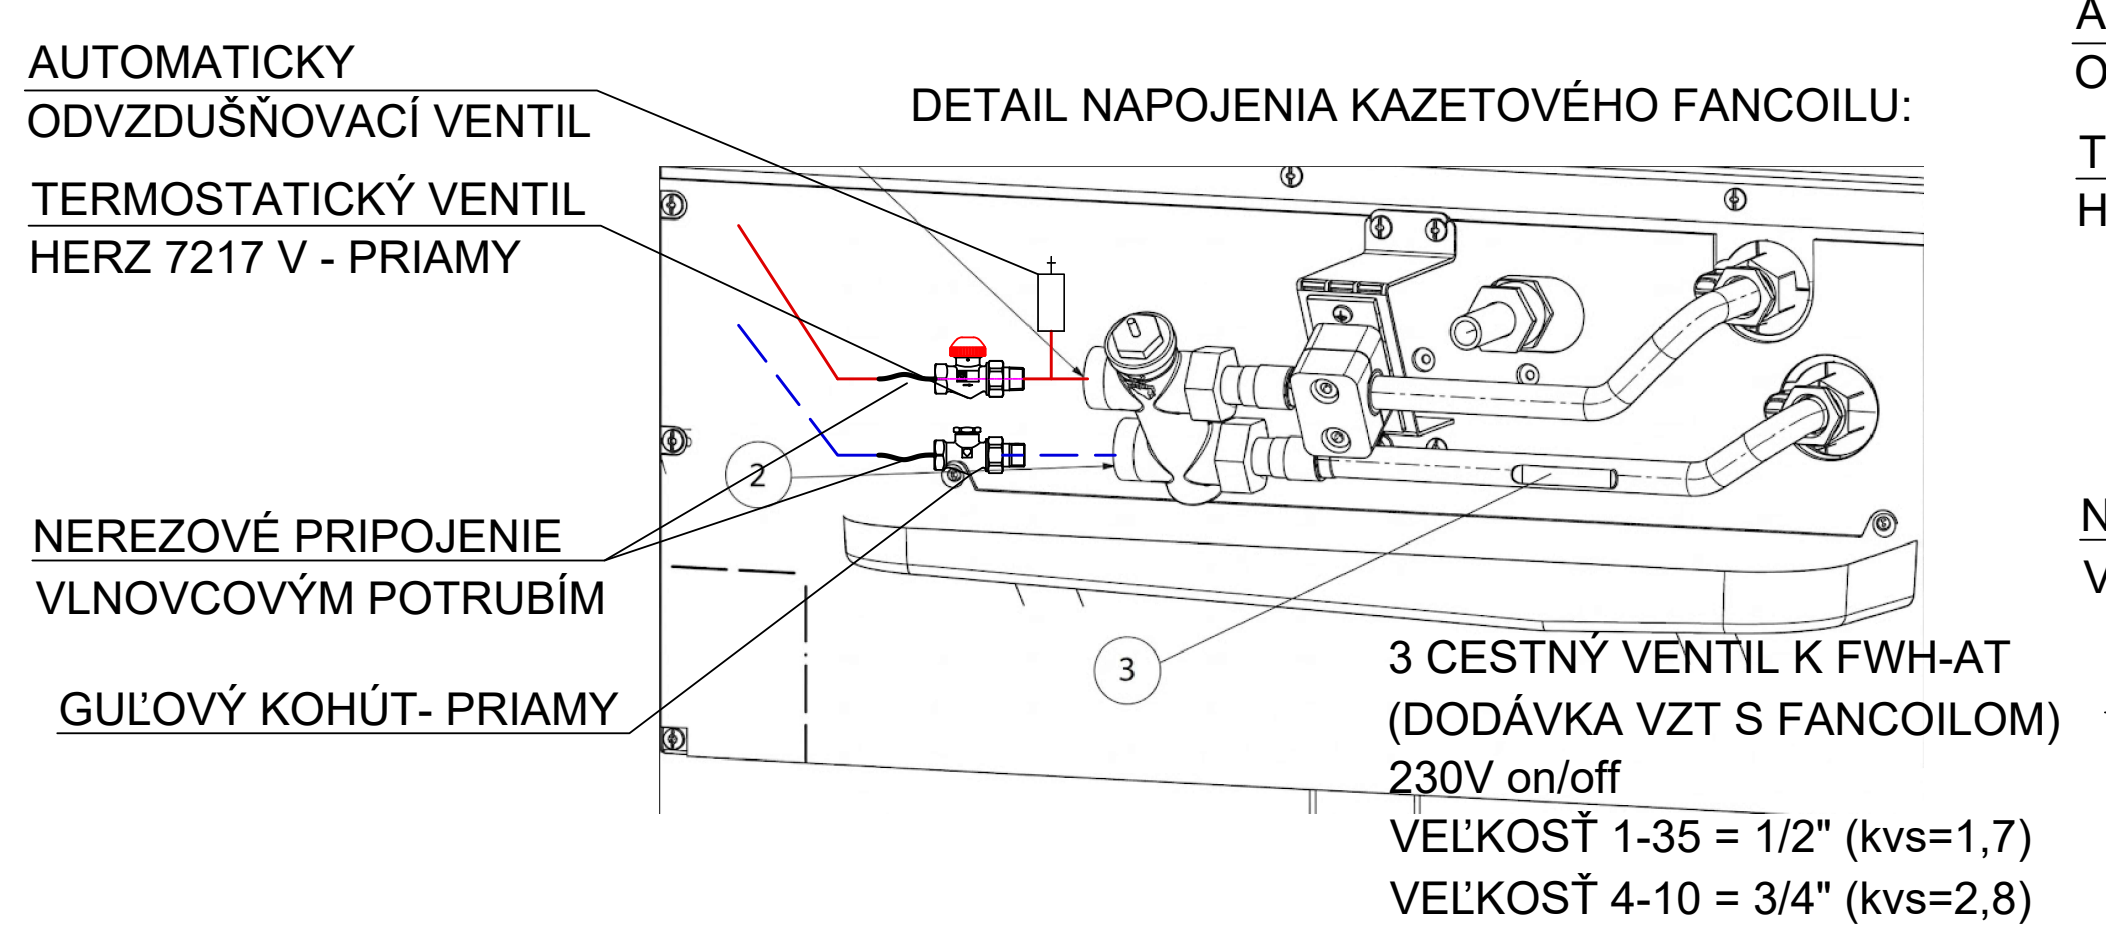
AUTOMATICKY ODVZDUŠŇOVACÍ VENTIL
TERMOSTATICKÝ VENTIL HERZ 7217 V - PRIAMY
NEREZOVÉ PRIPOJENIE VLNOVCOVÝM POTRUBÍM
GUĽOVÝ KOHÚT- PRIAMY
2
3

3 CESTNÝ VENTIL K FWH-AT
(DODÁVKA VZT S FANCOILOM)
230V on/off
VEĽKOSŤ 1-35 = 1/2" (kvs=1,7)
VEĽKOSŤ 4-10 = 3/4" (kvs=2,8)

DETAIL NAPOJENIA KANÁLOVÉHO FANCOILU:

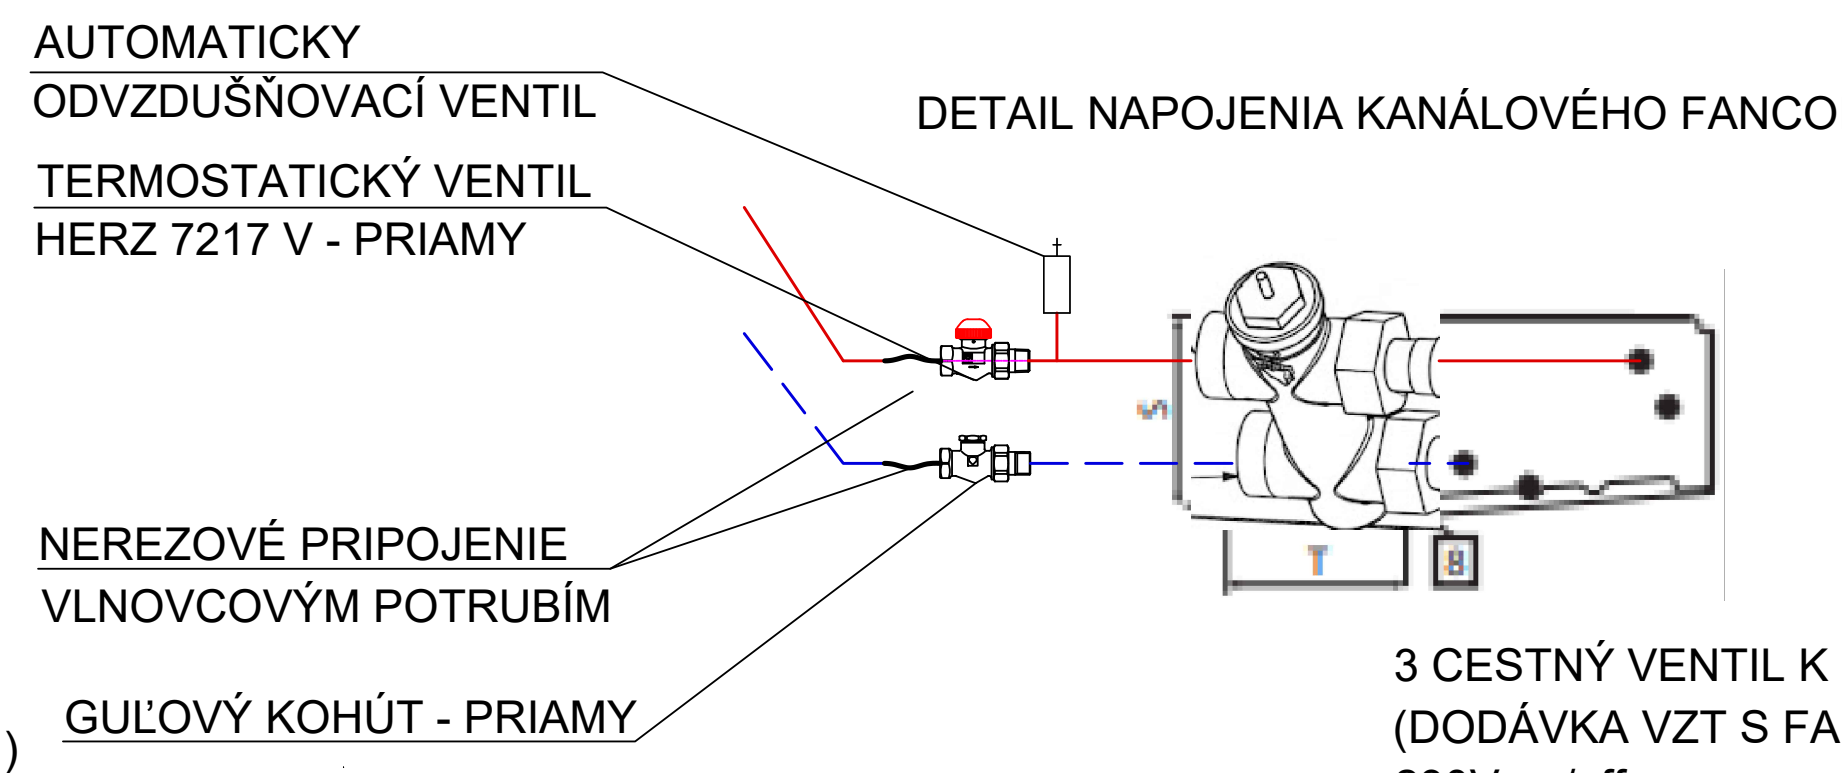
AUTOMATICKY ODVZDUŠŇOVACÍ VENTIL
TERMOSTATICKÝ VENTIL HERZ 7217 V - PRIAMY
NEREZOVÉ PRIPOJENIE VLNOVCOVÝM POTRUBÍM
GUĽOVÝ KOHÚT - PRIAMY

3 CESTNÝ VENTIL K FWM-AT
(DODÁVKA VZT S FANCOILOM)
230V on/off
VEĽKOSŤ 1-35 = 1/2" (kvs=1,7)
VEĽKOSŤ 4-10 = 3/4" (kvs=2,8)

DETAIL NAPOJENIA PARAPETNÉHO FANCOILU:

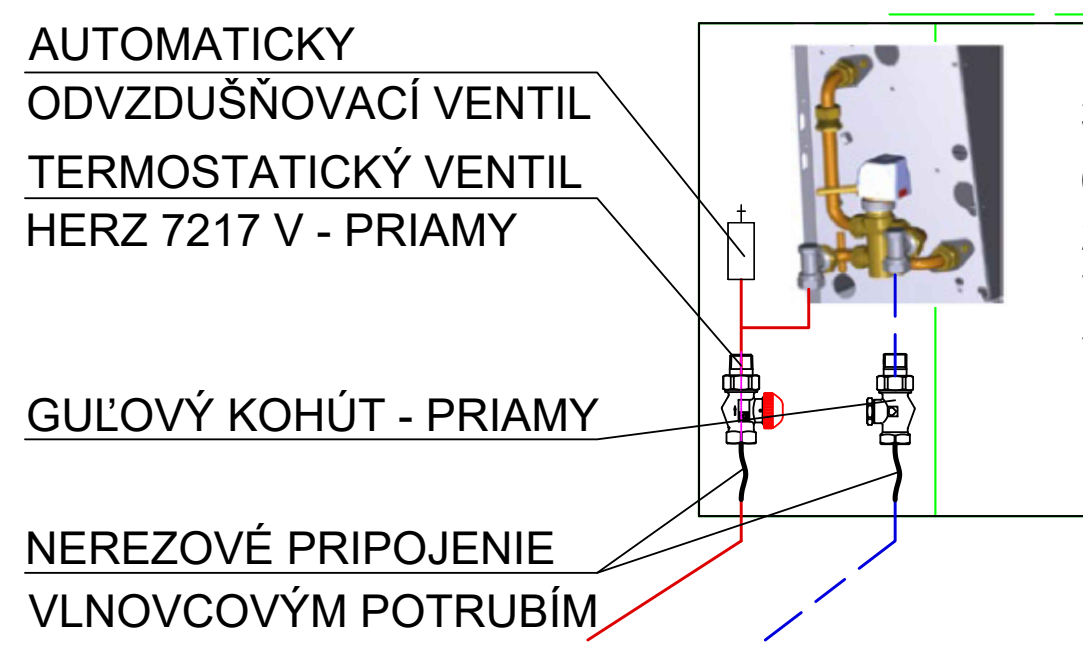
AUTOMATICKY ODVZDUŠŇOVACÍ VENTIL
TERMOSTATICKÝ VENTIL HERZ 7217 V - PRIAMY
GUĽOVÝ KOHÚT - PRIAMY
NEREZOVÉ PRIPOJENIE VLNOVCOVÝM POTRUBÍM

3 CESTNÝ VENTIL K FWL-DTV
(DODÁVKA VZT S FANCOILOM)
230V on/off
VEĽKOSŤ 1-35 = 1/2" (kvs=1,7)
VEĽKOSŤ 4-10 = 3/4" (kvs=2,8)

LEGENDA:

- VYKUROVACIE POTRUBIE - NÍZKOUHLÍKOVÉ OCELOVÉ POTRUBIE TEPLOTNÝ SPÁD 60/50 °C HLAVNÝ ROZVOD Z TEPELNÉHO ČERPADLA
- VYKUROVACIE POTRUBIE - NÍZKOUHLÍKOVÉ OCELOVÉ POTRUBIE TEPLOTNÝ SPÁD 60/50 °C HLAVNÝ ROZVOD Z AKUMULAČNEJ NÁDRŽE
- VYKUROVACIE POTRUBIE - PLASTOHLÍKOVÉ/NÍZKOUHLÍKOVÉ OCELOVÉ POTRUBIE TEPLOTNÝ SPÁD 45/40 °C PRE NAPOJENIE RADIATOROV
- VYKUROVACIE POTRUBIE - PLASTOHLÍKOVÉ POTRUBIE/NÍZKOUHLÍKOVÉ OCELOVÉ POTRUBIE TEPLOTNÝ SPÁD 45/40 °C
- EXPANZNÉ POTRUBIE
- DOSKOVÉ VYKUROVACIE TELESO
- STÚPANIE/KLESANIE POTRUBIA
- PARAPETNÁ FANCOIL JEDNOTKA
- KANÁLOVÁ VZDUCHOVÁ JEDNOTKA
- KAZETOVÁ STROPNÁ FANCOIL JEDNOTKA

LEGENDA VYKUROVACÍCH OKRUHOV:

UK1 - Prevádzka kancelárie 4.NP Fancoil
UK2 - Prevádzka Aula Fancoil
UK3 - Prevádzka škola Sever Fancoil
UK4 - Prevádzka škola Juh Fancoil
UK5 - Prevádzka škola Radiatory

LEGENDA POPISOVÝCH TABULIEK:

ČÍSLO MIESTNOSTI
ÚČEL MIESTNOSTI
OBJEM MIESTNOSTI
PLOCHA MIESTNOSTI
VÝPOČTOVÁ TEPLOTA
TEPELNÁ STRATA

- 1.12 -	
Chodba	
19.8 m2	55.2 m3
15 °C	2054 W

SADA ČÍSLO

±0,000 = ÚROVEŇ PODLAHY 1.NP

Objednávateľ:	Trenčiansky samosprávny kraj, K dolnej stanici 7282/20A, 911 01 Trenčín, Trenčianska univerzita Alexandra Dubčeka v Trenčíne, Študentská 2, 911 50 Trenčín
Generálny projektant:	Arch Konstrukt s.r.o., J. Braneckého 179/14, 911 01 Trenčín
Kontroloval:	Ing. Ján Bátor
Vypracoval:	Ing. J. Bátor, Ing. V. Labovský
Kraj:	Trenčiansky
Okres:	Púchov
Obec:	Púchov
Investor:	Trenčiansky samosprávny kraj, K dolnej stanici 7282/20A, 911 01 Trenčín, Trenčianska univerzita Alexandra Dubčeka v Trenčíne, Študentská 2, 911 50 Trenčín
Miesto stavby:	k.ú Horné Kočkovce, p.č.1509/1, 1510/1, 1527, 1528, 1529/1, 1529/2, 1530/1, 1533, 1535, 1548/2, 1548/4, 1548/5, 1548/6,
Stupeň PD:	DOKUMENTÁCIA PRE STAVEBNÉ POVOLENIE
Akcia:	EDU-TECH KAMPUS PÚCHOV
Objekt:	SO 201 FPT TnUAD
Obsah:	Pôdorys 3.NP
Dátum:	7/2026
Stupeň:	DSP
	Vykurovanie
Formát:	30xA4
Mierka:	1 : 50
Výkres:	03

ARCH KONSTRUKT
J. Braneckého 179/14, 911 01 Trenčín
tel. 0907/146 508
www.archkonstrukt.sk
email: filina@archkonstrukt.sk