POTRUBIE ULOŽENÉ V PODLAHE
HERZ 7217 V (1.30) PRIAMY DN20 Guľový kohút DN20
1
26x3,0
PRÍSTUP K VENTILOM CEZ REVÍZNE VRÁTKA
- 4.03 - FANCOLOVÁ PARAPETNÁ JEDNOTKA VSTAVANÁ FWL08DTN VÝKON - Qchl=4420 W, Qvyk=1946 W TEPLOTNÝ SPÁD - chl: 7/12°C, vyk: 45/40°C PRIETOK - 338.51 kg/h
HERZ 7217 V (1.20) PRIAMY DN20 Guľový kohút DN20
2
- 4.03 - FANCOLOVÁ PARAPETNÁ JEDNOTKA VSTAVANÁ FWL08DTN VÝKON - Qchl=4420 W, Qvyk=1946 W TEPLOTNÝ SPÁD - chl: 7/12°C, vyk: 45/40°C PRIETOK - chl: 338.51 l/h
HERZ 7217 V (0.10) PRIAMY DN20 Guľový kohút DN20
3
- 4.03 - FANCOLOVÁ PARAPETNÁ JEDNOTKA VSTAVANÁ FWL01DTN VÝKON - Qchl=1400 W, Qvyk=458 W TEPLOTNÝ SPÁD - chl: 7/12°C, vyk: 45/40°C PRIETOK - chl: 79.67 l/h
HERZ 7217 V (1.10) PRIAMY DN20 Guľový kohút DN20
4
- 4.03 - FANCOLOVÁ PARAPETNÁ JEDNOTKA VSTAVANÁ FWL04DTN VÝKON - Qchl=3000 W, Qvyk=1760 W TEPLOTNÝ SPÁD - chl: 7/12°C, vyk: 45/40°C PRIETOK - chl: 306.15 l/h
- 4.03 - Knižnica 54.8 m2 170.4 m3 20 °C 4115 W 26 °C 8003 W
- 4.04 - Sklad kníh 17.6 m2 53.9 m3 15 °C 513 W 26 °C 906 W
- 4.01 - FANCOLOVÁ PODSTROPNÁ JEDNOTKA FVH04AT VÝKON - Qchl=4300 W, Qvyk=744 W TEPLOTNÝ SPÁD - chl: 7/12°C, vyk: 45/40°C PRIETOK - chl: 740 l/h,vyk: 128 l/h
HERZ 7217 V (1.00) PRIAMY DN20 Guľový kohút DN20
69
40x3,5
40x3,5 POTRUBIE ULOŽENÉ POD STROPOM
32x3,0 POTRUBIE ULOŽENÉ POD STROPOM
POTRUBIE ULOŽENÉ POD STROPOM 26x3,0
20x2,0
26x3,0
PRÍSTUP K VENTILOM CEZ REVÍZNE VRÁTKA
galéria
-1.500
- 4.01 - Vstupná hala 71.6 m2 219.2 m3 20 °C 3014 W 26 °C 12801 W
4.01
4.02
4.03
4.04
4.05
4.06
4.07
4.08
4.09
HERZ 7217 V (1.00) PRIAMY DN20 Guľový kohút DN20
27
- 4.03 - FANCOLOVÁ PARAPETNÁ JEDNOTKA FWL04DTN VÝKON - Qchl=3000 W, Qvyk=1760 W TEPLOTNÝ SPÁD - chl: 7/12°C, vyk: 45/40°C PRIETOK - 306.15 kg/h
- 4.09 - FWL04DTN
- 4.09 - Seminárna miestnosť 73.5 m2 224.9 m3 20 °C 3646 W 26 °C 4327 W
+9.300
+7.500
4.14
4.48
ext. žalúzia
HERZ 7217 V (2.30) PRIAMY DN15 Guľový kohút DN15
5
- 4.10 - FANCOLOVÁ PARAPETNÁ JEDNOTKA FWL02DTN VÝKON - Qchl=1660 W, Qvyk=1200 W TEPLOTNÝ SPÁD - chl: 7/12°C, vyk: 45/40°C PRIETOK - 208.74 l/h
- 4.10 - Kancelária 22.5 m2 68.9 m3 20 °C 1224 W 26 °C 1166 W
HERZ 7217 V (1.90) PRIAMY DN15 Guľový kohút DN15
6
- 4.11 - FANCOLOVÁ PARAPETNÁ JEDNOTKA FWL02DTN VÝKON - Qchl=1500 W, Qvyk=1138 W TEPLOTNÝ SPÁD - chl: 7/12°C, vyk: 45/40°C PRIETOK - 197.95 l/h
- 4.11 - Kancelária 20.5 m2 62.8 m3 20 °C 1135 W 26 °C 1062 W
HERZ 7217 V (1.40) PRIAMY DN15 Guľový kohút DN15
7
- 4.12 - FANCOLOVÁ PARAPETNÁ JEDNOTKA FWL01DTN VÝKON - Qchl=1100 W, Qvyk=921 W TEPLOTNÝ SPÁD - chl: 7/12°C, vyk: 45/40°C PRIETOK - 160.21 l/h
- 4.12 - Kancelária 16.1 m2 49.2 m3 20 °C 943 W 26 °C 854 W
HERZ 7217 V (3.10) PRIAMY DN15 Guľový kohút DN15
8
- 4.13 - FANCOLOVÁ PARAPETNÁ JEDNOTKA FWL02DTN VÝKON - Qchl=1850 W, Qvyk=1418 W TEPLOTNÝ SPÁD - chl: 7/12°C, vyk: 45/40°C PRIETOK - 246.66 l/h
HERZ 7217 V (3.00) PRIAMY DN15 Guľový kohút DN15
9
- 4.13 - FANCOLOVÁ PARAPETNÁ JEDNOTKA FWL02DTN VÝKON - Qchl=1850 W, Qvyk=1418 W TEPLOTNÝ SPÁD - chl: 7/12°C, vyk: 45/40°C PRIETOK - 246.66 l/h
- 4.13 - Jazyková učebňa 54.9 m2 168.0 m3 20 °C 2898 W 26 °C 2760 W
- 4.47 - Chodba 54.5 m2 166.8 m3 18 °C 1611 W 26 °C 70 W
- 4.15 - Kancelária 28.0 m2 85.7 m3 20 °C 1749 W 26 °C 2133 W
- 4.15- FANCOLOVÁ PARAPETNÁ JEDNOTKA FWL03DTN VÝKON - Qchl=2600 W, Qvyk=1791 W TEPLOTNÝ SPÁD - chl: 7/12°C, vyk: 45/40°C PRIETOK - 311.54 l/h
68
HERZ 7217 V (1.10) PRIAMY DN20 Guľový kohút DN20
- 4.16 - Kancelária 16.4 m2 50.2 m3 20 °C 961 W 26 °C 1296 W
- 4.16 - FANCOLOVÁ PARAPETNÁ JEDNOTKA FWL02DTN VÝKON - Qchl=1600 W, Qvyk=937 W TEPLOTNÝ SPÁD - chl: 7/12°C, vyk: 45/40°C PRIETOK - 162.99 l/h
25
HERZ 7217 V (1.40) PRIAMY DN15 Guľový kohút DN15
- 4.17 - Kancelária 25.5 m2 77.9 m3 20 °C 1418 W 26 °C 1987 W
- 4.17- FANCOLOVÁ PARAPETNÁ JEDNOTKA FWL04DTN VÝKON - Qchl=2470 W, Qvyk=1389 W TEPLOTNÝ SPÁD - chl: 7/12°C, vyk: 45/40°C PRIETOK - 241.62 l/h
24
HERZ 7217 V (0.70) PRIAMY DN20 Guľový kohút DN20
- 4.18 - Kancelária 17.1 m2 52.5 m3 20 °C 985 W 26 °C 1362 W
- 4.18 - FANCOLOVÁ PARAPETNÁ JEDNOTKA FWL02DTN VÝKON - Qchl=1660 W, Qvyk=965 W TEPLOTNÝ SPÁD - chl: 7/12°C, vyk: 45/40°C PRIETOK - 167.86 l/h
26
HERZ 7217 V (1.40) PRIAMY DN15 Guľový kohút DN15
- 4.19 - Kancelária 18.7 m2 57.1 m3 20 °C 1045 W 26 °C 1440 W
- 4.19 - FANCOLOVÁ PARAPETNÁ JEDNOTKA FWL02DTN VÝKON - Qchl=1750 W, Qvyk=1024 W TEPLOTNÝ SPÁD - chl: 7/12°C, vyk: 45/40°C PRIETOK - 178.12 l/h
23
HERZ 7217 V (1.60) PRIAMY DN15 Guľový kohút DN15
- 4.20 - Kancelária 25.4 m2 77.8 m3 20 °C 1415 W 26 °C 1987 W
- 4.20 - FANCOLOVÁ PARAPETNÁ JEDNOTKA FWL04DTN VÝKON - Qchl=2470 W, Qvyk=1387 W TEPLOTNÝ SPÁD - chl: 7/12°C, vyk: 45/40°C PRIETOK - 241.27 l/h
22
HERZ 7217 V (0.70) PRIAMY DN20 Guľový kohút DN20
- 4.21 - Kancelária 32.0 m2 97.9 m3 20 °C 1748 W 26 °C 2460 W
- 4.21 - FANCOLOVÁ PARAPETNÁ JEDNOTKA FWL04DTN VÝKON - Qchl=3000 W, Qvyk=1711 W TEPLOTNÝ SPÁD - chl: 7/12°C, vyk: 45/40°C PRIETOK - 308.06 l/h
21b
HERZ 7217 V (1.00) PRIAMY DN20 Guľový kohút DN20
20x2,0
HERZ 7217 V (3.40) PRIAMY DN15 Guľový kohút DN15
- 4.23 - FANCOLOVÁ PARAPETNÁ JEDNOTKA FWL03DTN VÝKON - Qchl=2000 W, Qvyk=1499 W TEPLOTNÝ SPÁD - chl: 7/12°C, vyk: 45/40°C PRIETOK - 260.75 l/h
26x3,0 POTRUBIE ULOŽENÉ V PODLAHE
10
- 4.23 - Kancelária 28.1 m2 86.0 m3 20 °C 1539 W 26 °C 1436 W
HERZ 7217 V (3.40) PRIAMY DN15 Guľový kohút DN15
- 4.24 - FANCOLOVÁ PARAPETNÁ JEDNOTKA FWL03DTN VÝKON - Qchl=2050 W, Qvyk=1510 W TEPLOTNÝ SPÁD - chl: 7/12°C, vyk: 45/40°C PRIETOK - 262.66 l/h
15
- 4.24 - Kancelária 29.5 m2 90.2 m3 20 °C 1549 W 26 °C 1483 W
HERZ 7217 V (1.00) PRIAMY DN20 Guľový kohút DN15
11
- 4.25 - FANCOLOVÁ PARAPETNÁ JEDNOTKA FWL04DTN VÝKON - Qchl=2400 W, Qvyk=1775 W TEPLOTNÝ SPÁD - chl: 7/12°C, vyk: 45/40°C PRIETOK - 308.76 l/h
- 4.25 - Kancelária 34.4 m2 105.2 m3 20 °C 1821 W 26 °C 1752 W
HERZ 7217 V (3.70) PRIAMY DN15 Guľový kohút DN15
12
- 4.26 - FANCOLOVÁ PARAPETNÁ JEDNOTKA FWL03DTN VÝKON - Qchl=2100 W, Qvyk=1569 W TEPLOTNÝ SPÁD - chl: 7/12°C, vyk: 45/40°C PRIETOK - 272.93 l/h
- 4.26 - Kancelária 30.8 m2 94.2 m3 20 °C 1608 W 26 °C 1586 W
HERZ 7217 V (3.80) PRIAMY DN15 Guľový kohút DN15
13
- 4.27 - FANCOLOVÁ PARAPETNÁ JEDNOTKA FWL03DTN VÝKON - Qchl=2100 W, Qvyk=1584 W TEPLOTNÝ SPÁD - chl: 7/12°C, vyk: 45/40°C PRIETOK - 275.54 l/h
- 4.27 - Kancelária 31.1 m2 95.1 m3 20 °C 1624 W 26 °C 1586 W
HERZ 7217 V (1.20) PRIAMY DN20 Guľový kohút DN20
14
- 4.28 - FANCOLOVÁ PARAPETNÁ JEDNOTKA FWL04DTN VÝKON - Qchl=2470 W, Qvyk=1998 W TEPLOTNÝ SPÁD - chl: 7/12°C, vyk: 45/40°C PRIETOK - 347.55 l/h
- 4.28 - Kancelária 36.2 m2 110.6 m3 20 °C 1943 W 26 °C 1843 W
- 4.22 - Spojovacia chodba 105.9 m2 324.1 m3 18 °C 3248 W 26 °C 6861 W
+10.800
75x4,6
DN125-iz
29
TČ1
TČ1
POTRUBIE ULOŽENÉ POD STROPOM 75x4,6
63x4,5 POTRUBIE ULOŽENÉ POD STROPOM
UP
HERZ 7217 V (1.10) PRIAMY DN15 Guľový kohút DN15
28
- 4.44 - FANCOLOVÁ PARAPETNÁ JEDNOTKA FWL03DTN VÝKON - Qchl=1350 W, Qvyk=976 W TEPLOTNÝ SPÁD - chl: 7/12°C, vyk: 45/40°C PRIETOK - 168.77 l/h
- 4.44 - Sklad dizajn 20.2 m2 61.8 m3 15 °C 1055 W 26 °C 1092 W
tieniaca roleta
+9.000
- 4.42 - Schodisko 18.9 m2 57.9 m3 18 °C 0 W 26 °C 24 W
HERZ 7217 V (2.30) PRIAMY DN20 Guľový kohút DN20
- 4.45 - FANCOLOVÁ PODSTROPNÁ JEDNOTKA FWH04AT VÝKON - Qchl=4500 W, Qvyk=3136 W TEPLOTNÝ SPÁD - chl: 7/12°C, vyk: 45/40°C PRIETOK - 545.51 l/h
- 4.45 - Seminárna miestnosť 111.3 m2 340.7 m3 20 °C 6386 W 26 °C 7337 W
32x3,0 POTRUBIE ULOŽENÉ POD STROPOM
HERZ 7217 V (2.00) PRIAMY DN20 Guľový kohút DN20
- 4.45 - FANCOLOVÁ PODSTROPNÁ JEDNOTKA FWH04AT VÝKON - Qchl=4500 W, Qvyk=3136 W TEPLOTNÝ SPÁD - chl: 7/12°C, vyk: 45/40°C PRIETOK - 545.51 l/h
40x3,5 POTRUBIE ULOŽENÉ POD STROPOM
POTRUBIE ULOŽENÉ POD STROPOM 50x4,0
HERZ 7217 V (1.90) PRIAMY DN20 Guľový kohút DN20
- 4.29 - FANCOLOVÁ PODSTROPNÁ JEDNOTKA FWH04AT VÝKON - Qchl=4000 W, Qvyk=3017W TEPLOTNÝ SPÁD - chl: 7/12°C, vyk: 45/40°C PRIETOK - 524.81 l/h
HERZ 7217 V (1.90) PRIAMY DN20 Guľový kohút DN20
- 4.29 - FANCOLOVÁ PODSTROPNÁ JEDNOTKA FWH04AT VÝKON - Qchl=4000 W, Qvyk=3017W TEPLOTNÝ SPÁD - chl: 7/12°C, vyk: 45/40°C PRIETOK - 524.81 l/h
HERZ 7217 V (1.80) PRIAMY DN20 Guľový kohút DN20
- 4.29 - FANCOLOVÁ PODSTROPNÁ JEDNOTKA FWH04AT VÝKON - Qchl=4000 W, Qvyk=3017W TEPLOTNÝ SPÁD - chl: 7/12°C, vyk: 45/40°C PRIETOK - 524.81 l/h
- 4.29 - Multifunčný priestor 194.5 m2 595.3 m3 20 °C 7641 W 26 °C 3243 W
4.30
4.31
4.32
4.33
4.34
4.35
HERZ 7217 V (1.80) PRIAMY DN20 Guľový kohút DN20
- 4.46 - FANCOLOVÁ PODSTROPNÁ JEDNOTKA FWH04AT VÝKON - Qchl=4100 W, Qvyk=3080W TEPLOTNÝ SPÁD - chl: 7/12°C, vyk: 45/40°C PRIETOK - 535.77 l/h
- 4.46 - Ateliér II 49.4 m2 151.1 m3 20 °C 3091 W 26 °C 3582 W
HERZ 7217 V (1.80) PRIAMY DN20 Guľový kohút DN20
- 4.47 - FANCOLOVÁ PODSTROPNÁ JEDNOTKA FWH04AT VÝKON - Qchl=3000 W, Qvyk=1899 W TEPLOTNÝ SPÁD - chl: 7/12°C, vyk: 45/40°C PRIETOK - 521.85 l/h
- 4.47 - Kancelária 30.5 m2 93.3 m3 20 °C 1952 W 26 °C 2518 W
- 4.36 - Kancelária 32.2 m2 98.5 m3 20 °C 2420 W 26 °C 2475 W
- 4.36 - FANCOLOVÁ PARAPETNÁ JEDNOTKA FWL04DTN VÝKON - Qchl=3000 W, Qvyk=2497 W TEPLOTNÝ SPÁD - chl: 7/12°C, vyk: 45/40°C PRIETOK - 434.35 l/h
21a
HERZ 7217 V (1.40) PRIAMY DN20 Guľový kohút DN20
- 4.37 - Kancelária 21.6 m2 66.2 m3 20 °C 1121 W 26 °C 1648 W
- 4.37 - FANCOLOVÁ PARAPETNÁ JEDNOTKA FWL03DTN VÝKON - Qchl=2200 W, Qvyk=1057 W TEPLOTNÝ SPÁD - chl: 7/12°C, vyk: 45/40°C PRIETOK - 183.86 l/h
20
HERZ 7217 V (1.40) PRIAMY DN15 Guľový kohút DN15
- 4.38 - Kancelária 21.7 m2 66.3 m3 20 °C 1128 W 26 °C 1655 W
- 4.38 - FANCOLOVÁ PARAPETNÁ JEDNOTKA FWL03DTN VÝKON - Qchl=2200 W, Qvyk=1064 W TEPLOTNÝ SPÁD - chl: 7/12°C, vyk: 45/40°C PRIETOK - 185.08 l/h
19
HERZ 7217 V (1.40) PRIAMY DN15 Guľový kohút DN15
- 4.39 - Kancelária 21.7 m2 66.3 m3 20 °C 1121 W 26 °C 1648 W
- 4.39 - FANCOLOVÁ PARAPETNÁ JEDNOTKA FWL03DTN VÝKON - Qchl=2200 W, Qvyk=1057 W TEPLOTNÝ SPÁD - chl: 7/12°C, vyk: 45/40°C PRIETOK - 183.86 l/h
18
HERZ 7217 V (1.40) PRIAMY DN15 Guľový kohút DN15
- 4.41 - Kancelária 22.5 m2 68.9 m3 20 °C 1178 W 26 °C 1735 W
- 4.41 - FANCOLOVÁ PARAPETNÁ JEDNOTKA FWL03DTN VÝKON - Qchl=2300 W, Qvyk=1110W TEPLOTNÝ SPÁD - chl: 7/12°C, vyk: 45/40°C PRIETOK - 272.93 l/h
17
HERZ 7217 V (3.70) PRIAMY DN15 Guľový kohút DN15
- 4.42 - Kancelária 23.6 m2 72.1 m3 20 °C 1402 W 26 °C 1680 W
- 4.42 - FANCOLOVÁ PARAPETNÁ JEDNOTKA FWL03DTN VÝKON - Qchl=2200 W, Qvyk=1322 W TEPLOTNÝ SPÁD - chl: 7/12°C, vyk: 45/40°C PRIETOK - 229.96 l/h
16
HERZ 7217 V (2.50) PRIAMY DN15 Guľový kohút DN15
A
B
C
D
E
F
G
H
I
J
K
L
M
N
O
1
2
3
4
5
6
8
9

L.M. 4.NP - PBS		
Č.M.	Názov	Plocha
4.01	Vstupná hala	52.75
4.02	Výťah	3.47
4.03	Študovňa	44.85
4.04	Sklad kníh	17.09
4.05	Bezbarier. záchodová kabína	3.71
4.06	WC ženy	5.62
4.07	WC personál	1.97
4.08	WC muži	13.03
4.09	Seminárna miestnosť	67.28
4.10	Kancelária	21.00
4.11	Kancelária	19.47
4.12	Kancelária	16.26
4.13	Jazyková učebňa	48.19
4.14	Schodisko	21.56
4.15	Kancelária	26.52
4.16	Kancelária	16.03
4.17	Kancelária	24.69
4.18	Kancelária	16.84
4.19	Kancelária	17.04
4.20	Kancelária	24.64
4.21	Kancelária	27.91
4.22	Spojovacia chodba	220.43
4.23	Kancelária	26.85
4.24	Kancelária	26.34
4.25	Kancelária	33.03
4.26	Kancelária	29.12
4.27	Kancelária	29.64
4.28	Kancelária	31.93
4.29	Multifunkčný priestor	75.60
4.30	Bezbarier. záchodová kabína	3.46
4.31	WC ženy	10.38
4.32	WC muži	11.27
4.33	Upratovačka	4.90
4.34	Schodisko	29.94
4.35	Výťah	4.10
4.36	Kancelária	31.11
4.37	Kancelária	19.20
4.38	Kancelária	19.61
4.39	Kancelária	19.60
4.41	Kancelária	19.61
4.42	Kancelária	19.33
4.43	Schodisko	18.02
4.44	Sklad dizajn	19.74
4.45	Seminárna miestnosť	111.65
4.46	Ateliér II	48.46
4.47	Kancelária	26.43
4.48	Chodba	53.88

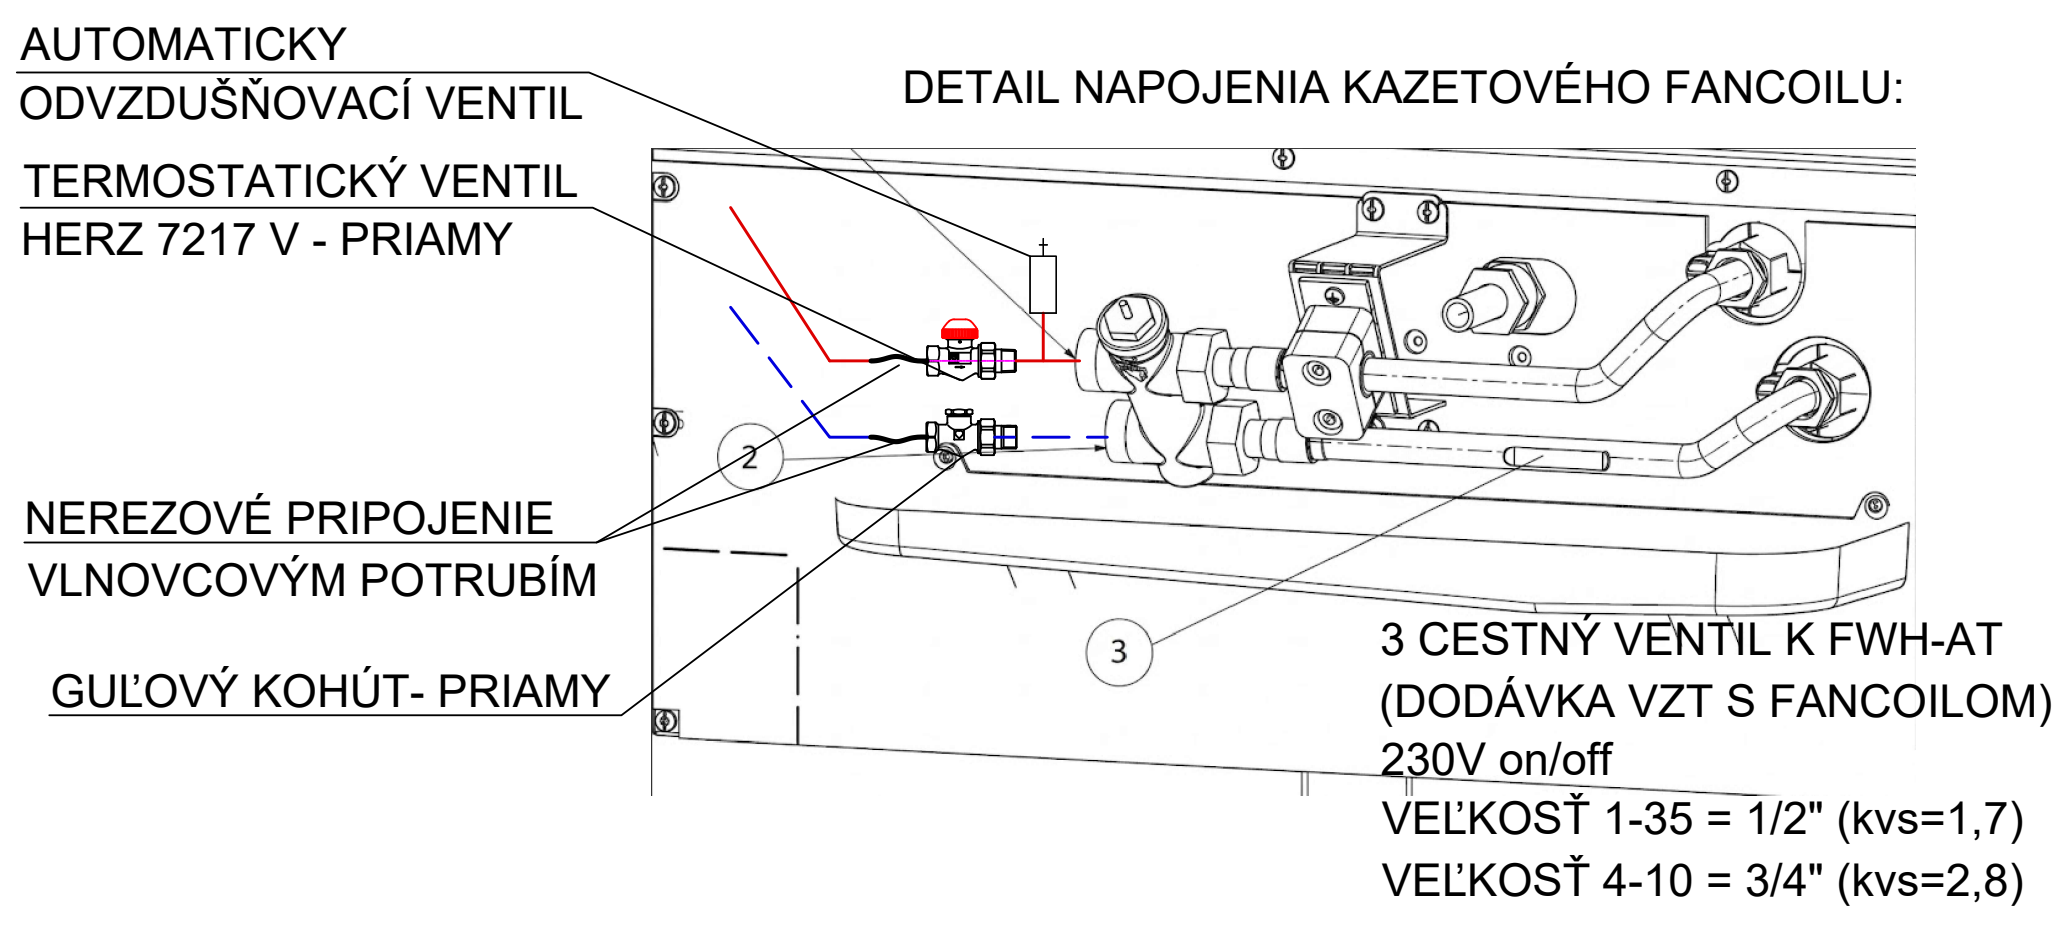
AUTOMATICKY ODVZDUŠŇOVACÍ VENTIL
TERMOSTATICKÝ VENTIL HERZ 7217 V - PRIAMY
NEREZOVÉ PRIPOJENIE VLNOVCOVÝM POTRUBÍM
GUĽOVÝ KOHÚT- PRIAMY

DETAIL NAPOJENIA KAZETOVÉHO FANCOILU:

3 CESTNÝ VENTIL K FWH-AT
(DODÁVKA VZT S FANCOILOM)
230V on/off
VEĽKOSŤ 1-35 = 1/2" (kvs=1,7)
VEĽKOSŤ 4-10 = 3/4" (kvs=2,8)

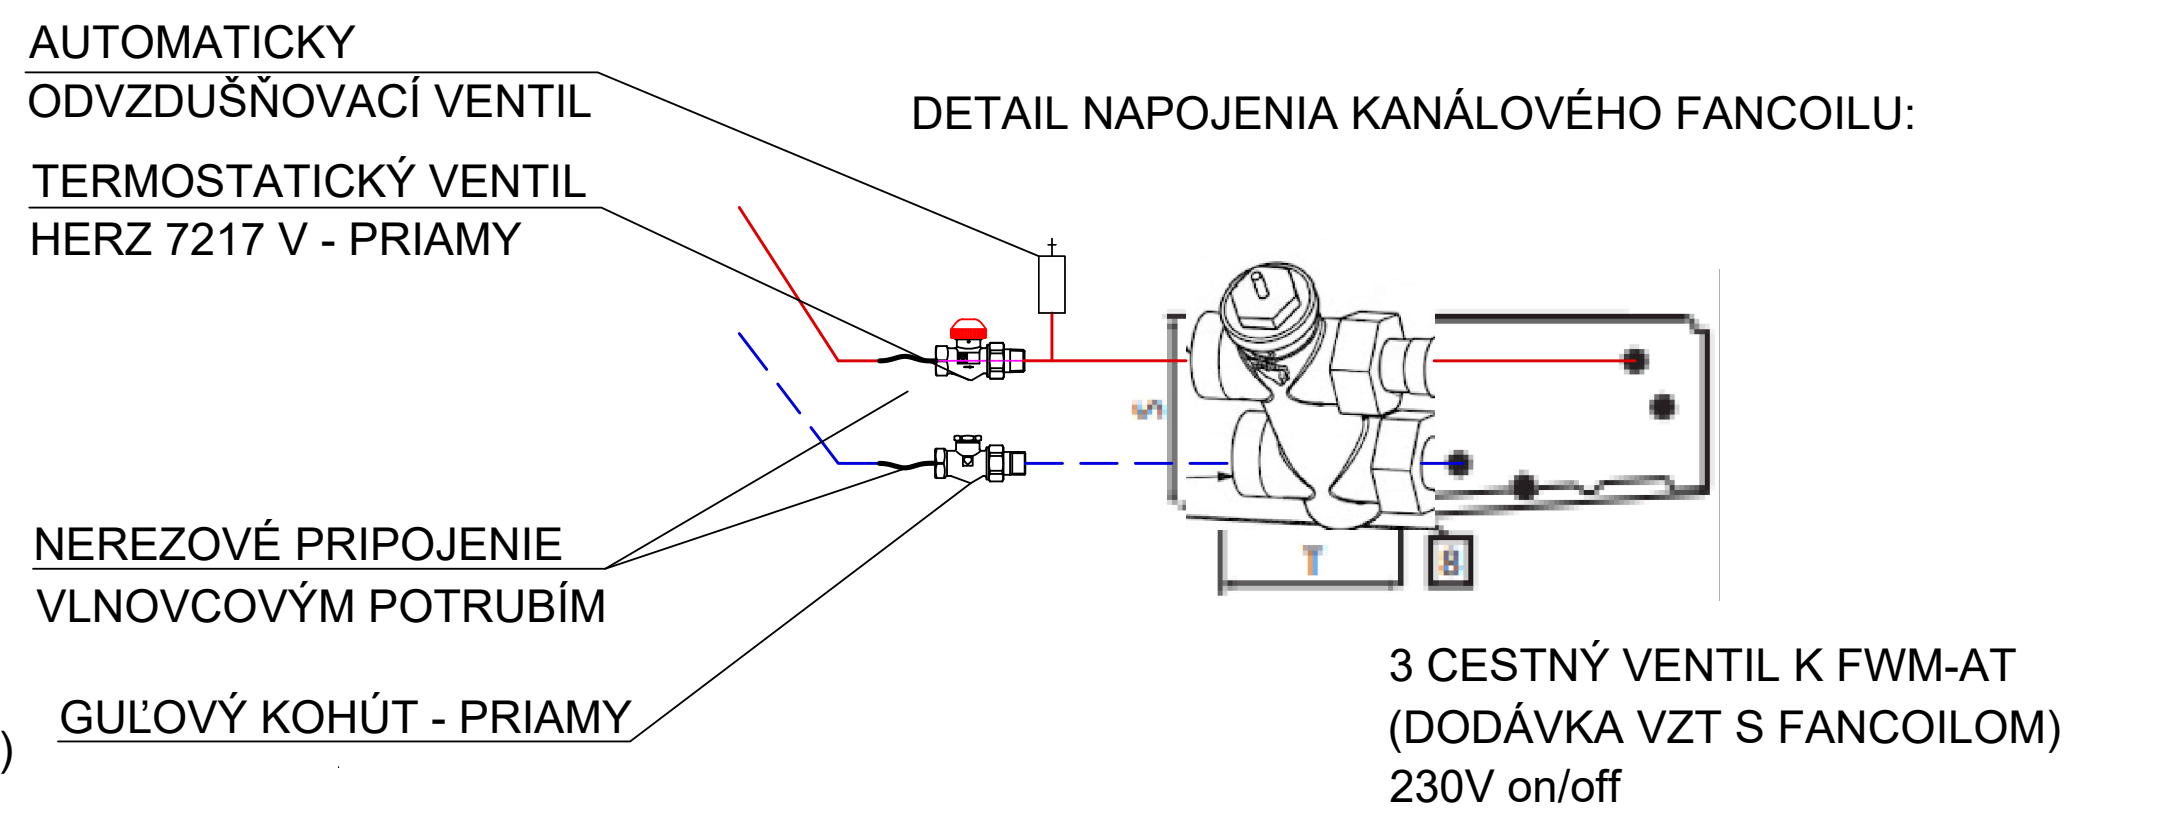
AUTOMATICKY ODVZDUŠŇOVACÍ VENTIL
TERMOSTATICKÝ VENTIL HERZ 7217 V - PRIAMY
NEREZOVÉ PRIPOJENIE VLNOVCOVÝM POTRUBÍM
GUĽOVÝ KOHÚT - PRIAMY

DETAIL NAPOJENIA KANÁLOVÉHO FANCOILU:

3 CESTNÝ VENTIL K FWM-AT
(DODÁVKA VZT S FANCOILOM)
230V on/off
VEĽKOSŤ 1-35 = 1/2" (kvs=1,7)
VEĽKOSŤ 4-10 = 3/4" (kvs=2,8)

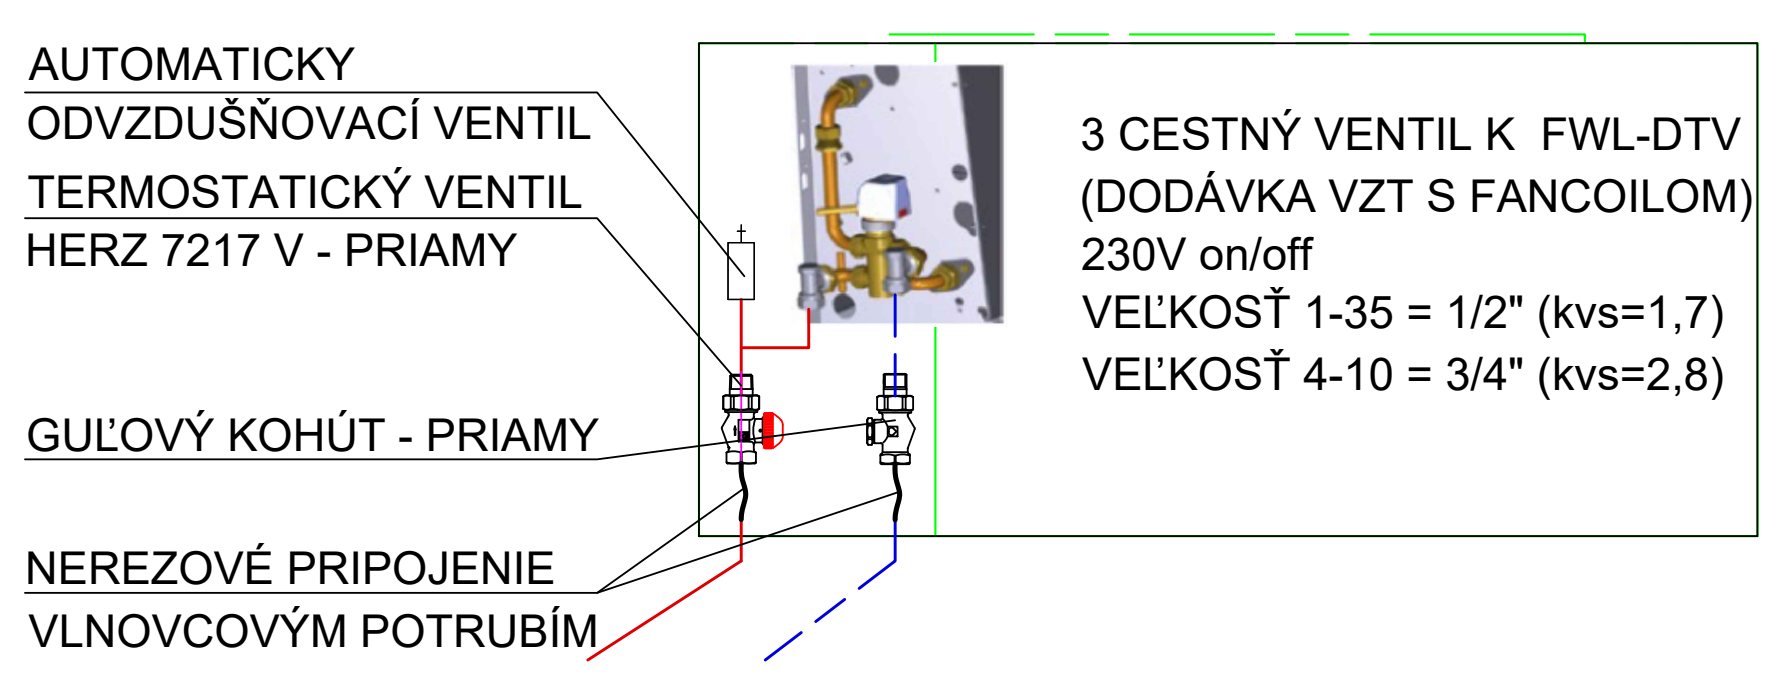
AUTOMATICKY ODVZDUŠŇOVACÍ VENTIL
TERMOSTATICKÝ VENTIL HERZ 7217 V - PRIAMY
GUĽOVÝ KOHÚT - PRIAMY
NEREZOVÉ PRIPOJENIE VLNOVCOVÝM POTRUBÍM

DETAIL NAPOJENIA PARAPETNÉHO FANCOILU:

3 CESTNÝ VENTIL K FWL-DTV
(DODÁVKA VZT S FANCOILOM)
230V on/off
VEĽKOSŤ 1-35 = 1/2" (kvs=1,7)
VEĽKOSŤ 4-10 = 3/4" (kvs=2,8)

LEGENDA:

- VYKUROVACIE POTRUBIE - NÍZKOUHLÍKOVÉ OCELOVÉ POTRUBIE TEPLOTNÝ SPÁD 60/50 °C HLAVNÝ ROZVOD Z TEPELNÉHO ČERPADLA
- VYKUROVACIE POTRUBIE - NÍZKOUHLÍKOVÉ OCELOVÉ POTRUBIE TEPLOTNÝ SPÁD 60/50 °C HLAVNÝ ROZVOD Z AKUMULAČNEJ NÁDRŽE
- VYKUROVACIE POTRUBIE - PLASTOHLÍKOVÉ/NÍZKOUHLÍKOVÉ OCELOVÉ POTRUBIE TEPLOTNÝ SPÁD 45/40 °C PRE NAPOJENIE RADIATOROV
- VYKUROVACIE POTRUBIE - PLASTOHLÍKOVÉ POTRUBIE/NÍZKOUHLÍKOVÉ OCELOVÉ POTRUBIE TEPLOTNÝ SPÁD 45/40 °C
- EXPANZNÉ POTRUBIE
- DOSKOVÉ VYKUROVACIE TELESO
- STÚPANIE/KLESANIE POTRUBIA
- PARAPETNÁ FANCOIL JEDNOTKA
- KANÁLOVÁ VZDUCHOVÁ JEDNOTKA
- KAZETOVÁ STROPNÁ FANCOIL JEDNOTKA

LEGENDA VYKUROVACÍCH OKRUHOV:

UK1 - Prevádzka kancelárie 4.NP Fancoil
UK2 - Prevádzka Aula Fancoil
UK3 - Prevádzka škola Sever Fancoil
UK4 - Prevádzka škola Juh Fancoil
UK5 - Prevádzka škola Radiatory

LEGENDA POPISOVÝCH TABULIEK:

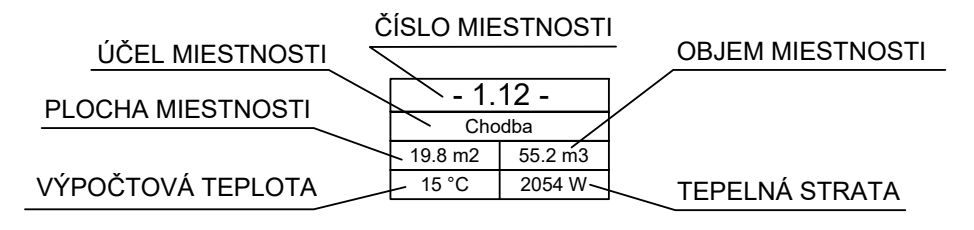

±0,000 = ÚROVEŇ PODLAHY 1.NP

SADA ČÍSLO

Objednávateľ:	Trenčiansky samosprávny kraj, K dolnej stanici 7282/20A, 911 01 Trenčín, Trenčianska univerzita Alexandra Dubčeka v Trenčíne, Študentská 2, 911 50 Trenčín
Generálny projektant:	Arch Konstrukt s.r.o., J. Braneckého 179/14, 911 01 Trenčín
Kontroloval:	Ing. Ján Bátor
Vypracoval:	Ing. J. Bátor, Ing. V. Labovský
Kraj:	Trenčiansky
Okres:	Púchov
Obec:	Púchov
Investor:	Trenčiansky samosprávny kraj, K dolnej stanici 7282/20A, 911 01 Trenčín, Trenčianska univerzita Alexandra Dubčeka v Trenčíne, Študentská 2, 911 50 Trenčín
Miesto stavby:	k.ú Horné Kočkovce, p.č.1509/1, 1510/1, 1527, 1528, 1529/1, 1529/2, 1530/1, 1533, 1535, 1548/2, 1548/4, 1548/5, 1548/6,
Stupeň PD:	DOKUMENTÁCIA PRE STAVEBNÉ POVOLENIE
Akcia:	EDU-TECH KAMPUS PÚCHOV
Objekt:	SO 201 FPT TnUAD
Obsah:	Pôdorys 4.NP
Dátum:	7/2026
Stupeň:	DSP
	Vykurovanie
Formát:	30xA4
Mierka:	1 : 50
Výkres:	04

ARCH KONSTRUKT
J. Braneckého 179/14, 911 01 Trenčín
tel. 0907/146 508
www.archkonstrukt.sk
email: filina@archkonstrukt.sk