
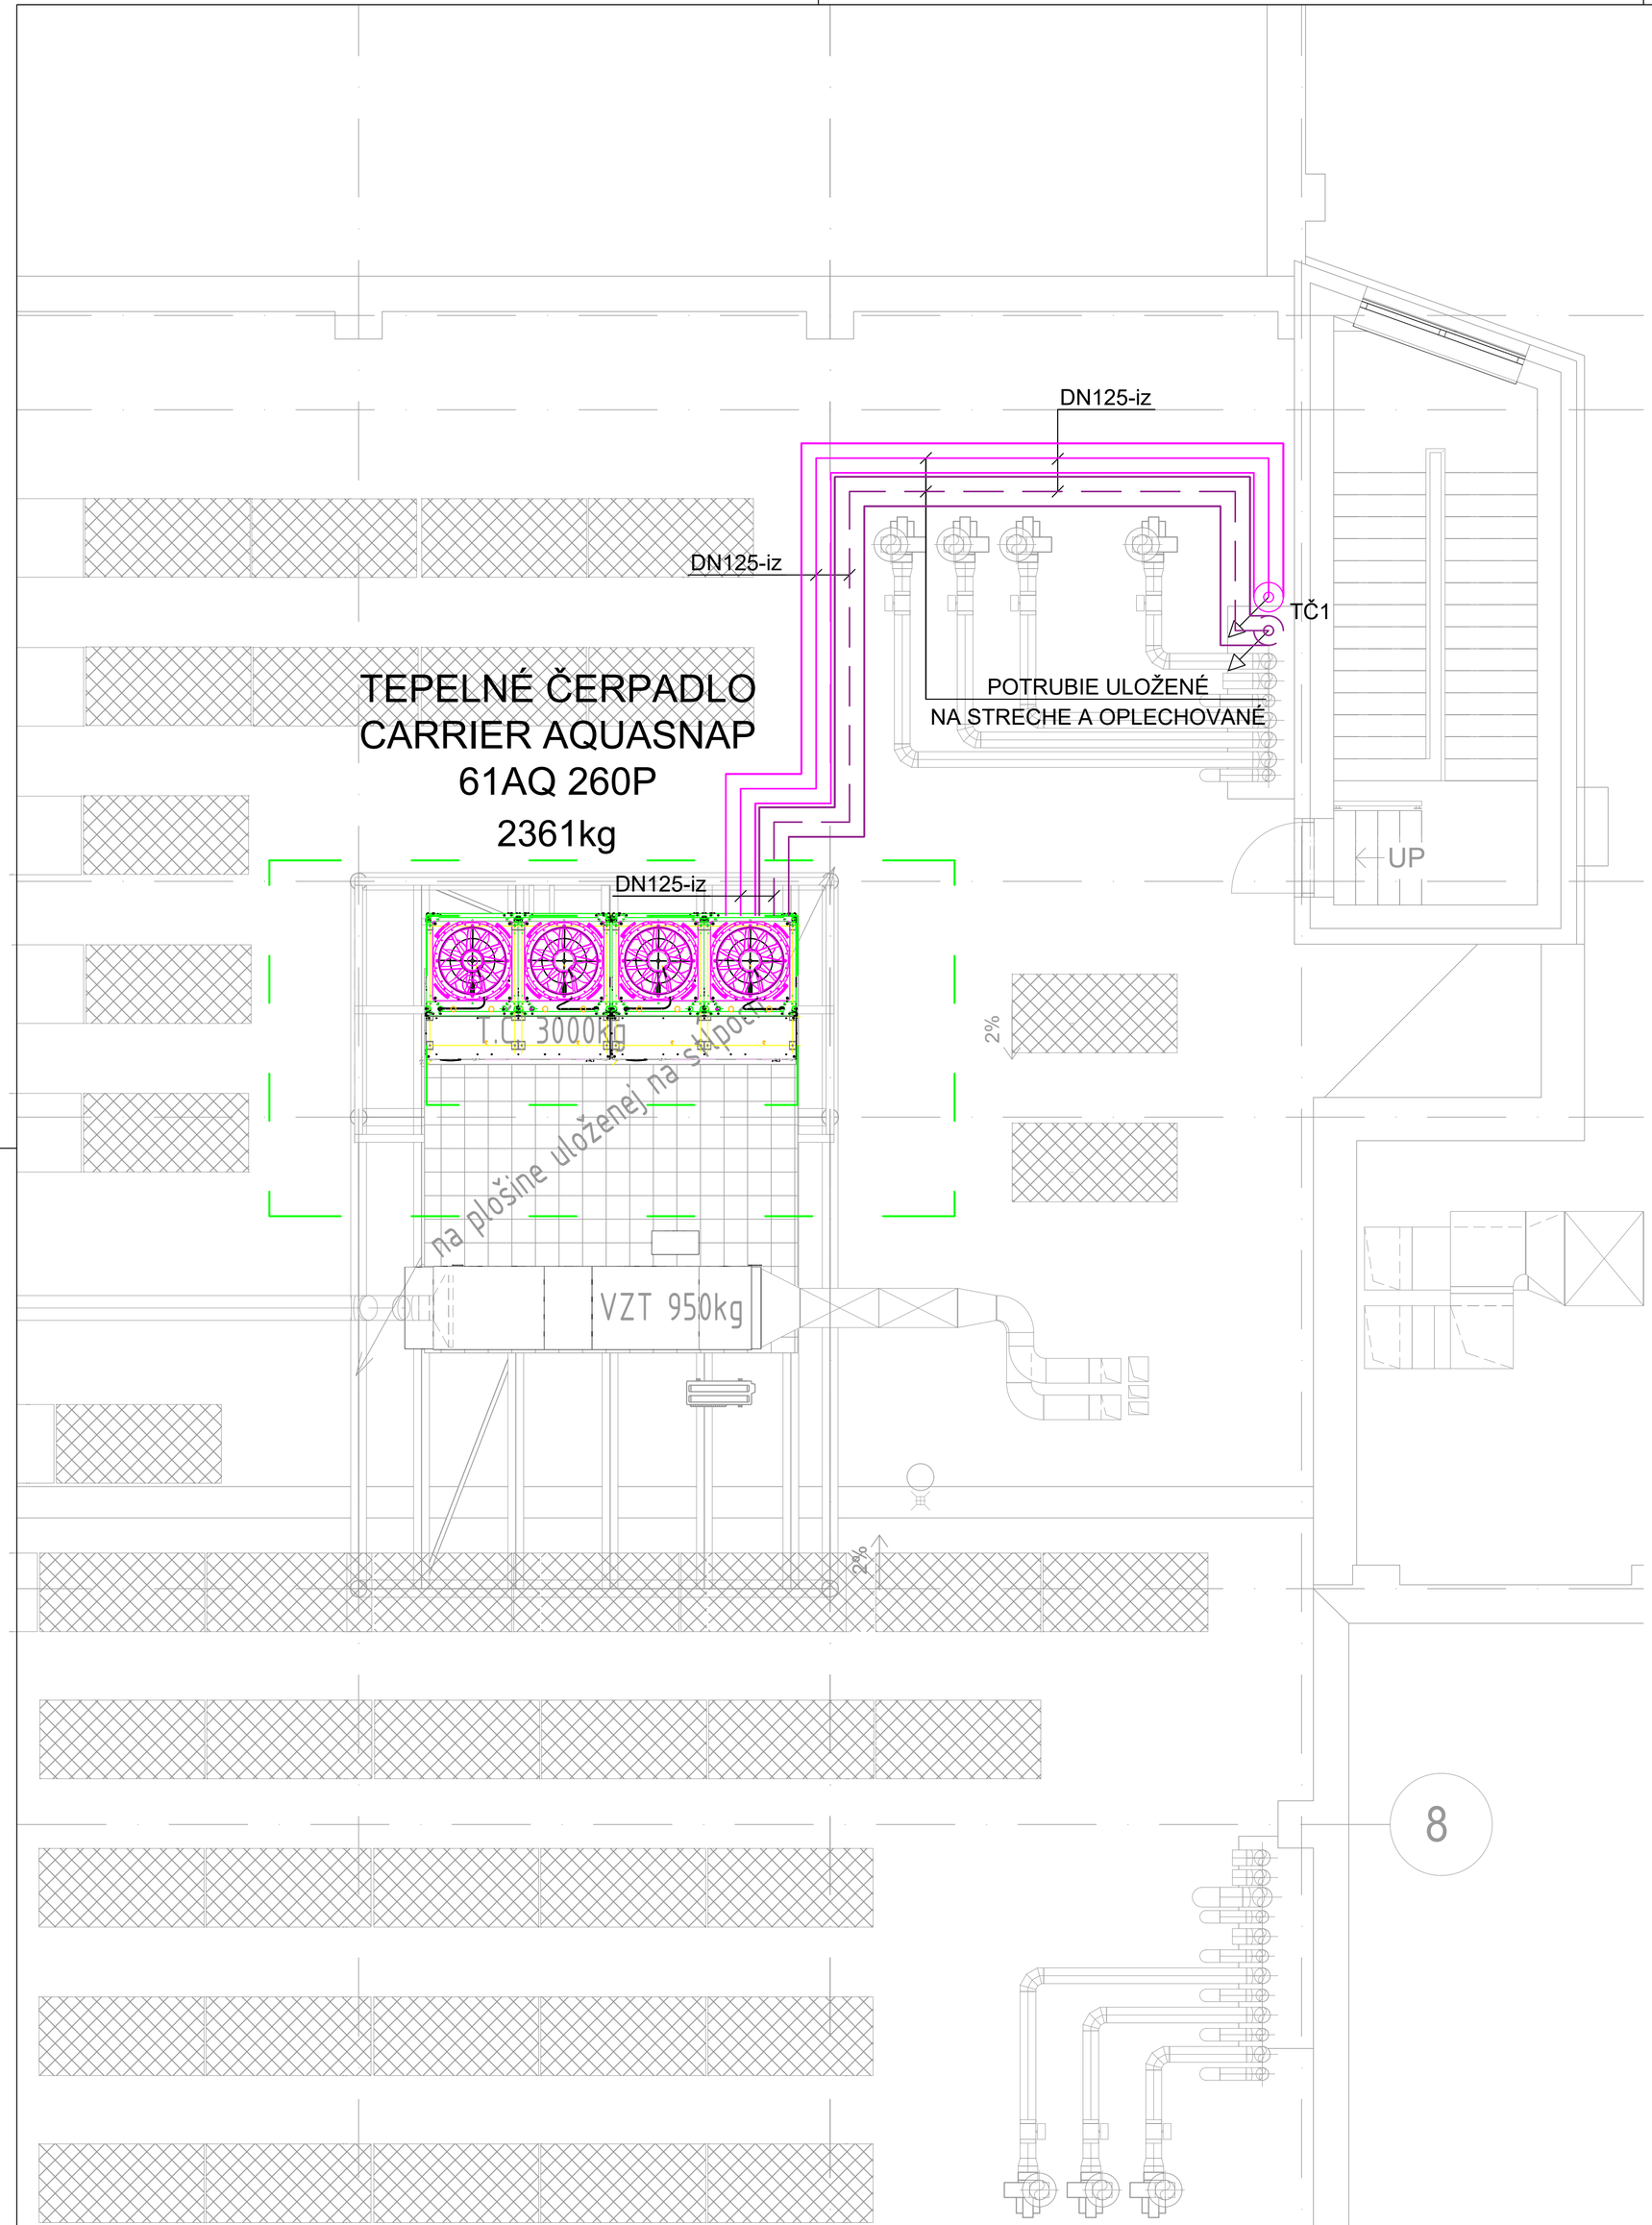


LEGENDA:

VYK. POTRUBIE NÍZKOUHLÍKOVÉ OCELOVÉ POTRUBIE - VETVA TEPELNÉ ČERPADLO TEPLOTNÝ SPÁD 60/50 °C

OCHRANNÉ PÁSMO TEPELNÉHO ČERPADLA

REZ ZAPOJENIA TČ:

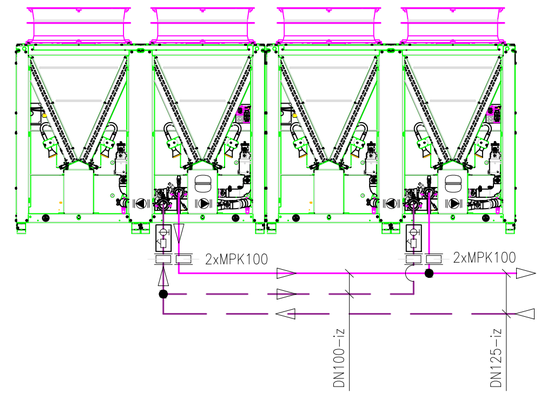

POZNÁMKY:

TEPELNÁ IZOLÁCIA A OPLECHOVANIE: Potrubie DN125 v exteriéri izolovať tepelnou izoláciou zo syntetického kaučuku. Pre zamedzenie tepelných strát a zamrznutia musí byť hrúbka izolácie min. 125 mm. Povrchová ochrana izolácie potrubí riešiť ako falcované exteriérové oplechovanie z hliníkového plechu (hr. min. 0,8 mm), všetky spoje a presahy musia byť vodotesne pretmelené trvalo pružným UV stabilným tmelom.

PROTIZÁMRZNÁ OCHRANA: Ako ochranu proti zamrznutiu pri výpadku prietoku inštalovať pod tepelnú izoláciu na celú dĺžku exteriérového vedenia samoregulačný elektrický vykurovací kábel. Spínanie zabezpečené priestorovým termostatom pri poklese vonkajšej teploty pod +3 °C.

ODVZDUŠNENIE: V najvyšších bodoch exteriérovej trasy inštalovať mrazuvzdorné automatické odvzdušňovacie ventily. Každý ventil musí byť oddeliteľný servisným guľovým kohútom a kompletne schovaný pod tepelnou izoláciou a oplechovaním (s odnímateľným revíznym krytom).

ULOŽENIE TECHNOLÓGIE: TČ Carrier osadiť na systémovú plošinu pre ploché strechy uloženej na stĺpoch. Plošina musí byť separovaná od strešnej krytiny antivibračnými prvkami.

ULOŽENIE POTRUBIA: Trasovanie po streche viesť výlučne na výškovo nastaviteľných strešných podstavcoch. Je prísne zakázaný priamy kontakt potrubia so strešným plášťom. Prechod potrubí do interiéru cez strešný plášť riešiť certifikovanou systémovou prechodovou manžetou s garanciou trvalej vodotesnosti.

±0,000 = ÚROVEŇ PODLAHY 1.NP

SADA ČÍSLO

Objednávateľ: Trenčiansky samosprávny kraj, K dolnej stanici 7282/20A, 911 01 Trenčín, Trenčianska univerzita Alexandra Dubčeka v Trenčíne, Študentská 2, 911 50 Trenčín	
Generálny projektant: Arch Konstrukt s.r.o., J. Braneckého 179/14, 911 01 Trenčín	
Kontroloval: Ing. Ján Bátor	Vypracoval: Ing. J. Bátor, Ing. V. Labovský
Kraj: Trenčiansky / Okres: Púchov	Obec: Púchov
Investor: Trenčiansky samosprávny kraj, K dolnej stanici 7282/20A, 911 01 Trenčín, Trenčianska univerzita Alexandra Dubčeka v Trenčíne, Študentská 2, 911 50 Trenčín	
Miesto stavby: k.ú Horné Kočkovce, p.č.1509/1, 1510/1, 1527, 1528, 1529/1, 1529/2, 1530/1, 1533, 1535, 1548/2, 1548/4, 1548/5, 1548/6,	
Stupeň PD: DOKUMENTÁCIA PRE STAVEBNÉ POVOLENIE Akcia: EDU-TECH KAMPUS PÚCHOV Objekt: SO 201 FPT TnUAD	
Obsah: Výkres strechy	

ARCH KONSTRUKT
J. Braneckého 179/14, 911 01 Trenčín
tel. 0907/146 508
www.archkonstrukt.sk
email: filina@archkonstrukt.sk

Dátum: 7/2026	Stupeň: DSP
Vykurovanie	Formát: 6xA4
Mierka: 1 : 50	Výkres: 05