VETVA RADIATORY

65
63
62
64
66
67
68
69
61
60
PP
RADIATORY

VETVA 4.NP

LEGENDA:

	VYK. POTRUBIE NÍZKOUHLÍKOVÉ OCELOVÉ/PLASTOHLINÍKOVÉ POTRUBIE
	VYK. POTRUBIE NÍZKOUHLÍKOVÉ OCELOVÉ/PLASTOHLINÍKOVÉ POTRUBIE, RADIATOROVÉ
PP	POŽIARNY PRESTUP

DETAIL NAPOJENIA KANÁLOVÉHO FANCOILU:

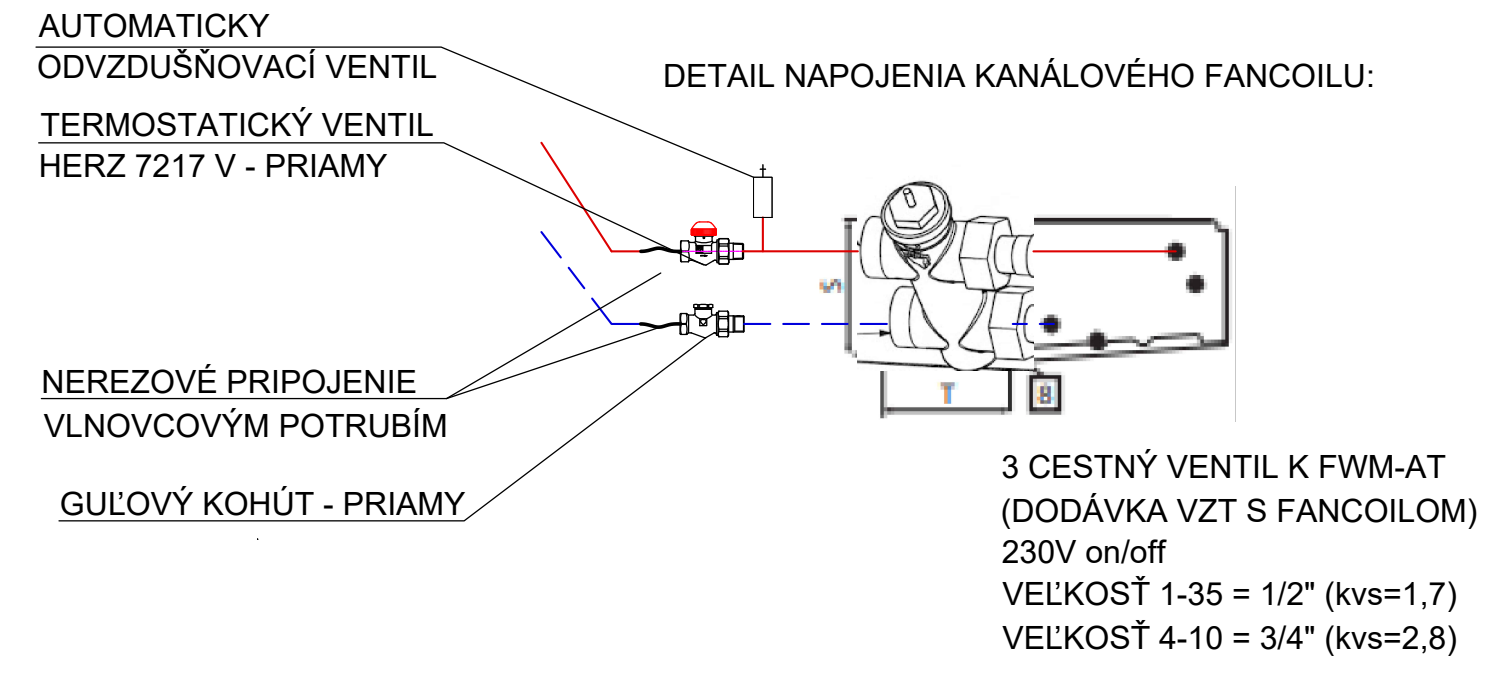
AUTOMATICKY ODVZDUŠŇOVACÍ VENTIL
TERMOSTATICKÝ VENTIL HERZ 7217 V - PRIAMY
NEREZOVÉ PRIPOJENIE VLNOVCOVÝM POTRUBÍM
GUĽOVÝ KOHÚT - PRIAMY

3 CESTNÝ VENTIL K FWM-AT
(DODÁVKA VZT S FANCOILOM)
230V on/off
VEĽKOSŤ 1-35 = 1/2" (kvs=1,7)
VEĽKOSŤ 4-10 = 3/4" (kvs=2,8)

DETAIL NAPOJENIA KAZETOVÉHO FANCOILU:

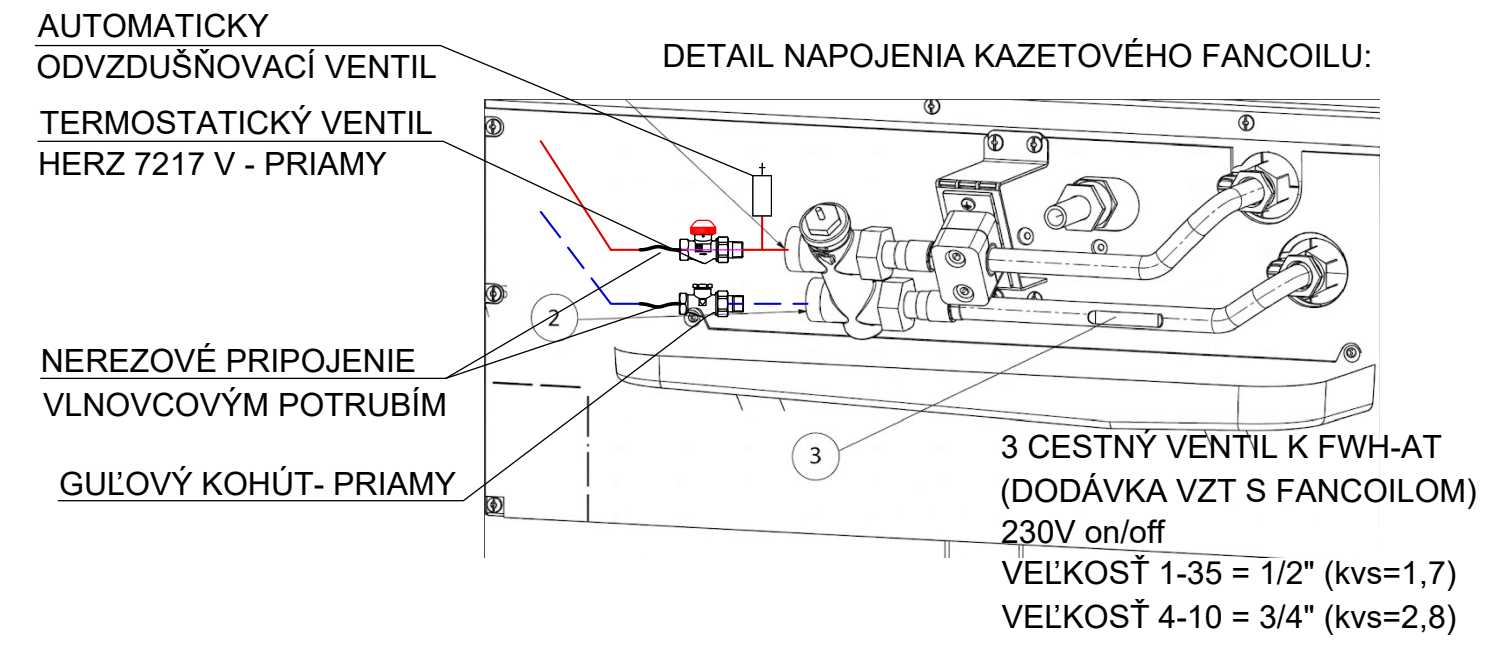
AUTOMATICKY ODVZDUŠŇOVACÍ VENTIL
TERMOSTATICKÝ VENTIL HERZ 7217 V - PRIAMY
NEREZOVÉ PRIPOJENIE VLNOVCOVÝM POTRUBÍM
GUĽOVÝ KOHÚT- PRIAMY
2
3

3 CESTNÝ VENTIL K FWH-AT
(DODÁVKA VZT S FANCOILOM)
230V on/off
VEĽKOSŤ 1-35 = 1/2" (kvs=1,7)
VEĽKOSŤ 4-10 = 3/4" (kvs=2,8)

DETAIL NAPOJENIA PARAPETNÉHO FANCOILU:

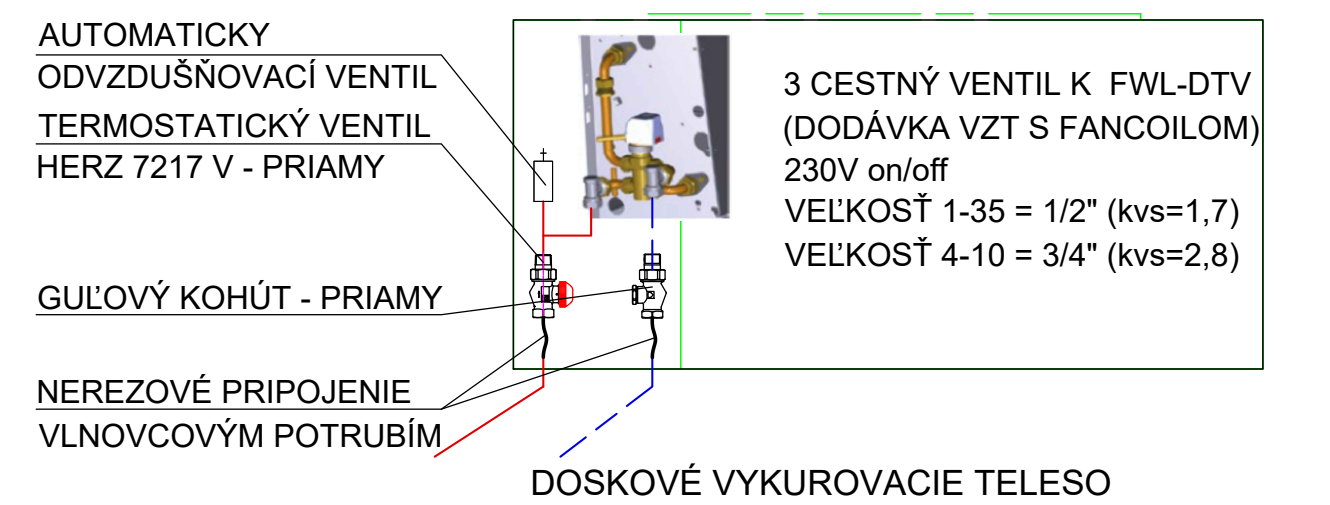
AUTOMATICKY ODVZDUŠŇOVACÍ VENTIL
TERMOSTATICKÝ VENTIL HERZ 7217 V - PRIAMY
GUĽOVÝ KOHÚT - PRIAMY
NEREZOVÉ PRIPOJENIE VLNOVCOVÝM POTRUBÍM

3 CESTNÝ VENTIL K FWL-DTV
(DODÁVKA VZT S FANCOILOM)
230V on/off
VEĽKOSŤ 1-35 = 1/2" (kvs=1,7)
VEĽKOSŤ 4-10 = 3/4" (kvs=2,8)

DOSKOVÉ VYKUROVACIE TELESO

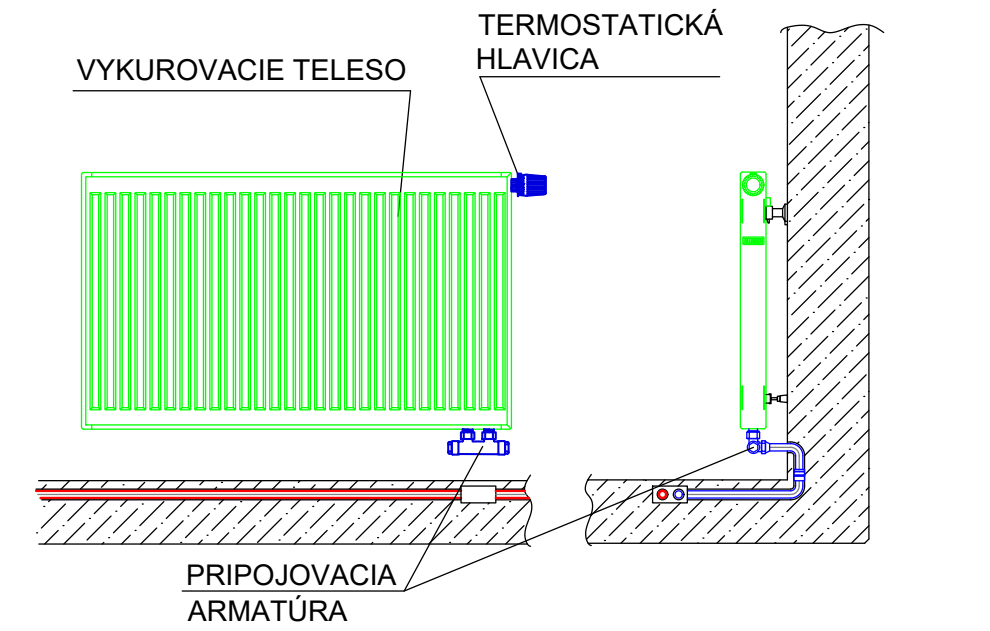
VYKUROVACIE TELESO
TERMOSTATICKÁ HLAVICA
PRIPOJOVACIA ARMATÚRA

LEGENDA OSADENIA REGULÁCIE NA PÄTE STÚPAČKY:

GK - Guľový kohút
VK - Vypúšťací kohút DN15
RTD - Regulátor tlakovej diferencie
PTV - Partnerský vyvažovací ventil Herz Stromax GM 2013 - závit Rp

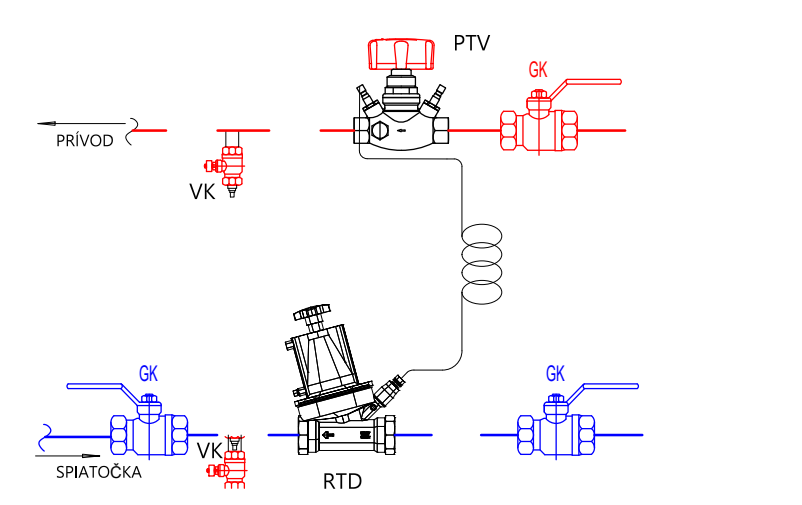
PTV
GK
PRÍVOD
VK
GK
GK
VK
SPIATOČKA
RTD

POZNÁMKY:

POTRUBIA A SPÁDOVANIE - Všetky potrubia ÚK a chladenia spádovať v smere prúdenia k najnižším bodom systému pod spádom min. 0,2 %. V najvyšších bodoch rozvodov osadiť automatické odvzdušňovacie ventily, v najnižších bodoch vypúšťacie kohúty s hadicovým nástavcom.

TEPELNÁ IZOLÁCIA POTRUBIA- Všetky potrubné rozvody tepla/chladu celoplošne a súvisle zaizolovať parotesnou elastomérnou izoláciou na báze syntetického kaučuku. Hrúbka izolácie musí byť dimenzovaná podľa priemeru potrubia v zmysle vyhlášky č. 14/2016 Z. z. (minimálne hrúbky pre vykurovanie) a zároveň musí bezpečne zabrániť vzniku kondenzátu v režime chladenia (min. hrúbka 13 mm pre DN 15–25, min. 19 mm pre DN 32 a väčšie, resp. podľa výpočtu pre dané prostredie).

FANCOILOVÉ JEDNOTKY A ZAPOJENIE - Pred montážou fancoilových jednotiek skontrolovať presný typ, výkon a orientáciu pripojenia podľa PD a dodávky stavby. Pripojenie fancoilu na pevné potrubné rozvody vyhotoviť pomocou nerezových vlnovcových potrubí z dôvodu eliminácie prenosu vibrácií a hluku do potrubnej siete. Pred každou fancoilovou jednotkou osadiť armatúry podľa PD.

SADA ČÍSLO

±0,000 = ÚROVEŇ PODLAHY 1.NP

Objednávateľ: Trenčiansky samosprávny kraj, K dolnej stanici 7282/20A, 911 01 Trenčín,
Trenčianska univerzita Alexandra Dubčeka v Trenčíne, Študentská 2, 911 50 Trenčín
Generálny projektant: Arch Konstrukt s.r.o., J. Braneckého 179/14, 911 01 Trenčín
Kontroloval: Ing. Ján Bátor
Vypracoval: Ing. J. Bátor, Ing. V. Labovský
Kraj: Trenčiansky
Okres: Púchov
Obec: Púchov
Investor: Trenčiansky samosprávny kraj, K dolnej stanici 7282/20A, 911 01 Trenčín,
Trenčianska univerzita Alexandra Dubčeka v Trenčíne, Študentská 2, 911 50 Trenčín
Miesto stavby: k.ú Horné Kočkovce, p.č.1509/1, 1510/1, 1527, 1528, 1529/1, 1529/2, 1530/1, 1533, 1535, 1548/2, 1548/4, 1548/5, 1548/6,
Stupeň PD: DOKUMENTÁCIA PRE STAVEBNÉ POVOLENIE
Akcia: EDU-TECH KAMPUS PÚCHOV
Objekt: SO 201 FPT TnUAD
Obsah: Schéma rozvodov ÚK

ARCH KONSTRUKT

J. Braneckého 179/14, 911 01 Trenčín
tel. 0907/146 508
www.archkonstrukt.sk
email: filina@archkonstrukt.sk

Dátum: 7/2026
Stupeň: DSP
Vykurovanie
Formát: 51xA4
Mierka:
Výkres: 08