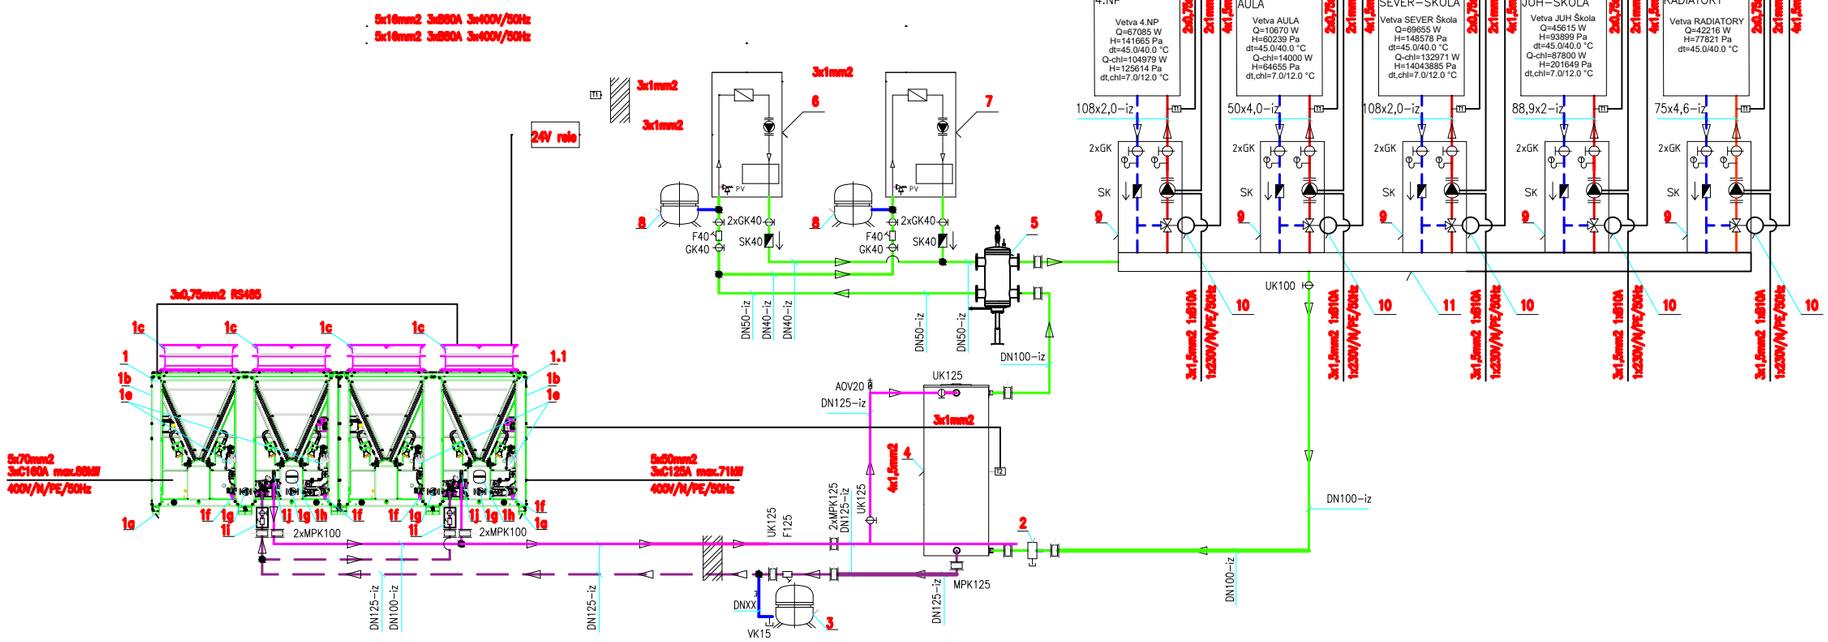


LEGENDA ZARIADENÍ:

POZ.	NÁZOV, ROZMER	P. KS
	TEPELNÉ ČERPADLO CARRIER 61AQ 260P skladá sa z dvoch modulov:	1
1	TEPELNÉ ČERPADLO CARRIER 61AQ 160P	
1.1	TEPELNÉ ČERPADLO CARRIER 61AQ 100P	
	MAX. VÝSTUPNÁ TEPLOTA 75°C, CHLADIVO R290 GWP3	
	VYK.VÝKON 30,5–197kW (A–7/W45)	
	CHLAD.VÝKON 26,9–105kW (A35/W7)	
1a	ANTIVIBRAČNE BLOKY – SILENT BLOKY – SADA opcia 308	–
1b	REGULÁCIA TEP.ČERPADLA SmartVu – v rozsahu dodávky pol.1	–
1c	EC–ELEKTRONICKY RIADENY VENTILÁTOR – v rozsahu dodávky pol.1	–
1d	SNÍMAČ VONKAJŠEJ TEPLOTY – opcia 312	–
1e	ODLUČOVAČ CHLADIVA PROPÁN S ODVZDUŠNOVACÍM VENTILOM – v rozsahu dodávky pol.1	–
1f	TERMOSTATICKÝ VENTIL PROTI ZAMRZNUTIU – v rozsahu dodávky pol.1	–
1g	OBEHOVÉ ČERPADLO S REGULÁCIOU OTÁČOK – opcia 116V	–
1h	EXPANZNÁ NÁDOBA OBJEM 8L – opcia 116V	–
1i	SADA FILTRA NA SYSTEM (treba namontovať) – v rozsahu dodávky pol.1	–
1j	POISTNÝ VENTIL PRE SYSTÉM 4bar – v rozsahu dodávky pol.1	–
2	ODLUČOVAČ SPIROTRAP S MAGNETOM DN100 PRÍRUBOVÝ (7784181)	3
3	EXPANZNÁ NÁDOBA N300, OBJEM 300L, 6bar STRIEBORNÁ	1
4	AKUM.ZÁSOBNÍK PRE UK VITOCELL 050–HC EC PRO SH2010HA OBJEM 2010L (Z028042)	1
5	HYDRAULIC.VYROVNÁVAČ TLAKOV S IZOLÁCIOU	1
6	ZÁVESNÝ ELEKTROKOTOL TYP EKCO.TM 16–48 kW (Z021557)	1
7	ZÁVESNÝ ELEKTROKOTOL TYP EKCO.T 16–48 kW (Z021561)	2
8	EXPANZNÁ NÁDOBA H25, OBJEM 25, 3bar BIELA (7938082)	1
9	RÝCHLOMONTÁŽNA SADA M32 SO ZMIEŠAVACOM DN50 MAGNA3 50–80F (ZK01668)	1
10	SERVOPOHON SR10 230V/50Hz (7199567)	1
11	MODULÁRNY ROZDEĽOVAČ PRE 5 OKRUHOV DN100	1
15		2
16		1
17		2
T1	SNÍMAČ VÝSTUPNEJ TEPLOTY (7426463)	5
T2	SNÍMAČ TEPLOTY ZÁSOBNÍKA – dodávka kaskádovej regulácie tep.čerpadiel	1
T3	SNÍMAČ TEPLOTY ZÁSOBNÍKA – opcia 312A	1
T4	SNÍMAČ VONKAJŠEJ TEPLOTY – v rozsahu dodávky pol.17	1
T5	SNÍMAČ TEPLOTY HYDRAULICKEJ VÝHYBKY – existujúci	1
T6	PONORNÝ SNÍMAČ TEPLOTY (7438702)	1

LEGENDA:

- VYKUROVACIE POTRUBIE - NÍZKOUHLÍKOVÉ OCELOVÉ POTRUBIE TEPLOTNÝ SPÁD 60/50 °C -VETVA TEPELNÉ ČERPADLO
- VYKUROVACIE POTRUBIE - NÍZKOUHLÍKOVÉ OCELOVÉ POTRUBIE TEPLOTNÝ SPÁD 60/50 °C -VETVA TEPELNÉ ČERPADLO Z AKUMULÁCIE
- VYKUROVACIE POTRUBIE - NÍZKOUHLÍKOVÉ OCELOVÉ POTRUBIE TEPLOTNÝ SPÁD 42/35 °C
- EXPANZNÉ POTRUBIE

±0,000 = ÚROVEŇ PODLAHY 1.NP

SADA ČÍSLO

Objednávateľ: Trenčiansky samosprávny kraj, K dolnej stanici 7282/20A, 911 01 Trenčín,
Trenčianska univerzita Alexandra Dubčeka v Trenčíne, Študentská 2, 911 50 Trenčín

Generálny projektant: Arch Konstrukt s.r.o., J. Braneckého 179/14, 911 01 Trenčín

Kontroloval: Ing. Ján Bátor | Vypracoval: Ing. J. Bátor, Ing. V. Labovský

Kraj: Trenčiansky | Okres: Púchov | Obec: Púchov

Investor: Trenčiansky samosprávny kraj, K dolnej stanici 7282/20A, 911 01 Trenčín,
Trenčianska univerzita Alexandra Dubčeka v Trenčíne, Študentská 2, 911 50 Trenčín

Miesto stavby: k.ú Horné Kočkovce, p.č.1509/1, 1510/1, 1527, 1528, 1529/1, 1529/2, 1530/1, 1533, 1535, 1548/2, 1548/4, 1548/5, 1548/6,

Stupeň PD: DOKUMENTÁCIA PRE STAVEBNÉ POVOLENIE

Akcia: EDU-TECH KAMPUS PÚCHOV

Objekt: SO 201 FPT TnUAD

Obsah: Schéma zapojenia

ARCH KONSTRUKT
J. Braneckého 179/14, 911 01 Trenčín
tel. 0907/146 508
www.archkonstrukt.sk
email: filina@archkonstrukt.sk

Dátum: 7/2026	Stupeň: DSP
Vykurovanie	Formát: 2xA4
Mierka: 1 : 50	Výkres: 06