## LEGENDA PODLAHOVÉHO VYKUROVANIA:

PODLAHOVÉ KÚRENIE REHAU

| | |
|---|---|
| Lpz=100 [mm] | ROZOSTUP VYK. RÚROK |
| S=8,6 m2 | VYKUROVACIA PLOCHA |
| PX: Keramická dlažba | TYP NÁŠLAPNEJ VRSTVY |
| Rúrka RAUTHERM S 17x2,0 | TYP VYKUROVACEJ RÚRKY |
| Nast.=0,63 (48 kg/h) | NASTAVENIE REG. OKRUHU(PRIETOK) |
| lo/lp=12.7 m/1.6 m | Dĺžka okruhu / dĺžka prípojky |
| RZ 1. NP-1/9 (tp=45°C) | rozdelovač na 1.NP 1. napojenie a |
| VARIONOVA | 9 vetiev ( tp - teplota prívodu) |
| PZ:21°C | typ prichytenia potrubi pre podlahove kurenie<br>maximálna povrchová teplota podlahovej zóny |

### RZ 1 - 1. NP (9)

ROZDELOVACIA STANICA PRE PODLAHOVÉ VYKUROVANIE 45/35°C
NAPR. FY. REHAU HKV-D 9, SKRINKA ROZDELOVAČA NA STENU AP 130/805 (805x730x130mm)
REGULAČNÝ ROZVÁDZAČ REHAU NEA (230V) (1ks)
PRIESTOROVÝ TERMOSTAT REHAU NEA (230V) (2ks)
ELEKTRICKÝ SERVOPOHON REHAU (230V) (9ks)

### RZ 2 - 1. NP (4)

ROZDELOVACIA STANICA PRE PODLAHOVÉ VYKUROVANIE 45/35°C
NAPR. FY. REHAU HKV-D 4, SKRINKA ROZDELOVAČA NA STENU AP 130/605 (605x730x130mm)
REGULAČNÝ ROZVÁDZAČ REHAU NEA (230V) (1ks)
ELEKTRICKÝ SERVOPOHON REHAU (230V) (4ks)


| - 1.01 - | |
|---|---|
| Vstup | |
| 2.0 m2 | 5.8 m3 |
| 20 °C | 136 W |
| - 1.02 - | |
| Kancelária | |
| 38.4 m2 | 109.2 m3 |
| 22 °C | 1467 W |
| - 1.03 - | |
| Kuchynka | |
| 6.0 m2 | 17.1 m3 |
| 22 °C | 327 W |
| - 1.04 - | |
| WC | |
| 2.5 m2 | 7.1 m3 |
| 22 °C | 129 W |
| - 1.05 - | |
| Sklad | |
| 69.9 m2 | 198.6 m3 |
| 20 °C | 3195 W |
| - 1.06 - | |
| Školiaca miestnosť | |
| 45.7 m2 | 129.9 m3 |
| 22 °C | 1701 W |
| - 1.07 - | |
| Technická miestnosť | |
| 7.3 m2 | 20.8 m3 |
| 24 °C | 541 W |
| - 1.08 - | |
| Sprcha | |
| 1.8 m2 | 5.1 m3 |
| 24 °C | 132 W |

## LEGENDA MIESTNOSTÍ

| Č.MIEST. | POPIS MIESTNOSTI | PLOCHA | PODLAHA | STENY | STROP |
|---|---|---|---|---|---|
| 1.01 | VSTUP | 2,04 m2 | P1 VINYL | INT. NÁTER | PLNÝ SDK PODHLAD |
| 1.02 | KANCELÁRIA | 38,44 m2 | P1 VINYL | INT. NÁTER | PLNÝ SDK PODHLAD |
| 1.03 | KUCHYNKA | 6,03 m2 | P1 VINYL | INT. NÁTER | PLNÝ SDK PODHLAD |
| 1.04 | WC | 2,50 m2 | P3 KERAM. DLAŽBA | KERAM. OBKLAD | PLNÝ SDK PODHLAD |
| 1.05 | SKLAD | 70,68 m2 | P3 EPOXIDOVÁ PODL. | INT. NÁTER | BEZ PODHLADU |
| 1.06 | ŠKOLIACA MIESTNOSŤ | 45,74 m2 | P1 VINYL | INT. NÁTER | PLNÝ SDK PODHLAD |
| 1.07 | TECHNICKÁ MIESTNOSŤ | 7,33 m2 | P3 EPOXIDOVÁ PODL. | INT. NÁTER | PLNÝ SDK PODHLAD |
| 1.08 | SPRCHA | 1,80 m2 | P3 KERAM. DLAŽBA | KERAM. OBKLAD | PLNÝ SDK PODHLAD |
| | | | | | – |

| | |
|---|---|
| CELKOVÁ PLOCHA / TOTAL AREA | 174,56 m2 |

| | | | | | |
|---|---|---|---|---|---|
| 1.09 | TERASA | 29,15 m2 | DREVENÁ TERASA | – | – |

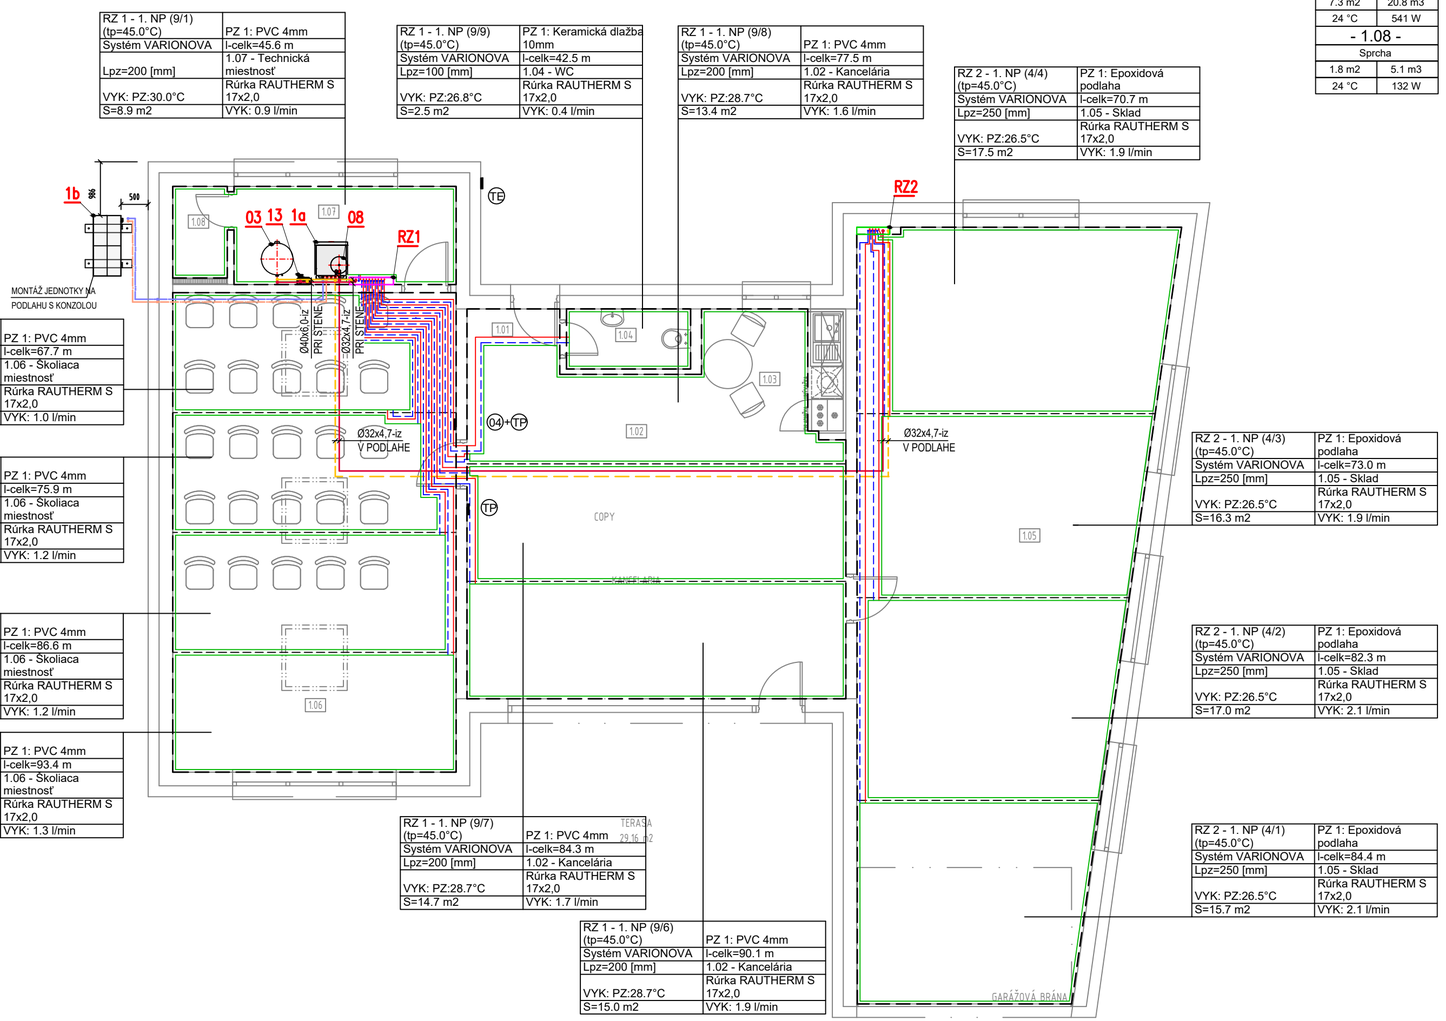


| RZ 1 - 1. NP (9/1) (tp=45.0°C) | PZ 1: PVC 4mm |
|---|---|
| Systém VARIONOVA | l-celk=45.6 m |
| Lpz=200 [mm] | 1.07 - Technická miestnosť |
| VYK: PZ:30.0°C | Rúrka RAUTHERM S 17x2,0 |
| S=8.9 m2 | VYK: 0.9 l/min |

| RZ 1 - 1. NP (9/9) (tp=45.0°C) | PZ 1: Keramická dlažba 10mm |
|---|---|
| Systém VARIONOVA | l-celk=42.5 m |
| Lpz=100 [mm] | 1.04 - WC |
| VYK: PZ:26.8°C | Rúrka RAUTHERM S 17x2,0 |
| S=2.5 m2 | VYK: 0.4 l/min |

| RZ 1 - 1. NP (9/8) (tp=45.0°C) | PZ 1: PVC 4mm |
|---|---|
| Systém VARIONOVA | l-celk=77.5 m |
| Lpz=200 [mm] | 1.02 - Kancelária |
| VYK: PZ:28.7°C | Rúrka RAUTHERM S 17x2,0 |
| S=13.4 m2 | VYK: 1.6 l/min |

| RZ 2 - 1. NP (4/4) (tp=45.0°C) | PZ 1: Epoxidová podlaha |
|---|---|
| Systém VARIONOVA | l-celk=70.7 m |
| Lpz=250 [mm] | 1.05 - Sklad |
| VYK: PZ:26.5°C | Rúrka RAUTHERM S 17x2,0 |
| S=17.5 m2 | VYK: 1.9 l/min |

| RZ 1 - 1. NP (9/2) (tp=45.0°C) | PZ 1: PVC 4mm |
|---|---|
| Systém VARIONOVA | l-celk=67.7 m |
| Lpz=150 [mm] | 1.06 - Školiaca miestnosť |
| VYK: PZ:28.3°C | Rúrka RAUTHERM S 17x2,0 |
| S=8.9 m2 | VYK: 1.0 l/min |

| RZ 1 - 1. NP (9/3) (tp=45.0°C) | PZ 1: PVC 4mm |
|---|---|
| Systém VARIONOVA | l-celk=75.9 m |
| Lpz=150 [mm] | 1.06 - Školiaca miestnosť |
| VYK: PZ:28.3°C | Rúrka RAUTHERM S 17x2,0 |
| S=10.2 m2 | VYK: 1.2 l/min |

| RZ 1 - 1. NP (9/4) (tp=45.0°C) | PZ 1: PVC 4mm |
|---|---|
| Systém VARIONOVA | l-celk=86.6 m |
| Lpz=150 [mm] | 1.06 - Školiaca miestnosť |
| VYK: PZ:28.3°C | Rúrka RAUTHERM S 17x2,0 |
| S=11.1 m2 | VYK: 1.2 l/min |

| RZ 1 - 1. NP (9/5) (tp=45.0°C) | PZ 1: PVC 4mm |
|---|---|
| Systém VARIONOVA | l-celk=93.4 m |
| Lpz=150 [mm] | 1.06 - Školiaca miestnosť |
| VYK: PZ:28.3°C | Rúrka RAUTHERM S 17x2,0 |
| S=11.4 m2 | VYK: 1.3 l/min |

| RZ 1 - 1. NP (9/7) (tp=45.0°C) | PZ 1: PVC 4mm |
|---|---|
| Systém VARIONOVA | l-celk=84.3 m |
| Lpz=200 [mm] | 1.02 - Kancelária |
| VYK: PZ:28.7°C | Rúrka RAUTHERM S 17x2,0 |
| S=14.7 m2 | VYK: 1.7 l/min |

| RZ 1 - 1. NP (9/6) (tp=45.0°C) | PZ 1: PVC 4mm |
|---|---|
| Systém VARIONOVA | l-celk=90.1 m |
| Lpz=200 [mm] | 1.02 - Kancelária |
| VYK: PZ:28.7°C | Rúrka RAUTHERM S 17x2,0 |
| S=15.0 m2 | VYK: 1.9 l/min |

| RZ 2 - 1. NP (4/3) (tp=45.0°C) | PZ 1: Epoxidová podlaha |
|---|---|
| Systém VARIONOVA | l-celk=73.0 m |
| Lpz=250 [mm] | 1.05 - Sklad |
| VYK: PZ:26.5°C | Rúrka RAUTHERM S 17x2,0 |
| S=16.3 m2 | VYK: 1.9 l/min |

| RZ 2 - 1. NP (4/2) (tp=45.0°C) | PZ 1: Epoxidová podlaha |
|---|---|
| Systém VARIONOVA | l-celk=82.3 m |
| Lpz=250 [mm] | 1.05 - Sklad |
| VYK: PZ:26.5°C | Rúrka RAUTHERM S 17x2,0 |
| S=17.0 m2 | VYK: 2.1 l/min |

| RZ 2 - 1. NP (4/1) (tp=45.0°C) | PZ 1: Epoxidová podlaha |
|---|---|
| Systém VARIONOVA | l-celk=84.4 m |
| Lpz=250 [mm] | 1.05 - Sklad |
| VYK: PZ:26.5°C | Rúrka RAUTHERM S 17x2,0 |
| S=15.7 m2 | VYK: 2.1 l/min |

## LEGENDA POTRUBIA:

POTRUBIE - PLASTHLINNÍKOVÁ RÚRKA RAUTHERM S 17x2,0, fy. REHAU
PRE OKRUHY PODLAHOVÉHO VYKUROVANIA, TEPLOTNÝ SPÁD 45/35°C

POTRUBIE - PLASTHLINNÍKOVÁ RÚRKA PE-Xa/AL/PE napr. RAUTITAN STABIL
SPÁJANÉ LISOVANÍM, IZOLOVANÉ POTRUBIE, TEPLOTNÝ SPÁD 45/35°C
POTRUBIE VEDENÉ V PODLAHE, PRE PODLAHOVÉ VYKUROVANIE

ROZVOD ÚK PRE PRIMÁRNY OKRUH TEPELNÉHO ČERPADLA
MATERIÁL MEĎ

## LEGENDA ZARIADENÍ A ARMATÚR :

| | |
|---|---|
| 1a | KOMPAKTNÁ VNÚTORNÁ JEDNOTKA TEPELNÉHO ČERPADLA VITOCAL 222-S AWBT-M-E 221.E08 |
| 1b | VONKAJ.JEDNOTKA VITOCAL 222-S AWBT-M-E 221.E08 (230V) |
| | MAX.VÝSTUPNÁ TEPLOTA 60°C,TEPELNY VYKON 2,6-9kW A7/W35 |
| | EKOLOGICKE CHLADIVO R32, REGULÁCIA ONE-BASE,WIFI (Z022722) |
| 03 | AKUMULACNY ZASOBNIK VITOCELL 100-W TYP SVWA 200L |
| 04 | BEZDRÔDOTVÉ DIAĽKOVÉ OVLÁDANIE VITOTROL 300-E |
| 08 | UZAVRETÁ TLAKOVÁ EXPANZNÁ NÁDOBA VIESSMANN N25 OBJEM 25L, 3bar |
| | ROZMERY : Ø=308 mm, VÝŠKA 477 mm , HMOTNOSŤ 4,3 kg + NASTENNY DRZIAK PRE N25 (9572216) |
| TP | PRIESTOROVÝ REGULÁTOR NEA SMART 2.0 PRE MERANIE TEPLOTY V MIESTNOSTI, FY. REHAU |
| TE | SNÍMAČ VONKAJŠEJ TEPLOTY |
| 13 | RYCHLOMONT.SADA SO ZMIESAVACOM M32 DN25 ALPHA2+(7741079) |
| | UPEVNENIE NA STENU PRE RMS DN25 (7741097) |

## POZNÁMKA :

- V PRÍPADE NEJASNOSTÍ VO VÝKRESOVEJ DOKUMENTÁCII KONTAKTOVAŤ ZODPOVEDNÉHO PROJEKTANTA
- VŠETKY ROZMERY STAVEBNÝCH PRÁC KONTROLOVAŤ NA MIESTE STAVBY
- PRED UVEDENÍM SYSTÉMU DO PREVÁDZKY JE POTREBNÉ VYKONAŤ DÔKLADNÝ PREPLACH SYSTÉMU S VYČISTENÍM VŠETKÝCH FILTROV NA ROZVODE
- PO NAPUSTENÍ SYSTÉMU JE POTREBNÉ VYKONAŤ JEHO ODVZDUŠNENIE
- DODÁVATEL STAVBY JE POVINNÝ REALIZOVAŤ VŠETKY PRÁCE V ZMYSLE PLATNÝCH STN EN S DODRŽANÍM TECHNOLOGICKÝCH A BEZPEČNOSTNÝCH POSTUPOV. ĎALEJ JE POVINNÝ REŠPEKTOVAŤ USTANOVENIÁ STN 730421 O PRÍSLUŠNÝCH ROZMEROVÝCH ODCHÝLKACH REALIZOVANÝCH KONŠTRUKCIÍ PROTI PROJEKTOVANÉMU STAVU. KAŽDÚ ODCHÝLKU OD PROJEKTU JE POTREBNÉ PREROKOVAŤ S GP.

**±0,000 = úroveň 1.N.P. = 126,40 m.n.m.**

| | | | |
|---|---|---|---|
| **ARCHITEKT STAVBY** | **Ing. arch. JURAJ ZATKALÍK** | **zatkalík architects, s.r.o.**<br>**Liščie údolie 65**<br>**841 05 Bratislava** | |
| **ZODPOVEDNÝ PROJEKTANT** | **Ing. Norbert Jokay** | | |
| **VYPRACOVAL** | **Bc. Viktor Labovský** | | |
| **INVESTOR** | **MEDISYNER SK, s.r.o.**<br>**ROYOVA 9**<br>**921 01 PIEŠŤANY** | | |
| **STAVBA** | **MEDISYNER**<br>**BRATISLAVA, KOMÁRŇANSKÁ ul., p.č. 194/403** | **STUPEŇ** | PSP - ZMENA STAVBY |
| | | **DÁTUM** | OKTOBER 2025 |
| **PROFESIA** | **VYKUROVANIE** | **FORMÁT** | 630 x 420 |
| **DRUH STAVBY** | **HOSPODÁRSKO ADMINISTRATÍVNY OBJEKT** | **MIERKA** | M 1:75 |
| **NÁZOV VÝKRESU** | **PODORYS 1.N.P.** | **ČÍSLO VÝKRESU** | 1 |