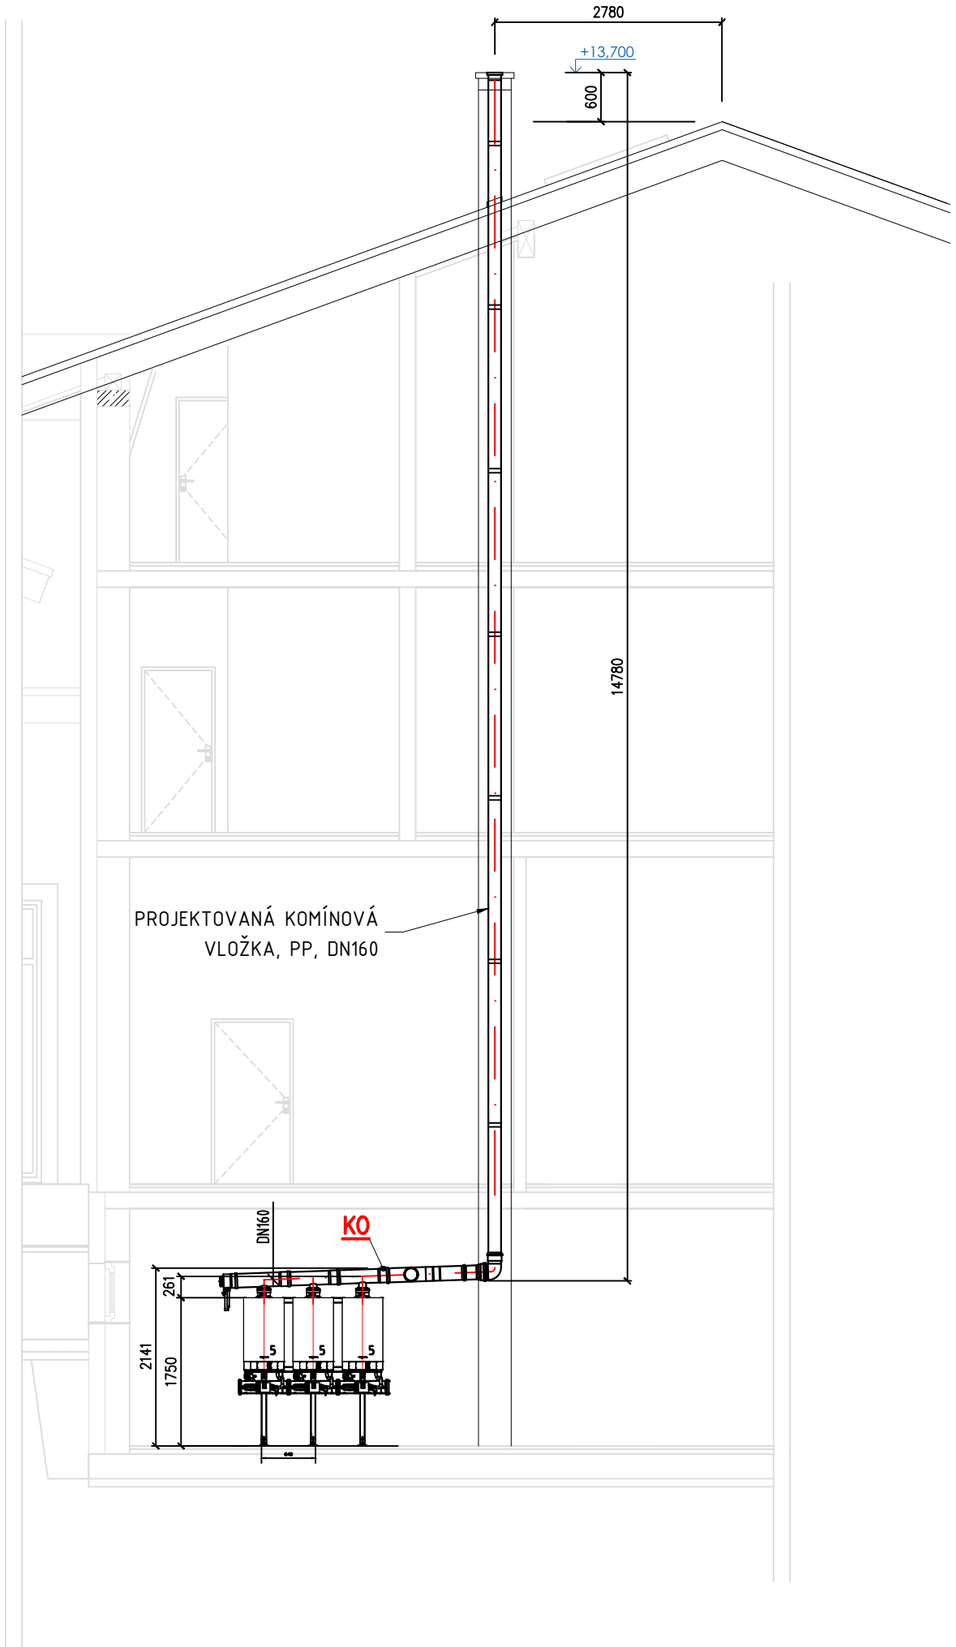


LEGENDA ZARIADENÍ A ARMATÚR :

5	3xNASTENNY KONDENZAČNÝ KOTOL VITODENS 200-W 12-49kW+KASKADOVA REGULACIA (B2HA159)
KO	SPALINOVA KASKADA PRE TRI KOTLY 49kW DN160 (ZK00678) PP Ø160mm

POZNÁMKA :

- V PRÍPADE NEJASNOSTÍ VO VÝKRESOVEJ DOKUMENTÁCII KONTAKTOVAŤ ZODPOVEDNÉHO PROJEKTANTA
- VŠETKY ROZMERY STAVEBNÝCH PRÁC KONTROLOVAŤ NA MIESTE STAVBY
- PRED UVEDENÍM SYSTÉMU DO PREVÁDZKY JE POTREBNÉ VYKONAŤ DÔKLADNÝ PREPLACH SYSTÉMU S VYČISTENÍM VŠETKÝCH FILTROV NA ROZVODE
- PO NAPUSTENÍ SYSTÉMU JE POTREBNÉ VYKONAŤ JEHO ODVZDUŠNENIE
- DODÁVATEL STAVBY JE POVINNÝ REALIZOVAŤ VŠETKY PRÁCE V ZMYSLE PLATNÝCH STN EN S DODRŽANÍM TECHNOLOGICKÝCH A BEZPEČNOSTNÝCH POSTUPOV. ĎALEJ JE POVINNÝ REŠPEKTOVAŤ USTANOVENIÁ STN 730421 O PRÍSLUŠNÝCH ROZMEROVÝCH ODCHÝLKACH REALIZOVANÝCH KONŠTRUKCIÍ PROTI PROJEKTOVANÉMU STAVU. KAŽDÚ ODCHÝLKU OD PROJEKTU JE POTREBNÉ PREROKOVAŤ S GP.
- PRESTUPY INŽINIERSKYCH SIETÍ A ROZVODOV V OBJEKTE JE POTREBNÉ VYNECHAŤ PRI REALIZÁCII STAVBY.
- PROJEKTOVÁ DOKUMENTÁCIA JE SPRACOVANÁ PRE ÚČEL VYDANIA STAVEBNÉHO POVOLENIA A NENAHRÁDZA REALIZAČNÝ PROJEKT

OBJEDNÁVATEĽ:
O&L, s.r.o., Štefánska 3793/22, 058 01 Poprad

STAVBA:

CHATA NA JANKOVEJ LÚKE
prestavba pôvodnej Jankovej koliby

Štrba, Štrbské Pleso,
ul. K vodopádom, č. 4095/17

ZODP. PROJEKTANT:
Ing. Norbert Jókay

VYPRACOVAL:
Bc. Viktor Labovský

STUPEŇ PD:
DSP

DATUM SPRACOVANIA:
03/2025

OBSAH VÝKRESU:
REZ KOMÍNOVÝM TELESOM

MIERKA:
M=1:75

Č. VÝKRESU:
05