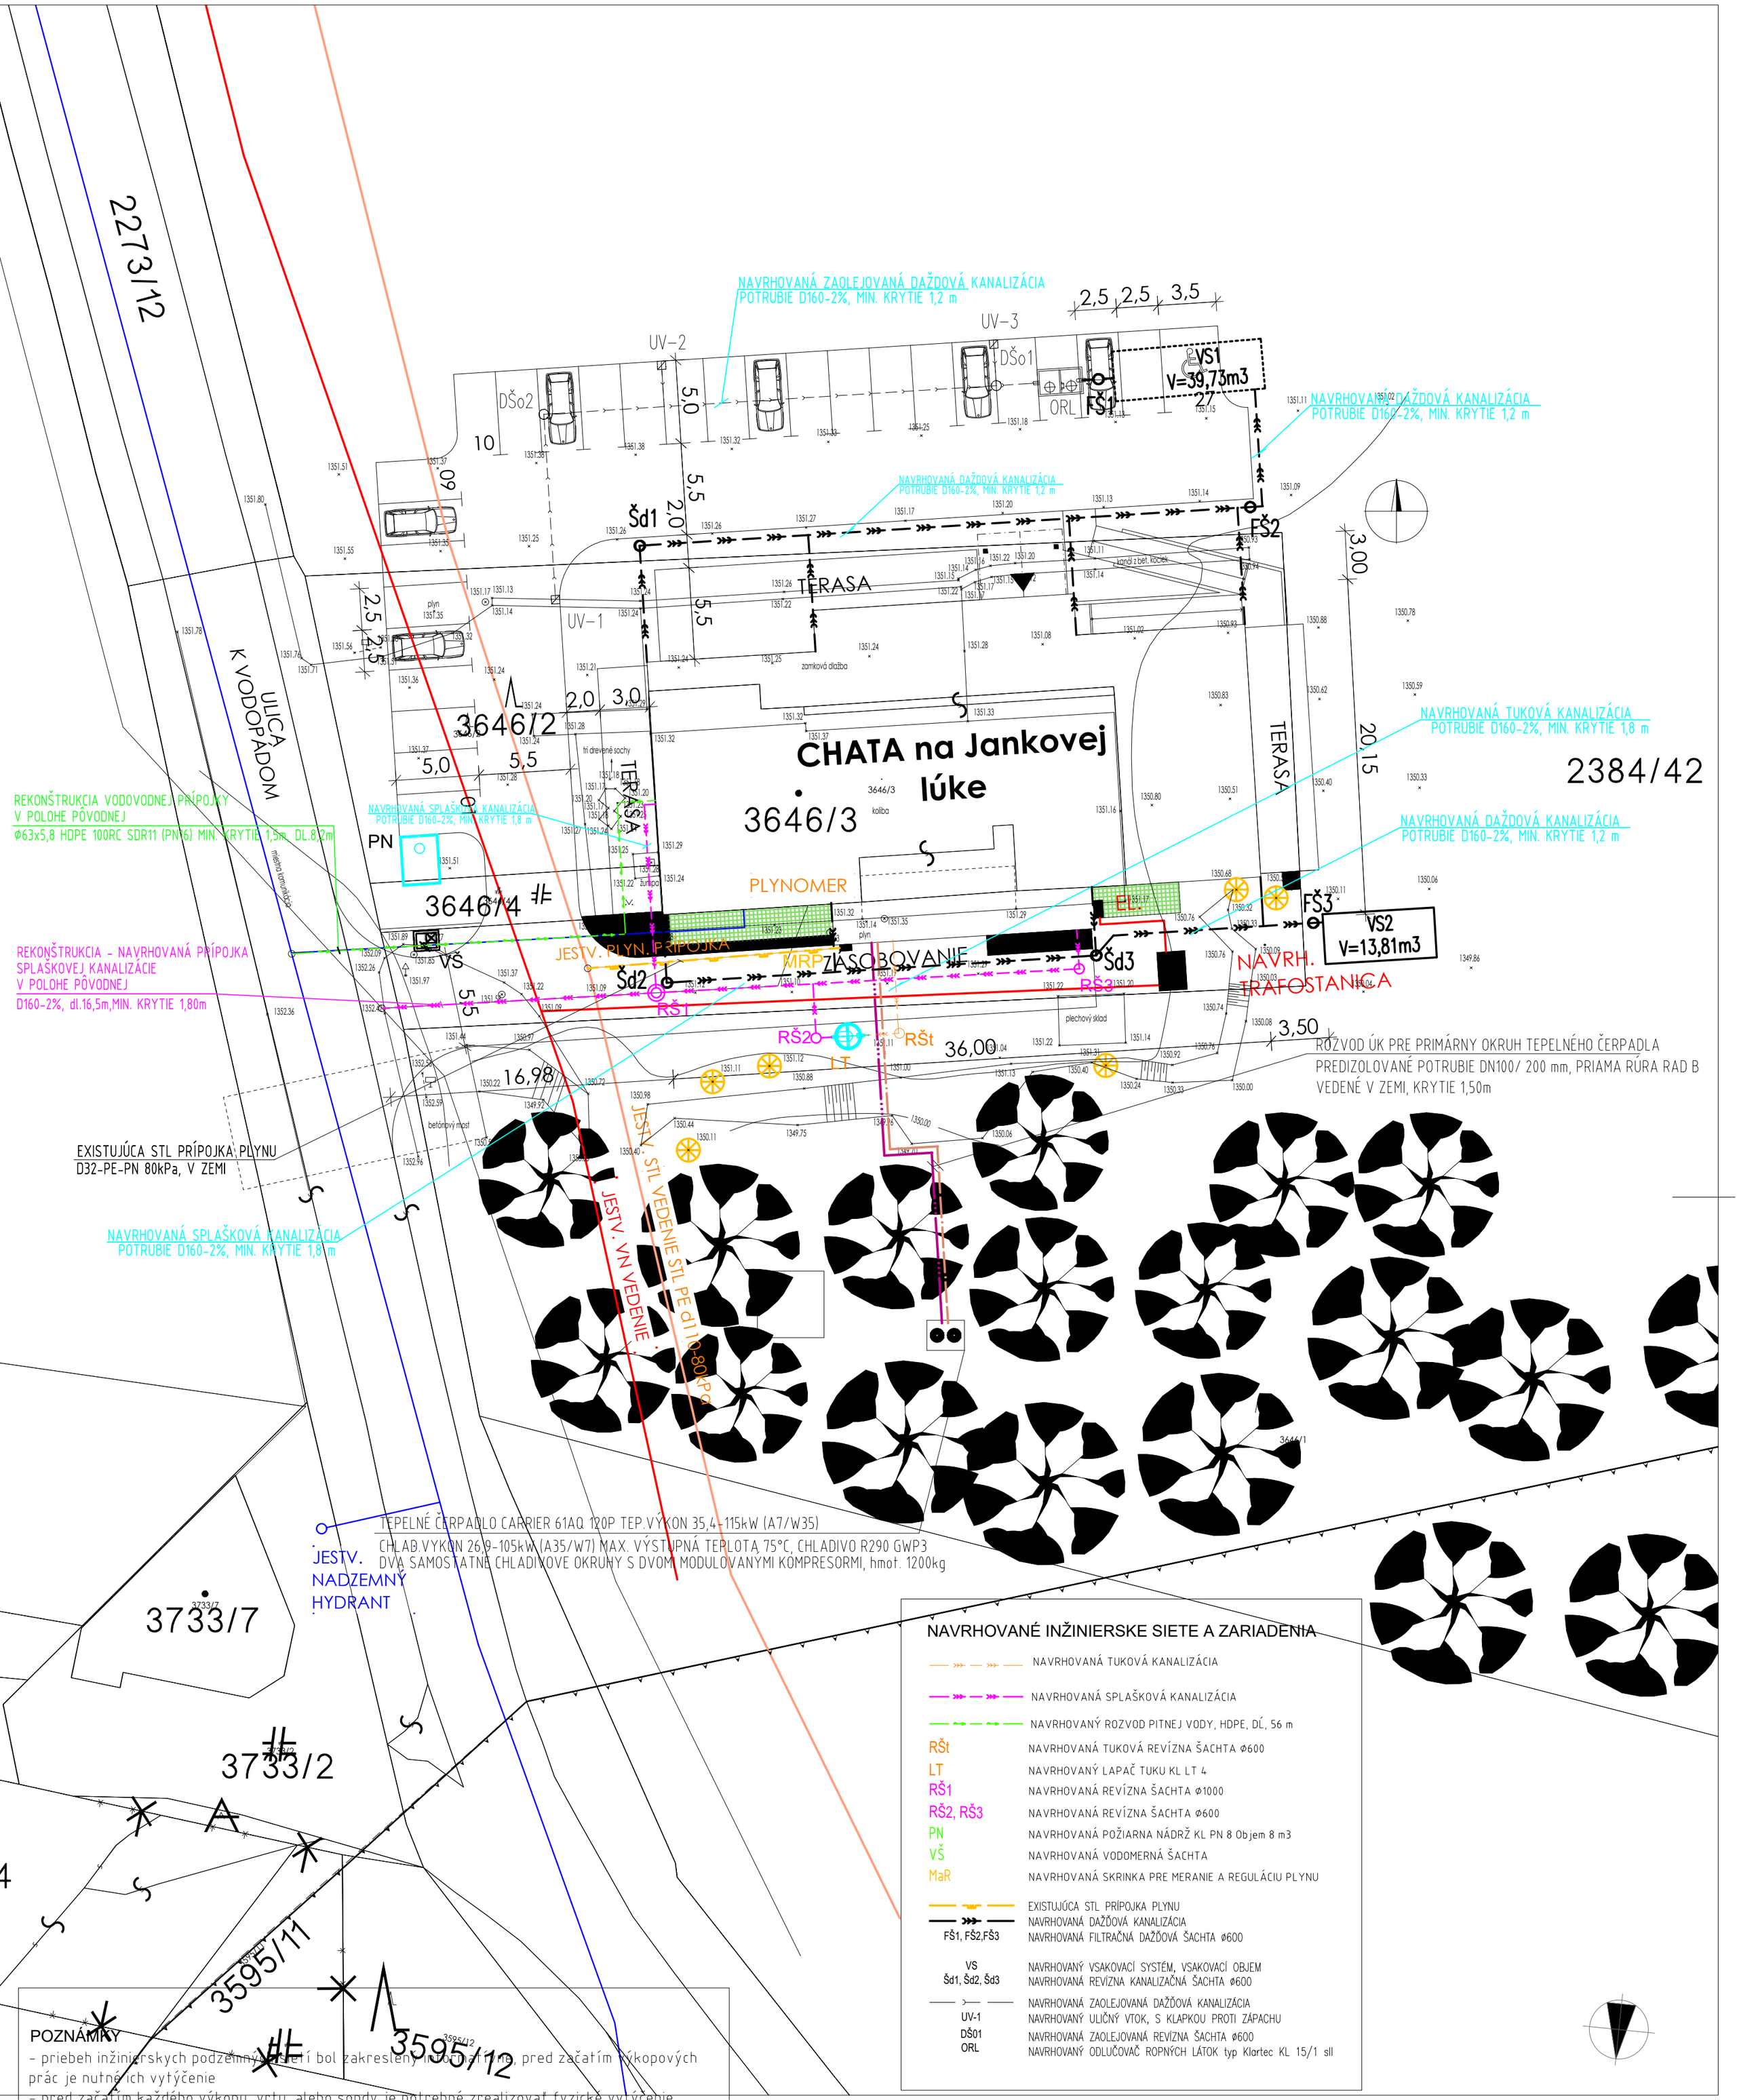


NAVRHOVANÉ INŽINIERSKE SIETE A ZARIADENIA

	NAVRHOVANÁ TUKOVÁ KANALIZÁCIA
	NAVRHOVANÁ SPLAŠKOVÁ KANALIZÁCIA
	NAVRHOVANÝ ROZVOD PITNEJ VODY, HDPE, DĹ. 56 m
RŠt	NAVRHOVANÁ TUKOVÁ REVÍZNA ŠACHTA Ø600
LT	NAVRHOVANÝ LAPAČ TUKU KL LT 4
RŠ1	NAVRHOVANÁ REVÍZNA ŠACHTA Ø1000
RŠ2, RŠ3	NAVRHOVANÁ REVÍZNA ŠACHTA Ø600
PN	NAVRHOVANÁ POŽIARNA NÁDRŽ KL PN 8 Objem 8 m3
VŠ	NAVRHOVANÁ VODOMERNÁ ŠACHTA
MaR	NAVRHOVANÁ SKRINKA PRE MERANIE A REGULÁCIU PLYNU
	EXISTUJÚCA STL PRÍPOJKA PLYNU
	NAVRHOVANÁ DAŽĎOVÁ KANALIZÁCIA
FŠ1, FŠ2,FŠ3	NAVRHOVANÁ FILTRAČNÁ DAŽĎOVÁ ŠACHTA Ø600
VS	NAVRHOVANÝ VSAKOVACÍ SYSTÉM, VSAKOVACÍ OBJEM
Šd1, Šd2, Šd3	NAVRHOVANÁ REVÍZNA KANALIZAČNÁ ŠACHTA Ø600
	NAVRHOVANÁ ZAOLEJOVANÁ DAŽĎOVÁ KANALIZÁCIA
UV-1	NAVRHOVANÝ ULIČNÝ VTOK, S KLAPKOU PROTI ZÁPACHU
DŠ01	NAVRHOVANÁ ZAOLEJOVANÁ REVÍZNA ŠACHTA Ø600
ORL	NAVRHOVANÝ ODLUČOVAČ ROPNÝCH LÁTOK typ Klartec KL 15/1 sll

POZNÁMKY

- priebeh inžinierskych podzemných sietí bol zakreslený informatívne, pred začatím výkopových prác je nutné ich vytýčenie
- pred začatím každého výkopu, vrtu, alebo sondy je potrebné zrealizovať fyzické vytýčenie každého podzemného objektu jeho majiteľom, správcom alebo prevádzkovateľom
- pred realizáciou každého napojenia na inžinierske siete je potrebné pred začatím prác najskôr odhaliť a premerať bod napojenia
- pri realizácii a križovaní vedení musia byť dodržané dotknuté ustanovenia STN, ON a technologických predpisov
- pri realizácii jednotlivých vedení treba dodržať STN 73 6005 - Priestorová úprava vedení technického vybavenia
- projektant nenesie žiadnu zodpovednosť za zmeny uskutočnené bez jeho písomného súhlasu
- zhotoviteľ je povinný o zistených nezrovnalostiach v projektovej dokumentácii neodkladne informovať projektanta
- rozdiely zistené na stavbe oproti PD je nutné v technickom riešení odsúhlasiť s projektantom ešte pred samotnou realizáciou
- obsah výkresu je duševným vlastníctvom autorov a jeho použitie na iný účel podlieha autorskému zákonu

OBJEDNÁVATEĽ:	STAVBA: **CHATA NA JANKOVEJ LÚKE** prestavba pôvodnej Jankovej koliby Štrba, Štrbské Pleso, ul. K vodopádom, č. 4095/17	**ZODP. PROJEKTANT:** Ing. Norbert Jókay	
STUPEŇ PD: DSP		**VYPRACOVAL:** Ing. Norbert Jókay	
DATUM SPRACOVANIA: 03/2025	**OBSAH VÝKRESU:** **UK-SITUACIA**	**MIERKA:** M=1:250	**Č. VÝKRESU:** 01