RZ 2 - 1. NP (9/7) (tp=45.0°C)	PZ 1: Drevené parkety 13mm
Systém TECTO	l-celk=66.9 m
Lpz=150 [mm]	1.06 - Spalna master
VYK: PZ:25.8°C	COMFORT PIPE PLUS (kotúč) 16x2
S=7.2 m2	VYK: 0.8 l/min

RZ 2 - 1. NP (9/8) (tp=45.0°C)	PZ 1: Keramická dlažba 15mm + lepidlo
Systém TECTO	l-celk=52.6 m
Lpz=100 [mm]	1.07 - Kupelna master
VYK: PZ:32.5°C	COMFORT PIPE PLUS (kotúč) 16x2
S=3.7 m2	VYK: 0.9 l/min

RZ 2 - 1. NP (9/9) (tp=45.0°C)	PZ 1: Keramická dlažba 15mm + lepidlo
Systém TECTO	l-celk=58.3 m
Lpz=100 [mm]	1.07 - Kupelna master
VYK: PZ:32.5°C	COMFORT PIPE PLUS (kotúč) 16x2
S=4.0 m2	VYK: 0.9 l/min

RZ 2 - 1. NP (9/1) (tp=45.0°C)	PZ 1: Keramická dlažba 15mm + lepidlo
Systém TECTO	l-celk=47.3 m
Lpz=100 [mm]	1.08 - Kupelna
VYK: PZ:32.5°C	COMFORT PIPE PLUS (kotúč) 16x2
S=3.9 m2	VYK: 0.7 l/min

RZ 2 - 1. NP (9/2) (tp=45.0°C)	PZ 1: Drevené parkety 13mm
Systém TECTO	l-celk=118.1 m
Lpz/Loz=150/100 [mm]	1.09 - Pracovna
VYK: PZ:26.1°C [OZ:26.5°C]	COMFORT PIPE PLUS (kotúč) 16x2
S=14.0 m2	VYK: 1.4 l/min

- 1.07 -	
Kupelna master	
24 °C	522 W

- 1.08 -	
Kupelna	
24 °C	200 W

RZ 2 - 1. NP (9/6) (tp=45.0°C)	PZ 1: Drevené parkety 13mm
Systém TECTO	l-celk=96.3 m
Lpz=150 [mm]	1.06 - Spalna master
VYK: PZ:25.8°C	COMFORT PIPE PLUS (kotúč) 16x2
S=12.7 m2	VYK: 1.2 l/min

- 1.06 -	
Spalna master	
22 °C	698 W

- 1.09 -	
Pracovna	
22 °C	372 W

RZ 2 - 1. NP (9/5) (tp=45.0°C)	PZ 1: Drevené parkety 13mm
Systém TECTO	l-celk=81.5 m
Lpz=150 [mm]	1.05 - Spalna
VYK: PZ:26.1°C	COMFORT PIPE PLUS (kotúč) 16x2
S=10.2 m2	VYK: 1.0 l/min

RZ 2 - 1. NP (9/4) (tp=45.0°C)	PZ 1: Drevené parkety 13mm
Systém TECTO	l-celk=81.9 m
Lpz=150 [mm]	1.05 - Spalna
VYK: PZ:26.1°C	COMFORT PIPE PLUS (kotúč) 16x2
S=10.2 m2	VYK: 1.0 l/min

- 1.05 -	
Spalna	
22 °C	809 W

RZ 2 - 1. NP (9/3) (tp=45.0°C)	PZ 1: Drevené parkety 13mm
Systém TECTO	l-celk=54.5 m
Lpz=150 [mm]	1.04 - Chodba 2
VYK: PZ:25.8°C	COMFORT PIPE PLUS (kotúč) 16x2
S=7.7 m2	VYK: 0.7 l/min

- 1.04 -	
Chodba 2	
22 °C	927 W

RZ 1 - 1. NP (4/3) (tp=45.0°C)	PZ 1: Drevena podlaha 13 mm
Systém TECTO	l-celk=81.5 m
Lpz=200 [mm]	1.03 - Obývačka s kuchynou
VYK: PZ:24.6°C [OZ:25.0°C]	COMFORT PIPE PLUS (kotúč) 16x2
S=11.2 m2	VYK: 1.4 l/min

RZ 1 - 1. NP (4/2) (tp=45.0°C)	PZ 1: Drevena podlaha 13 mm
Systém TECTO	l-celk=80.1 m
Lpz=200 [mm]	1.03 - Obývačka s kuchynou
VYK: PZ:24.6°C [OZ:25.0°C]	COMFORT PIPE PLUS (kotúč) 16x2
S=13.5 m2	VYK: 1.5 l/min


RZ 1 - 1. NP (4/1) (tp=45.0°C)	PZ 1: Drevené parkety 13mm
Systém TECTO	l-celk=50.2 m
Lpz=150 [mm]	1.01 - Chodba
VYK: PZ:26.1°C	COMFORT PIPE PLUS (kotúč) 16x2
S=7.2 m2	VYK: 0.7 l/min

- 1.03 -	
Obývačka s kuchynou	
20 °C	1782 W


RZ 1 - 1. NP (4/4) (tp=45.0°C)	PZ 1: Drevena podlaha 13 mm
Systém TECTO	l-celk=85.1 m
Lpz/Loz=200/150 [mm]	1.03 - Obývačka s kuchynou
VYK: PZ:24.6°C [OZ:25.0°C]	COMFORT PIPE PLUS (kotúč) 16x2
S=12.1 m2	VYK: 1.4 l/min

- 1.01 -	
Chodba	
22 °C	524 W

- 1.02 -	
WC	
22 °C	61 W

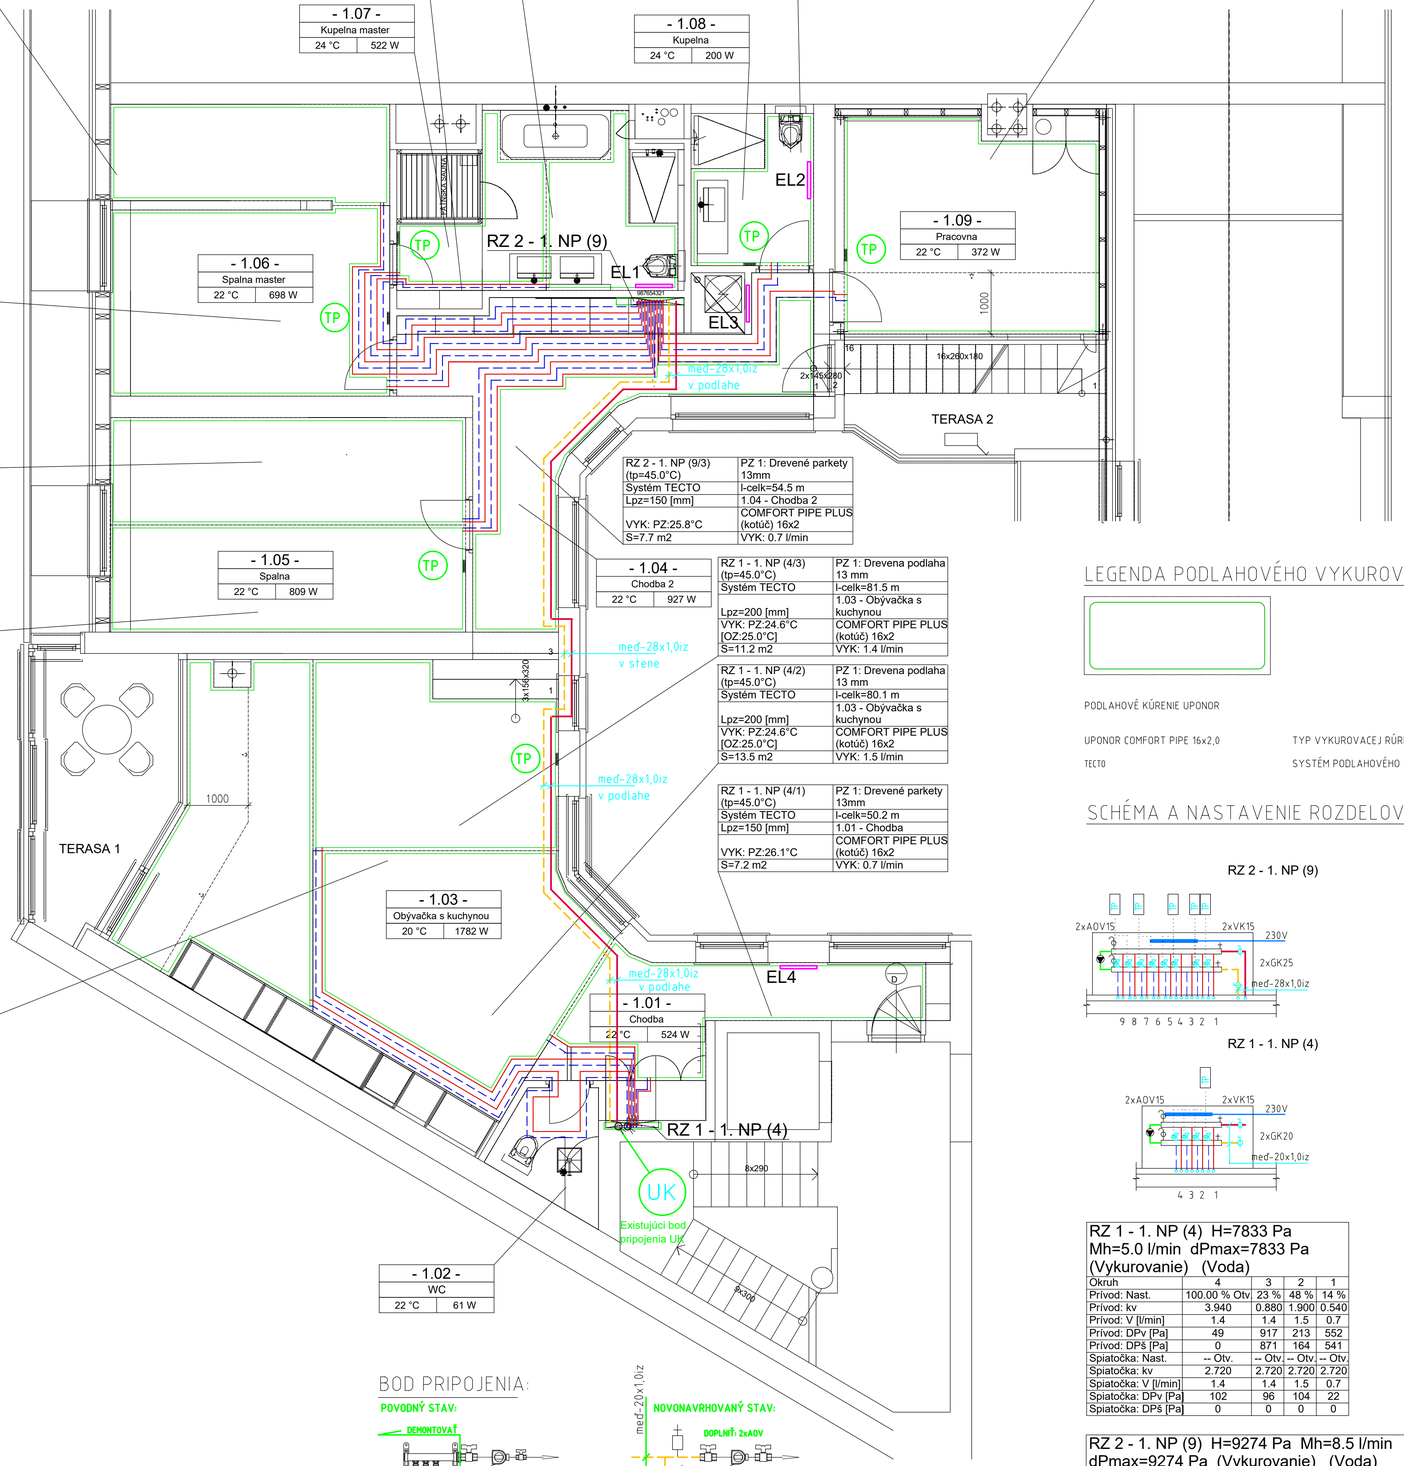

BOD PRIPOJENIA:

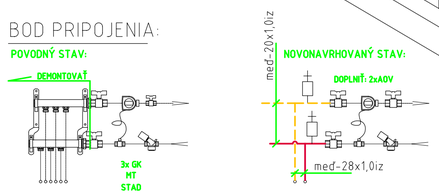

LEGENDA PODLAHOVÉHO VYKUROVANIA:

PODLAHOVÉ KÚRENIE UPONOR

UPONOR COMFORT PIPE 16x2,0	TYP VYKUROVACEJ RÚRKY
TECTO	SYSTÉM PODLAHOVÉHO VYKUROVANIA

SCHÉMA A NASTAVENIE ROZDELOVAČOV:

RZ 2 - 1. NP (9)

RZ 1 - 1. NP (4)

RZ 1 - 1. NP (4) H=7833 Pa Mh=5.0 l/min dPmax=7833 Pa (Vykurovanie) (Voda)				
Okruh	4	3	2	1
Prívod: Nast.	100.00 % Otv	23 %	48 %	14 %
Prívod: kv	3.940	0.880	1.900	0.540
Prívod: V [l/min]	1.4	1.4	1.5	0.7
Prívod: DPv [Pa]	49	917	213	552
Prívod: DPš [Pa]	0	871	164	541
Spiatočka: Nast.	-- Otv.	-- Otv.	-- Otv.	-- Otv.
Spiatočka: kv	2.720	2.720	2.720	2.720
Spiatočka: V [l/min]	1.4	1.4	1.5	0.7
Spiatočka: DPv [Pa]	102	96	104	22
Spiatočka: DPš [Pa]	0	0	0	0

RZ 2 - 1. NP (9) H=9274 Pa Mh=8.5 l/min dPmax=9274 Pa (Vykurovanie) (Voda)									
Okruh	9	8	7	6	5	4	3	2	1
Prívod: Nast.	14 %	14 %	14 %	14 %	14 %	14 %	14 %	100.00 % Otv	14 %
Prívod: kv	0.540	0.540	0.540	0.540	0.540	0.540	0.540	3.940	0.540
Prívod: V [l/min]	0.9	0.9	0.8	1.2	1.0	1.0	0.7	1.4	0.7
Prívod: DPv [Pa]	1014	918	745	1718	1297	1306	558	44	631
Prívod: DPš [Pa]	995	901	731	1686	1273	1281	547	0	619
Spiatočka: Nast.	-- Otv.	-- Otv.	-- Otv.	-- Otv.	-- Otv.	-- Otv.	-- Otv.	-- Otv.	-- Otv.
Spiatočka: kv	2.720	2.720	2.720	2.720	2.720	2.720	2.720	2.720	2.720
Spiatočka: V [l/min]	0.9	0.9	0.8	1.2	1.0	1.0	0.7	1.4	0.7
Spiatočka: DPv [Pa]	40	36	29	68	51	51	22	91	25
Spiatočka: DPš [Pa]	0	0	0	0	0	0	0	0	0

LEGENDA MIESTNOSTÍ :

č.m.	Účel miestnosti	A [m²]
1.1	Chodba	7.65
1.2	WC	2.88
1.3	Obývačka + kuchyňa	46.69
1.4	Chodba 2	17.70
1.5	Spálňa	20.28
1.6	Spálňa Master	21.70
1.7	Kúpeľňa Master	14.68
1.8	Kúpeľňa	5.27
1.9	Pracovňa	14.74
	Spolu:	157.59

LEGENDA ZARIADENÍ A ARMATÚR :

GV	GUĽOVÝ VENTIL ZÁVITOVÝ
RV	PREDNASTAVITEĽNÝ REGULAČNÝ VENTIL PRIAMY - STAD
VK	VYPÚŠŤACÍ KOHÚT
OV	ODVZDUŠŇOVACÍ VENTIL
TP	PRIESTOROVÝ REGULÁTOR PRE MERANIE TEPLOTY V MIESTNOSTI Smatrix Base Style termostat D+RH T-149Bus (obj.č. 1087813)
UK1-5	STÚPAČKA VYKUROVANIA
UKVZT	STÚPAČKA VYKUROVANIA PRE OKRUH VZT ZARIADENÍ
RZ	ROZDELOVACIA STANICA PRE VYKUROVACIE TELESÁ A PODLAHOVÉ VYKUROVANIE

POTRUBIE:

Plastový rozvod - plastthliníková rúrka s kyslíkovou bariérou Pex-Al-Pex.

Medený rozvod - medená rúrka prívodného potrubia
Medený rozvod - medená rúrka vratného potrubia

Potrubie pre napojenie rozdelovacej stanice vedené v podlahe uložiť do izolácie podlahy pod podlahové vykurovanie.
Potrubie vedené v podlahe izolovať tepelnou izoláciou na báze kaučuku hr. 9mm.
Volne vedené potrubie izolovať tepelnou izoláciou na báze kaučuku hr. 19mm.
Prestup potrubia cez požiarnu deliacu konštrukciu izolovať minerálnou vlnou a z oboch strán zatrieť protipožiarnou pastou.
Pri prestupe rozvodov cez stavebnú konštrukciu opatrif tepelnú izoláciu chráničkou z ocel. pozinkovaného plechu hr. 0,6mm

(UK) Označenie stúpacích potrubí

LEGENDA VYKUROVACÍCH TELIES:

EL1 - ELEKTRICKÝ REBRÍKOVÝ RADIÁTOR (MIN. VÝKON 500W), PRESNÝ TYP URČÍ ARCHITEKT

EL2 - ELEKTRICKÝ REBRÍKOVÝ RADIÁTOR (MIN. VÝKON 300W), PRESNÝ TYP URČÍ ARCHITEKT

EL3 - ELEKTRICKÝ REBRÍKOVÝ RADIÁTOR (MIN. VÝKON 350W), PRESNÝ TYP URČÍ ARCHITEKT

EL4 - ELEKTRICKÝ REBRÍKOVÝ RADIÁTOR (MIN. VÝKON 150W), PRESNÝ TYP URČÍ ARCHITEKT

POZNÁMKA :

- V PRÍPADE NEJASNOSTÍ VO VÝKRESOVEJ DOKUMENTÁCII KONTAKTOVAŤ ZODPOVEDNÉHO PROJEKTANTA
- VŠETKY ROZMERY STAVEBNÝCH PRÁC KONTROLOVAŤ NA MIESTE STAVBY
- PRED UVEDENÍM SYSTÉMU DO PREVÁDZKY JE POTREBNÉ VYKONAŤ DÔKLADNÝ PREPLACH SYSTÉMU S VYČISTENÍM VŠETKÝCH FILTROV NA ROZVODE
- PO NAPUSTENÍ SYSTÉMU JE POTREBNÉ VYKONAŤ JEHO ODVZDUŠNENIE
- DODÁVATEL STAVBY JE POVINNÝ REALIZOVAŤ VŠETKY PRÁCE V ZMYSLE PLATNÝCH STN EN S DODRŽANÍM TECHNOLOGICKÝCH A BEZPEČNOSTNÝCH POSTUPOV. ĎALEJ JE POVINNÝ REŠPEKTOVAŤ USTANOVENIÁ STN 730421 O PRÍSLUŠNÝCH ROZMEROVÝCH ODCHÝLKACH REALIZOVANÝCH KONŠTRUKCIÍ PROTI PROJEKTOVANÉMU STAVU. KAŽDÚ ODCHÝLKU OD PROJEKTU JE POTREBNÉ PREROKOVAŤ S GP.
- PRESTUPY INŽINIERSKYCH SIETÍ A ROZVODOV V OBJEKTE JE POTREBNÉ VYNECHAŤ PRI REALIZÁCII STAVBY.
- PROJEKTOVÁ DOKUMENTÁCIA JE SPRACOVANÁ PRE ÚČEL VYDANIA STAVEBNÉHO POVOLENIA A NENAHRÁDZA REALIZAČNÝ PROJEKT

UPOZORNENIE!

Realizačný projekt nenahrádza výrobnú a dielenskú dokumentáciu zhotovitela stavby !
Všetky rozmery kontrolovať na stavbe !
Pred montážou trasy rozvodov koordinovať s ostatnými profesiami.

t_e=-11°C
teplotná oblasť – 1

PARÉ Č.

±0,000 = 217 m n.m. Výškový systém: Balt p.v.

INVESTOR	ING. JOZEF BRHEL, EVA BRHLOVÁ, ZÁMOCKÁ 16, 811 01 BRATISLAVA		
NÁZOV STAVBY	STAVEBNÉ ÚPRAVY V BYTOVEJ JEDNOTKE		
MIESTO/Č. PARCELY	ZÁMOCKÁ 16, 811 01 BRATISLAVA		
AUTORI	ING. ARCH. MICHAL LANG, ING. ARCH. BORISLAV BENEDEK		
GP	LANG BENEDEK ASSOCIATED ARCHITECTS S.R.O., DUNAJSKÁ 6, 811 08 BRATISLAVA, +421 918 927 985, OFFICE@LANGBENEDEK.COM		
HIP	ING. ARCH. MICHAL LANG, LANG BENEDEK ASSOCIATED ARCHITECTS S.R.O., DUNAJSKÁ 6, 811 08 BRATISLAVA, +421 918 927 985, OFFICE@LANGBENEDEK.COM		
ZODP. PROJEKTANT	ING. NORBERT JOKAY		
VYPRACOVAL	BC. VIKTOR LABOVSKÝ	FORMÁT	8XA4
ČASŤ PD	VYKUROVANIE	MIERKA	1:50
PS, SO		DÁTUM	11/2025
OBSAH VÝKRESU	PÔDORYS	STUPEŇ RP	Č. V. 01