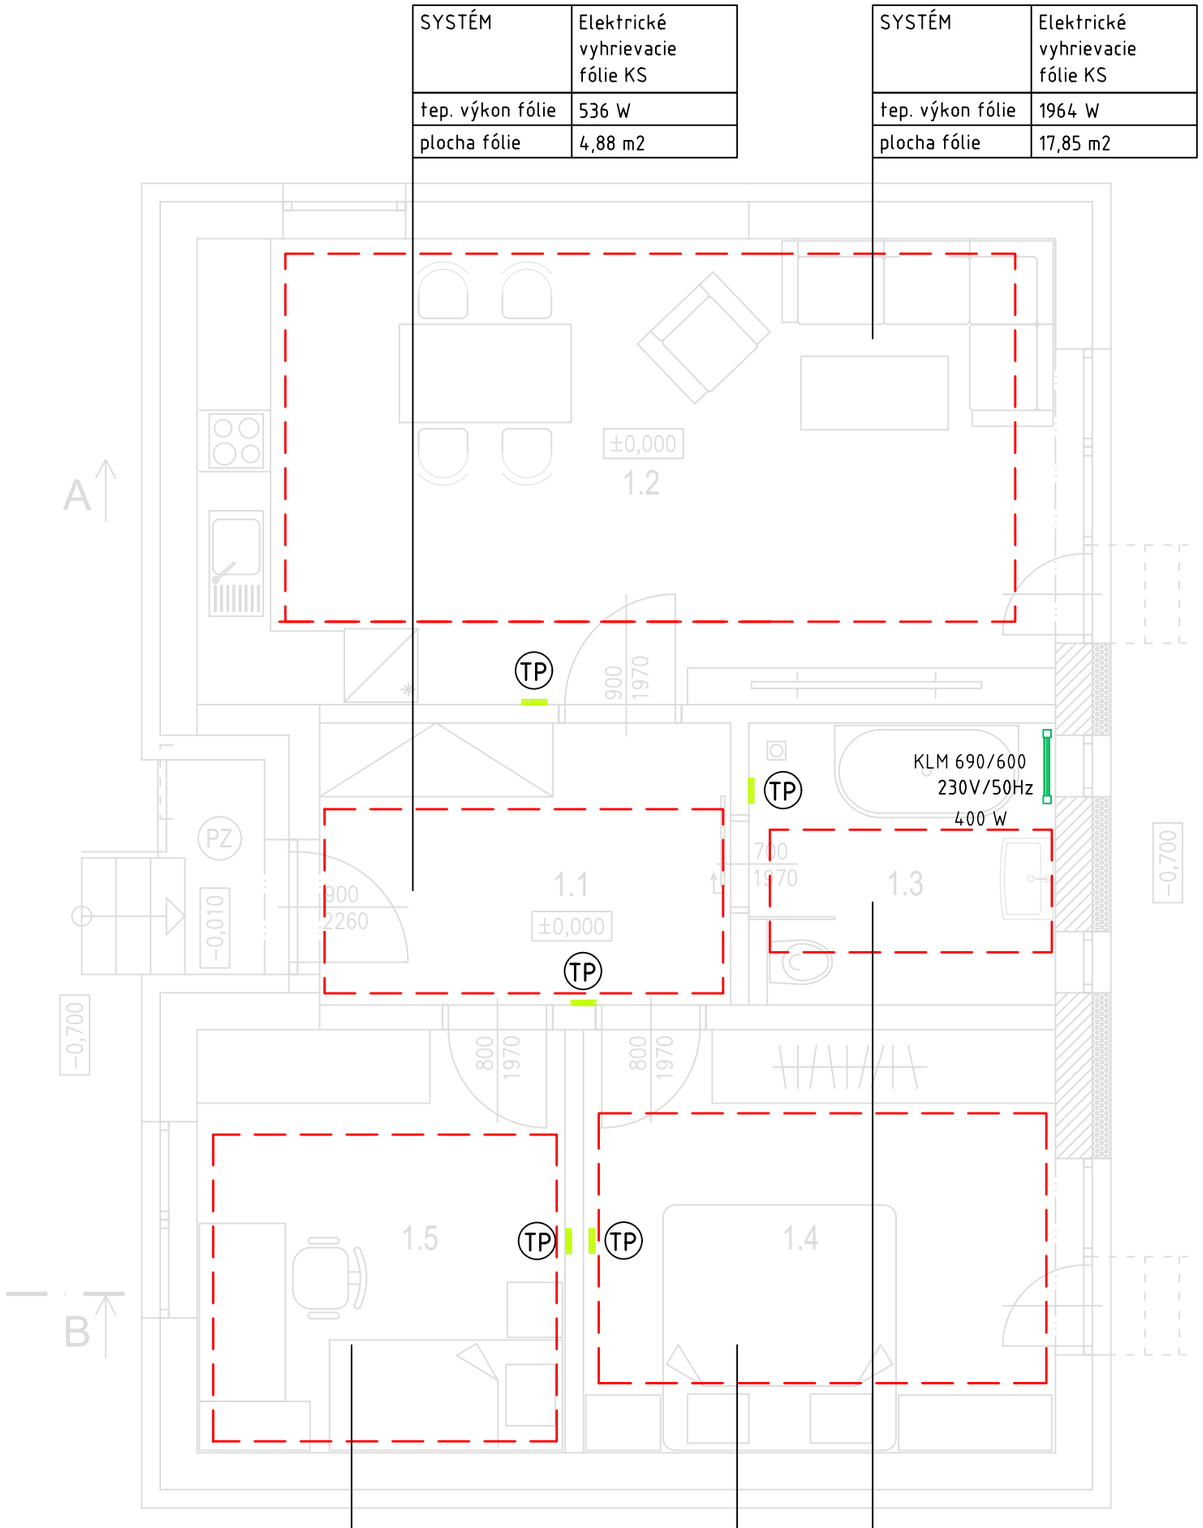


LEGENDA MIESTNOSTÍ 1.NP

Č.M.	NÁZOV MIESTNOSTI	PLOCHA m²	PODLAHY	ÚPRAVY POVRCHOV		POZNÁMKA
				STENY	STROP	
1.1	PREDSIEŇ	8,40	KERAMICKÁ DLAŽBA	OMIETKA	OMIETKA	KERAM. SOKEL
1.2	OBÝVACIA IZBA + KUCHYŇA	26,60	LAMINÁTOVÉ PARKETY	OMIETKA	OMIETKA	K.OBKLAD PRI KUCH. LINKE
1.3	KÚPELŇA -WC	5,75	KERAMICKÁ DLAŽBA	KER.OBKLAD	OMIETKA	KER.OBKLAD v=2,1m
1.4	IZBA	13,11	LAMINÁTOVÉ PARKETY	OMIETKA	OMIETKA	LEMOVACIA LIŠTA
1.5	IZBA	10,06	LAMINÁTOVÉ PARKETY	OMIETKA	OMIETKA	LEMOVACIA LIŠTA
	SPOLU :	63,92				

LEGENDA:

FÓLIOVÁ TECHNOLÓGIA SYSTÉMU VYHRIEVANIA NA ZÁKLADE DLHOVLNNÉHO INFRAČERVENÉHO ŽIARENIA

TP PRIESTOROVÝ REGULÁTOR TEPLOTY PRE PODLAHOVÉ VYKUROVANIE, napr. Heatflow

ELEKRICKÉ REBRÍKOVÉ VYKUROVACIE TELESO napr. KORALUX LINEAR MAX-ERA

POZNÁMKY:

- VŠETKY ROZMERY STAVEBNÝCH PRÁC KONTROLOVAŤ NA MIESTE STAVBY
- DOPORUČUJEM PREKÁBLOVANIE JEDNOTLIVÝCH TERMOSTATOV PODLAHOVÉHO VYKUROVANIA
- V PRÍPADE NEJASNOSTÍ VO VÝKRESOVEJ DOKUMENTÁCII KONTAKTOVAŤ ZODPOVEDNÉHO PROJEKTANTA S PRISLÚCHAJÚCOU REGULÁCIOU EŠTE PRED ZHOTOVENÍM OMIETOK
- DODÁVATEL STAVBY JE POVINNÝ REALIZOVAŤ VŠETKY PRÁCE V ZMYSLE PLATNÝCH STN EN S DODRŽANÍM TECHNOLOGICKÝCH A BEZPEČNOSTNÝCH POSTUPOV. ĎALEJ JE POVINNÝ REŠPEKTOVAŤ USTANOVENIA STN 730421 O PRÍSLUŠNÝCH ROZMEROVÝCH ODCHÝLKACH REALIZOVANÝCH KONŠTRUKCIÍ PROTI PROJEKTOVANÉMU STAVU. KAŽDÚ ODCHÝLKU OD PROJEKTU JE POTREBNÉ PREROKOVAŤ S GP.
- ±0,000 SA VZŤAHUJE K ÚROVNI FINÁLNEJ ÚPRAVY PODLAHY
- VÝBER VYKUROVACÍCH TELIES PODĽA INVESTORA

±0,000 = ÚROVEŇ PODLAHY NA 1.NP

HLAVNÝ INŽINIER PROJEKTU	ING. PETER TABERY	KRESLIL	BC. VIKTOR LABOVSKÝ	**Ing. Peter TABERY** **Leknová ul.1** **821 07 BRATISLAVA** č.opr.: 2575*A*1 – POZEMNÉ STAVBY
ZODPOVEDNÝ PROJEKTANT	ING. NORBERT JÓKAY	OBEC	BRATISLAVA - VRAKUŇA	
STAVEBNÍK	.			

NÁZOV STAVBY CHATA k.ú. Bratislava - Vrakuňa	ČÍSLO ZÁKAZKY	
	FORMÁT	2x A4
	DÁTUM	11 . 2025
NÁZOV OBJEKTU PROFESIA VYKUROVANIE	MIERKA	1 : 50
	STUPEŇ PD	
NÁZOV VÝKRESU PÔDORYS 1.NP	ČÍSLO VÝKRESU 1	ČÍSLO SÚPRAVY