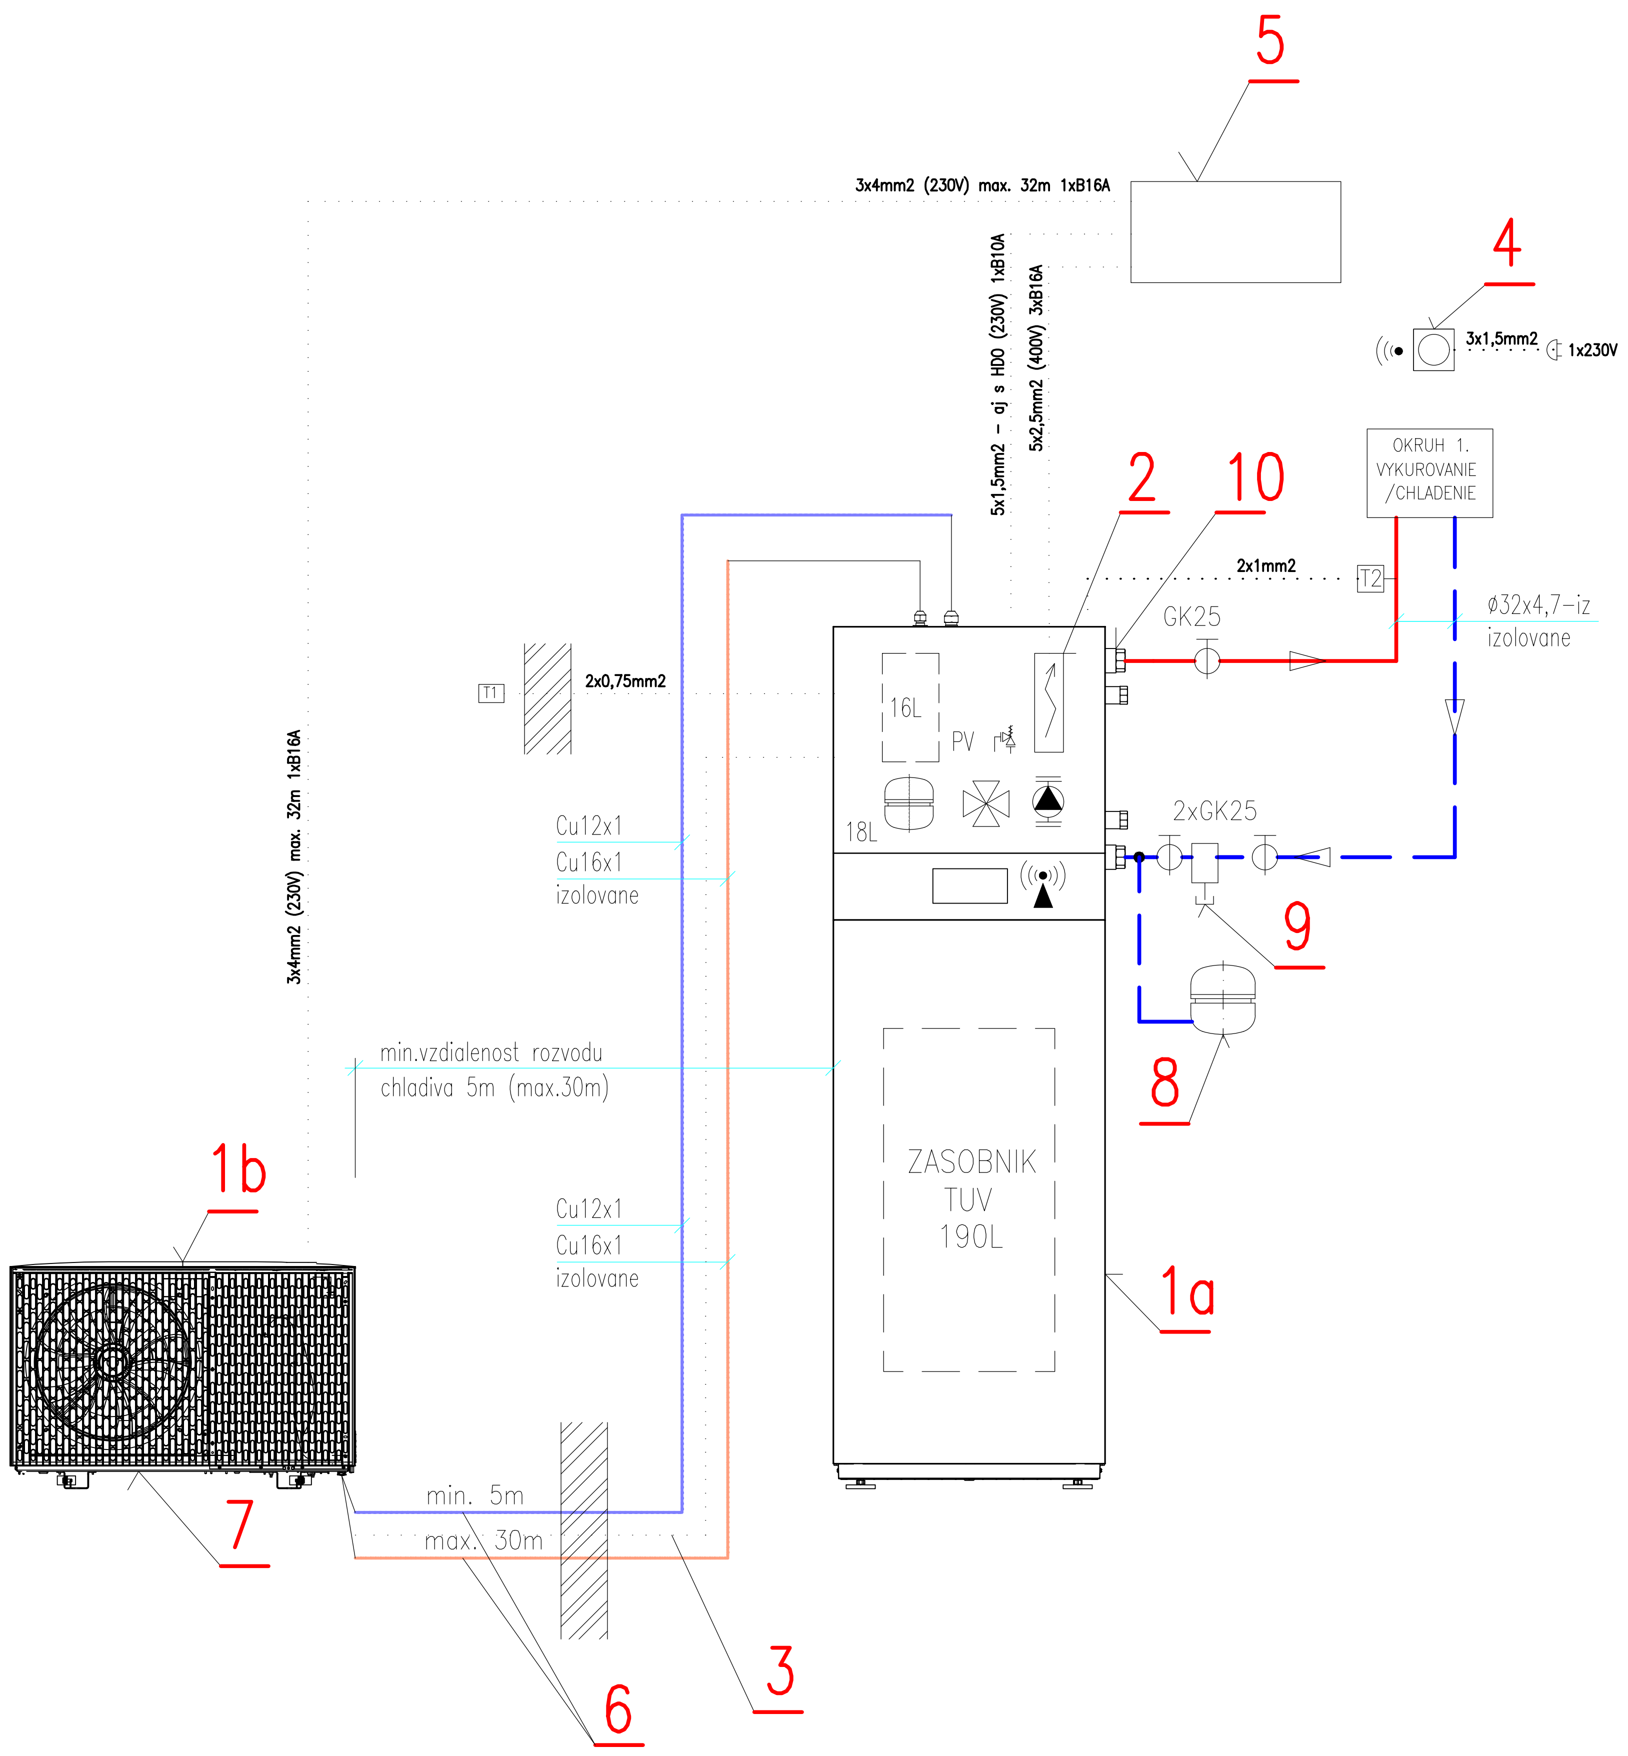

LEGENDA ZARIADENÍ:

POZ.	NÁZOV, ROZMER	P. KS
1a	VNUTORNA JEDNOTKA VITOCAL 222–S AWBT–M–E–AC 221.E06	1
1b	VONKAJ.JEDNOTKA VITOCAL 222–S AWBT–M–E–AC 221.E06 (230V)	1
	MAX.VÝSTUPNÁ TEPLOTA 60°C,TEPELNY VYKON 2,6–7,5kW A7/W35	
	EKOLOGICKE CHLADIVO R32, REGULÁCIA ONE–BASE,WIFI (Z022720)	
2	ELEKTRIC.PRIETOKOVY OHRIEVAC 8kW –v rozsahu dodavky pol.1a	1
3	CANBUS KOMUNIKACNY KABEL MEDZI JEDNOTKY 15m (ZK06217)	1
4	BEZDRATOVÉ DIALKOVE OVLADANIE VITOTROL 300–E (7959522)	1
5	ELEKTRICKY ROZVADZAC OBJEKTU	1
6	INSTALAC.SADA 12/6 NA ZEM+KONZOLA – 12,5M RURY (ZK06312)	1
7	ELEKTRIC.VYHREVNY PAS PRE VANU KONDENZATU 2,5m (ZK04098)	1
8	EXPANZNA NADOBA N25 OBJEM 25L, 3bar BIELA (7938081)	1
	NASTENNY DRZIAK PRE N25 (9572216)	1
9	ODKALOVAC S MAGNETOM A IZOLACIOU VITOTRAP 28mm (ZK04654)	1
10	PRIPOJOVACIA SADA NA OMIETKU–SPRAVA (ZK06403)–treba upresnit	1
T1	SNIMAC VONKAJSEJ TEPLOTY – v rozsahu dodavky tep.cerpadla	1
T2	SNIMAC ROSNEHO BODU – VLHKOSTI (7181418)	1

LEGENDA POTRUBIA:

🟥 🟦	POTRUBIE - PLASTHLINNÍKOVÁ RÚRKA RAUTITAN STABIL, fy. REHAU PRE OKRUHY KONVEKČNÉHO VYKUROVANIA, TEPLOTNÝ SPÁD 50/40°C, PRÍVOD A SPIATOČKA
🟧 🟦	ROZVOD ÚK PRE PRIMÁRNY OKRUH TEPELNÉHO ČERPADLA MATERIÁL MEĎ

LEGENDA ARMATÚR :

GK	GUĽOVÝ KOHÚT ZÁVITOVÝ , PN 16/120°C
UK	UZATVÁRACIA KLAPKA BEZPRÍRUBOVÁ , PN 16/120°C
AOV	AUTOMATICKÝ ODVZDUŠŇOVACÍ VENTIL S UZATVÁRACÍM VENTILOM , PN 16/120°C
VK	VYPÚŠŤACÍ KOHÚT , PN 16/120°C
SK	SPÄTNÁ KLAPKA ZÁVITOVÁ CELOKOVOVÁ ŤAŽKÁ , PN 16/120°C
F	FILTER ZÁVITOVÝ , SITO S OKOM 0,40mm , PN 16/120°C
OV	ODVZDUŠŇOVACÍ VENTIL , PN 16/120°C
PV	POISTNÝ VENTIL ZÁVITOVÝ , PN 16/120°C

POZNÁMKA :

- V PRÍPADE NEJASNOSTÍ VO VÝKRESOVEJ DOKUMENTÁCIÍ KONTAKTOVAŤ ZODPOVEDNÉHO PROJEKTANTA
- VŠETKY ROZMERY STAVEBNÝCH PRÁC KONTROLOVAŤ NA MIESTE STAVBY
- PRED UVEDENÍM SYSTÉMU DO PREVÁDZKY JE POTREBNÉ VYKONAŤ DÔKLADNÝ PREPLACH SYSTÉMU S VYČISTENÍM VŠETKÝCH FILTROV NA ROZVODE
- PO NAPUSTENÍ SYSTÉMU JE POTREBNÉ VYKONAŤ JEHO ODVZDUŠNENIE
- DODÁVATEL STAVBY JE POVINNÝ REALIZOVAŤ VŠETKY PRÁCE V ZMYSLE PLATNÝCH STN EN S DODRŽANÍM TECHNOLOGICKÝCH A BEZPEČNOSTNÝCH POSTUPOV. ĎALEJ JE POVINNÝ REŠPEKTOVAŤ USTANOVENIÁ STN 730421 O PRÍSLUŠNÝCH ROZMEROVÝCH ODCHÝLKACH REALIZOVANÝCH KONŠTRUKCIÍ PROTI PROJEKTOVANÉMU STAVU. KAŽDÚ ODCHÝLKU OD PROJEKTU JE POTREBNÉ PREROKOVAŤ S GP.
- PRESTUPY INŽINIERSKYCH SIETÍ A ROZVODOV V OBJEKTE JE POTREBNÉ VYNECHAŤ PRI REALIZÁCII STAVBY.

Autorom projektu a výhradným vlastníkom autorských a majetkových práv je spoločnosť M PRO s.r.o, Ing. Andrej Marcík. Projektová dokumentácia, ako aj samotné architektonické dielo podlieha autorskej ochrane podľa zákona 185/2015 Z. z. - Autorský zákon v znení neskorších predpisov. Vyhotovenie napodobenín, rozmnožovanie a akékoľvek úpravy bez písomného súhlasu autora je trestné.

Výškové osadenie:
±0,000=
130,875 m.n.m.
(BPV)
Súradnicový systém:
JTSK

Generálny projektant:
M PRO s.r.o.
Kadnárova 23, 831 52 Bratislava
mprosro@gmail.com +421 905 489 533
Ing. Andej Marcík

Autor/Spoluautor:
Ing. Andrej Marcík
Ing. Daniela Marcíková
Ing. Miroslav Greguš
Ing.Ing.arch.Mgr.art.J.Kuráň,PhD.

Projektant časti:
JOPRO group s.r.o.
Trnavská cesta 67, 821 04 Bratislava
jokay@jopro.sk +421 905 549 978
Ing. Norbert Jókay

Zodpovedný projektant:
Ing. Norbert Jókay
Vypracoval:
Bc. Viktor Labovský

Orientácia na svetové strany:

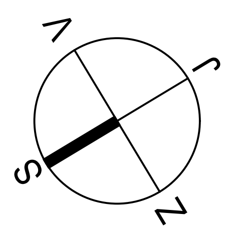

Názov projektu / stavby:
OBECNÝ DOM LIMBACH

Stavebník:
Obec Limbach
SNP 55, 900 91 Limbach

Miesto stavby:
SNP 21/17, 900 91 Limbach
Parcela číslo:
reg.C:144, k.ú. Limbach

Stavebný objekt:
SO-01 OBECNÝ DOM

Stupeň projektovej dokumentácie:
Projekt stavby

Obsah výkresu:
SCHÉMA ZAPOJENIA

Dátum:
09/2025
Formát:
3xA4
Mierka:
1:50
Číslo výkresu:
N.02

Číslo výkresu v zmysle prílohy č.24 vyhlášky 60/2025 Z.z.
252CB3_PSP_01_1241_S01_VYK_N02_SCH_00
1 2 3 4 5 6 7 8 9