
POZ.	NÁZOV, ROZMER	P. KS
1a	VNUTORNA JEDNOTKA VITOCAL 222-S AWBT-M-E-AC 221.E06	1
1b	VONKAJ.JEDNOTKA VITOCAL 222-S AWBT-M-E-AC 221.E06 (230V)	1
	MAX.VÝSTUPNÁ TEPLOTA 60°C,TEPELNY VYKON 2,6-7,5kW A7/W35	
	EKOLOGICKE CHLADIVO R32, REGULÁCIA ONE-BASE,WIFI (Z022722)	
2	ELEKTRIC.PRIETOKOVY OHRIEVAC 8kW -v rozsahu dodavky pol.1a	1
3	CANBUS KOMUNIKACNY KABEL MEDZI JEDNOTKY 15m (ZK06217)	1
4	BEZDRATOVÉ DIALKOVE OVLADANIE VITOTROL 300-E (7959522)	1
5	ELEKTRICKY ROZVADZAC OBJEKTU	1
6	INSTALAC.SADA 12/6 NA ZEM+KONZOLA - 12,5M RURY (ZK06312)	1
7	ELEKTRIC.VYHREVNY PAS PRE VANU KONDENZATU 2,5m (ZK04098)	1
8	EXPANZNA NADOBA N25 OBJEM 25L, 3bar BIELA (7938081)	1
	NASTENNY DRZIAK PRE N25 (9572216)	1
9	ODKALOVAC S MAGNETOM A IZOLACIOU VITOTRAP 28mm (ZK04654)	1
10	PRIPOJOVACIA SADA NA OMIETKU-ZHORA	1
TE	SNIMAC VONKAJSEJ TEPLOTY - v rozsahu dodavky tep.cerpadla	1
T2	SNIMAC ROSNEHO BODU - VLHKOSTI (7181418)	1

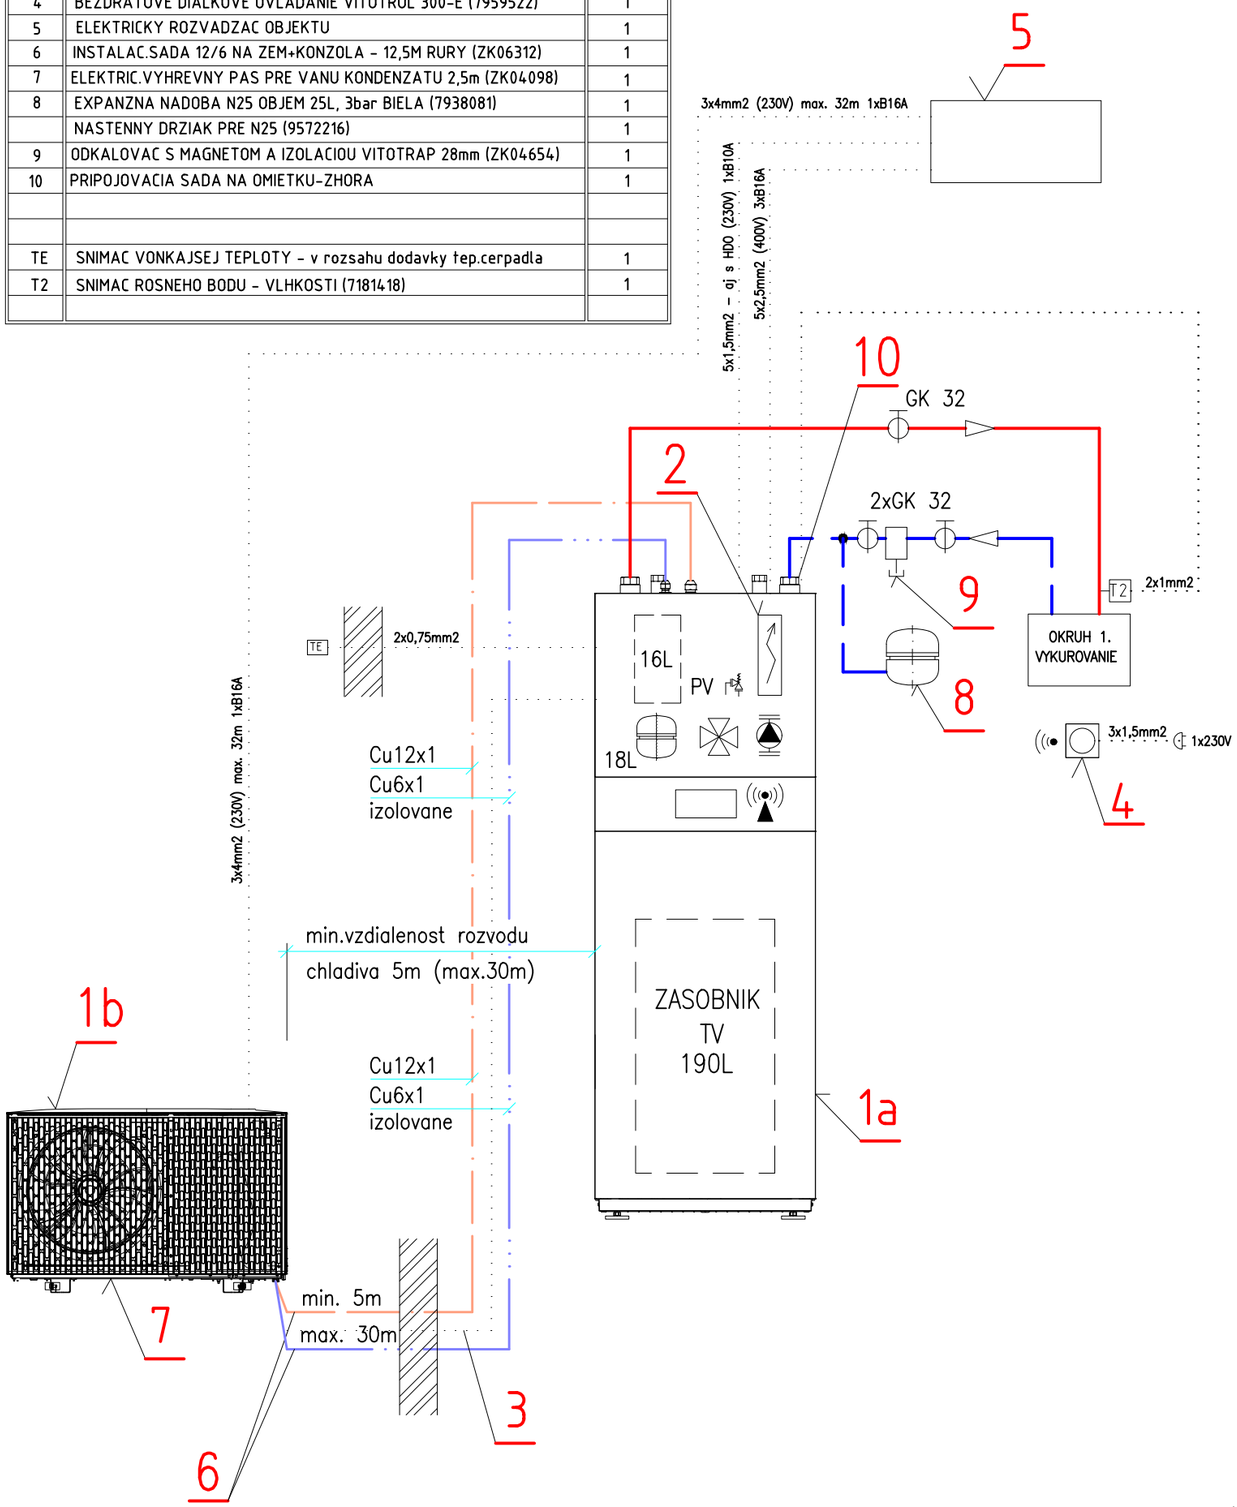

LEGENDA POTRUBIA:

POTRUBIE - PLASTHLINNÍKOVÁ RURKA PE-Xa/AL/PE napr. RAUTITAN Stabil REHAU
SPÁJANÉ LISOVANÍM, IZOLOVANÉ POTRUBIE, TEPLOTNÝ SPÁD 45/35°C

ROZVOD ÚK PRE PRIMÁRNY OKRUH TEPELNÉHO ČERPADLA
MATERIÁL MEĎ

LEGENDA ARMATÚR :

OV	ODVZDUŠŇOVACÍ VENTIL , PN 16/120°C
GK	GULOVÝ KOHÚT ZÁVITOVÝ , PN 16/120°C
AOV	AUTOMATICKÝ ODVZDUŠŇOVACÍ VENTIL S UZATVÁRACÍM VENTILOM , PN 16/120°C
VK	VYPÚŠŤACÍ KOHÚT , PN 16/120°C
F	FILTER ZÁVITOVÝ , SITO S OKOM 0,75mm , PN 16/120°C
PV	POISTNÝ VENTIL, OTVÁRACÍ PRETLAK 300 kPa

POZNÁMKA :

- V PRÍPADE NEJASNOSTÍ VO VÝKRESOVEJ DOKUMENTÁCII KONTAKTOVAŤ ZODPOVEDNÉHO PROJEKTANTA
- VŠETKY ROZMERY STAVEBNÝCH PRÁC KONTROLOVAŤ NA MIESTE STAVBY
- PRED UVEDENÍM SYSTÉMU DO PREVÁDZKY JE POTREBNÉ VYKONAŤ DÔKLADNÝ PREPLACH SYSTÉMU S VYČISTENÍM VŠETKÝCH FILTROV NA ROZVODE
- PO NAPUSTENÍ SYSTÉMU JE POTREBNÉ VYKONAŤ JEHO ODVZDUŠNENIE
- DODÁVATEL STAVBY JE POVINNÝ REALIZOVAŤ VŠETKY PRÁCE V ZMYSLE PLATNÝCH STN EN S DODRŽANÍM TECHNOLOGICKÝCH A BEZPEČNOSTNÝCH POSTUPOV. ĎALEJ JE POVINNÝ REŠPEKTOVAŤ USTANOVENIÁ STN 730421 O PRÍSLUŠNÝCH ROZMEROVÝCH ODCHÝLKACH REALIZOVANÝCH KONŠTRUKCIÍ PROTI PROJEKTOVANÉMU STAVU. KAŽDÚ ODCHÝLKU OD PROJEKTU JE POTREBNÉ PREROKOVAŤ S GP.

ddak Doršic Doršicová
Architektonická Kancelária
záhradnícka 36, bratislava

OPRÁVNENÝ PROJEKTANT:	ING. NORBERT JÓKAY TRNAVSKÁ CESTA 67, 821 04 BRATISLAVA
VYPRACOVAL:	BC. VIKTOR LABOVSKÝ
INVESTOR:	ING.LUBOŠ GAJDOŠÍK a manž. ING.LENKA GAJDOŠíKOVÁ FRAŇA KRÁLA 1/B, 903 01 SENEC

NÁZOV STAVBY:

novostavba RD

MIESTO: SENEC, POD VINICAMI p.č. 5299/19, 5301/8
PROFESIA: VYKUROVANIE
NÁZOV VÝKRESU:

Schéma zapojenia

DÁTUM:	01_2026
MIERKA:	
FORMÁT:	2XA4
SADA	VÝKRES Č.: 2