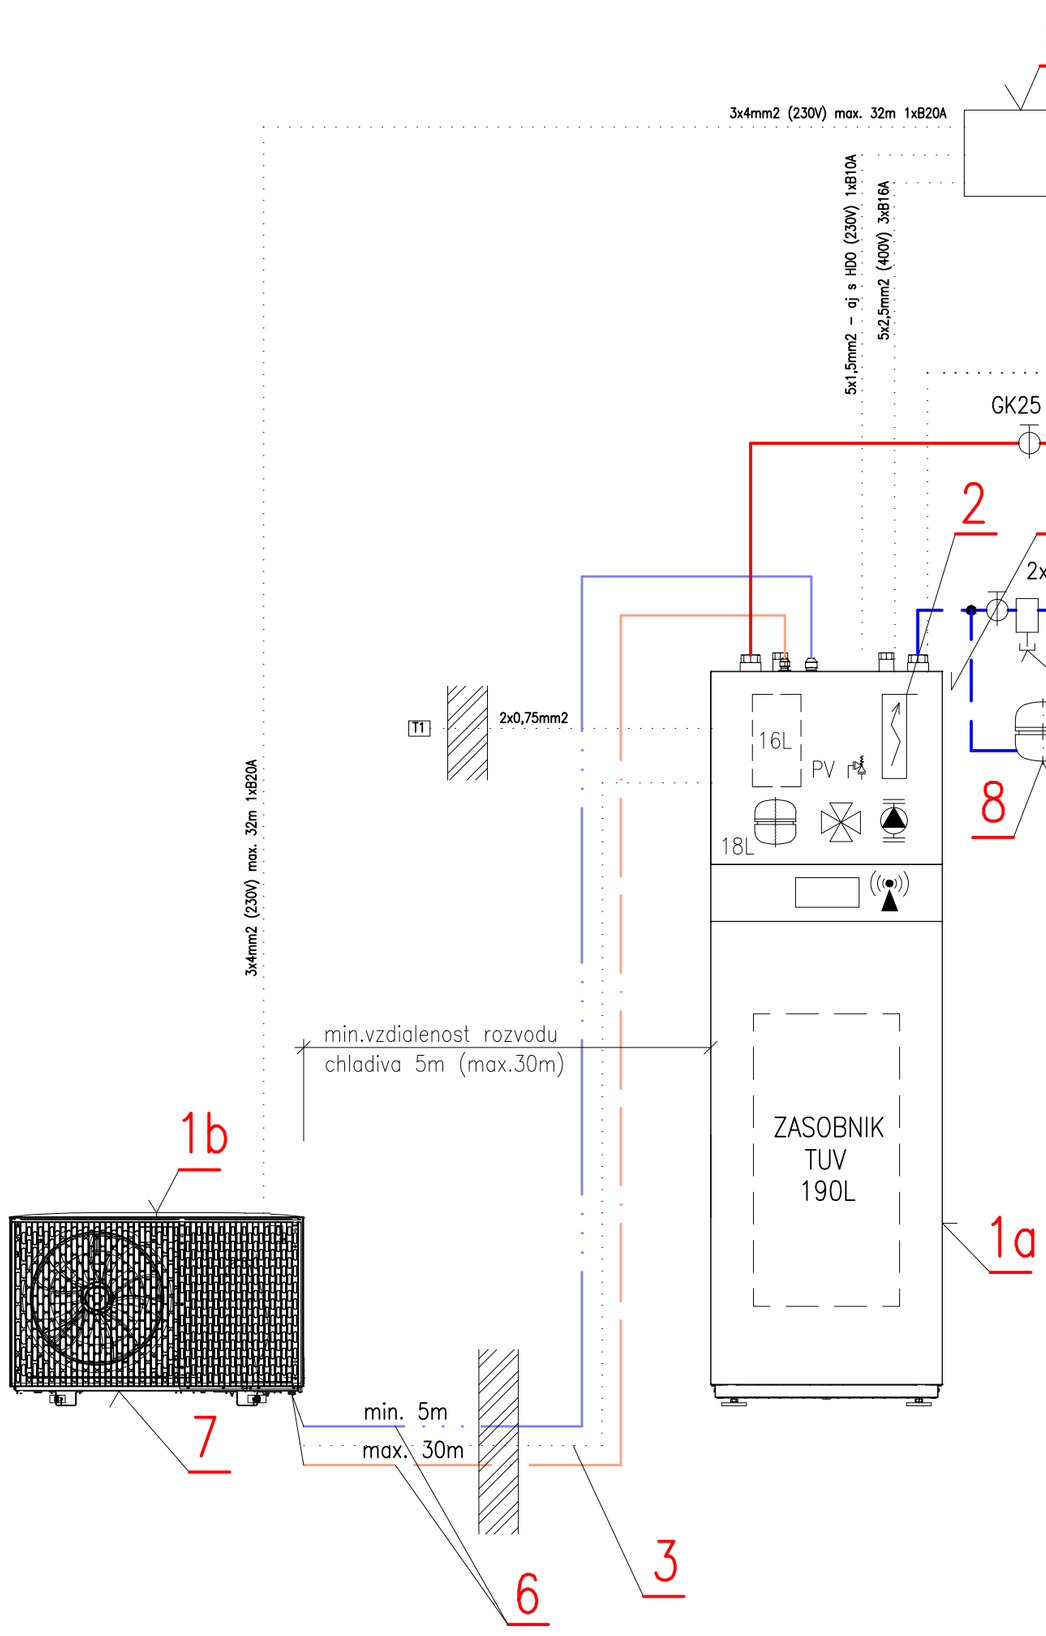


LEGENDA ZARIADENÍ:

POZ.	NÁZOV, ROZMER	P. KS
1a	VNUTORNA JEDNOTKA VITOCAL 222-S AWBT-M-E-AC 221.E10	1
1b	VONKAJ.JEDNOTKA VITOCAL 222-S AWBT-M-E-AC 221.E10 (230V)	1
	MAX.VÝSTUPNÁ TEPLOTA 60°C,TEPELNY VYKON 2,6-10,4kW A7/W35	
	EKOLOGICKE CHLADIVO R32, REGULÁCIA ONE-BASE,WIFI (Z022724)	
2	ELEKTRIC.PRIETOKOVY OHRIEVAC 8kW -v rozsahu dodavky pol.1a	1
3	CANBUS KOMUNIKACNY KABEL MEDZI JEDNOTKY 15m (ZK06217)	1
4	BEZDRATOVÉ DIALKOVE OVLADANIE VITOTROL 300-E (7959522)	1
5	ELEKTRICKY ROZVADZAC OBJEKTU	1
6	INSTALAC.SADA 16/6 NA ZEM+KONZOLA - 12,5M RURY (ZK06313)	1
7	ELEKTRIC.VYHREVNY PAS PRE VANU KONDENZATU 2,5m (ZK04098)	1
8	EXPANZNA NADOBA N25 OBJEM 25L, 3bar BIELA (7938081)	1
	NASTENNY DRZIAK PRE N25 (9572216)	1
9	ODKALOVAC S MAGNETOM A IZOLACIOU VITOTRAP 28mm (ZK04654)	1
10	PRIPOJOVACIA SADA NA OMIETKU-ZHORA	1
T1	SNIMAC VONKAJSEJ TEPLOTY - v rozsahu dodavky tep.cerpadla	1
T2	SNIMAC ROSNEHO BODU - VLHKOSTI (7181418)	1

LEGENDA POTRUBIA:

POTRUBIE - PLASTHLINNÍKOVÁ RÚRKA NAPR. GEBERIT MEPLA
PRE OKRUH PODLAHOVÉHO VYKUROVANIA, TEPLOTNÝ SPÁD 45/35°C, PRÍVOD A SPATOČKA

ROZVOD ÚK PRE PRIMÁRNY OKRUH TEPELNÉHO ČERPADLA
MATERIÁL MEĎ

LEGENDA ARMATÚR :

GK GUĽOVÝ KOHÚT ZÁVITOVÝ , PN 16/120°C
UK UZATVÁRACIA KLAPKA BEZPRÍRUBOVÁ , PN 16/120°C
AOV AUTOMATICKÝ ODVZDUŠŇOVACÍ VENTIL S UZATVÁRACÍM VENTILOM , PN 16/120°C
VK VYPÚŠŤACÍ KOHÚT , PN 16/120°C
SK SPÄTNÁ KLAPKA ZÁVITOVÁ CELOKOVOVÁ ŤAŽKÁ , PN 16/120°C
F FILTER ZÁVITOVÝ , SITO S OKOM 0,40mm , PN 16/120°C
OV ODVZDUŠŇOVACÍ VENTIL , PN 16/120°C
PV POISTNÝ VENTIL ZÁVITOVÝ , PN 16/120°C

VYKUROVANIE

A-DESIGN s.r.o.
ARCHITEKTONICKÝ ATELIÉR
HABURSKÁ 20 ; 821 01 BRATISLAVA

NÁZOV STAVBY: OBČIANSKÁ VYBAVENOSŤ - NOVÝ SVET
MIESTO STAVBY: NOVÝ SVET ; K.ú. Nový Svet; Okr.Senec P.č. 341/370,371

GENERÁLNY PROJEKTANT:	A-DESIGN s.r.o. BRATISLAVA	INVESTOR:	Ing. Verner Richard Bratislavská 9110/2F, 841 06 Bratislava	Stupeň PD:	STAVEBNÝ ZÁMER
HIP:	Ing.arch.I.POHANIČ		Ing. Čierny Matrin Šípková ulica 1257/6, 900 42 Miloslavov	DÁTUM:	11/2025
				ZÁK.ČÍSLO	852025
ZODPOVEDNÝ PROJEKTANT:	Ing. N. JÓKAY	STAVEBNÝ OBJEKT:	SO-01 Občianská vybavenosť	FORMÁT	2xA4
				MIERKA:	
VYPRACOVAL:	Bc. Viktor Labovský	OBSAH:	SCHÉMA ZAPOJENIA	Č.VÝKRESU:	04