- 1.7 -	
Garáž	
19.5 m2	45.1 m3
-1 °C	0 W

- 1.6 -	
Obývačka + kuchyňa	
24.9 m2	57.4 m3
22 °C	1375 W

- 1.1 -	
Vstup	
17.5 m2	40.3 m3
20 °C	1136 W

- 1.5 -	
Spálňa	
11.2 m2	25.8 m3
22 °C	561 W

- 1.3 -	
Chodba	
10.7 m2	24.7 m3
22 °C	307 W

- 1.4 -	
Hygiena	
4.7 m2	10.8 m3
24 °C	209 W

LEGENDA MIESTNOSTÍ 1.NP

ČÍSLO	MIESTNOSŤ	M²
1.01	VSTUP	11,89
1.02	SCHODISKO	5,6
1.03	CHODBA	9,54
1.04	HYGIENA	4,7
1.05	SPÁLŇA	11,2
1.06	OBYTNÝ PRIESTOR	24,48
1.07	GARÁŽ	19,37
	TERASA	17,50

ÚŽITKOVÁ PLOCHA 1.NP 86,78m²
CELKOVÁ ÚŽITKOVÁ PLOCHA OBJEKTU 204,29m²

LEGENDA PODLAHOVÉHO VYKUROVANIA:

PODLAHOVÉ KÚRENIE REHAU

Lpz=100 [mm] ROZOSTUP VYK. RÚROK
S=8,6 m2 VYKUROVACIA PLOCHA
PZ: Keramická dlažba TYP NÁŠLAPNEJ VRSTVY
Rúrka RAUTHERM S 17x2,0 TYP VYKUROVACEJ RÚRKY
Nasť.=0,63 (48 kg/h) NASTAVENIE REG. OKRUHU(PRIETOK)
lo/lp=12.7 m/1.6 m Dĺžka okruhu / dĺžka prípojky
RZ 1.NP (1) (tp=45°C) rozdelovač na 1.NP 1. napojenie a
VARIONOVA 9 vetiev (tp - teplota prívodu)
PZ:21°C typ prichytenia potrubi pre podlahove kurenie
maximálna povrchová teplota podlahovej zóny

LEGENDA POTRUBIA:

POTRUBIE - PLASTHLINNÍKOVÁ RURKA PE-Xa/AL/PE napr. RAUTITAN Stabil REHAU
SPÁJANÉ LISOVANÍM, IZOLOVANÉ POTRUBIE, TEPLOTNÝ SPÁD 45/35°C. PRE PODLAHOVÉ VYKUROVANIE

POTRUBIE - PLASTHLINNÍKOVÁ RÚRKA NAPR. GEBERIT MEPLA
SPÁJANÉ LISOVANÍM, IZOLOVANÉ POTRUBIE, TEPLOTNÝ SPÁD 45/35°C

ROZVOD ÚK PRE PRIMÁRNY OKRUH TEPELNÉHO ČERPADLA
PRE OKRUHY KONVEKČNÉHO VYKUROVANIA, PRÍVOD A SPATOČKA
MATERIÁL MEĎ

LEGENDA VYKUROVACÍCH TELIES:

EL1 - ELEKTRICKÝ RADIÁTOR (MIN. VÝKON 700W), PRESNÝ TYP URČÍ ARCHITEKT
EL2 - ELEKTRICKÝ REBRÍKOVÝ RADIÁTOR (MIN. VÝKON 300W), PRESNÝ TYP URČÍ ARCHITEKT

LEGENDA VYKUROVACÍCH TELIES:


ST05 - ELEKTRICKÉ SÁLAVÉ PANELY (MIN. VÝKON 400W), PRESNÝ TYP URČÍ ARCHITEKT
ST06 - ELEKTRICKÉ SÁLAVÉ PANELY (MIN. VÝKON 300W), PRESNÝ TYP URČÍ ARCHITEKT
ST07 - ELEKTRICKÉ SÁLAVÉ PANELY (MIN. VÝKON 750W), PRESNÝ TYP URČÍ ARCHITEKT

RZ 2 - 1.NP (6/1) (tp=45.0°C)	1.1 - Vstup
PZ 1: Keramická dlažba	VYK: PZ:27.2°C
Systém VARIONOVA	Rúrka RAUTHERM S 17x2,0
lo/lp=79.5 m/2.4 m	S=7.9 m2
Lpz=100 [mm]	VYK: 1.3 l/min

RZ 2 - 1.NP (6/2) (tp=45.0°C)	1.3 - Chodba
PZ 1: Drevené parkety 18mm	VYK: PZ:26.9°C
Systém VARIONOVA	Rúrka RAUTHERM S 17x2,0
lo/lp=23.4 m/11.9 m	S=2.3 m2
Lpz=100 [mm]	VYK: 0.2 l/min

RZ 2 - 1.NP (6/3) (tp=45.0°C)	1.4 - Hygiena
PZ 1: Keramická dlažba	VYK: PZ:30.4°C
Systém VARIONOVA	Rúrka RAUTHERM S 17x2,0
lo/lp=57.8 m/17.6 m	S=2.9 m2
Lpz=50 [mm]	VYK: 0.5 l/min

RZ 2 - 1.NP (6/4) (tp=45.0°C)	1.5 - Spálňa
PZ 1: Drevené parkety	VYK: PZ:24.7°C [OZ:25.1°C]
Systém VARIONOVA	Rúrka RAUTHERM S 17x2,0
lo/lp=86.3 m/19.5 m	S=11.2 m2
Lpz/Loz=150/100 [mm]	VYK: 0.6 l/min

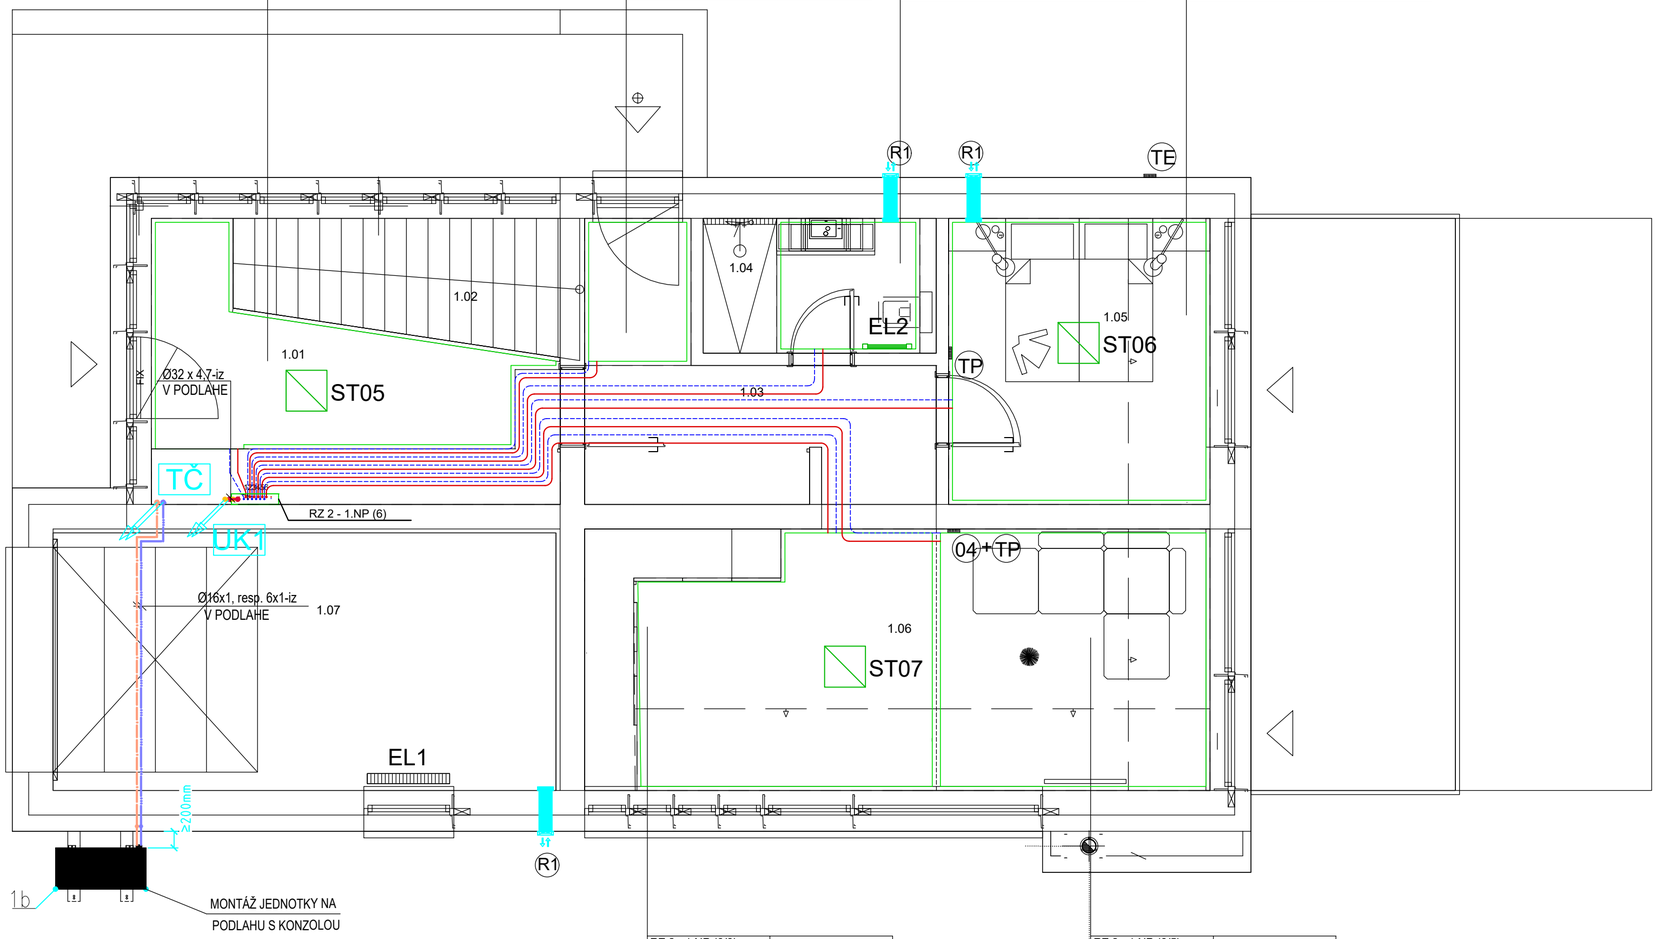

RZ 2 - 1.NP (6/6) (tp=45.0°C)	PZ 1: Drevené parkety
Systém VARIONOVA	l-celk=89.1 m
Lpz=150 [mm]	1.6 - Obývačka + kuchyňa
VYK: PZ:25.1°C	Rúrka RAUTHERM S 17x2,0
S=10.7 m2	VYK: 1.1 l/min

RZ 2 - 1.NP (6/5) (tp=45.0°C)	PZ 1: Drevené parkety
Systém VARIONOVA	l-celk=92.7 m
Lpz=150 [mm]	1.6 - Obývačka + kuchyňa
VYK: PZ:25.1°C	Rúrka RAUTHERM S 17x2,0
S=10.7 m2	VYK: 1.1 l/min

LEGENDA ZARIADENÍ A ARMATÚR :

1a KOMPAKTNÁ VNÚTORNÁ JEDNOTKA TEPELNÉHO ČERPADLA VITOCAL 222-S AWBT-M-E 221.E06
1b VONKAJ.JEDNOTKA VITOCAL 222-S AWBT-M-E 221.E06 (230V)
MAX.VÝSTUPNÁ TEPLOTA 60°C,TEPELNY VYKON 2,6-7,5kW A7/W35
EKOLOGICKE CHLADIVO R32, REGULÁCIA ONE-BASE,WIFI (Z022722)
04 BEZDRÔTOVÉ DIAĽKOVÉ OVLÁDANIE VITOTROL 300-E
08 UZAVRETÁ TLAKOVÁ EXPANZNÁ NÁDOBA VIESSMANN N25 OBJEM 25L, 3bar
ROZMERY : Ø=308 mm, VÝŠKA 477 mm , HMOTNOSŤ 4,3 kg + NASTENNY DRZIAK PRE N25 (9572216)
TP PRIESTOROVÝ REGULÁTOR NEA SMART 2.0 PRE MERANIE TEPLOTY V MIESTNOSTI, FY. REHAU
TE SNÍMAČ VONKAJŠEJ TEPLOTY
OV ODVZDUŠŇOVACÍ VENTIL , PN 16/120°C
TČ STUPACIE POTRUBIE PRIMÁRNEHO OKRUHU TEPELNÉHO ČERPADLA
UK1 STUPACIE POTRUBIE PODLAHOVÉHO VYKUROVANIA (Ø 32 x 4,7)

R1 DECENTRÁLNA REKUPERAČNÁ JEDNOTKA VIESSMANN VITOVENT 100-D, TYP H40E B55 (F)
VZDUCHOVÝ VÝKN S VENTILÁTOROM MAX. 55 m3/h, TRIEDA FILTRÁCIE G3, EL. PRIPOJENIE 230 V / 50 Hz
PRECHOD CEZ STENU Ø162 MM, HLUČNOSŤ NAJVIAC 46,2 dB, NAJMENENJ 24,8 dB
ROZMER 218x218x32,8 (výška * šírka * hĺbka), POLOHA OSADENIA = OS +2,00m OD H.P., 0,4m OD STENY
SPOTREBA PRÍKON MAX. 6,9 W, ÚČINNOSŤ REKUPERÁCIE 87%, BIELA FARBA

POZNÁMKA :

- V PRÍPADE NEJASNOSTÍ VO VÝKRESOVEJ DOKUMENTÁCII KONTAKTOVAŤ ZODPOVEDNÉHO PROJEKTANTA
- VŠETKY ROZMERY STAVEBNÝCH PRÁC KONTROLOVAŤ NA MIESTE STAVBY
- PRED UVEDENÍM DO PREVÁDZKY JE POTREBNÉ VYKONAŤ DÔKLADNÝ PREPLACH SYSTÉMU S VYČISTENÍM VŠETKÝCH FILTROV NA ROZVODE
- PO NAPUSTENÍ SYSTÉMU JE POTREBNÉ VYKONAŤ JEHO ODVZDUŠNENIE
- DODÁVATEL STAVBY JE POVINNÝ REALIZOVAŤ VŠETKY PRÁCE V ZMYSLE PLATNÝCH STN EN S DODRŽANÍM TECHNOLOGICKÝCH A BEZPEČNOSTNÝCH POSTUPOV. JE POVINNÝ REŠPEKTOVAŤ USTANOVENIA STN 730421 O PRÍSLUŠNÝCH ROZMEROVÝCH ODCHÝLKACH KONŠTRUKCIÍ PROTI PROJEKTOVANÉMU STAVU. KAŽDÚ ODCHÝLKU OD PROJEKTU JE POTREBNÉ PREROKOVAŤ S GP.

0 2,5 5 7,5 10

názov stavby:	**RODINNÝ DOM NEMCOVÁ**
investor:	NEMCOVÁ Tatiana r. Matušovská, Mgr., PhDr., Na Roličkách 14003/6, Bratislava, PSČ 831 03,SR
obec: BA. - NOVÉ MESTO	katastrálne územie: VINOHRADY / okres: BRATISLAVA III. / parcelné číslo: 18368/1, 18368/2
zodpovedný projektant:	Ing. Norbert Jókay / kresli: Bc. Viktor Labovský / dátum: 01/2026 / mierka: 1:50
autor projektu:	Ing. arch. Lucia ULRICHOVÁ / stupeň: SZ, PS / formát: 630x420
názov výkresu:	**PÔDORYS 1.NP** / číslo výkresu: P 0 2 / 02