- 1.02 -	
TZB + Toaleta	
12.7 m2	36.8 m3
20 °C	292 W

- 1.01 -	
Chodba	
18.8 m2	54.5 m3
22 °C	401 W

- 1.06 -	
Hygiena 2	
5.4 m2	15.8 m3
24 °C	244 W

- 1.03 -	
Spalňa	
19.8 m2	57.5 m3
22 °C	885 W

- 1.08 -	
Obývačka + kuhcyna	
46.4 m2	105.9 m3
22 °C	2637 W

- 1.04 -	
Hygiena 1	
6.9 m2	20.0 m3
24 °C	413 W

- 1.05 -	
Izba	
10.6 m2	30.6 m3
22 °C	576 W

LEGENDA MIESTNOSTÍ 1.PP

ČÍSLO	MIESTNOSŤ	M²
01.01	CHODBA	16,6
01.02	TOALETA + TZB	8,95
01.03	SPÁLŇA	19,84
01.04	HYGIENA	6,88
01.05	IZBA	10,56
01.06	HYGIENA	5,44
01.07	ŠPAJZA	2,88
01.08	HLAVNÝ OBYTNÝ PRIESTOR	46,36

ÚŽITKOVÁ PLOCHA 1.PP
CELKOVÁ ÚŽITKOVÁ PLOCHA OBJEKTU

LEGENDA PODLAHOVÉHO VYKUROVANIA:

🟩 PODLAHOVÉ KÚRENIE REHAU

Lpz=100 [mm]	ROZOSTUP VYK. RÚROK
S=8,6 m2	VYKUROVACIA PLOCHA
PZ: Keramická dlažba	TYP NÁŠLAPNEJ VRSTVY
Rúrka RAUTHERM S 17x2,0	TYP VYKUROVACEJ RÚRKY
Nast.=0,63 (48 kg/h)	NASTAVENIE REG. OKRUHU(PRIETOK)
lo/lp=12.7 m/1.6 m	Dlžka okruhu / dlžka prípojky
RZ 1. NP-1 (tp=45°C) 177,59m²	rozdelovač na 1 .NP 1. napojenie a
VARIONOVA 204,29m²	9 vetiev (tp - teplota prívodu)
PZ:21°C	typ prichytenia potrubi pre podlahove kurenie
	maximálna povrchová teplota podlahovej zóny

LEGENDA POTRUBIA:

🟥	POTRUBIE - PLASTHLINNÍKOVÁ RURKA PE-Xa/AL/PE napr. RAUTITAN Stabil REHAU SPÁJANÉ LISOVANÍM, IZOLOVANÉ POTRUBIE, TEPLOTNÝ SPÁD 45/35°C. PRE PODLAHOVÉ VYKUROVANIE
🟥	POTRUBIE - PLASTHLINNÍKOVÁ RÚRKA NAPR. GEBERIT MEPLA SPÁJANÉ LISOVANÍM, IZOLOVANÉ POTRUBIE, TEPLOTNÝ SPÁD 45/35°C
🟦	ROZVOD ÚK PRE PRIMÁRNY OKRUH TEPELNÉHO ČERPADLA PRE OKRUHY KONVEKČNÉHO VYKUROVANIA, PRÍVOD A SPATOČKA MATERIÁL MEĎ

LEGENDA VYKUROVACÍCH TELIES:

EL2 - ELEKTRICKÝ REBRÍKOVÝ RADIÁTOR (MIN. VÝKON 300W), PRESNÝ TYP URČÍ ARCHITEKT

LEGENDA VYKUROVACÍCH TELIES:

ST01 - ELEKTRICKÉ SÁLAVÉ PANELY (MIN. VÝKON 300W), PRESNÝ TYP URČÍ ARCHITEKT
ST02 - ELEKTRICKÉ SÁLAVÉ PANELY (MIN. VÝKON 300W), PRESNÝ TYP URČÍ ARCHITEKT
ST03 - ELEKTRICKÉ SÁLAVÉ PANELY (MIN. VÝKON 750W), PRESNÝ TYP URČÍ ARCHITEKT
ST04 - ELEKTRICKÉ SÁLAVÉ PANELY (MIN. VÝKON 750W), PRESNÝ TYP URČÍ ARCHITEKT

RZ 1 - 1.PP (11/1) (tp=45.0°C)	1.02 - TZB + Toaleta
PZ 1: Keramická dlažba	VYK: PZ:31.4°C
Systém VARIONOVA	Rúrka RAUTHERM S 17x2,0
lo/lp=39.8 m/2.6 m	S=4.0 m2
Lpz=100 [mm]	VYK: 0.9 l/min

RZ 1 - 1.PP (11/2) (tp=45.0°C)	1.01 - Chodba
PZ 1: Keramická dlažba	VYK: PZ:27.9°C
Systém VARIONOVA	Rúrka RAUTHERM S 17x2,0
lo/lp=56.4 m/8.6 m	S=8.5 m2
Lpz=150 [mm]	VYK: 1.2 l/min

RZ 1 - 1.PP (11/3) (tp=45.0°C)	1.06 - Hygiena 2
PZ 1: Keramická dlažba	VYK: PZ:32.8°C
Systém VARIONOVA	Rúrka RAUTHERM S 17x2,0
lo/lp=32.0 m/30.4 m	S=3.2 m2
Lpz=100 [mm]	VYK: 0.7 l/min

RZ 1 - 1.PP (11/4) (tp=45.0°C)	1.08 - Obývačka + kuhcyna
PZ 1: Drevené parkety	VYK: PZ:24.8°C
Systém VARIONOVA	Rúrka RAUTHERM S 17x2,0
lo/lp=62.1 m/23.0 m	S=9.3 m2
Lpz=150 [mm]	VYK: 0.6 l/min

RZ 1 - 1.PP (11/5) (tp=45.0°C)	1.08 - Obývačka + kuhcyna
PZ 1: Drevené parkety	VYK: PZ:24.2°C [OZ:24.2°C]
Systém VARIONOVA	Rúrka RAUTHERM S 17x2,0
lo/lp=63.6 m/32.6 m	S=9.5 m2
Lpz/Loz=150/150 [mm]	VYK: 0.4 l/min

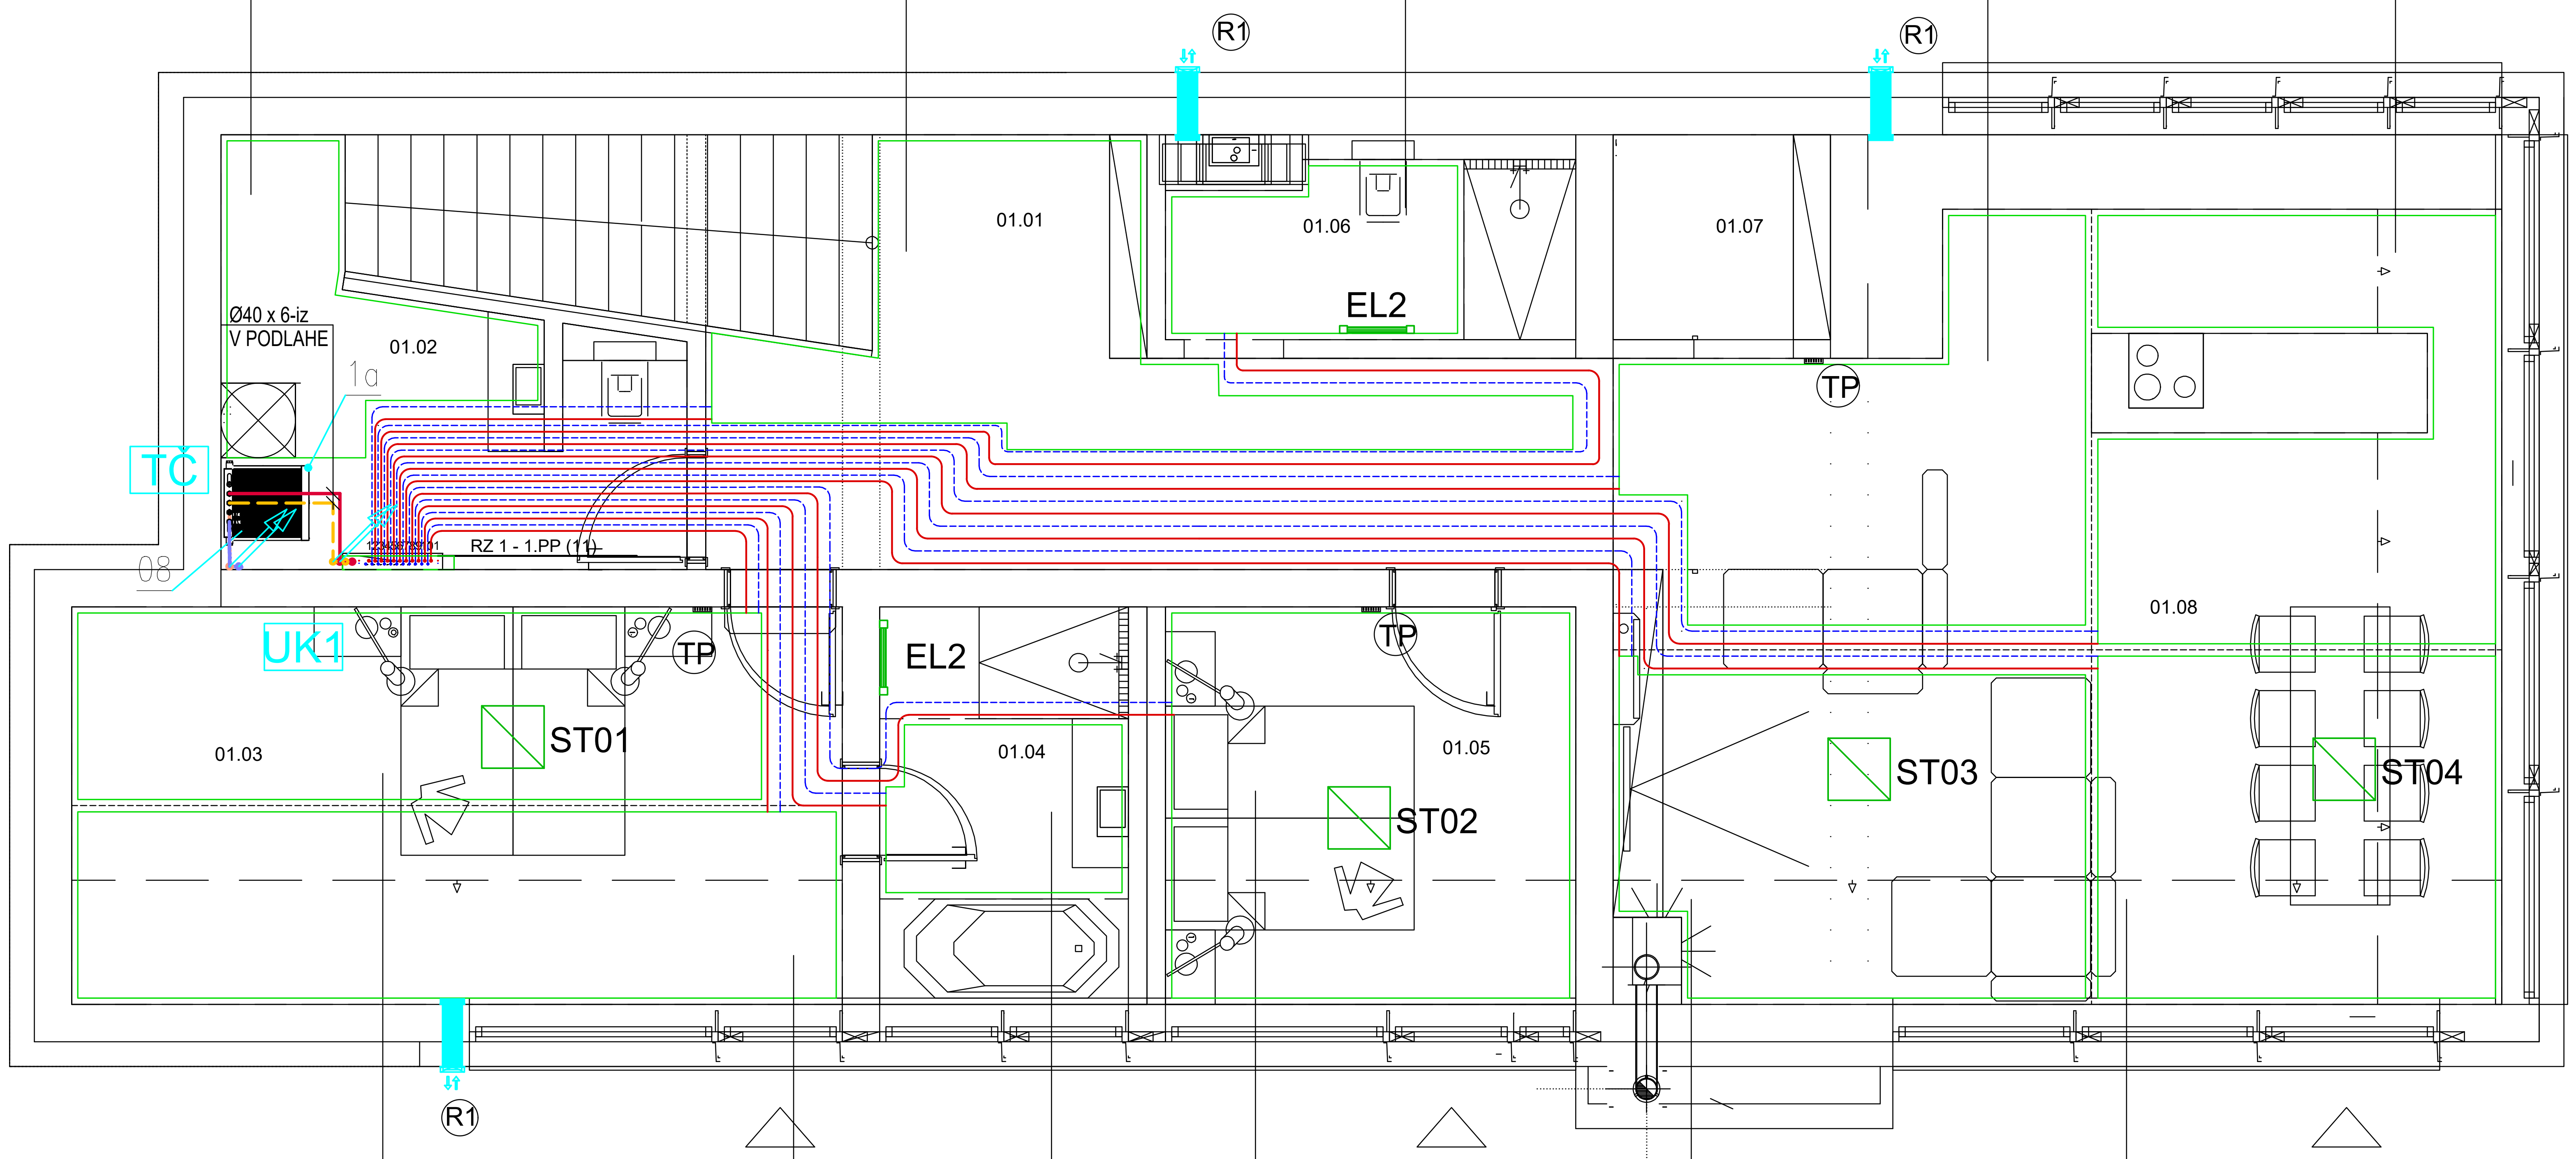

LEGENDA ZARIADENÍ A ARMATÚR :

1a	KOMPAKTNÁ VNÚTORNÁ JEDNOTKA TEPELNÉHO ČERPADLA VITOCAL 222-S AWBT-M-E 221.E06
1b	VONKAJ.JEDNOTKA VITOCAL 222-S AWBT-M-E 221.E06 (230V) MAX.VÝSTUPNÁ TEPLOTA 60°C,TEPELNY VYKON 2,6-7,5kW A7/W35 EKOLOGICKE CHLADIVO R32, REGULÁCIA ONE-BASE,WIFI (Z022722)
04	BEZDRÔDOTVÉ DIAĽKOVÉ OVLÁDANIE VITOTROL 300-E
08	UZAVRETÁ TLAKOVÁ EXPANZNÁ NÁDOBA VIESSMANN N25 OBJEM 25L, 3bar ROZMERY : Ø=308 mm, VÝŠKA 477 mm , HMOTNOSŤ 4,3 kg + NASTENNY DRZIAK PRE N25 (9572216)
TP	PRIESTOROVÝ REGULÁTOR NEA SMART 2.0 PRE MERANIE TEPLOTY V MIESTNOSTI, FY. REHAU
TE	SNÍMAČ VONKAJŠEJ TEPLOTY
OV	ODVZDUŠŇOVACÍ VENTIL , PN 16/120°C
TČ	STUPACIE POTRUBIE PRIMÁRNEHO OKRUHU TEPELNÉHO ČERPADLA
UK1	STUPACIE POTRUBIE PODLAHOVÉHO VYKUROVANIA (Ø 32 x 4,7)
R1	DECENTRÁLNA REKUPERAČNÁ JEDNOTKA VIESSMANN VITOVENT 100-D, TYP H40E B55 (F) VZDUCHOVÝ VÝKN S VENTILÁTOROM MAX. 55 m3/h, TRIEDA FILTRÁCIE G3, EL. PRIPOJENIE 230 V / 50 Hz PRECHOD CEZ STENU Ø162 MM, HLUČNOSŤ NAJVIAC 46,2 dB, NAJMENENJ 24,8 dB ROZMER 218x218x32,8 (výška * šírka * hĺbka), POLOHA OSADENIA = OS +2,00m OD H.P., 0,4m OD STENY SPOTREBA PRÍKON MAX. 6,9 W, ÚČINNOSŤ REKUPERÁCIE 87%, BIELA FARBA

POZNÁMKA :

- V PRÍPADE NEJASNOSTÍ VO VÝKRESOVEJ DOKUMENTÁCIÍ KONTAKTOVAŤ ZODPOVEDNÉHO PROJEKTANTA
- VŠETKY ROZMERY STAVEBNÝCH PRÁC KONTROLOVAŤ NA MIESTE STAVBY
- PRED UVEDENÍM DO PREVÁDZKY JE POTREBNÉ VYKONAŤ DÔKLADNÝ PREPLACH SYSTÉMU S VYČISTENÍM VŠETKÝCH FILTROV NA ROZVODE
- PO NAPUSTENÍ SYSTÉMU JE POTREBNÉ VYKONAŤ JEHO ODVZDUŠNENIE
- DODÁVATEL STAVBY JE POVINNÝ REALIZOVAŤ VŠETKY PRÁCE V ZMYSLE PLATNÝCH STN EN S DODRŽANÍM TECHNOLOGICKÝCH A BEZPEČNOSTNÝCH POSTUPOV. JE POVINNÝ REŠPEKTOVAŤ USTANOVENIÁ STN 730421 O PRÍSLUŠNÝCH ROZMEROVÝCH ODCHÝLKACH KONŠTRUKCIÍ PROTI PROJEKTOVANÉMU STAVU. KAŽDÚ ODCHÝLKU OD PROJEKTU JE POTREBNÉ PREROKOVAŤ S GP.

RZ 1 - 1.PP (11/11) (tp=45.0°C)	1.03 - Spalňa
PZ 1: Drevené parkety	VYK: PZ:25.4°C
Systém VARIONOVA	Rúrka RAUTHERM S 17x2,0
lo/lp=89.6 m/7.8 m	S=9.0 m2
Lpz=100 [mm]	VYK: 0.8 l/min

RZ 1 - 1.PP (11/10) (tp=45.0°C)	1.03 - Spalňa
PZ 1: Drevené parkety	VYK: PZ:24.8°C [OZ:24.8°C]
Systém VARIONOVA	Rúrka RAUTHERM S 17x2,0
lo/lp=99.2 m/11.8 m	S=9.9 m2
Lpz/Loz=100/100 [mm]	VYK: 0.4 l/min

RZ 1 - 1.PP (11/9) (tp=45.0°C)	1.04 - Hygiena 1
PZ 1: Keramická dlažba	VYK: PZ:34.0°C
Systém VARIONOVA	Rúrka RAUTHERM S 17x2,0
lo/lp=28.2 m/13.8 m	S=2.8 m2
Lpz=100 [mm]	VYK: 0.8 l/min

RZ 1 - 1.PP (11/8) (tp=45.0°C)	1.05 - Izba
PZ 1: Drevené parkety	VYK: PZ:24.8°C [OZ:25.3°C]
Systém VARIONOVA	Rúrka RAUTHERM S 17x2,0
lo/lp=81.4 m/19.5 m	S=10.6 m2
Lpz/Loz=150/100 [mm]	VYK: 0.8 l/min

RZ 1 - 1.PP (11/7) (tp=45.0°C)	1.08 - Obývačka + kuhcyna
PZ 1: Drevené parkety	VYK: PZ:24.2°C [OZ:24.6°C]
Systém VARIONOVA	Rúrka RAUTHERM S 17x2,0
lo/lp=78.6 m/24.4 m	S=10.1 m2
Lpz/Loz=150/100 [mm]	VYK: 0.4 l/min

RZ 1 - 1.PP (11/6) (tp=45.0°C)	1.08 - Obývačka + kuhcyna
PZ 1: Drevené parkety	VYK: PZ:24.3°C [OZ:24.6°C]
Systém VARIONOVA	Rúrka RAUTHERM S 17x2,0
lo/lp=83.3 m/32.5 m	S=9.4 m2
Lpz/Loz=150/100 [mm]	VYK: 0.4 l/min

0 2,5 5 7,5 10

názov stavby:	**RODINNÝ DOM NEMCOVÁ**						
investor:	NEMCOVÁ Tatiana r. Matušovská, Mgr., PhDr., Na Roličkách 14003/6, Bratislava, PSČ 831 03,SR						
obec:	BA. - NOVÉ MESTO	katastrálne územie :	VINOHRADY	okres:	BRATISLAVA III.	parcelné číslo :	18368/1, 18368/2
zodpovedný projektant :	Ing. Norbert Jókay			kreslil :	Bc. Viktor Labovský	dátum : 01/2026	mierka : 1:50
autor projektu :	Ing. arch. Lucia ULRICHOVÁ					stupeň : SZ, PS	formát : 630x420
názov výkresu :	**PÔDORYS 1.PP**					číslo výkresu : P 0 1	01