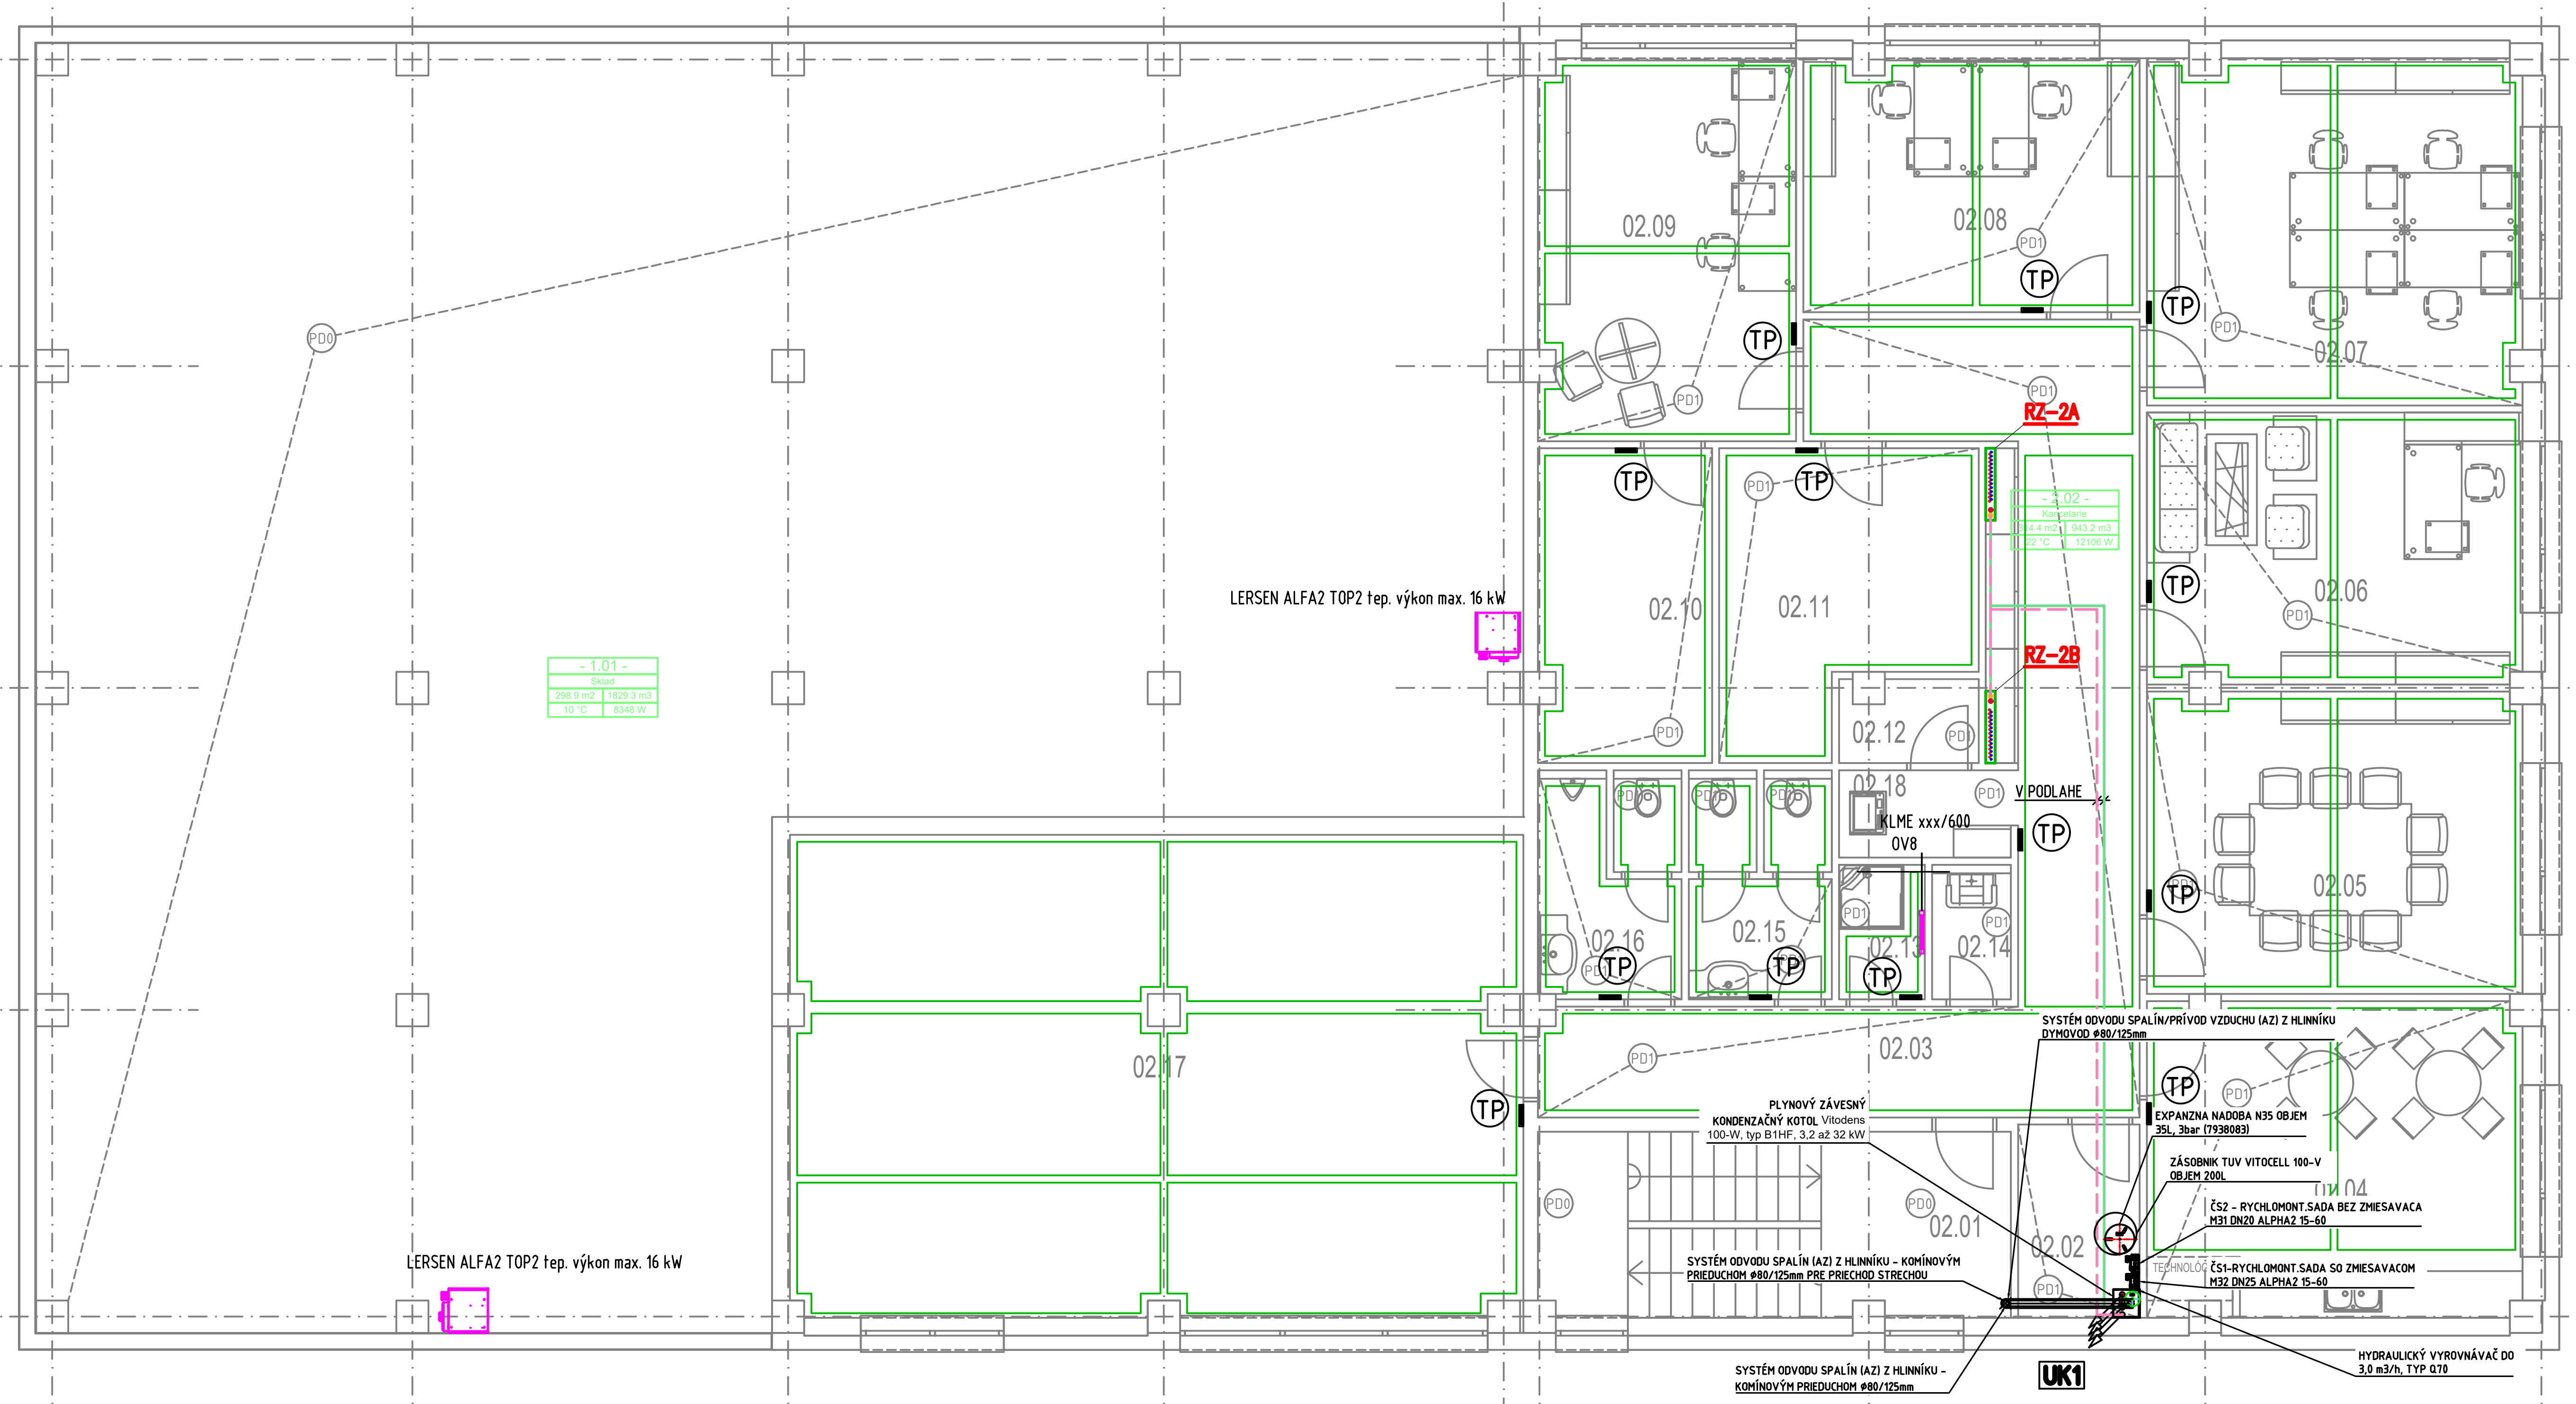
02.01
02.02
02.03
02.04
02.05
02.06
02.07
02.08
02.09
02.10
02.11
02.12
02.13
02.14
02.15
02.16
02.17
02.18
TP
PD0
PD1
RZ-2A
RZ-2B
V PODLAHE
KLME xxx/600
OV8
LERSEN ALFA2 TOP2 tep. výkon max. 16 kW
LERSEN ALFA2 TOP2 tep. výkon max. 16 kW
SYSTÉM ODVODU SPALÍN/PRÍVOD VZDUCHU (AZ) Z HLINNÍKU DYMOVOD ø80/125mm
PLYNOVÝ ZÁVESNÝ KONDENZAČNÝ KOTOL Vitodens 100-W, typ B1HF, 3,2 až 32 kW
EXPANZNA NADOBA N35 OBJEM 35L, 3bar (7938083)
ZÁSOBNIK TUV VITOCELL 100-V OBJEM 200L
ČS2 - RYCHLOMONT.SADA BEZ ZMIESAVACA M31 DN20 ALPHA2 15-60
ČS1-RYCHLOMONT.SADA SO ZMIESAVACOM M32 DN25 ALPHA2 15-60
TECHNOLÓG
SYSTÉM ODVODU SPALÍN (AZ) Z HLINNÍKU - KOMÍNOVÝM PRIEDUCHOM ø80/125mm PRE PRIECHOD STRECHOU
SYSTÉM ODVODU SPALÍN (AZ) Z HLINNÍKU - KOMÍNOVÝM PRIEDUCHOM ø80/125mm
HYDRAULICKÝ VYROVNÁVAČ DO 3,0 m3/h, TYP Q70
UK1

DETAIL ZAPOJENIA VYKUROVACÍCH TELIES DOSKOVÉ VYKUROVACIE TELESO

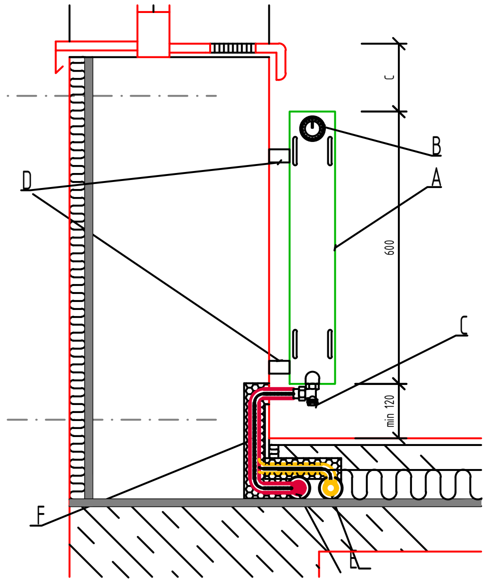
A
B
C
D
E
F
600
c
min 120

DETAIL OSADENIA VYK. TELESA NA ROZVODY ÚK, M = 1:25

- A OCELOVÉ VYKUROVACIE TELESO TYP VK
- B TERMOSTATICKÁ HLAVICA
- C ROHOVÁ PRIPOJOVACIA ARMATÚRA PRE DVOJTRUBKOVÉ SYSTÉMY
- D DRŽIAK
- E ROZVODY ÚSTREDNÉHO KÚRENIA
- F TRUBICOVÁ IZOLÁCIA

DETAIL ZAPOJENIA VYKUROVACÍCH TELIES REBRÍKOVÉ VYKUROVACIE TELESO

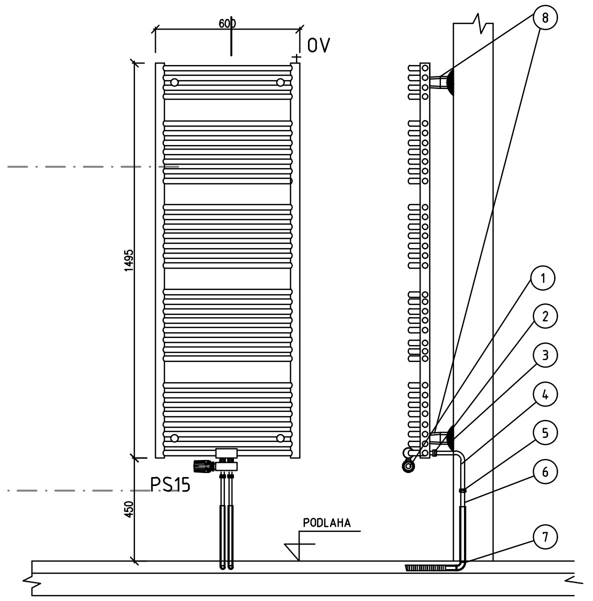
600
OV
1495
450
PS15
PODLAHA
1
2
3
4
5
6
7
8

LEGENDA:

1. Stredové pripojenie vykurovacieho telesa, rozteč H=50mm rohové, farbia biela
2. Svorková spojka
3. Krycia rozeta
4. Pripojovacia garnitúra s upevňovacím
5. Násuvná objímka
6. Vykurovacia rúrka
7. Vodiaci oblúk 90°
8. Stenová konzola

LEGENDA MIESTNOSTÍ 2.N.P

Č.M.	ÚČEL MIESTNOSTI	PLOCHA (m2)	POPIS POVRCHOVÝCH ÚPRAV		
			PODLAHA	STENY	STROPY
02.01	SCHODISKO	17,00	KERAMICKÁ DLAŽBA	SÁDROVÁ OMIETKA	SDK PODHĽAD - PLNÝ
02.02	ARCHÍV	4,59	VINYL	SÁDROVÁ OMIETKA	SDK PODHĽAD - PLNÝ
02.03	CHODBA	36,36	VINYL	SÁDROVÁ OMIETKA	SDK PODHĽAD - PLNÝ
02.04	KUCHYNKA	22,78	VINYL	SÁDROVÁ OMIETKA	SDK PODHĽAD - PLNÝ
02.05	ZASADAČKA	22,07	VINYL	SÁDROVÁ OMIETKA	SDK PODHĽAD - PLNÝ
02.06	KANCELÁRIA RIADITEĽ	19,84	VINYL	KERAM. OBKLAD	SDK PODHĽAD - PLNÝ
02.07	KANCELÁRIA	25,23	VINYL	SÁDROVÁ OMIETKA	SDK PODHĽAD - PLNÝ
02.08	KANCELÁRIA OBCHOD	16,58	VINYL	SÁDROVÁ OMIETKA	SDK PODHĽAD - PLNÝ
02.09	KANCELÁRIA EKONÓM	19,14	VINYL	SÁDROVÁ OMIETKA	SDK PODHĽAD - PLNÝ
02.10	ARCHÍV	10,60	VINYL	SÁDROVÁ OMIETKA	SDK PODHĽAD - PLNÝ
02.11	SKLAD	13,33	VINYL	SÁDROVÁ OMIETKA	SDK PODHĽAD - PLNÝ
02.12	SERVER	2,13	VINYL	SÁDROVÁ OMIETKA	SDK PODHĽAD - PLNÝ
02.13	SPRCHA	2,26	KERAMICKÁ DLAŽBA	SÁDROVÁ OMIETKA	SDK PODHĽAD - PLNÝ
02.14	UPRATOVAČKA	2,07	KERAMICKÁ DLAŽBA	SÁDROVÁ OMIETKA	SDK PODHĽAD - PLNÝ
02.15	WC ŽENY	6,40	KERAMICKÁ DLAŽBA	SÁDROVÁ OMIETKA	SDK PODHĽAD - PLNÝ
02.16	WC MUŽI	6,40	KERAMICKÁ DLAŽBA	SÁDROVÁ OMIETKA	SDK PODHĽAD - PLNÝ
02.17	VOĽNÝ PRIESTOR	68,60	VINYL	SÁDROVÁ OMIETKA	SDK PODHĽAD - PLNÝ
02.18	COPY POINT	3,00	VINYL	SÁDROVÁ OMIETKA	SDK PODHĽAD - PLNÝ
	CELKOM	298,38			

LEGENDA POTRUBIA:

🟥	POTRUBIE - PLASTHLINNÍKOVÁ RÚRKA NAPR. GEBERIT MEPLA SPÁJANÉ LISOVANÍM, IZOLOVANÉ POTRUBIE, TEPLOTNÝ SPÁD 70/50°C POTRUBIE VEDENÉ POD STROPOM, PRE RADIATORI, PRÍVOD A SPIATOČKA
🟩	POTRUBIE - PLASTHLINNÍKOVÁ RÚRKA NAPR. GEBERIT MEPLA SPÁJANÉ LISOVANÍM, IZOLOVANÉ POTRUBIE, TEPLOTNÝ SPÁD 45/35°C POTRUBIE VEDENÉ V PODLAHE, V ŠACHTE, PRE PODLAHOVÉ VYKUROVANIE, PRÍVOD A SPIATOČKA

POZNÁMKA :

- V PRÍPADE NEJASNOSTÍ VO VÝKRESOVEJ DOKUMENTÁCIÍ KONTAKTOVAŤ ZODPOVEDNÉHO PROJEKTANTA
- VŠETKY ROZMERY STAVEBNÝCH PRÁC KONTROLOVAŤ NA MIESTE STAVBY
- PRED UVEDENÍM SYSTÉMU DO PREVÁDZKY JE POTREBNÉ VYKONAŤ DÔKLADNÝ PREPLACH SYSTÉMU S VYČISTENÍM VŠETKÝCH FILTROV NA ROZVODE
- PO NAPUSTENÍ SYSTÉMU JE POTREBNÉ VYKONAŤ JEHO ODVZDUŠNENIE
- DODÁVATEL STAVBY JE POVINNÝ REALIZOVAŤ VŠETKY PRÁCE V ZMYSLE PLATNÝCH STN EN S DODRŽANÍM TECHNOLOGICKÝCH A BEZPEČNOSTNÝCH POSTUPOV. ĎALEJ JE POVINNÝ REŠPEKTOVAŤ USTANOVENIÁ STN 730421 O PRÍSLUŠNÝCH ROZMEROVÝCH ODCHÝLKACH REALIZOVANÝCH KONŠTRUKCIÍ PROTI PROJEKTOVANÉMU STAVU. KAŽDÚ ODCHÝLKU OD PROJEKTU JE POTREBNÉ PREROKOVAŤ S GP.
- PRESTUPY INŽINIERSKYCH SIETÍ A ROZVODOV V OBJEKTE JE POTREBNÉ VYNECHAŤ PRI REALIZÁCII STAVBY.
- PROJEKTOVÁ DOKUMENTÁCIA JE SPRACOVANÁ PRE ÚČEL VYDANIA STAVEBNÉHO POVOLENIA A NENAHRÁDZA REALIZAČNÝ PROJEKT

LEGENDA ZARIADENÍ A ARMATÚR :

PS	PRIPÁJACÍ BLOK S INTEGROVANÝM TERMOSTATICKÝM VENTILOM TYP BB PRE VYKUROVACIE TELESÁ SO STREDOVÝM PRIPOJENÍM, ROHOVÉ, DN15, PRIPOJENIE RADIÁTORA VONKAJŠÍ ZÁVIT 1/2", PRIPOJENIE DO STENY VONKAJŠÍ ZÁVIT 3/4" S TERMOSTATICKOU HLAVICOU NAPR. THERA-4 KLASIK S KVAPAL. SNÍMAČOM
GV	GUĽOVÝ VENTIL ZÁVITOVÝ
RV	PREDNASTAVITEĽNÝ REGULAČNÝ VENTIL PRIAMY - STAD
VK	VYPÚŠŤACÍ KOHÚT
OV	ODVZDUŠŇOVACÍ VENTIL
TP	PRIESTOROVÝ REGULÁTOR NEA SMART 2.0 PRE MERANIE TEPLOTY V MIESTNOSTI, FY. REHAU
UK1	STÚPAČKA VYKUROVANIA
TS	Termostat SALUS týdenní programovatelný, 0-230V, 0,5°C, 5A, pro ALFA, SIGMA, ZETA, COMPACT
RZ	ROZDELOVACIA STANICA PRE VYKUROVACIE TELESÁ A PODLAHOVĚ VYKUROVANIE

▭	LAVICOVÉ VYKUROVACIE TELESO KORALINE LDE 300/2000
▬	OCEĽOVÉ DOSKOVÉ VYKUROVACIE TELESO RADIK VK TYP VENTIL KOMPAKT, S PRAVÝM SPODNÝM PRIPOJENÍM
▭	REBRÍKOVÉ VYKUROVACIE TELESO TYP KORALUX LINEAR MAX-E, FY. KORADO
▢	PLYNOVÝ TEPLOVZDUŠNÝ OHRIEVAČ LERSEN ALFA2 TOP2 tep. výkon max. 16 kW

SPÔSOB ZNAČENIA
22 VK 600/ ...

- ... STAVEBNÁ DĹŽKA V MILIMETROCH
- 600 STAVEBNÁ VÝŠKA V MILIMETROCH
- VK PREVEDENIE VENTIL-KOMAPKT
- 22 TYP DVOJRADOVÝ

LEGENDA PODLAHOVÉHO VYKUROVANIA:

PODLAHOVÉ KÚRENIE REHAU

Rúrka RAUTHERM S 17x2,0	TYP VYKUROVACEJ RÚRKY
VARIONOVA	SYSTÉM PODLAHOVÉHO VYKUROVANIA

±0,000 = úroveň 1.N.P. = 126,40 m.n.m.

ARCHITEKT STAVBY	Ing. arch. JURAJ ZATKALÍK	zatkalík architects, s.r.o. Líščie údolie 65 841 05 Bratislava	
ZODPOVEDNÝ PROJEKTANT	Ing. Norbert Jókay		
VYPRACOVAL	Bc. Viktor Labovský		
INVESTOR	Unimpex Bratislava s.r.o. Horné Predmestie 3 900 21 Svätý Jur		
STAVBA	VINÁRSKE CENTRUM UNIMPEX NA PAŽITI, SVATÝ JUR p.č. 4513/45, 4513/46	**STUPEŇ**	PSP
		DÁTUM	NOVEMBER 2024
PROFESIA	VYKUROVANIE	**FORMÁT**	3 x A4
DRUH STAVBY	ADMINISTRATÍVNO OBCHODNÁ STAVBA	**MIERKA**	M 1 : 100
NÁZOV VÝKRESU	PÔDORYS 2. NADZEMNÉHO PODLAŽIA	**ČÍSLO VÝKRESU**	A02