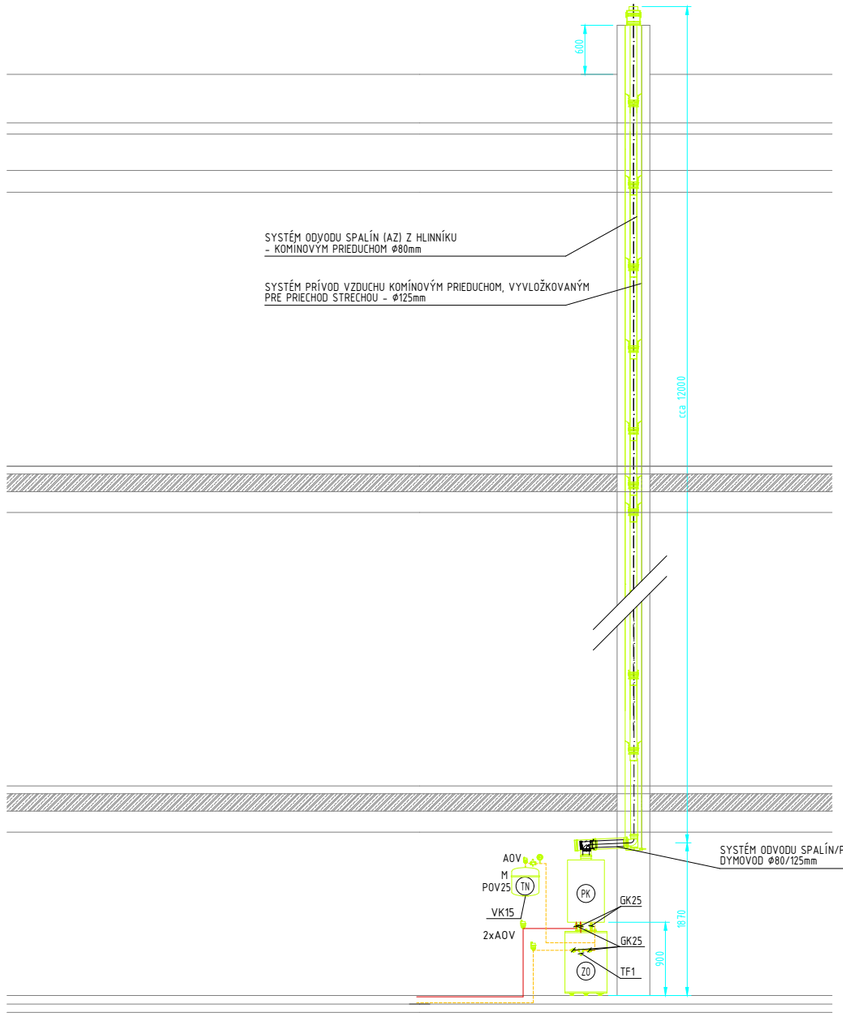



# LEGENDA ZARIADENÍ:

PK — KONDENZAČNÝ PLYNOVÝ NÁSTENNÝ KOTOL – WTC-GW 15-B prev. W
MENOVITÝ TEPELNÝ PRÍKON 2 AŽ 14 kW

ZO — ZÁSOBNÍKOVÝ OHRIEVAČ TEPLEJ VODY – WEISHAUPT
TYP: WAS 100 ECO A – S OBJEMOM 113l

TN — UZAVRETÁ TLAKOVÁ EXPANZNÁ NÁDOBA REFLEX DD12 10/4, O OBJEME 12l

# LEGENDA POTRUBÍ:

ROZVOD ÚK – Rúrka RAUTITAN stabil , FY REHAU , – teplotný spád 45/35°C
PRE RADIÁTOROVÉ VYKUROVANIE, PRÍVOD A SPIATOČKA

# LEGENDA ARMATÚR:

| | |
|---|---|
| SR | STUPAČKA PRE RADIATOROVÉ VYKUROVANIE |
| TF1 | FILTER |
| AOV | AUTOMATICKÝ ODVZDUŠŇOVAČ |
| GK | GUĽOVÝ KOHÚT |
| T | TEPLOMER |
| M | TLAKOMER |
| VK | VYPÚŠŤACÍ KOHÚT |
| POV | POISTNÝ VENTIL |
| OV | ODVZDUŠŇOVACÍ VENTIL |
| iz | TEPELNÁ IZOLÁCIA |

# POZNÁMKY :

- V PRÍPADE NEJASNOSTÍ VO VÝKRESOVEJ DOKUMENTÁCII KONTAKTOVAŤ ZODPOVEDNÉHO PROJEKTANTA
- VŠETKY ROZMERY STAVEBNÝCH PRÁC KONTROLOVAŤ NA MIESTE STAVBY
- DODÁVATEL STAVBY JE POVINNÝ REALIZOVAŤ VŠETKY PRÁCE V ZMYSLE PLATNÝCH STN EN S DODRŽANÍM TECHNOLOGICKÝCH A BEZPEČNOSTNÝCH POSTUPOV. ĎALEJ JE POVINNÝ REŠPEKTOVAŤ USTANOVENIÁ STN 730421 O PRÍSLUŠNÝCH ROZMEROVÝCH ODCHÝLKACH REALIZOVANÝCH KONŠTRUKCIÍ PROTI PROJEKTOVANÉMU STAVU. KAŽDÚ ODCHÝLKU OD PROJEKTU JE POTREBNÉ PREROKOVAŤ S GP.
- ±0,000 SA VZŤAHUJE K ÚROVNI FINÁLNEJ ÚPRAVY PODLAHY
- VÝBER RADIATOROV PODLA INVESTORA

±0,000 = Výška podlahy

| | | | | |
|---|---|---|---|---|
| H.I.P | ZODPOVEDNÝ PROJEKTANT | VYPRACOVAL | FORMÁT | 2 x A4 |
| Ing. arch. Peter Novotný | Ing. Norbert Jókay | Bc. Viktor Labovský | DÁTUM | 12/2025 |
| Ing. arch. Michal Cinzer | | | STUPEŇ P.D. | PODS |
| MIESTO STAVBY | Björnsonova 3, 811 04 Bratislava | | MIERKA | 1:75 |
| INVESTOR | Samuel Štipkala | | Č. VÝKRESU | 04 |
| NÁZOV | Rekonštrukcia bytu | | Č.KÓPIE | |
| PROFESIA | Vykurovanie | | | |
| OBSAH | Rez odvodu spalín a schéma zapojenia | | | |