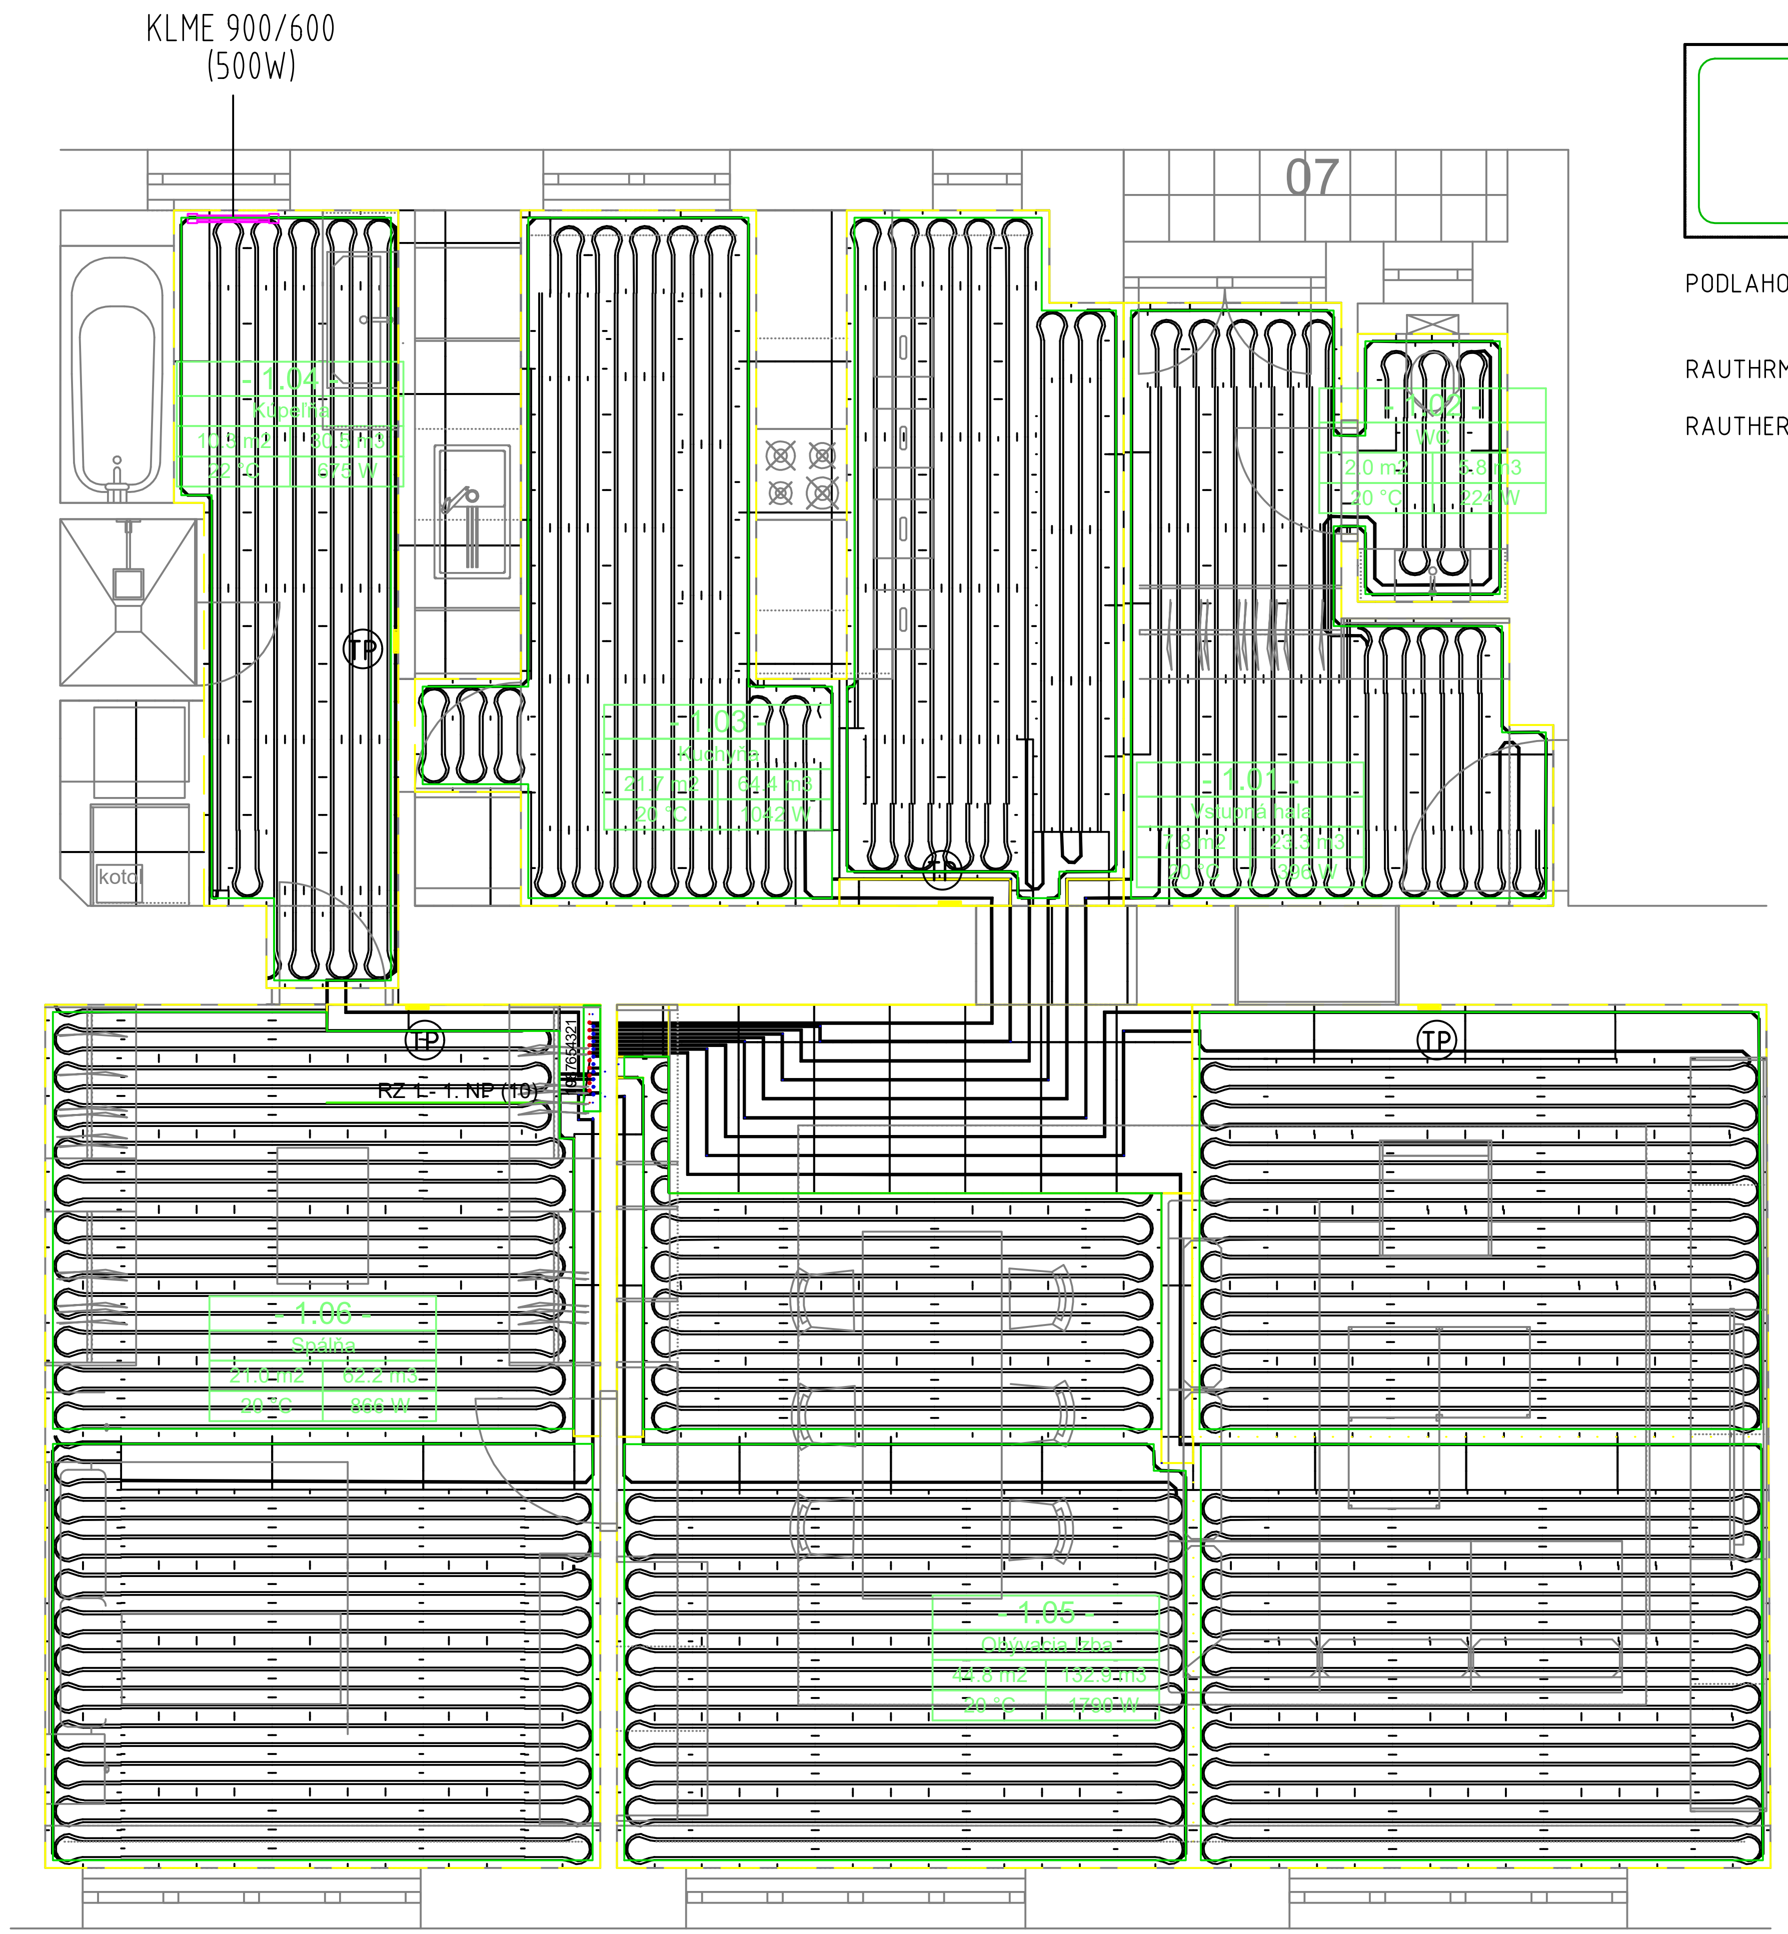

LEGENDA PODLAHOVÉHO VYKUROVANIA:

▭ PODLAHOVÉ KÚRENIE REHAU

RAUTHRM SPEED 16x1,5	TYP VYKUROVACEJ RÚRKY
RAUTHERM SPEED	SYSTÉM PODLAHOVÉHO VYKUROVANIA

DETAIL PODLAHOVÉHO VYKUROVANIA:

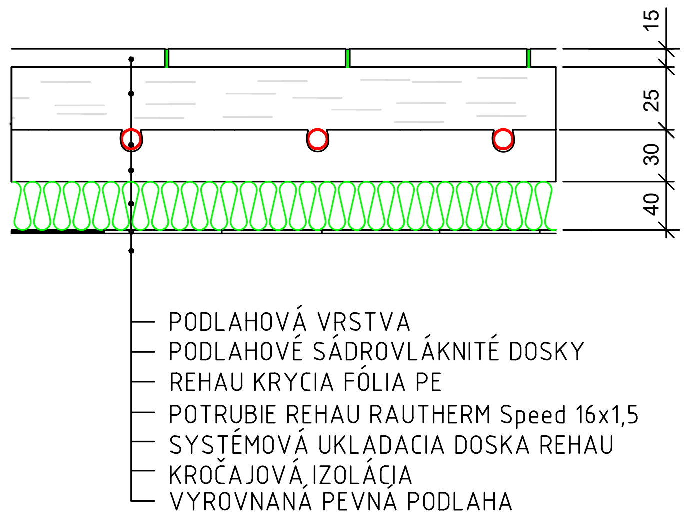
15
25
30
40
PODLAHOVÁ VRSTVA
PODLAHOVÉ SÁDROVLÁKNITÉ DOSKY
REHAU KRYCIA FÓLIA PE
POTRUBIE REHAU RAUTHERM Speed 16x1,5
SYSTÉMOVÁ UKLADACIA DOSKA REHAU
KROČAJOVÁ IZOLÁCIA
VYROVNANÁ PEVNÁ PODLAHA

LEGENDA MIESTNOSTÍ:

Č.M.	ÚČEL MIESTNOSTI	plocha v m2
01	vstupná hala	7,75
02	wc	1,76
03	kuchyňa	22,63
04	kúpelňa	10,61
05	obývacia izba	44,51
06	spálňa	21,12
celková plocha		108,38

07	loggia	1,55

LEGENDA POTRUBIA:

🟥 Plastový rozvod - plasthliníková rúrka s kyslíkovou bariérou Pex-Al-Pex.

— — — Potrubie pre napojenie rozdelovacej stanice vedené v podlahe uložiť do izolácie podlahy pod podlahové vykurovanie. Prívod aj spiatočka

LEGENDA VYKUROVACÍCH TELIES:

KLME 900/600 - ELEKTRICKÉ REBRÍKOVÝ RADIATOR KORALUX LINEAR MAX-ERA, VÝKON 500W

POZNÁMKA :

- V PRÍPADE NEJASNOSTÍ VO VÝKRESOVEJ DOKUMENTÁCIÍ KONTAKTOVAŤ ZODPOVEDNÉHO PROJEKTANTA
- VŠETKY ROZMERY STAVEBNÝCH PRÁC KONTROLOVAŤ NA MIESTE STAVBY
- PRED UVEDENÍM SYSTÉMU DO PREVÁDZKY JE POTREBNÉ VYKONAŤ DÔKLADNÝ PREPLACH SYSTÉMU S VYČISTENÍM VŠETKÝCH FILTROV NA ROZVODE
- PO NAPUSTENÍ SYSTÉMU JE POTREBNÉ VYKONAŤ JEHO ODVZDUŠNENIE
- DODÁVATEL STAVBY JE POVINNÝ REALIZOVAŤ VŠETKY PRÁCE V ZMYSLE PLATNÝCH STN EN S DODRŽANÍM TECHNOLOGICKÝCH A BEZPEČNOSTNÝCH POSTUPOV. ĎALEJ JE POVINNÝ REŠPEKTOVAŤ USTANOVENIÁ STN 730421 O PRÍSLUŠNÝCH ROZMEROVÝCH ODCHÝLKACH REALIZOVANÝCH KONŠTRUKCIÍ PROTI PROJEKTOVANÉMU STAVU. KAŽDÚ ODCHÝLKU OD PROJEKTU JE POTREBNÉ PREROKOVAŤ S GP.
- PRESTUPY INŽINIERSKYCH SIETÍ A ROZVODOV V OBJEKTE JE POTREBNÉ VYNECHAŤ PRI REALIZÁCII STAVBY.
- PROJEKTOVÁ DOKUMENTÁCIA JE SPRACOVANÁ PRE ÚČEL VYDANIA STAVEBNÉHO POVOLENIA A NENAHRÁDZA REALIZAČNÝ PROJEKT

±0,000 = Výška podlahy

H.I.P	ZODPOVEDNÝ PROJEKTANT	VYPRACOVAL	FORMÁT	3 x A4
Ing. arch. Peter Novotný	Ing. Norbert Jókay	Bc. Viktor Labovský	DÁTUM	12/2025
Ing. arch. Michal Cinzer			STUPEŇ P.D.	PODS
MIESTO STAVBY	Björnsonova 3, 811 04 Bratislava		MIERKA	1:50
INVESTOR	Samuel Štipkala		Č. VÝKRESU	03
NÁZOV	Rekonštrukcia bytu		Č.KÓPIE	
PROFESIA	Vykurovanie			
OBSAH	Kladačský výkres			