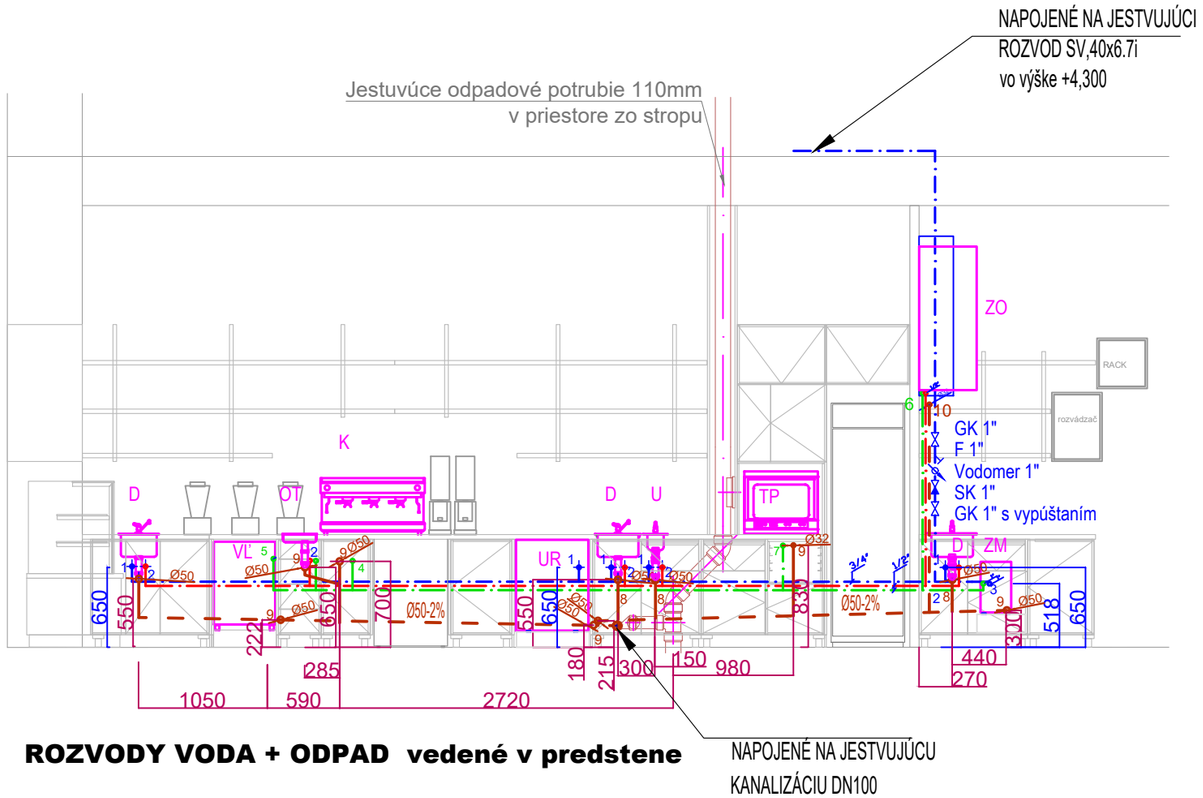


ROZVODY VODA + ODPAD vedené v predstene

LEGENDA

STUDENÁ VODA (PEX/AL/PEX)
TEPLÁ ÚŽITKOVÁ VODA (PEX/AL/PEX)
STUDENÁ VODA ZMAKČENÁ (PEX/AL/PEX)
PRIPOJOVACIE A ODPADOVÉ KANALIZAČNÉ POTRUBIE Z PP RÚR - HT SYSTÉM

1- *Prívod studenej vody R1/2" pre stojankovú bateriu ukončenie ventilom R3/4" so sitkom v=650*
2- *Prívod teplej vody R1/2" pre stojankovú bateriu ukončenie ventilom R3/4" so sitkom v=650*
3- *Prívod studenej vody R1/2" pre zmäkčovač R3/4" ukončenie pračkovým ventilompre hadicu so sitkom v=650*
4- *Prívod zmäkčenej vody R1/2" pre trysku/kávovar ukončenie ventilom R3/4" pre hadicu v=750*
5- *Prívod zmäkčenej vody R1/2" pre umývačku/výrobník ľadu ukončenie pračkovým ventilom R3/4" pre hadicu a R3/8" ventil pre batériu v=650*
6- *Prívod zmäkčenej vody R1/2" pre ohrievač vody ukončenie ventilom R3/4" so sitkom v=2000*
7- *Prívod zmäkčenej vody R1/2" pre pec ukončenie ventilom R3/4" so sitkom v=850*
8- *Odpad pre drez/umývadlo pr50mm v=550*
9- *Odpad pre spotrebiče pr32/40/50mm v=viď kóta*
10 - *Odpad pre ohrievač vody pr32 ukončené prepadovým sifónom v=1950*

LEGENDA ZNAČIEK

K	KÁVOVAR + ZÁPACHOVÝ UZÁVER
D	KUCHYNSKÝ DREZ + ZÁPACHOVÝ UZÁVER ALEBO NAPOJIŤ NA SIFÓN DREZU
ZM	ZMAKČOVAČ VODY + ZÁPACHOVÝ UZÁVER
U	UMÝVADLO + ZÁPACHOVÝ UZÁVER
UR	UMÝVAČKA RIADU + ZÁPACHOVÝ UZÁVER ALEBO NAPOJIŤ NA SIFÓN DREZU
ZO	ELEKTRICKÝ ZÁSOBNÍKOVÝ OHRIEVAČ ELIZ EURO 120 , 2 kW (120L) + ZÁPACHOVÝ UZÁVER
OT	OPLACHOVACIA TRYSKA + ZÁPACHOVÝ UZÁVER
VĽ	VÝROBNÍK ĽADU + ZÁPACHOVÝ UZÁVER
TP	TEPLOVZDUŠNÁ PARNÁ PEC + ZÁPACHOVÝ UZÁVER
GK	GUĽOVÝ KOHÚT
F	FILTER MECH. NEČISTOT
SK	SPATNÁ KLAPKA

LEGENDA MIESTNOSTÍ:

Č.M.	NÁZOV MIESTNOSTI	PLOCHA (m^2)
1.01	NEFAJČIARSKA ČASŤ	42.53
1.02	FAJČIARSKA ČASŤ	34.47
1.03	PRIESTOR BARU	17.89
1.04	SKLAD	4.20
CELKOVÁ ÚŽIT. PLOCHA		99.09

POZNÁMKA:

Rozvod SV, TV z hlavného rozvodu k zariadovacim predmetom bude z potrubia PEX/AL/PEX izolované tepelnou izoláciou.
Na odbočkách z hlavného rozvodu budú osadené uzatváracie armatúry.

Min. vzdialenosti podpier pre uchytenie PEX/AL/PEX potrubia
Ø 16 x 2 uchytenie potrubia po 1m
Ø 20 x 2,5 uchytenie potrubia po 1,25m

Min. vzdialenosti podpier pre uchytenie kanalizácie
Ø 50 uchytenie potrubia po 0,5m

GK gulovy kohut na rozvod pitnej vody, bude opatreny vypuštacím

Všetky zariadenia pripojené na teplú a studenú vodu musia mať mechanický filter a uzatvárací rohový ventil.

G-1704	
Celková plocha:	104,91 m^2
Podlahová plocha:	99,09 m^2

0,000 = 137,50 m n.m., B.p.v.

ZODP. PROJEKTANT	**HIP**	**VYPRACOVAL**		
Ing. Lukáš Skalík, Phd.	**akad. arch. Ivan Cabadaj**	**Ing. Viktor Labovský**		
STAVBA	**OC Polus, Vajnorská 100 Bratislava**			
Č. OBCHOD. JEDNOTKY	**G-1704**			
INVESTOR	**HOBOKEN SK, s.r.o., 811 07 Bratislava, Kmeťovo námestie 2764/1**			
NÁZOV OBCH.JEDNOTKY	**Klasico CAFE**			
PROFESIA	**E1.3 ZDRAVOTECHNIKA**		**STUPEŇ PD**	**DSP**
AUTOR PROJEKTU	**Ing. Viktor Labovský**	**mobil: +421 915 341 479**		
		mail: labovskýviktor@gmail.com	**FORMÁT**	**2 x A4**
KONTAKTNÁ OSOBA NÁJOMCU	**Julius Šútö**	**mobil: +421 911 709 509**	**DÁTUM**	**8/2026**
		mail: sutojulius@gmail.com	**MIERKA 1:50**	**Č.PARÉ**
OBSAH VÝKRESU	**ZVISLÁ SCHÉMA**		**Č.VÝKRESU**	**E1.3-02**

Obsah tohto výkresu je výhradným majetkom autora. Výroba kopií diela, alebo jeho častí, alebo jeho použitie na iné účely, ako pre uvedenú stavbu sú bez súhlasu vlastníka autorských práv zakázané.