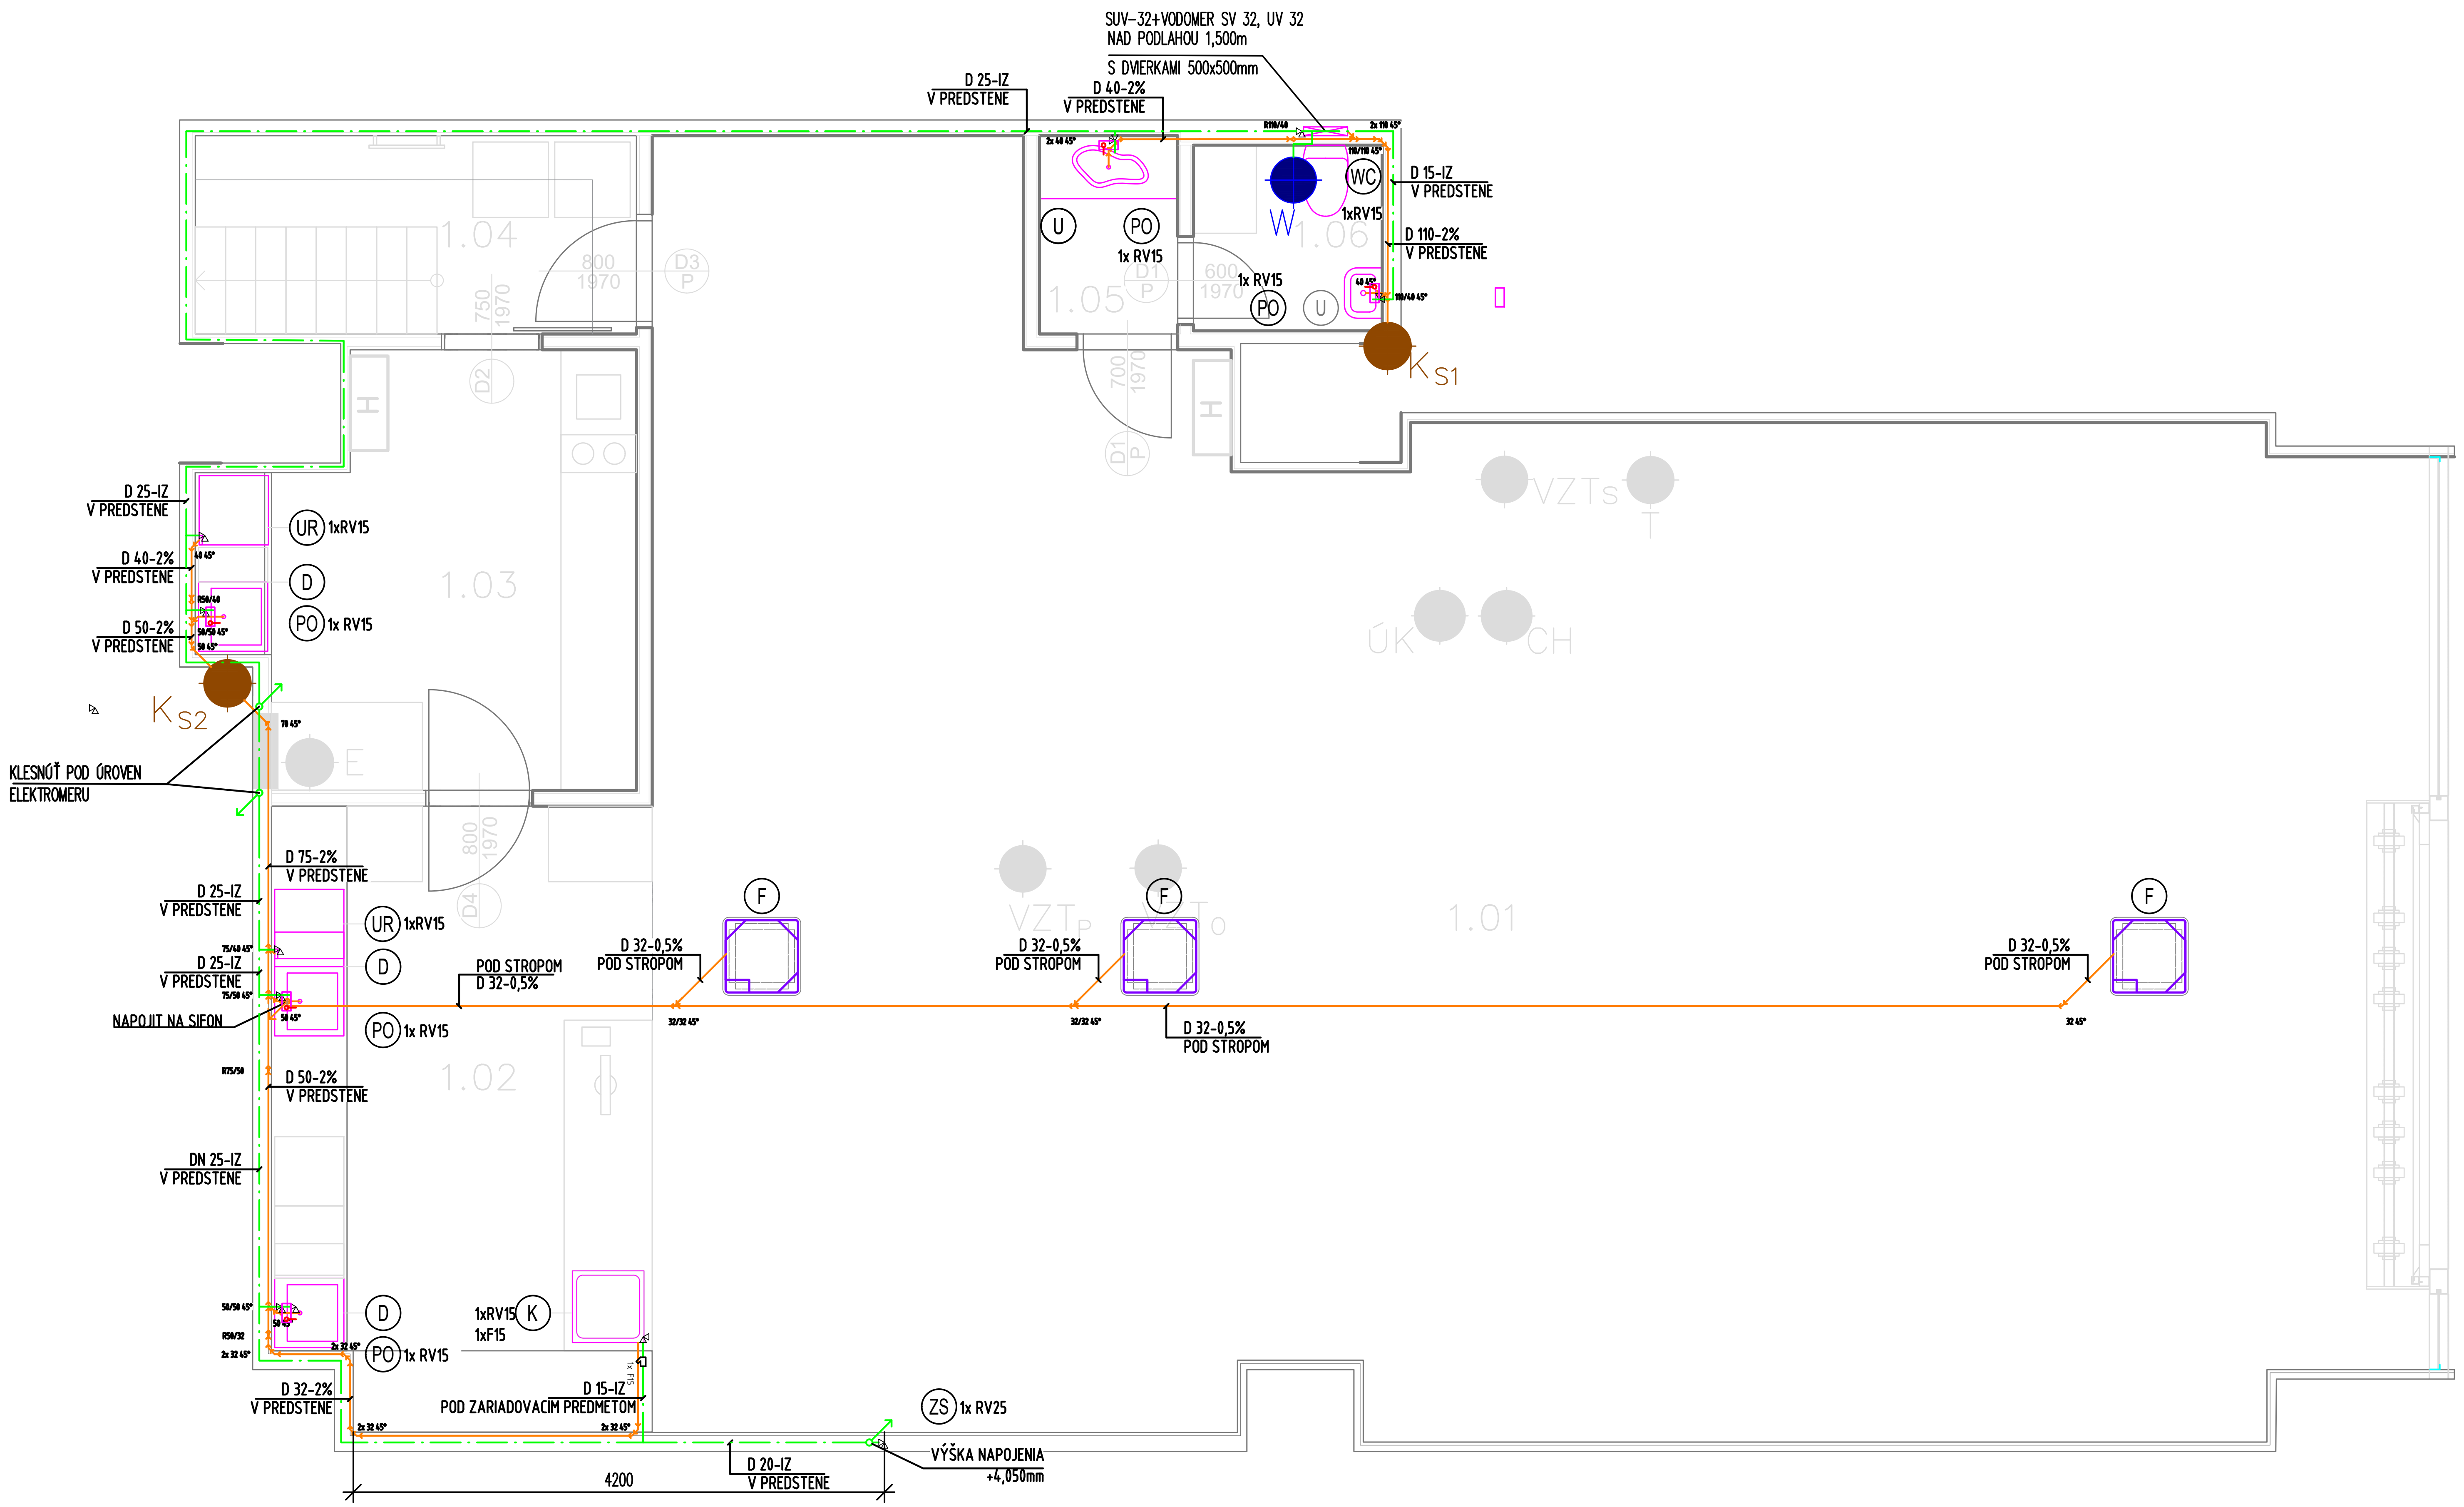

LEGENDA POTRUBIA

—	KANALIZAČNÉ ZVODOVÉ POTRUBIE HRDLOVÉ Z RÚR A TVAROVIEK S GUMOVÝM TESNENÍM MATERIÁL: WAVIN AS PRE VNÚTORNÉ ROZVODY
—·—	POTRUBIE ROZVODU STUDENEJ PITNEJ VODY - IZOLOVANÝ TEPELNOU IZOLÁCIOU TUBOLIT DG HR. 9mm MATERIAL: PEX/Al/PEX
—··—	POTRUBIE ROZVODU TEPLEJ VODY - PRIPOJOVACIA FLEXI HADICA
W	EXISTUJÚCI VODOVOD, BOD NAPOJENIA D32
K_{S1} , K_{S2}	EXISTUJÚCE ODPADOVÉ POTRUBIE SPLAŠKOVEJ KANALIZÁCIE, BOD NAPOJENIA D110

POZNÁMKY

Všetky kóty a rozmery PREMERAŤ NA STAVBE pred zahájením prác. Zvlášť preveriť polohy pripojenia technologických zariadení.
Montážne trasy potrubí koordinovať s profesiami VZT a EL.
Práce realizovať striktne podľa platných STN/EN noriem. Kanalizačné potrubia osadiť v požadovanom spáde (min. 2%).
Zhotoviteľ je POVINNÝ pred zakrytím vykonať tlakovú skúšku vody a skúšku tesnosti kanalizácie. O skúškach vyhotoviť PROTOKOL.
Rozvody TÚV a SV izolovať izoláciou typu TUBOLIT (alebo ekvivalentom) v normou požadovanej hrúbke.
Projektant nenesie zodpovednosť za funkčnosť systému v prípade, že montáž nebola vykonaná v súlade s touto PD, platnými normami a technologickými postupmi výrobcu.

LEGENDA MIESTNOSTÍ 02.OP.05 / SU – A 102:

Č.M.	NÁZOV MIESTNOSTI	PLOCHA (m²)	POPIS POVRCHOVÝCH ÚPRAV					
			STENY		STROPY		PODLAHA	
			DRUH	OBKLAD	DRUH	PODHĽAD	DRUH	SOKEL
1.01	PRIESTOR KAVIARNE	119.60	DVOJNÁSOBNÝ NÁTER	–	NÁSTREK EXISTUJÚCEHO PODHĽADU	–	KERAMICKÁ DLAŽBA	–
1.02	PRIESTOR BARU	14.62	DVOJNÁSOBNÝ NÁTER	NAD PRACOVNOU DOSKOU		–	KERAMICKÁ DLAŽBA	KERAMICKÁ DLAŽBA V. 70 mm
1.03	KUCHYNKA	10.41	DVOJNÁSOBNÝ NÁTER	NAD PRACOVNOU DOSKOU		SDK PODHĽAD S.V. 2800 mm	KERAMICKÁ DLAŽBA	KERAMICKÁ DLAŽBA V. 70 mm
1.04	SKLAD	5.53	DVOJNÁSOBNÝ NÁTER	–		SDK PODHĽAD S.V. 3800 mm	KERAMICKÁ DLAŽBA	KERAMICKÁ DLAŽBA V. 70 mm
1.05	UMYVÁRKA	1.68	DVOJNÁSOBNÝ NÁTER	KERAMICKÝ OBKLAD V. 1,2 m		SDK PODHĽAD S.V. 2800 mm	KERAMICKÁ DLAŽBA	KERAMICKÝ OBKLAD V. 1,2 m
1.06	TOALETA	2.21	DVOJNÁSOBNÝ NÁTER	KERAMICKÝ OBKLAD V. 1,2 m		SDK PODHĽAD S.V. 2800 mm	KERAMICKÁ DLAŽBA	KERAMICKÝ OBKLAD V. 1,2 m
CELKOVÁ ÚŽITKOVÁ PLOCHA		154.05						

LEGENDA ZARIAĎOVACÍCH PREDMETOV A ARMATÚR

WC	ZÁVESNÉ WC, INŠTALAČNÝ PRVOK PRE ZÁVESNÉ WC SO ZABUDOVANOU SPLACHOVACOU NÁDRŽKOU A ZÁPACHOVOU UZÁVIERKOU, S REDUKCIOU NA D 110
U	UMÝVADLO, INŠTALAČNÝ PRVOK PRE UMÝVADLO, ZÁPACHOVÁ UZÁVIERKA D 40
D	KUCHYNSKÝ DREZ, DREZOVÁ ZÁPACHOVÁ UZÁVIERKA D 50
K	KÁVOVAR, ZÁPACHOVÁ UZÁVIERKA D 32
UR	UMÝVAČKA RIADU S INTEGROVANOU PODOMIETKOVOU ZÁPACHOVOU UZÁVIERKOU D 40
F	FANCOIL
PO	PRIETOKOVÝ OHRIEVAČ ESH 5 U-N Trend (2kW)
ZS	ZELENÁ STENA, VÝŠKA NAPOJENIA +4,050mm NAD PODLAHOU

SU – A 102	
Plocha nájmu (Leasing):	**171,80 m²**
Podlahová plocha:	**154,05 m²**

0,000 = 137,50 m n.m., B.p.v.

ZODP. PROJEKTANT	HIP	VYPRACOVAL		
Ing. Norbert Jókay	Ing. arch. Pavol Vojtek	Bc. Viktor Labovský		
STAVBA	POLYFUNKČNÝ OBJEKT AUTOBUSOVÁ STANICA MLYNSKÉ NIVY			
Č. OBCHOD. JEDNOTKY	02.OP.05, SU – A 102			
INVESTOR	Stanica Nivy s.r.o, Mlynské Nivy 16, 821 09 Bratislava a Nivy Tower s.r.o., Mlynské Nivy 16, 821 09 Bratislava			
NÁZOV OBCH.JEDNOTKY	Rozprávková kaviareň			
PROFESIA	ZTI		STUPEŇ PD	RPD
AUTORI PROJEKTU	Bc. Viktor Labovský	mobil: +421 915 341 479		
		mail: labovskyviktor@gmail.com	FORMÁT	3 x A4
KONTAKTNÁ OSOBA NÁJOMCU	Ing. arch. Pavol Vojtek	mobil: +421 917 803 225	DÁTUM	10/2025
		mail: pavol.vojtek.org@gmail.com	MIERKA 1:50	Č.PARÉ
OBSAH VÝKRESU	PÔDORYS ZTI		Č.VÝKRESU ZTI–1	

Obsah tohto výkresu je výhradným majetkom autora. Výroba kopií diela, alebo jeho častí, alebo jeho použitie na iné účely, ako pre uvedenú stavbu sú bez súhlasu vlastníka autorských práv zakázané.