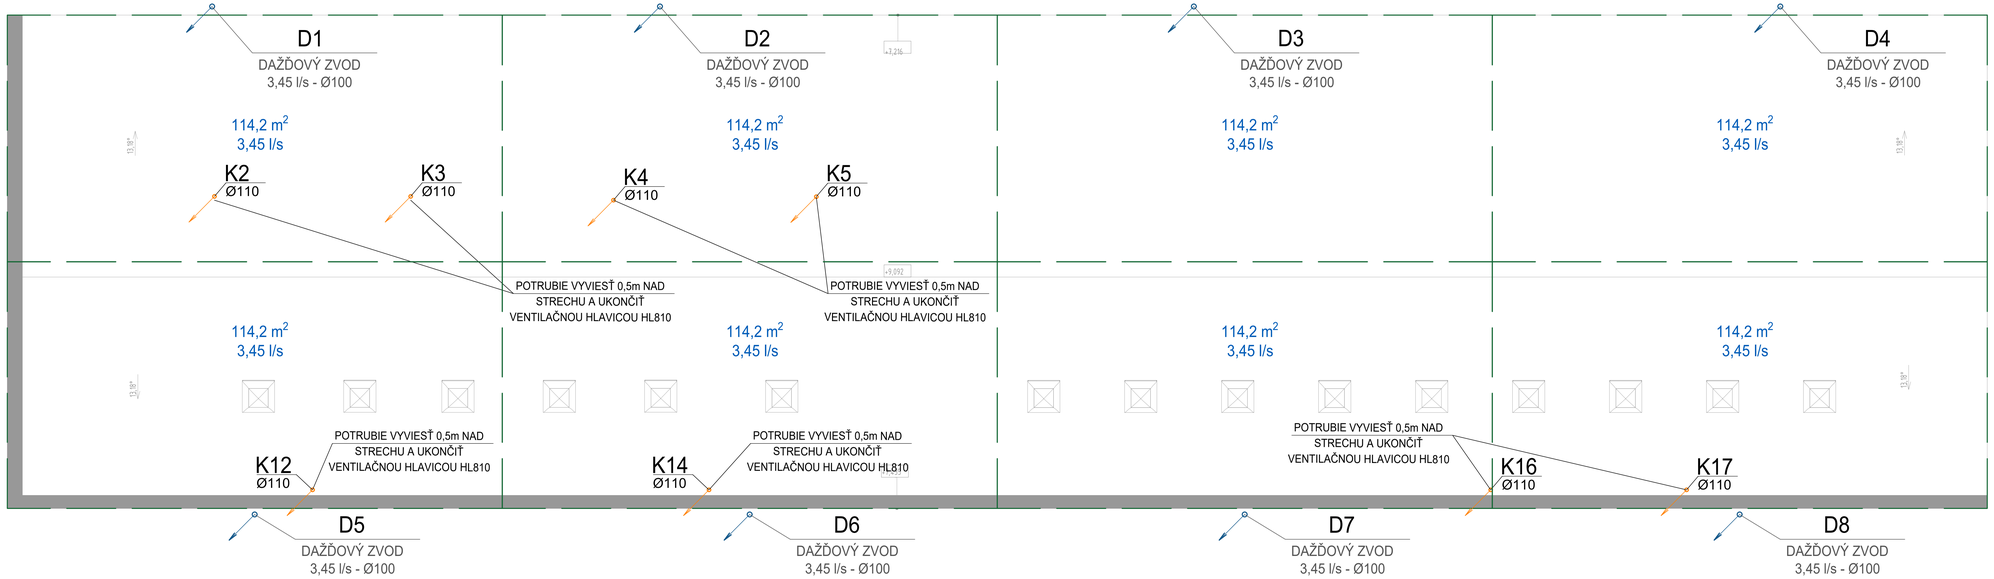


LEGENDA POTRUBIA

KANALIZAČNÉ HRDLOVÉ RÚRY - SPLAŠKOVÁ KANALIZÁCIA V STENE - PP HT RÚRY

LEGENDA

D1 — DAŽĎOVÝ ZVOD 3,45 l/s - Ø100 — VONKAJŠÍ POZNAČOVANÝ DAŽĎOVÝ ZVOD

131,5 m² - 3,96 l/s — PRIETOK DAŽĎOVÝCH VÔD

ODVODŇOVANÁ PLOCHA

GRAVITAČNÉ ODVODNENIE

POZNÁMKY

Všetky kóty a rozmery PREMERAŤ NA STAVBE pred zahájením prác. Zvlášť preveriť polohy pripojenia technologických zariadení.
Montážne hrasy potrubí koordinovať s profesiami VZT a EL.
Práce realizovať striktne podľa platných STN/EN noriem. Kanalizačné potrubia osadiť v požadovanom spáde (min. 2%).
Zhotoviteľ je POVINNÝ pred zakrytím vykonať tlakovú skúšku vody a skúšku tesnosti kanalizácie. O skúškach vyhotoviť PROTOKOL.
Rozvody TÚV a SV izolovať izoláciou typu TUBOLIT (alebo ekvivalentom) v rozsahu požadovanej hrúbke.
Projektant nenesie zodpovednosť za funkčnosť systému v prípade, že montáž nebola vykonaná v súlade s touto PD, platnými normami a technologickými postupmi výrobcu.

±0,000=133,70m n. m. Bpv

AUTORI:	Ing. arch. Ivor Mešiar, ArtD.		
HIP.:	Ing. arch. Ivor Mešiar, ArtD.		
ZODP. PROJEKTANT:	Ing. Ján Bátor		
VYPRACOVAL:	Ing. Viktor Labovský		
INVESTOR:	Chaco, s.r.o., Stará Vajnorská 17, 831 04 Bratislava		
NÁZOV STAVBY:	ASOC" – Administratívno-skladové a obchodné centrum – Hala „A"	DÁTUM:	03/2026
		FORMÁT:	1260 x 297mm
		MIERKA:	1 : 75
MIESTO STAVBY:	Stará Vajnorská 17, Bratislava 3, 831 04	STUPEŇ:	PSO
SO:	SO 01 – HALA „A"	ČASŤ PD:	ZTI
OBSAH VÝKRESU:	PÔDORYS STRECHY	REVÍZIA ČÍSLO VÝKRESU:	03