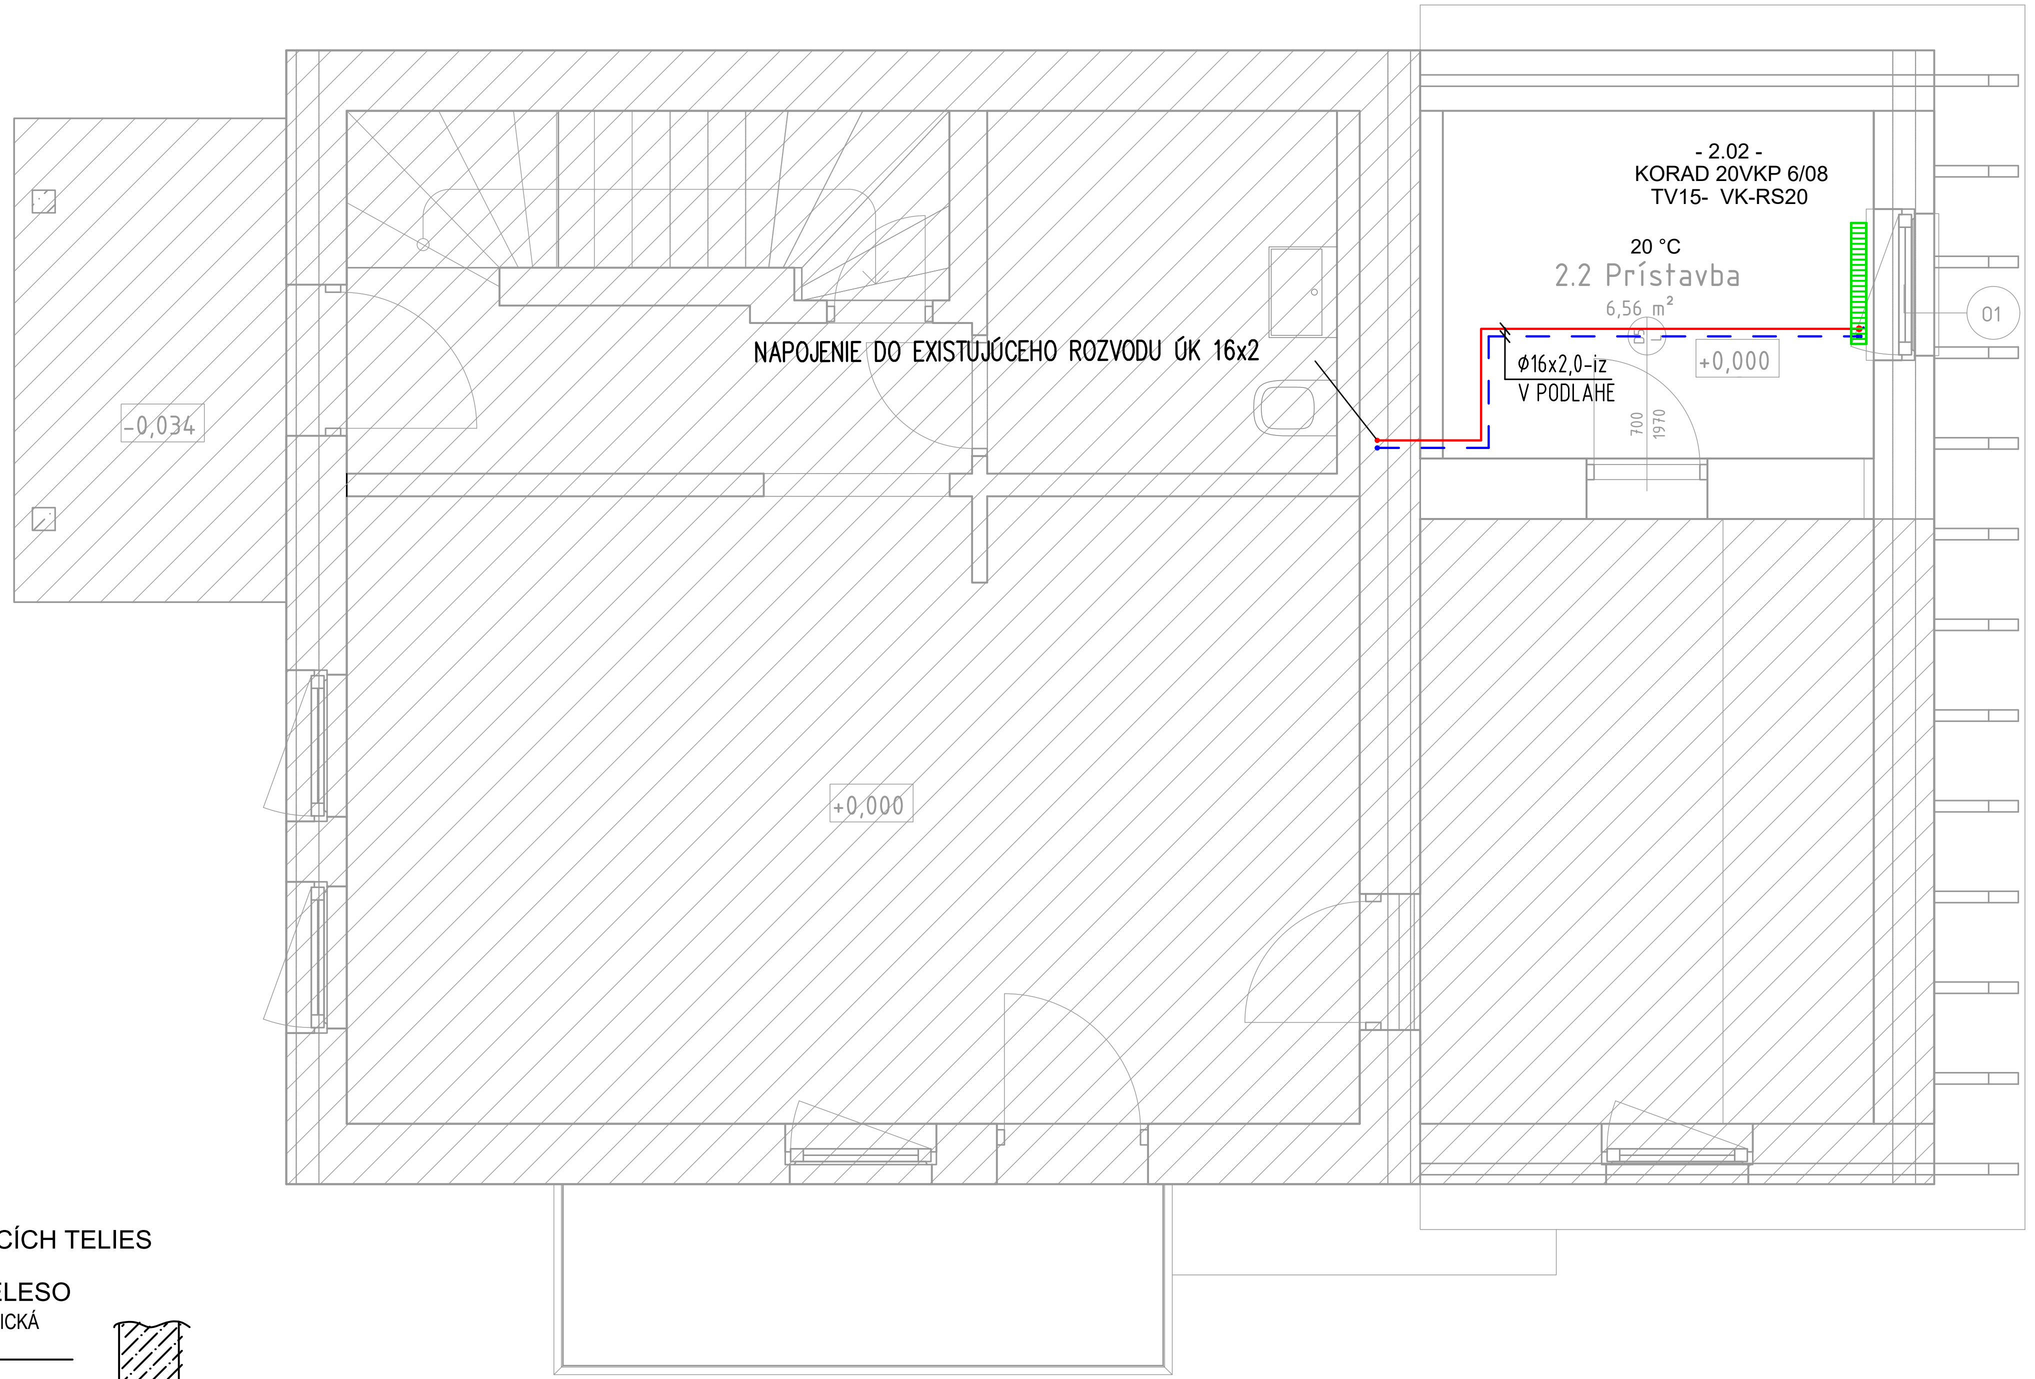

## DETAIL NAPOJENIA VYKUROVACÍCH TELIES

### DOSKOVÉ VYKUROVACIE TELESO

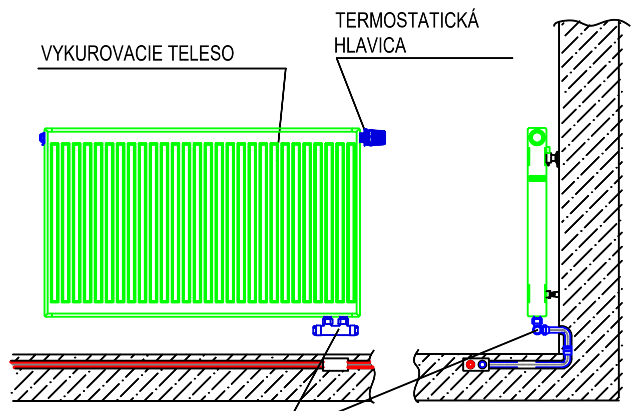

## LEGENDA

| | |
|---|---|
| 🟥 - - - | POTRUBIE – PLASTHLINNÍKOVÁ RÚRKA PE–Xa/AL/PE napr. RAUTITAN STABIL SPÁJANÉ LISOVANÍM, IZOLOVANÉ POTRUBIE |
| 🟩 | OCE?OVÉ DOSKOVÉ VYKUROVACIE TELESO min. VÝKON 600W napr. KORAD |

## POZNÁMKA :

- V PRÍPADE NEJASNOSTÍ VO VÝKRESOVEJ DOKUMENTÁCIÍ KONTAKTOVAŤ ZODPOVEDNÉHO PROJEKTANTA
- VŠETKY ROZMERY STAVEBNÝCH PRÁC KONTROLOVAŤ NA MIESTE STAVBY
- PRED UVEDENÍM SYSTÉMU DO PREVÁDZKY JE POTREBNÉ VYKONAŤ DÔKLADNÝ PREPLACH SYSTÉMU S VYČISTENÍM VŠETKÝCH FILTROV NA ROZVODE
- PO NAPUSTENÍ SYSTÉMU JE POTREBNÉ VYKONAŤ JEHO ODVZDUŠNENIE
- DODÁVATEL STAVBY JE POVINNÝ REALIZOVAŤ VŠETKY PRÁCE V ZMYSLE PLATNÝCH STN EN S DODRŽANÍM TECHNOLOGICKÝCH A BEZPEČNOSTNÝCH POSTUPOV. ĎALEJ JE POVINNÝ REŠPEKTOVAŤ USTANOVENIÁ STN 730421 O PRÍSLUŠNÝCH ROZMEROVÝCH ODCHÝLKACH REALIZOVANÝCH KONŠTRUKCIÍ PROTI PROJEKTOVANÉMU STAVU. KAŽDÚ ODCHÝLKU OD PROJEKTU JE POTREBNÉ PREROKOVAŤ S GP.
- PRESTUPY INŽINIERSKYCH SIETÍ A ROZVODOV V OBJEKTE JE POTREBNÉ VYNECHAŤ PRI REALIZÁCII STAVBY.
- DOKUMENTÁCIA SLÚŽI VÝHRADNE AKO PROJEKT PRE STAVEBNÝ ZÁMER A OVERENIE PROJEKTU STAVBY

TABULKA REVIZIÍ

| ČÍSLO REVÍZIE | DÁTUM | POPIS ZMENY | VYPRACOVAL |
|---|---|---|---|
| | | | |
| | | | |

0,000=132,6 m n. m.

| | | |
|---|---|---|
| AUTOR PROJEKTU: | Ing. arch. Ivor Mečiar ArtD. | GENERÁLNY PROJEKTANT:<br>Alla s.r.o.<br>Riazanská 70/683<br>831 02 Bratislava<br>tel.: +421 907 693 679<br>email: ateliar@alla.sk |
| H.I.P.: | Ing. arch. Ivor Mečiar ArtD. | |
| ZODP. PROJEKTANT: | Ing. arch. Ivor Mečiar ArtD. | |
| VYPRACOVAL: | Ing. Viktor Labovský | |

| | | | |
|---|---|---|---|
| INVESTOR: | Peter Lelkes, Kvetinárska 33, 821 06 Bratislava | PEČIATKA: | PARÉ: |
| NÁZOV PROJEKTU: | RD – AKTUÁL 20 | | ČÍSLO VÝKRESU:<br>001 |
| MIESTO STAVBY: | p.č. 341/6, k.ú. Podunajské Biskupice | | |
| OBSAH VÝKRESU: | PODORYS 1.NP | | |
| STAVEBNÝ OBJEKT: | S01 – RODINNÝ DOM | | |

| ID STAVBY: | STUPEŇ PD | URČENIE STAVBY: | IDENTIFIK. KÓD: | ČLENENIE DOK.: | PROFESIE: | ČÍSLO VÝKRESU: | NÁZOV VÝKRESU: | REVÍZIA: |
|---|---|---|---|---|---|---|---|---|
| --- | SZP | 01 | 1111 | SO1 | VYK | 001 | N01 | 00 |

NÁZOV VÝKRESU V ELEKTRONICKEJ PODOBE: -------SZP__1111_SO1_VYK_001_N01_00

| | |
|---|---|
| DÁTUM: | 07/2026 |
| FORMÁT: | 630 x 297mm |
| KÓD AKCIE: | |
| MIERKA: | 1:50 |