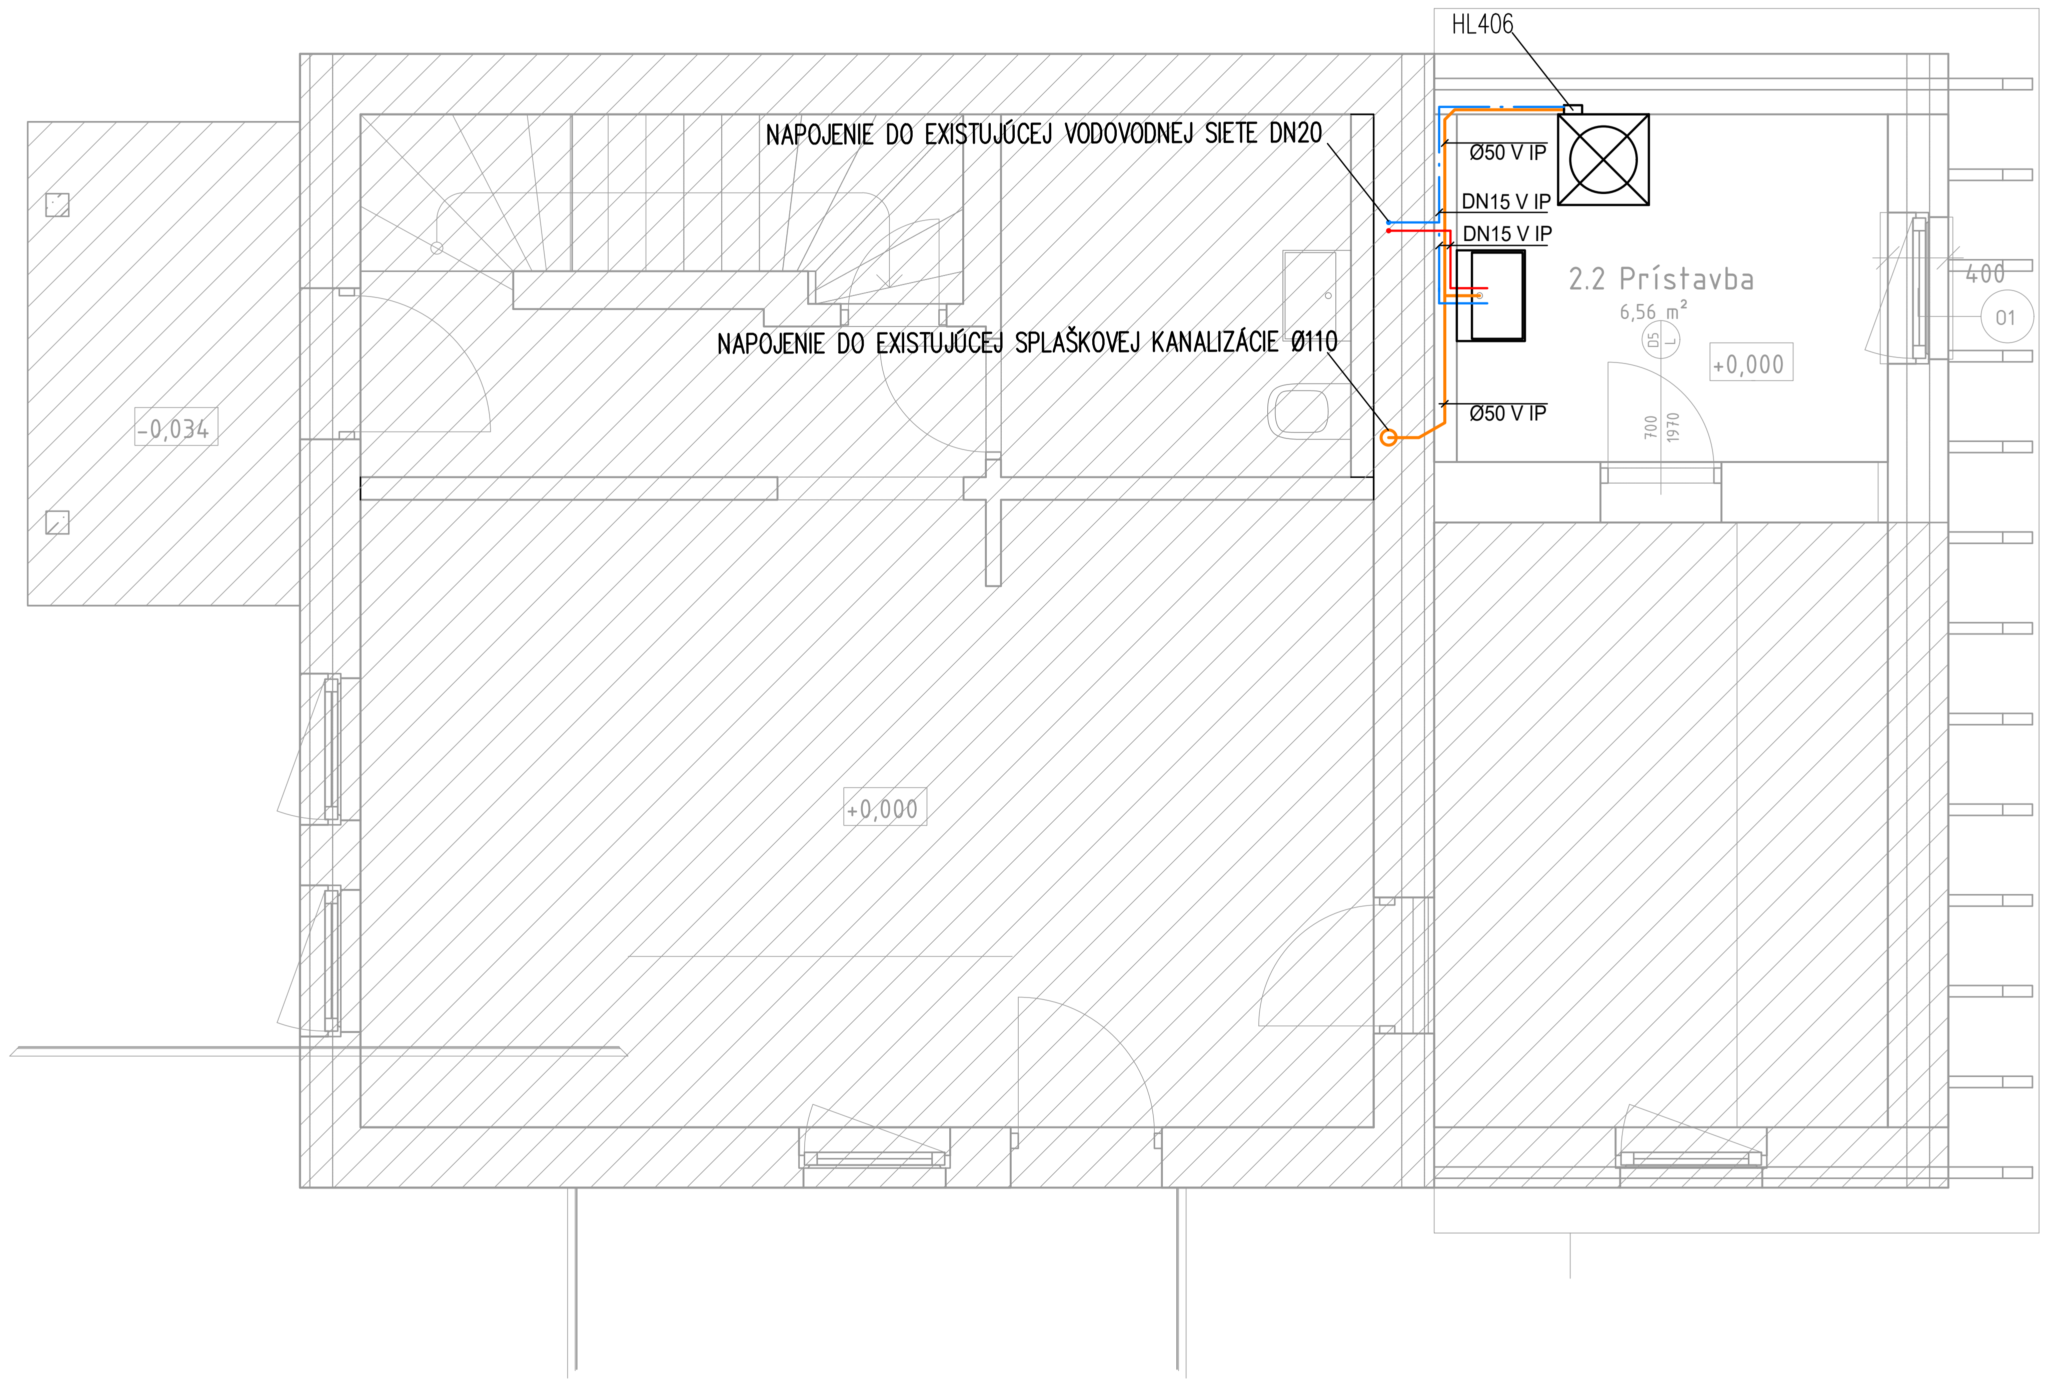
NAPOJENIE DO EXISTUJÚCEJ VODOVODNEJ SIETE DN20
NAPOJENIE DO EXISTUJÚCEJ SPLAŠKOVEJ KANALIZÁCIE Ø110
HL406
Ø50 V IP
DN15 V IP
DN15 V IP
Ø50 V IP
2.2 Prístavba
6,56 m²
D5
L
700
1970
+0,000
400
01
-0,034
+0,000

LEGENDA

POTRUBIE HDPE–Al–PEXb napr. GEBERIT MEPLA – STUDENÁ VODA
+ PLASTOVÁ TEPELNÁ IZOLÁCIA napr. MIRELON
SPÁJANÉ LISOVANÍM, IZOLOVANÉ POTRUBIE
+ PLASTOVÁ TEPELNÁ IZOLÁCIA napr. MIRELON

POTRUBIE ODPADOVÉ HRDLOVÉ Z PP RÚR PRE VNÚTORNÚ KANALIZÁCIU
+ odporúčané vyhotoviť z odhlučneného potrubia vrátane objímok
napr. MASTER3, Geberit silent

U	UMÝVADLO DITURVITOVÉ + PÁKOVÁ BATÉRIA STOJÁNKOVÁ + 2 x ROHOVÝ VENTIL DN 15
AP	AUTOMATICKÁ PRÁČKA, HL406.1

POZNÁMKA :

- V PRÍPADE NEJASNOSTÍ VO VÝKRESOVEJ DOKUMENTÁCIÍ KONTAKTOVAŤ ZODPOVEDNÉHO PROJEKTANTA
- VŠETKY ROZMERY STAVEBNÝCH PRÁC KONTROLOVAŤ NA MIESTE STAVBY
- PRED UVEDENÍM SYSTÉMU DO PREVÁDZKY JE POTREBNÉ VYKONAŤ DÔKLADNÝ PREPLACH SYSTÉMU S VYČISTENÍM VŠETKÝCH FILTROV NA ROZVODE
- PO NAPUSTENÍ SYSTÉMU JE POTREBNÉ VYKONAŤ JEHO ODVZDUŠNENIE
- DODÁVATEL STAVBY JE POVINNÝ REALIZOVAŤ VŠETKY PRÁCE V ZMYSLE PLATNÝCH STN EN S DODRŽANÍM TECHNOLOGICKÝCH A BEZPEČNOSTNÝCH POSTUPOV. ĎALEJ JE POVINNÝ REŠPEKTOVAŤ USTANOVENIÁ STN 730421 O PRÍSLUŠNÝCH ROZMEROVÝCH ODCHÝLKACH REALIZOVANÝCH KONŠTRUKCIÍ PROTI PROJEKTOVANÉMU STAVU. KAŽDÚ ODCHÝLKU OD PROJEKTU JE POTREBNÉ PREROKOVAŤ S GP.
- PRESTUPY INŽINIERSKYCH SIETÍ A ROZVODOV V OBJEKTE JE POTREBNÉ VYNECHAŤ PRI REALIZÁCII STAVBY.
- DOKUMENTÁCIA SLÚŽI VÝHRADNE AKO PROJEKT PRE STAVEBNÝ ZÁMER A OVERENIE PROJEKTU STAVBY

TABULKA REVIZIÍ

ČÍSLO REVÍZIE	DÁTUM	POPIS ZMENY	VYPRACOVAL

0,000=132,6 m n. m.

AUTOR PROJEKTU:	Ing. arch. Ivor Mečiar ArtD.	GENERÁLNY PROJEKTANT: Alla s.r.o. Riazanská 70/683 831 02 Bratislava tel.: +421 907 693 679 email: ateliar@alla.sk
H.I.P.:	Ing. arch. Ivor Mečiar ArtD.	
ZODP. PROJEKTANT:	Ing. arch. Ivor Mečiar ArtD.	
VYPRACOVAL:	Ing. Viktor Labovský	

INVESTOR:	Peter Lelkes, Kvetinárska 33, 821 06 Bratislava	PEČIATKA:	PARÉ:
NÁZOV PROJEKTU:	RD – AKTUÁL 20		
MIESTO STAVBY:	p.č. 341/6, k.ú. Podunajské Biskupice		ČÍSLO VÝKRESU: 001
OBSAH VÝKRESU:	PODORYS 1.NP		
STAVEBNÝ OBJEKT:	S01 – RODINNÝ DOM		

ID STAVBY:	STUPEŇ PD	URČENIE STAVBY:	IDENTIFIK. KÓD:	ČLENENIE DOK.:	PROFESIE:	ČÍSLO VÝKRESU:	NÁZOV VÝKRESU:	REVÍZIA:
---	SZP	01	1111	SO1	ZTI	001	N01	00

NÁZOV VÝKRESU V ELEKTRONICKEJ PODOBE: -------SZP__1111_SO1_ZTI_001_N01_00

DÁTUM: 07/2026
FORMÁT: 630 x 297mm
KÓD AKCIE:
MIERKA: 1:50