DETAIL ZAPOJENIA VYKUROVACÍCH TELIES REBRÍKOVÉ VYKUROVACIE TELESO

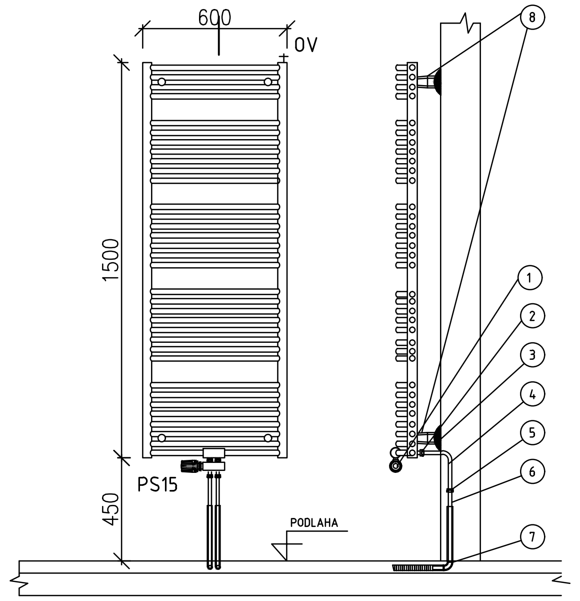

LEGENDA:

1 Stredové pripojenie vykurovacieho telesa, rozteč H=50mm
2 Svorková spojka
3 Krycia rozeta
4 Pripojovacia garnitúra s upevňovacím
5 Násuvná objímka
6 Vykurovacia rúrka
7 Vodiaci oblúk 90°
8 Stenová konzola

DETAIL ZAPOJENIA VYKUROVACÍCH TELIES DOSKOVÉ VYKUROVACIE TELESO

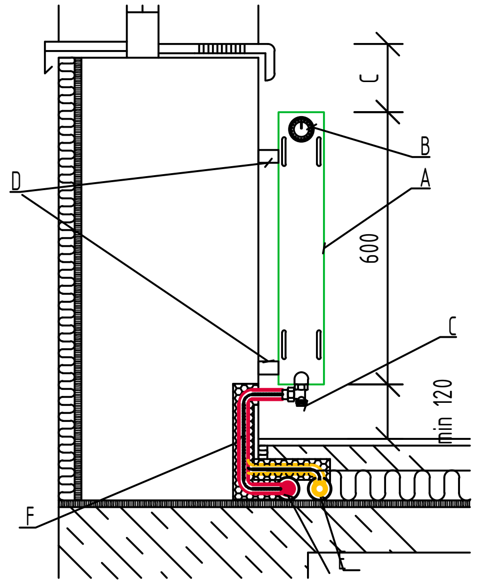

DETAIL OSADENIA VYK. TELESA
NA ROZVODY ÚK

A VYKUROVACIE TELESO
B TERMOSTATICKÁ HLAVICA
C ROHOVÁ PRIPOJOVACIA ARMATÚRA
D DRŽIAK
E ROZVODY ÚSTREDNÉHO KÚRENIA
F TRUBICOVÁ IZOLÁCIA

- 2.02 -	
Detska izba 1	
19.2 m2	47.0 m3
22 °C	488 W

- 2.03 -	
Detska izba 2	
16.8 m2	42.1 m3
22 °C	468 W

- 2.04 -	
Kupelna + wc	
6.1 m2	15.3 m3
24 °C	221 W

SYSTÉM	Elektrické vyhrievacie fólie KS
tep. výkon fólie	330 W
plocha fólie	3,0 m2

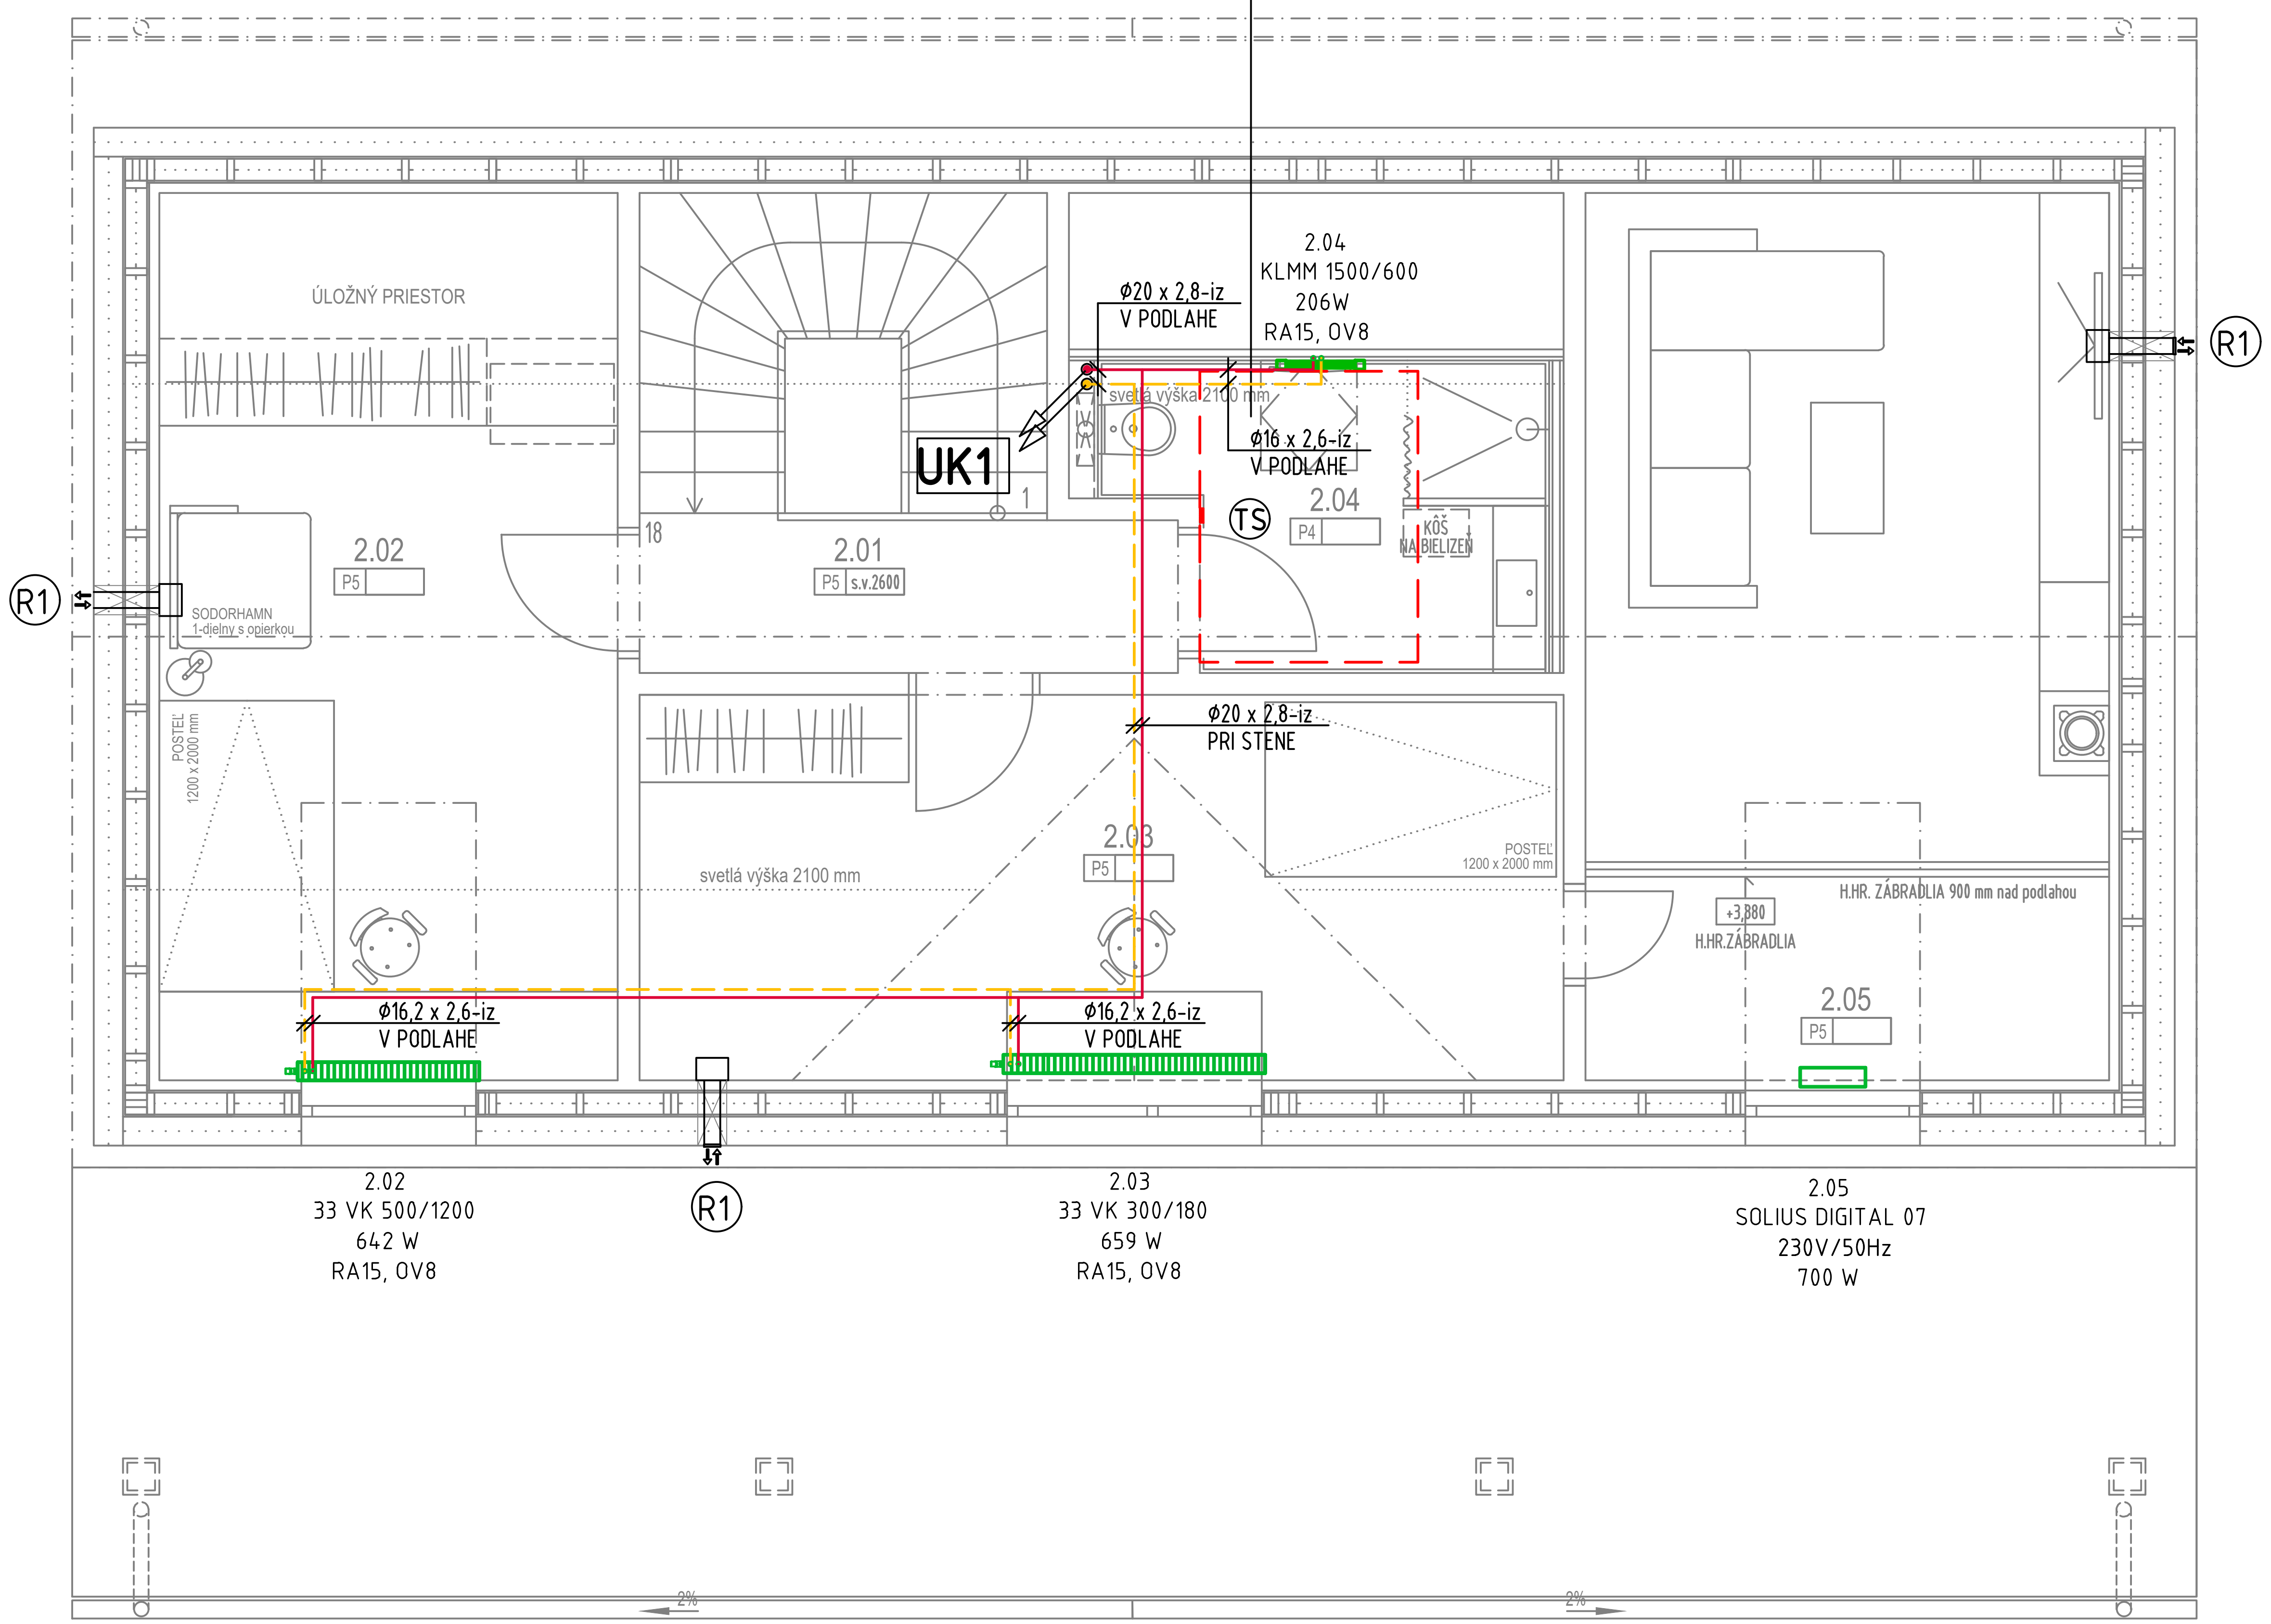

LEGENDA VYKUROVACÍCH TELIES:

🟩 OCEĽOVÉ DOSKOVÉ VYKUROVACIE TELESO RADIK
SPÔSOB ZNAČENIA TYP RADIK, SO SPODNÝM PRIPOJENÍM

33 VK 900 /900

- 900 – STAVEBNÁ DĹŽKA V MILIMETROCH
- 900 – STAVEBNÁ VÝŠKA V MILIMETROCH
- VK – PREVEDENIE VENTIL KOMPAKT - SO SPODNÝM PRIPOJENÍM
- 33 – TYP DVOJRADOVÝ

🟩 REBRÍKOVÉ VYKUROVACIE TELESO
TYP KORALUX LINEAR MAX-M, FY. KORADO

🟥 FÓLIOVÁ TECHNOLÓGIA SYSTÉMU VYHRIEVANIA NA ZÁKLADE DLHOVLNNÉHO INFRAČERVENÉHO ŽIARENIA

LEGENDA POTRUBIA:

POTRUBIE - PLASTHLINNÍKOVÁ RURKA PE-Xa/AL/PE napr. RAUTITAN Stabil REHAU
SPÁJANÉ LISOVANÍM, IZOLOVANÉ POTRUBIE, TEPLOTNÝ SPÁD 45/35°C. PRE PODLAHOVÉ VYKUROVANIE

POTRUBIE - PLASTHLINNÍKOVÁ RURKA PE-Xa/AL/PE napr. RAUTITAN Stabil REHAU
SPÁJANÉ LISOVANÍM, IZOLOVANÉ POTRUBIE, TEPLOTNÝ SPÁD 45/35°C.

ROZVOD ÚK PRE PRIMÁRNY OKRUH TEPELNÉHO ČERPADLA
PRE OKRUHY KONVEKČNÉHO VYKUROVANIA, PRÍVOD A SPATOČKA
MATERIÁL MEĎ

LEGENDA ZARIADENÍ A ARMATÚR :

1a	VNÚTORNÁ JEDNOTKA TEPELNÉHO ČERPADLA BRILON ELCO AEROTOP SPLIT 08.2 M-CR 1Z
1b	VONKAJ.JEDNOTKA BRILON ELCO AEROTOP SPLIT 08.2 M-CR 1Z MAX.VÝSTUPNÁ TEPLOTA 60°C,TEPELNY VYKON 8kW A7/W35, 3f-400V
03	AKUMULAČNÍ ZÁSOBNÍK VYKUROVACEJ VODY WPPS 130, Objem 130l
04	UZAVRETÁ TLAKOVÁ EXPANZNÁ NÁDOBA VIESSMANN C35 OBJEM 35L, 3bar
TP	TERMOSTAT PRIESTOROVÝ REMOCON PLUS 2
TE	SNÍMAČ VONKAJŠEJ TEPLOTY
R1	LOKÁLNA REKUPERAČNÁ JEDNOTKA TYPU NAPR. VIESSMANN VITOVENT 100-D
TS	PRIESTOROVÝ REGULÁTOR TEPLOTY PRE ELEKTRICKÉ PODLAHOVÉ VYKUROVANIE

- PRÍPADNÉ ZMENY PROJEKTU JE NUTNÉ PRED ICH REALIZÁCIOU PREKONZULTOVAŤ S AUTOROM PROJEKTU, ICH REALIZÁCIA JE MOŽNÁ NA ZÁKLADE JEHO PÍSOMNÉHO SÚHLASU !
- PRÍPADNÉ NEJASNOSTI V PROJEKTE JE NUTNÉ BEZODKLADNE OZNÁMIŤ ZODPOVEDNÉMU PROJEKTANTOVI !
- PROJEKTOVANÉ ROZMERY STAVEBNÝCH VÝROBKOV A KONŠTRUKCIÍ JE NUTNÉ PRED ICH ZADANÍM DO VÝROBY OVERIŤ PREMERANÍM PRIAMO NA STAVBE !

±0,000 = 300 mm nad U.T.

AUTOR PROJEKTU	Ing. Zlatica Janečková				
ZODPOVEDNÝ PROJEKTANT	Ing. Norbert Jókay				
INVESTOR	Petra Baričičová Kuchyňa 611				
MIESTO STAVBY	parc.č. 186/11 a 186/12, k.ú. Kuchyňa, obec Kuchyňa				
PROFESIA	Vykurovanie				
DRUH STAVBY	RODINNÝ DOM "PeBa"				
NÁZOV VÝKRESU	Pôdorys 2.NP	STUPEŇ	PSP	FORMÁT	3xA4
		DÁTUM	02/2026	MIERKA	1:50
OZNAČENIE VÝKRESU	2619AD_PSP_01_1111_S01_VYK_002_N02_00				