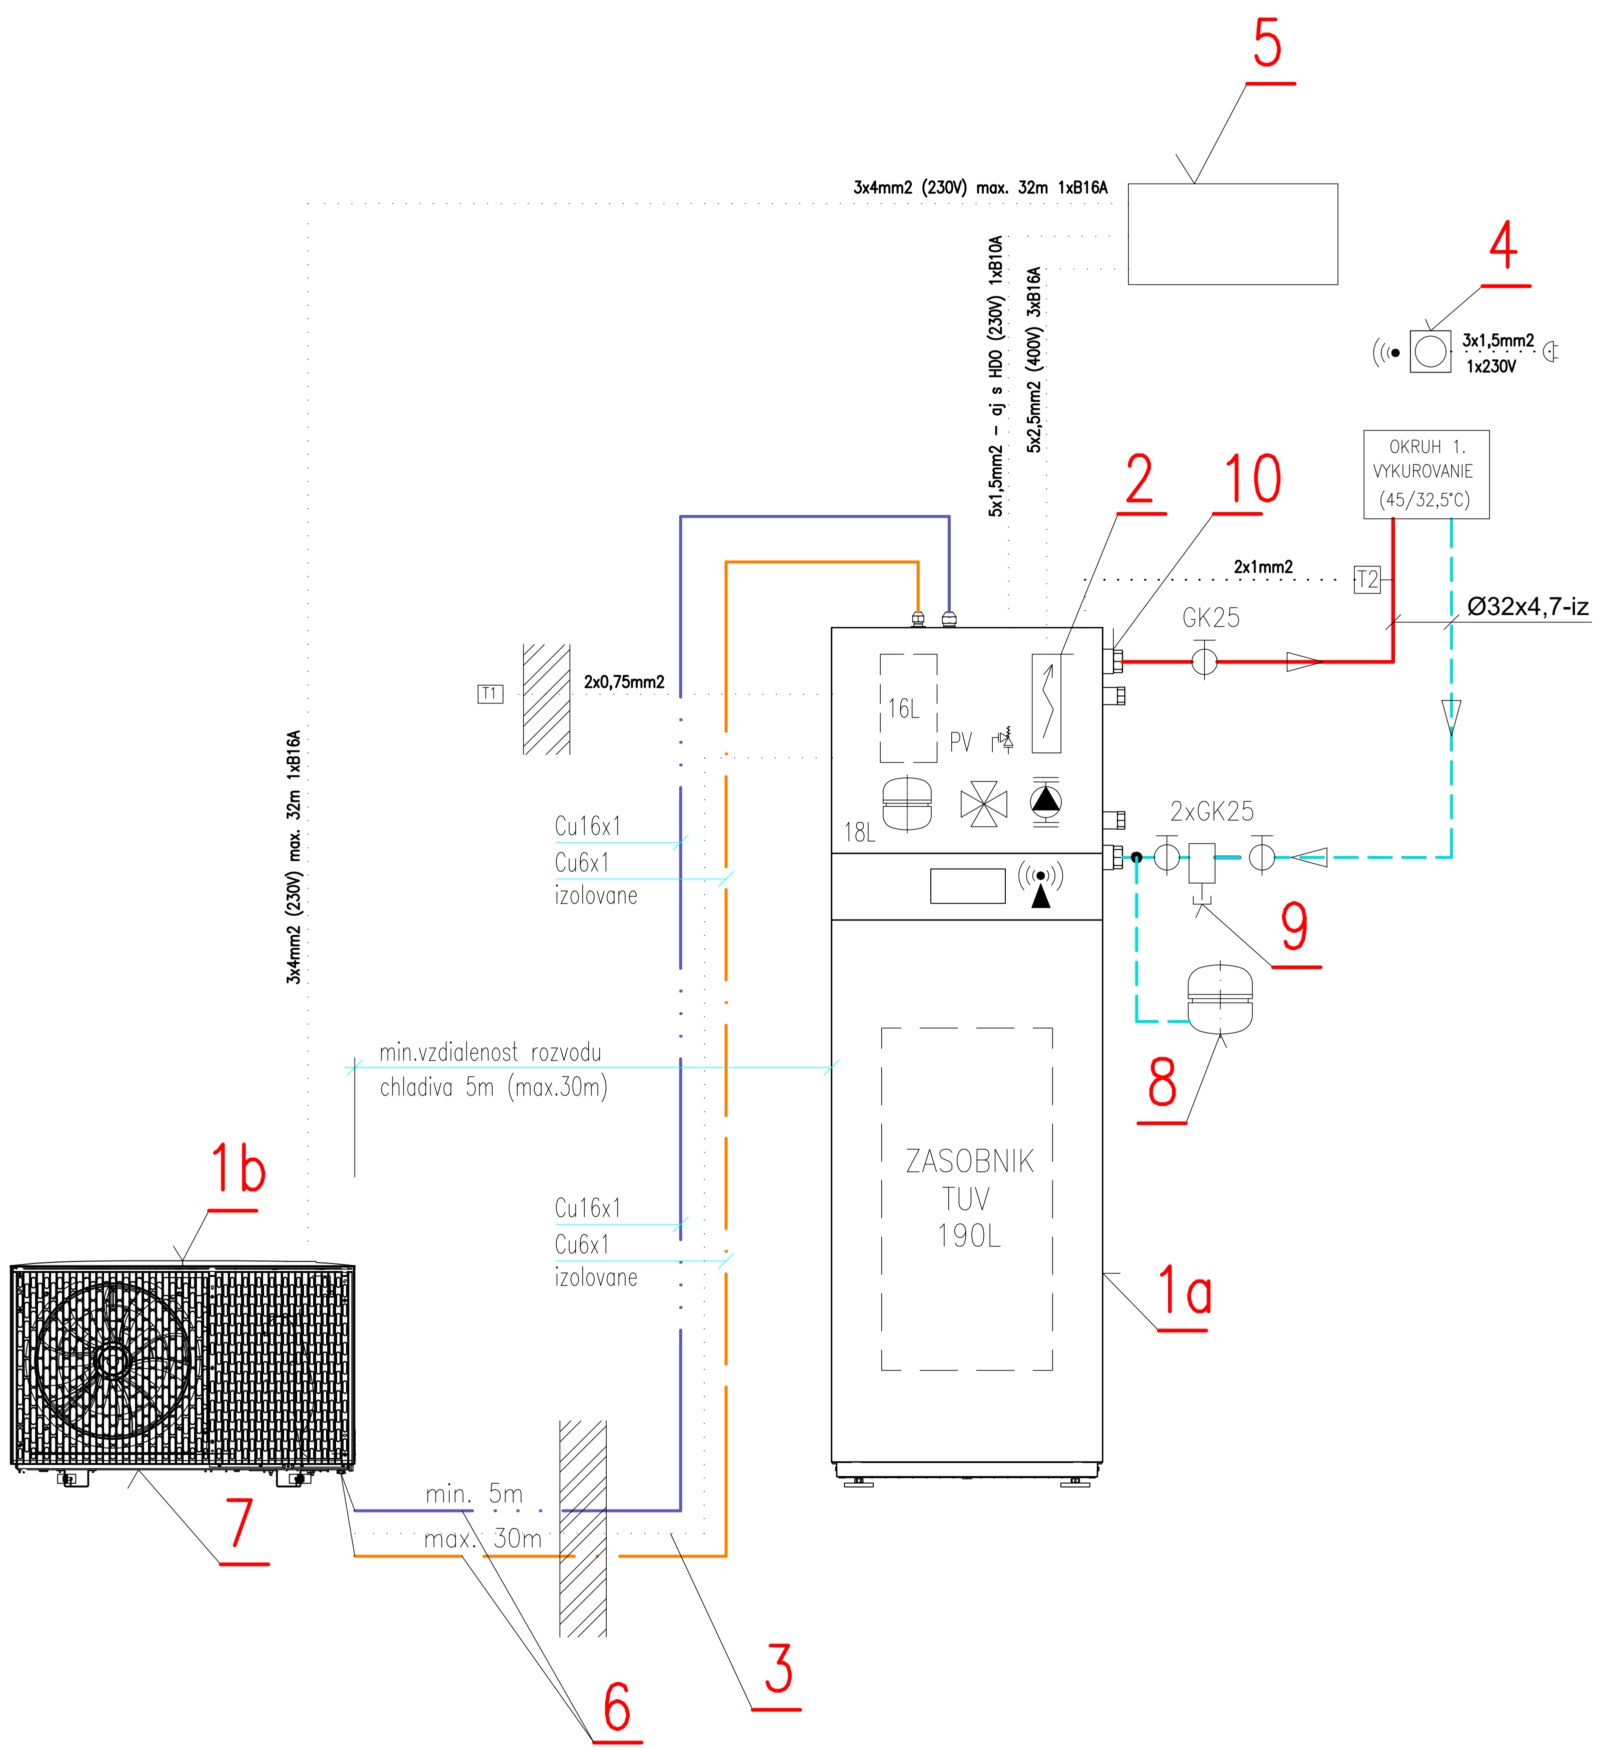

LEGENDA ZARIADENÍ:

POZ.	NÁZOV, ROZMER	P. KS
1a	VNUT. JEDNOTKA napr. VITOCAL 222-S AWBT-M-E-AC 221.E10	1
1b	VON. JEDNOTKA napr. VITOCAL 222-S AWBT-M-E-AC 221.E10 (230V)	1
	MAX.VÝSTUPNÁ TEPLOTA 60°C,TEPELNY VYKON 2,6-10,4kW A7/W35	
	EKOLOGICKE CHLADIVO R32, REGULÁCIA ONE-BASE,WIFI (Z022720)	
2	ELEKTRIC.PRIETOKOVY OHRIEVAC 8kW -v rozsahu dodavky pol.1a	1
3	CANBUS KOMUNIKACNY KABEL MEDZI JEDNOTKY 15m (ZK06217)	1
4	BEZDROTOVÉ DIALKOVE OVLADANIE VITOTROL 300-E (7959522)	1
5	ELEKTRICKY ROZVADZAC OBJEKTU	1
6	INSTALAC.SADA 12/6 NA ZEM+KONZOLA - 12,5M RURY (ZK06312)	1
7	ELEKTRIC.VYHREVNY PAS PRE VANU KONDENZATU 2,5m (ZK04098)	1
8	EXPANZNA NADOBA N25 OBJEM 25L, 4bar BIELA (7938081)	1
	NASTENNY DRZIAK PRE N25 (9572216)	1
9	ODKALOVAC S MAGNETOM A IZOLACIOU VITOTRAP 28mm (ZK04654)	1
10	PRIPOJOVACIA SADA NA OMIETKU-SPRAVA (ZK06403)-treba upresnit	1
T1	SNIMAC VONKAJSEJ TEPLOTY - v rozsahu dodavky tep.cerpadla	1
T2	SNIMAC ROSNEHO BODU - VLHKOSTI (7181418)	1

LEGENDA POTRUBÍ:

PLASTHLINÍKOVÉ POTRUBIE MATERIÁL: PE-XA/AL/PE NAPR. RAUTITAN STABIL, ZAIZOLOVANÉ POTRUBIE, TEPLOTNÝ SPÁD 45/32,5 °C.

MEDENÉ POTRUBIE PRIMÁRNEHO OKRUHU TEPELNÉHO ČERPADLA: CU Φ16×1, 6×1-IZ.

LEGENDA ARMATÚR :

GK	GUĽOVÝ KOHÚT SO ZÁVITOM
AOV	AUTOMATICKÝ ODVZDUŠŇOVACÍ VENTIL S UZATVÁRACOU ARMATÚROU
PV	POISTNÝ VENTIL SO ZÁVITOM

POZNÁMKY :

- V PRÍPADE AKÝCHKOĽVEK NEJASNOSTÍ V PROJEKTOVEJ DOKUMENTÁCII JE NUTNÉ KONTAKTOVAŤ ZODPOVEDNÉHO PROJEKTANTA.
- VŠETKY STAVEBNÉ ROZMERY A PRESTUPY JE POTREBNÉ OVERIŤ PRIAMO NA MIESTE REALIZÁCIE.
- PRED SAMOTNÝM SPUSTENÍM SYSTÉMU DO PREVÁDZKY SA MUSÍ VYKONAŤ DÔKLADNÝ PREPLACH ROZVODOV A VYČISTENIE VŠETKÝCH INŠTALOVANÝCH FILTROV.
- PO NAPUSTENÍ VYKUROVACEJ SÚSTAVY MÉDIOM JE NEVYHNUTNÉ ZABEZPEČIŤ JEJ POSTUPNÉ ODVZDUŠNENIE.
- ZHOTOVITEĽ JE POVINNÝ POSTUPOVAŤ V SÚLADE S PLATNÝMI NORMAMI STN EN A DODRŽIAVAŤ TECHNOLOGICKÉ AJ BEZPEČNOSTNÉ PREDPISY. ZÁROVEŇ MUSÍ REŠPEKTOVAŤ USTANOVENIA STN 730421 O ROZMEROVÝCH ODCHÝLKACH. KAŽDÚ ZMENU OPROTI PROJEKTU JE NUTNÉ VOPRED SKONZULTOVAŤ S HIP.
- OTVORY PRE PRESTUPY INŽINIERSKYCH SIETÍ A POTRUBNÝCH ROZVODOV V OBJEKTE JE POTREBNÉ PRIPRAVIŤ POČAS REALIZÁCIE HRUBEJ STAVBY.
- TÁTO DOKUMENTÁCIA NENAHRÁDZA REALIZAČNÚ DOKUMENTÁCIU STAVBY!
-VÝŠKOVÁ ÚROVEŇ ±0,000 V PROJEKTE ZODPOVEDÁ ÚROVNI FINÁLNEJ NÁŠĽAPNEJ VRSTVY PODLAHY.

TABUĽKA REVÍZIÍ

ČÍSLO REVÍZIE	DÁTUM	POPIS ZMENY	VYPRACOVAL

0,000=123,200 m n. m.

AUTOR PROJEKTU: Ing. arch. Ivor Mečiar, Matúš Sorokáč
H.I.P.: Ing. arch. Ivor Mečiar, ArtD.
ZODP. PROJEKTANT: Ing. Ján Bátor
VYPRACOVAL: Ing. Viktor Labovský

GENERÁLNY PROJEKTANT:
Alla s.r.o.
Riazanská 70/683
831 02 Bratislava
tel.: +421 907 693 679
email: ateliar@alla.sk

ALLA ARCHITEKTI

INVESTOR: Dominik Vanek, Veľka Paka 230, 930 51, Veľká Paka

NÁZOV PROJEKTU:

Bungalov - Veľká Paka

MIESTO STAVBY: 20/1, 20/2, Veľká Paka, PSČ 930 51
OBSAH VÝKRESU: SCHÉMA ZAPOJENIA
STAVEBNÝ OBJEKT: SO-01 RODINNÝ DOM

PEČIATKA: Ing. Ján BÁTOR 6172 * 14
PARÉ:
ČÍSLO VÝKRESU: 02

ID STAVBY:	STUPEŇ PD:	URČENIE STAVBY:	IDENTIFIK. KÓD:	ČLENENIE DOK.:	PROFESIE:	ČÍSLO VÝKRESU:	NÁZOV VÝKRESU:	REVÍZIA:
---	PSP	01	1111	SO1	VYK	002	N02	00

NÁZOV VÝKRESU V ELEKTRONICKEJ PODOBE:

DÁTUM: 06/2026
FORMÁT: 630x297
KÓD AKCIE:
MIERKA: