R-Z ZOSTAVA ROZDEĽOVAČA PODLAHOVÉHO VYKUROVANIA (TEPLOTNÝ SPÁD 45/35 °C)

10-OKRUHOVÝ ROZDEĽOVAČ NAPR. REHAU HKVD SX-AG 10, SKRINKA (ROZMER 577 X 510 X 80 MM).
ĎIAĽKOVÉ OVLÁDANIE TERMOSTATOV NAPR. REHAU NEA (230V)

4 KS PRIESTROVÝ TERMOSTAT NAPR. REHAU NEA (230V)

10 KS ELEKTRICKÝ SERVO-POHON (230V)

RZ 1 - 1. NP (9/9) (tp=45.0°C)	1.08 - Kúpelňa
PZ 1: Keramická dlažba 8 mm	S=3.7 m2
Systém VARIONOVA	Rúrka RAUTHERM S 17x2,0
Lpz=150 [mm]	lo/lp=24.9 m/5.1 m

RZ 1 - 1. NP (9/8) (tp=45.0°C)	1.07 - Detská izba
PZ 1: Laminátová podlaha 10 mm	S=11.2 m2
Systém VARIONOVA	Rúrka RAUTHERM S 17x2,0
Lpz/Loz=150/100 [mm]	lo/lp=84.2 m/15.1 m

RZ 1 - 1. NP (9/1) (tp=45.0°C)	1.06 - Detská izba
PZ 1: Laminátová podlaha 10 mm	S=12.6 m2
Systém VARIONOVA	Rúrka RAUTHERM S 17x2,0
Lpz/Loz=150/100 [mm]	lo/lp=94.0 m/9.3 m

RZ 1 - 1. NP (9/7) (tp=45.0°C)	1.03 - Obývacia izba
PZ 1: Laminátová podlaha 10 mm	S=6.4 m2
Systém VARIONOVA	Rúrka RAUTHERM S 17x2,0
Lpz/Loz=150/100 [mm]	lo/lp=49.0 m/14.6 m

RZ 1 - 1. NP (9/2) (tp=45.0°C)	1.05 - Spálňa
PZ 1: Laminátová podlaha 10 mm	S=8.0 m2
Systém VARIONOVA	Rúrka RAUTHERM S 17x2,0
Lpz/Loz=150/100 [mm]	lo/lp=59.4 m/11.5 m

RZ 1 - 1. NP (9/6) (tp=45.0°C)	1.03 - Obývacia izba
PZ 1: Laminátová podlaha 10 mm	S=6.6 m2
Systém VARIONOVA	Rúrka RAUTHERM S 17x2,0
Lpz/Loz=150/100 [mm]	lo/lp=50.5 m/18.7 m

RZ 1 - 1. NP (9/3) (tp=45.0°C)	1.05 - Spálňa
PZ 1: Laminátová podlaha 10 mm	S=8.2 m2
Systém VARIONOVA	Rúrka RAUTHERM S 17x2,0
Lpz/Loz=150/100 [mm]	lo/lp=60.7 m/14.4 m

RZ 1 - 1. NP (9/4) (tp=45.0°C)	1.04 - WC
PZ 1: Keramická dlažba 8 mm	S=4.0 m2
Systém VARIONOVA	Rúrka RAUTHERM S 17x2,0
Lpz=150 [mm]	lo/lp=26.7 m/12.2 m

RZ 1 - 1. NP (9/5) (tp=45.0°C)	1.02 - Kuchyňa
PZ 1: Laminátová podlaha 10 mm	S=8.3 m2
Systém VARIONOVA	Rúrka RAUTHERM S 17x2,0
Lpz=150 [mm]	lo/lp=55.5 m/11.6 m

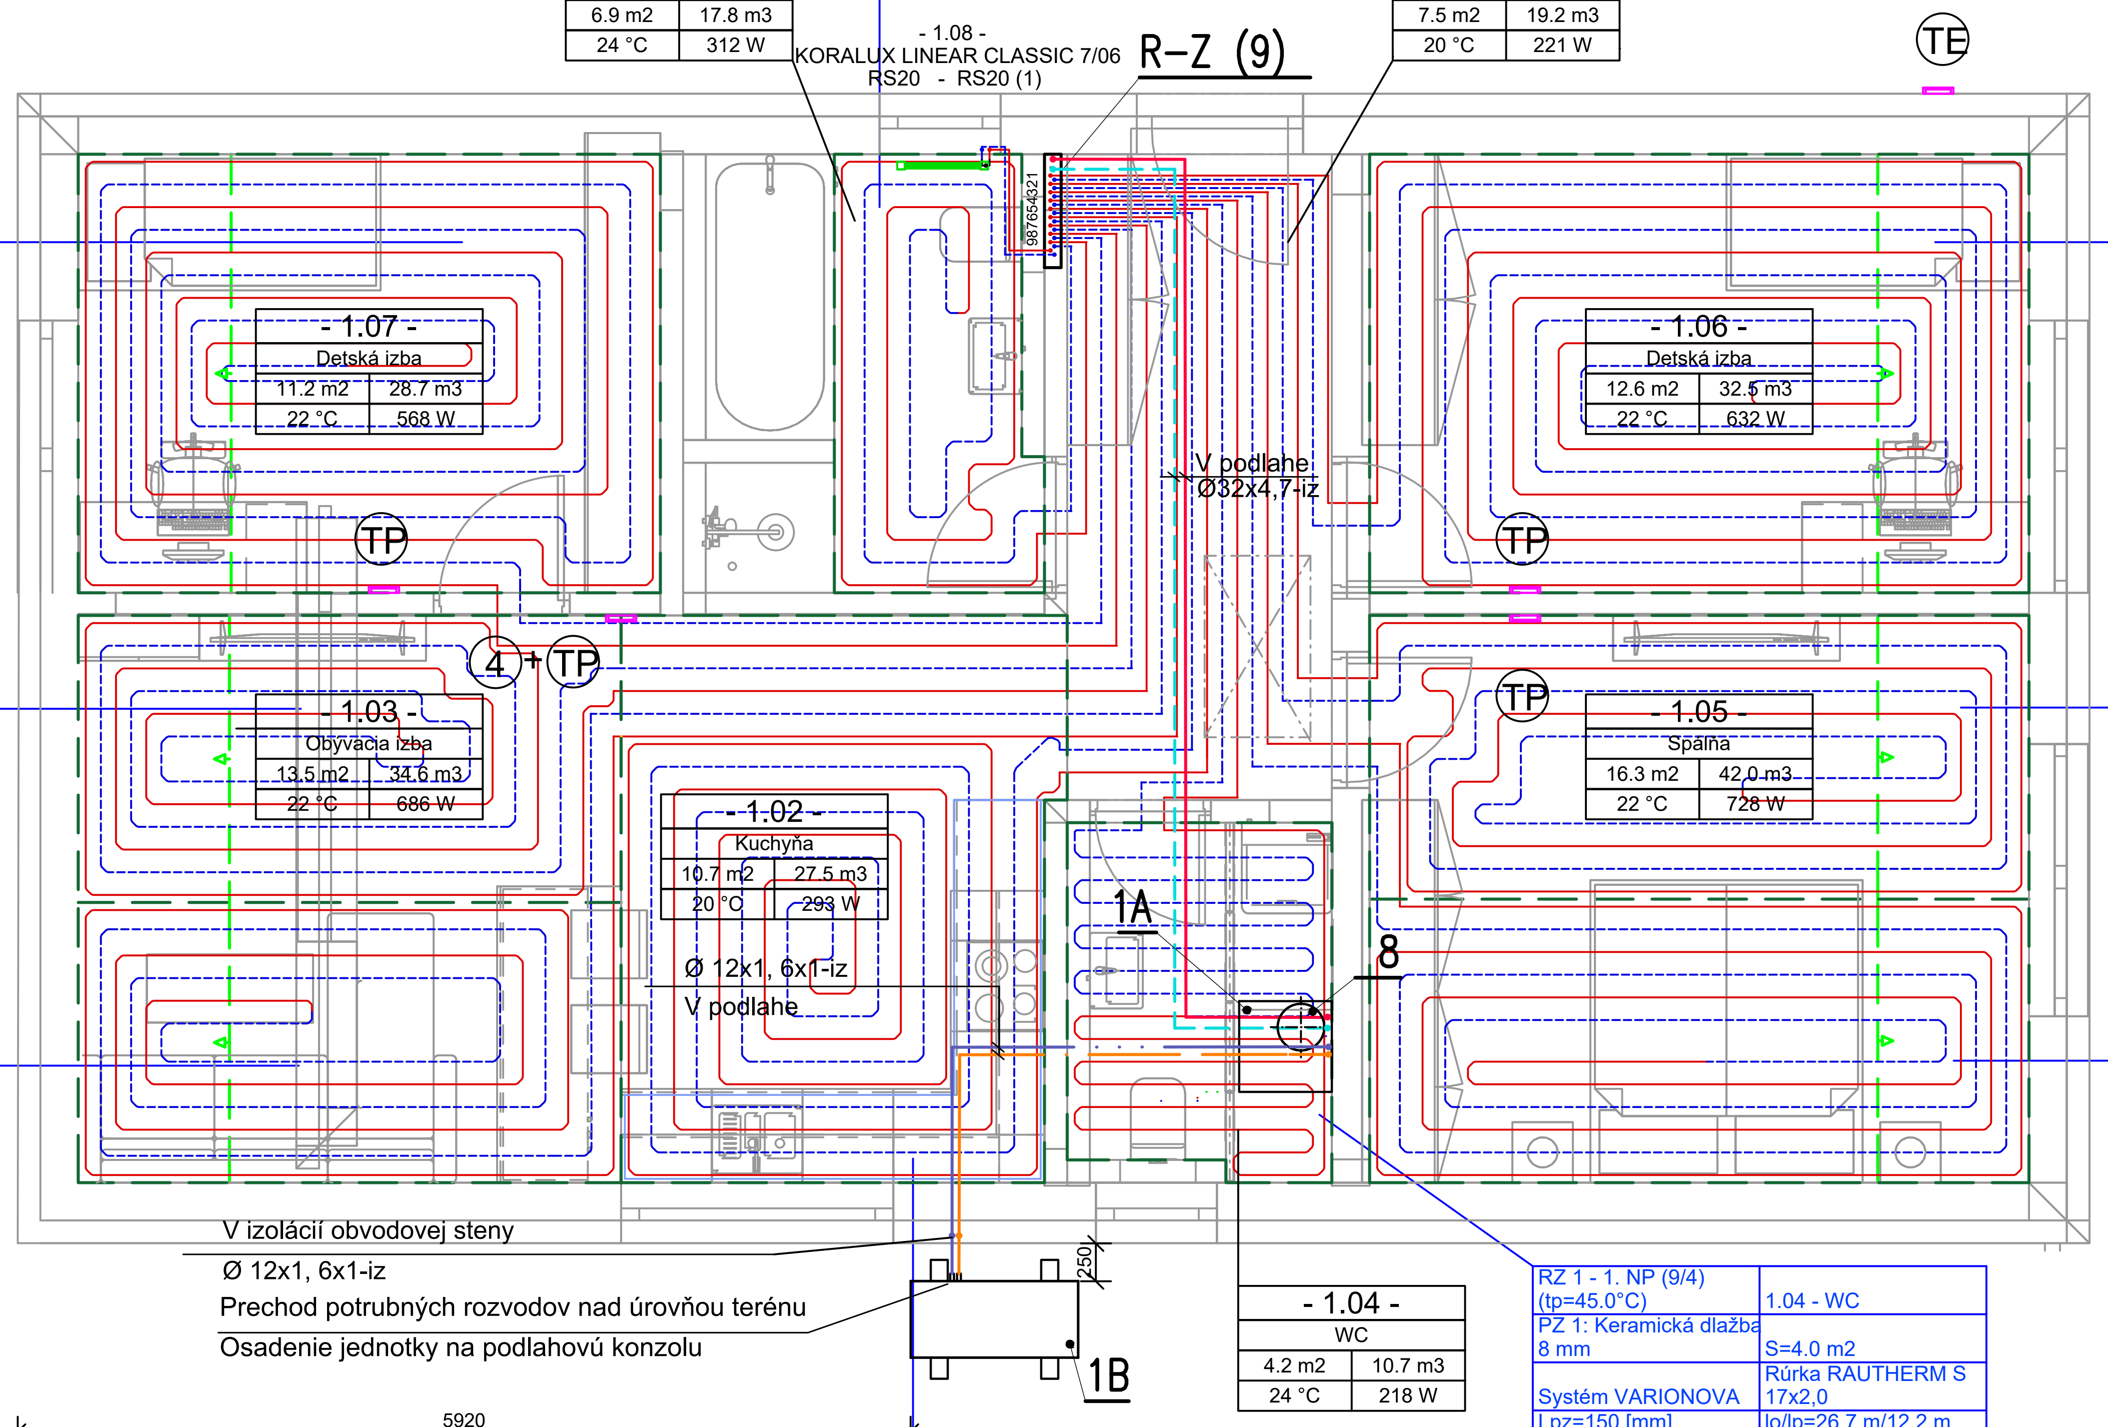

Podlahové vykurovanie Rehau

Vykurovacia plocha: S=4.2 m²

Typ nášľapnej vrstvy (PX): Keramická dlažba

Typ vykurovacej rúrky: Rúrka Rautherm S 17×2,0

Rozdeľovač: Rozdeľovač Rehau , skrinka rozdeľovača . 1. NP, napojenie 9 okruhov (tp=45 °C)

Systém uchytenia: Varionova – typ prichytenia potrubia pre podlahové kúrenie

TABUĽKA MIESTNOSTÍ 1.NP

Č. MIESTNOSTI	NÁZOV MIESTNOSTI	PLOCHA (m2)
1.01	Chodba	7,66
1.02	Kuchyňa	14,34
1.03	Obývacia izba	13,78
1.04	WC	4,28
1.05	Spálňa	19,18
1.06	Detská izba	15,22
1.07	Detská izba	11,70
1.08	WC	7,27
		93,43 m²

DETAIL NAPOJENIA VYKUROVACÍCH TELIES

REBRÍKOVÉ VYKUROVACIE TELESO

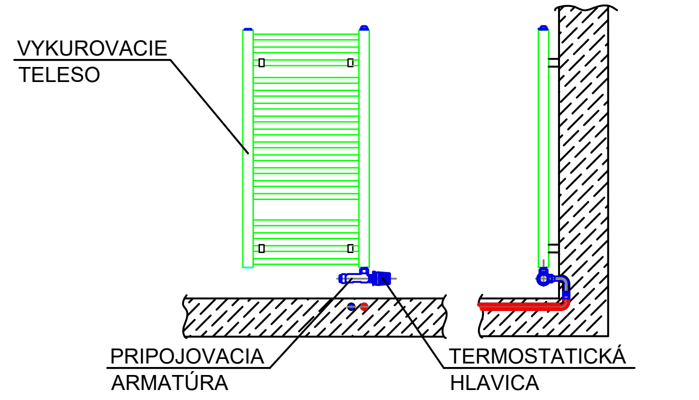

POZNÁMKY :

- V PRÍPADE AKÝCHKOĽVEK NEJASNOSTÍ V PROJEKTOVEJ DOKUMENTÁCII JE NUTNÉ KONTAKTOVAŤ ZODPOVEDNÉHO PROJEKTANTA.
- VŠETKY STAVEBNÉ ROZMERY A PRESTUPY JE POTREBNÉ OVERIŤ PRIAMO NA MIESTE REALIZÁCIE.
- PRED SAMOTNÝM SPUSTENÍM SYSTÉMU DO PREVÁDZKY SA MUSÍ VYKONAŤ DÔKLADNÝ PREPLACH ROZVODOV A VYČISTENIE VŠETKÝCH INŠTALOVANÝCH FILTROV.
- PO NAPUSTENÍ VYKUROVACEJ SÚSTAVY MÉDIOM JE NEVYHNUTNÉ ZABEZPEČIŤ JEJ POSTUPNÉ ODVZDUŠNENIE.
- ZHOTOVITEĽ JE POVINNÝ POSTUPOVAŤ V SÚLADE S PLATNÝMI NORMAMI STN EN A DODRŽIAVAŤ TECHNOLOGICKÉ AJ BEZPEČNOSTNÉ PREDPISY. ZÁROVEŇ MUSÍ REŠPEKTOVAŤ USTANOVENIA STN 730421 O ROZMEROVÝCH ODCHÝLKACH. KAŽDÚ ZMENU OPROTI PROJEKTU JE NUTNÉ VOPRED SKONZULTOVAŤ S HIP.
- OTVORY PRE PRESTUPY INŽINIERSKYCH SIETÍ A POTRUBNÝCH ROZVODOV V OBJEKTE JE POTREBNÉ PRIPRAVIŤ POČAS REALIZÁCIE HRUBEJ STAVBY.
- TÁTO DOKUMENTÁCIA NENAHRÁDZA REALIZAČNÚ DOKUMENTÁCIU STAVBY!
-VÝŠKOVÁ ÚROVEŇ ±0,000 V PROJEKTE ZODPOVEDÁ ÚROVNI FINÁLNEJ NÁŠĽAPNEJ VRSTVY PODLAHY.

LEGENDA POTRUBÍ:

🟥 ━━━ / 🟦 – – –	PLASTHLINÍKOVÉ POTRUBIE NAPR. RAUTHERM S 17×2,0 REHAU, TEPLOTNÝ SPÁD 45/35 °C, VEDENÉ V PODLAHE.
🟥 ━━━ / – – –	PLASTHLINÍKOVÉ POTRUBIE MATERIÁL: PE-XA/AL/PE NAPR. RAUTITAN STABIL, ZAIZOLOVANÉ POTRUBIE, TEPLOTNÝ SPÁD 45/35 °C.
—··· — / —·—	MEDENÉ POTRUBIE PRIMÁRNEHO OKRUHU TEPELNÉHO ČERPADLA: CU Φ12×1, 6×1-IZ.

LEGENDA ZARIADENÍ:

1A	TEPELNÉ ČERPADLO (VNÚTORNÁ JEDNOTKA) NAPR.: VIESSMANN VITOCAL 222-S. INTEGROVANÝ ZÁSOBNÍK NA TV (190 L), NAPÁJANIE 230V/50HZ.
1B	TEPELNÉ ČERPADLO (VONKAJŠIA JEDNOTKA) NAPR.: VITOCAL 222-S. VÝKON (A7/W35): 2,6 – 7,5 KW.
4	OVLÁDANIE: BEZDRÔTOVÝ DIAĽOVÝ OVLÁDAČ NAPR. VITOTROL 300-E.
8	EXPANZNÁ NÁDOBA NAPR: VIESSMANN N25 (OBJEM 25 L, MAX. TLAK 3 BAR).
TP	IZBOVÝ REGULÁTOR NAPR.: REHAU NEA SMART 2.0 (MERANIE TEPLOTY).
TE	SNÍMAČ TEPLOTY EXTERIÉRU.
🟩	REBRÍKOVÉ VYKUROVACIE TELESO KORALUX LINEAR CLASSIC DOPLNENÉ O EL. VYKUROVACIU VLOŽKU 230V

TABUĽKA REVÍZIÍ

ČÍSLO REVÍZIE	DÁTUM	POPIS ZMENY	VYPRACOVAL

0,000=223,560 m n. m.

AUTOR PROJEKTU:	Ing. arch. Ivor Mečiar, Matúš Sorokáč
H.I.P.:	Ing. arch. Ivor Mečiar, ArtD.
ZODP. PROJEKTANT:	Ing. Ján Bátor
VYPRACOVAL:	Ing. Viktor Labovský

GENERÁLNY PROJEKTANT:
Alla s.r.o.
Riazanská 70/683
831 02 Bratislava
tel.: +421 907 693 679
email: ateliar@alla.sk
ALLA ARCHITEKTI

INVESTOR:	Sýkora Daniel, Ing., Palisády 736/46, Bratislava, PSČ 811 06, SR
NÁZOV PROJEKTU:	**IBV - POD PRIEHRADOU**
MIESTO STAVBY:	Kuchyňa, p.č. 2375/42,43,44,45,46
OBSAH VÝKRESU:	PÔDORYS 1.NP
STAVEBNÝ OBJEKT:	SO-01 RODINNÝ DOM

PEČIATKA: Ing. Ján BÁTOR 6172 * 14

PARÉ:

ČÍSLO VÝKRESU: 01

ID STAVBY:	STUPEŇ PD:	URČENIE STAVBY:	IDENTIFIK. KÓD:	ČLENENIE DOK.:	PROFESIE:	ČÍSLO VÝKRESU:	NÁZOV VÝKRESU:	REVÍZIA:
---	PSP	01	1111	SO1	VYK	001	N01	00

NÁZOV VÝKRESU V ELEKTRONICKEJ PODOBE:

DÁTUM: 06/2026
FORMÁT: 630x420
KÓD AKCIE:
MIERKA: 1:50