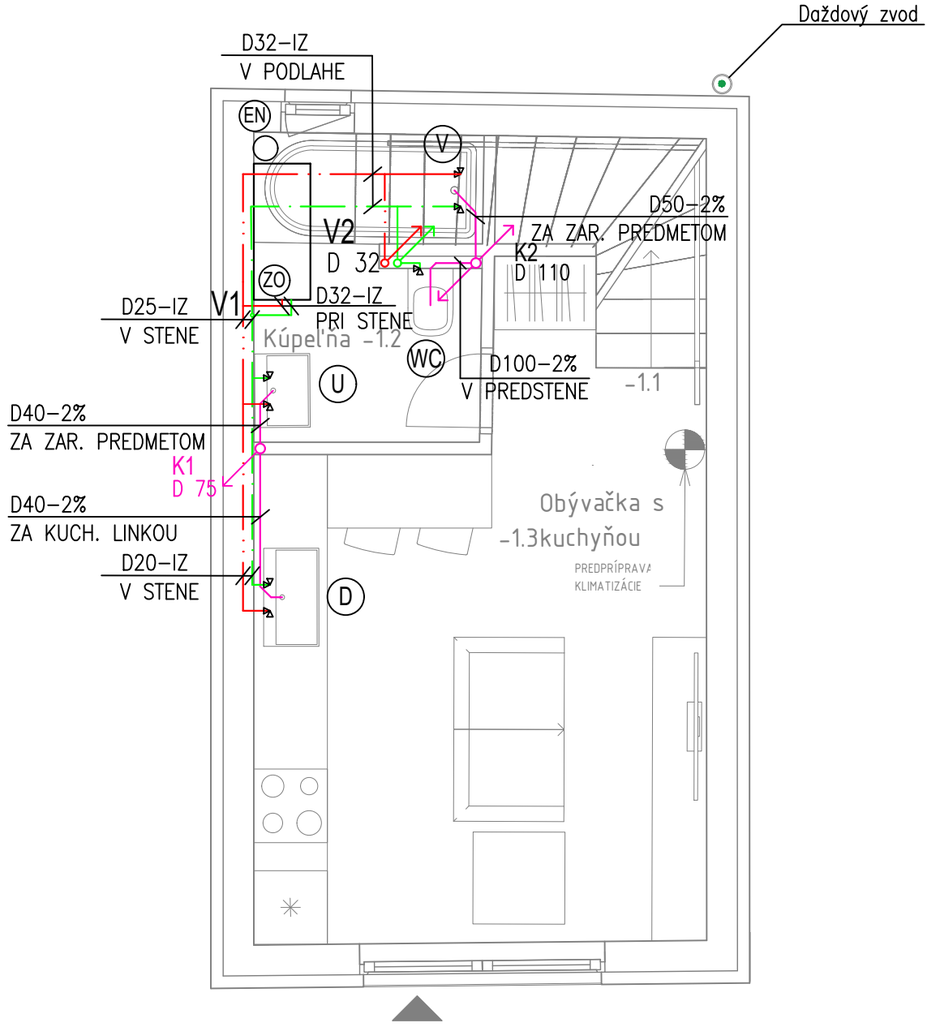


LEGENDA PROJEKTOVANÉHO POTRUBIA

- POTRUBIE STUDENEJ PITNEJ VODY
- POTRUBIE OHRIATEJ PITNEJ VODY
- SPLAŠKOVÉ KANALIZAČNÉ POTRUBIE
- DAŽDOVÉ KANALIZAČNÉ POTRUBIE

K1	STÚPACIE KANALIZAČNÉ POTRUBIE - SPLAŠKOVÉ
D1	STÚPACIE KANALIZAČNÉ POTRUBIE - DAŽDOVÉ
V1	STÚPACIE VODOVODNÉ POTRUBIE

LEGENDA MIESTNOSTÍ 1.PP

M.Č.	Názov	Plocha	Povrchové úpravy			Poznámky
			Podlahy	Steny		
2.1	Schody	4,40 m²	podľa výberu investora	podľa výberu investora	podľa výberu investora	
2.2	Kúpeľňa	4,51 m²	podľa výberu investora	podľa výberu investora	podľa výberu investora	
2.3	Obývačka s kuchyňou	14,71 m²	podľa výberu investora	podľa výberu investora	podľa výberu investora	
Spolu: 3		23,61 m²				

LEGENDA ZARIADENÍ

- (U) UMÝVADLO
- (D) DREZ
- (V) VAŇA
- (S) SPRCHA
- (WC) TOALETA
- (EN) TLAKOVÁ EXPANZNÁ NÁDOBA 8l
- (ZO) ZÁSOBNÍKOVÝ OHRIEVAČ TEPLEJ VODY, ZÁVESNÝ, S OBJEMOM 120 l, EL. VÝKON 2,0 kW

POZNÁMKY:

- VŠETKY ROZMERY STAVEBNÝCH PRÁC KONTROLOVAŤ NA MIESTE STAVBY
- DOPORUČUJEM PREKÁBLOVANIE JEDNOTLIVÝCH TERMOSTATOV PODLAHOVÉHO VYKUROVANIA
- V PRÍPADE NEJASNOSTÍ VO VÝKRESOVEJ DOKUMENTÁCII KONTAKTOVAŤ ZODPOVEDNÉHO PROJEKTANTA S PRISLÚCHAJÚCOU REGULÁCIOU EŠTE PRED ZHOTOVENÍM OMIETOK
- DODÁVATEĽ STAVBY JE POVINNÝ REALIZOVAŤ VŠETKY PRÁCE V ZMYSLE PLATNÝCH STN EN S DODRŽANÍM TECHNOLOGICKÝCH A BEZPEČNOSTNÝCH POSTUPOV. ĎALEJ JE POVINNÝ REŠPEKTOVAŤ USTANOVENIA STN 730421 O PRÍSLUŠNÝCH ROZMEROVÝCH ODCHÝLKACH REALIZOVANÝCH KONŠTRUKCIÍ PROTI PROJEKTOVANÉMU STAVU. KAŽDÚ ODCHÝLKU OD PROJEKTU JE POTREBNÉ PREROKOVAŤ S GP.
- ±0,000 SA VZŤAHUJE K ÚROVNI FINÁLNEJ ÚPRAVY PODLAHY
- VÝBER VYKUROVACÍCH TELIES PODĽA INVESTORA

TABUĽKA REVÍZIÍ

ČÍSLO REVÍZIE	DÁTUM	POPIS ZMENY	VYPRACOVAL

0,000=256,300 m n. m.

AUTOR PROJEKTU:	Ing. arch. Ivor Mečiar, ArtD.
H.I.P.:	Ing. arch. Ivor Mečiar, ArtD.
ZODP. PROJEKTANT:	Ing. arch. Ivor Mečiar, ArtD.
VYPRACOVAL:	Bc. Viktor Labovský

GENERÁLNY PROJEKTANT:
Alla s.r.o.
Riazanská 70/683
831 02 Bratislava
tel.: +421 907 693 679
email: ateliar@alla.sk

INVESTOR: Haverčáková Viera r. Miznerová, Novohradská 1283/1, Bratislava

NÁZOV PROJEKTU: ZAHRADNA CHATKA ZLATÁ HORA

MIESTO STAVBY: Zlatá hora B, Stupava, p.č 5329/11

OBSAH VÝKRESU: **ZTI - Pôdorys 1. PP**

STAVEBNÝ OBJEKT: REKREAČNÁ ZÁHRADNÁ STAVBA

ID STAVBY:	STUPEŇ PD:	URČENIE STAVBY:	IDENTIFIK. : KÓD	ČLENENIE DOK.:	PROFESIE:	ČÍSLO VÝKRESU:	NÁZOV VÝKRESU:	REVÍZIA:

NÁZOV VÝKRESU V ELEKTRONICKEJ PODOBE:

PEČIATKA:

PARÉ:

ČÍSLO VÝKRESU: 2

DÁTUM: 05/2026

FORMÁT: 420 x 297mm

KÓD AKCIE:

MIERKA: 1:50