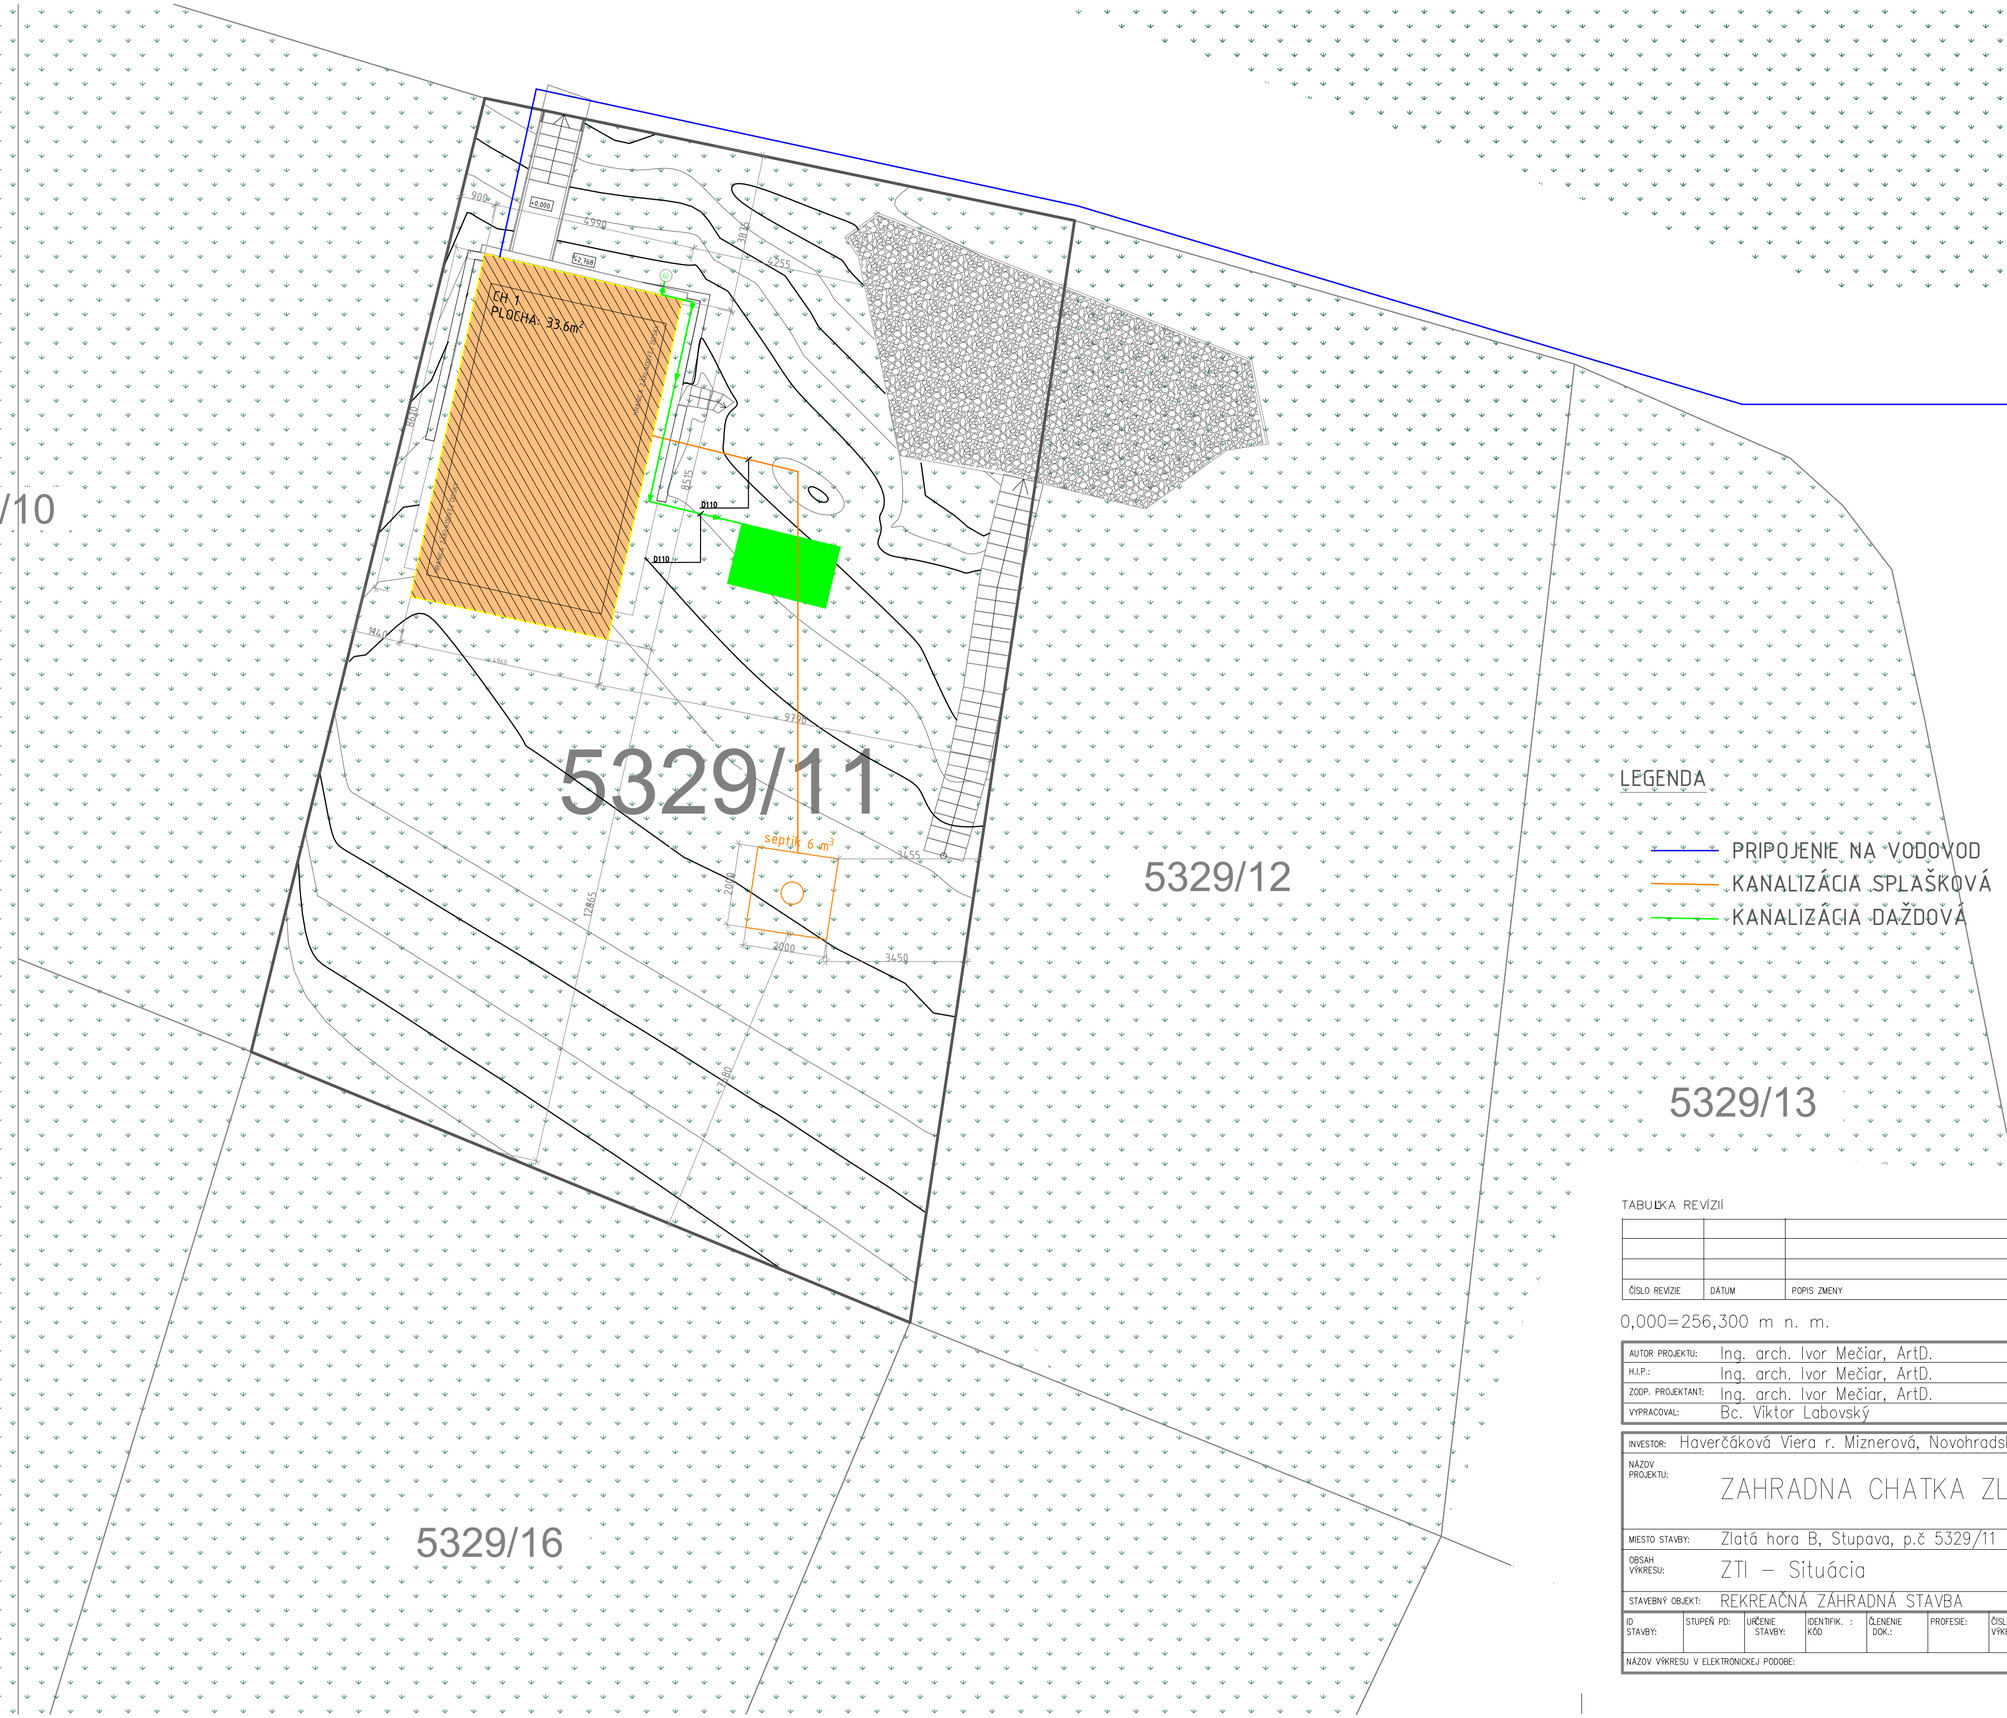


LEGENDA

- PRIPOJENIE NA VODOVOD
- KANALIZÁCIA SPLAŠKOVÁ
- KANALIZÁCIA DAŽDOVÁ

TABUĽKA REVÍZIÍ

ČÍSLO REVÍZIE	DÁTUM	POPIS ZMENY	VYPRACOVAL

0,000=256,300 m n. m.

AUTOR PROJEKTU:	Ing. arch. Ivor Mečiar, ArtD.	GENERÁLNY PROJEKTANT: Alla s.r.o. Riazanská 70/683 831 02 Bratislava tel.: +421 907 693 679 email: ateliar@alla.sk
H.I.P.:	Ing. arch. Ivor Mečiar, ArtD.	
ZODP. PROJEKTANT:	Ing. arch. Ivor Mečiar, ArtD.	
VYPRACOVAL:	Bc. Viktor Labovský	

INVESTOR:	Haverčáková Viera r. Miznerová, Novohradská 1283/1, Bratislava									PEČIATKA:	PARE:
NÁZOV PROJEKTU:	ZAHRADNA CHATKA ZLATÁ HORA										
MIESTO STAVBY:	Zlatá hora B, Stupava, p.č 5329/11										ČÍSLO VÝKRESU: 1
OBSAH VÝKRESU:	ZTI – Situácia										
STAVEBNÝ OBJEKT:	REKREAČNÁ ZÁHRADNÁ STAVBA										
ID STAVBY:	STUPEŇ PD:	URČENIE STAVBY:	IDENTIFIK. : KÓD	ČLENENIE DOK.:	PROFESIE:	ČÍSLO VÝKRESU:	NÁZOV VÝKRESU:	REVÍZIA:	DÁTUM: 05/2026	MIERKA: 1:100	
NÁZOV VÝKRESU V ELEKTRONICKEJ PODOBE:									FORMÁT: 630 x 420mm		
									KÓD AKCIE:		