
SYSTÉM	Elektrické vyhrievacie fólie KS
tep. výkon fólie	165 W
plocha fólie	1,50 m2

SYSTÉM	Elektrické vyhrievacie fólie KS
tep. výkon fólie	165 W
plocha fólie	1,50 m2

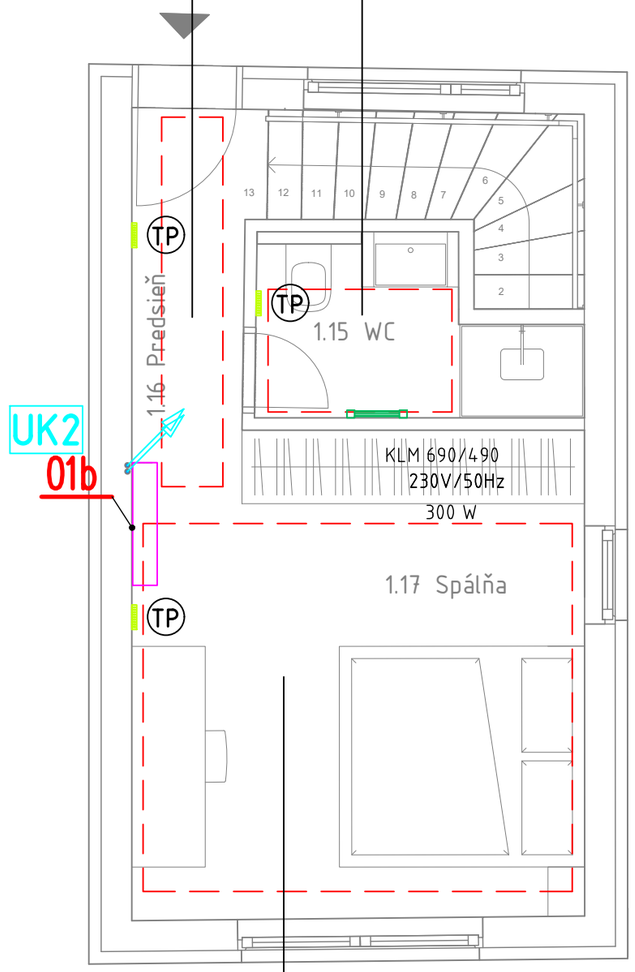

SYSTÉM	Elektrické vyhrievacie fólie KS
tep. výkon fólie	1155 W
plocha fólie	10,5 m2

LEGENDA MIESTNOSTÍ 1.NP

M.Č.	Názov	Plocha	Povrchové úpravy			Poznámky
			Podlahy	Steny	Stropy	
2.15	WC	3,20 m^2	podľa výberu investora	podľa výberu investora	podľa výberu investora	
2.16	Predsieň	6,03 m^2	podľa výberu investora	podľa výberu investora	podľa výberu investora	
2.17	Spálňa	14,16 m^2	podľa výberu investora	podľa výberu investora	podľa výberu investora	
Spolu: 3		23,39 m^2				

LEGENDA:

FÓLIOVÁ TECHNOLÓGIA SYSTÉMU VYHRIEVANIA NA ZÁKLADE DLHOVLNNÉHO INFRAČERVENÉHO ŽIARENIA

VNÚTORNÁ KLIMATIZAČNÁ JEDNOTKA, PRESNÝ TYP URČÍ ARCHITEKT

TP PRIESTOROVÝ REGULÁTOR TEPLOTY PRE PODLAHOVÉ VYKUROVANIE, napr. Heatflow

ELEKRICKÉ REBRÍKOVÉ VYKUROVACIE TELESO napr. KORALUX LINEAR MAX-ERA

POZNÁMKY:

- VŠETKY ROZMERY STAVEBNÝCH PRÁC KONTROLOVAŤ NA MIESTE STAVBY
- DOPORUČUJEM PREKÁBLOVANIE JEDNOTLIVÝCH TERMOSTATOV PODLAHOVÉHO VYKUROVANIA
- V PRÍPADE NEJASNOSTÍ VO VÝKRESOVEJ DOKUMENTÁCII KONTAKTOVAŤ ZODPOVEDNÉHO PROJEKTANTA S PRISLÚCHAJÚCOU REGULÁCIOU EŠTE PRED ZHOTOVENÍM OMIETOK
- DODÁVATEL STAVBY JE POVINNÝ REALIZOVAŤ VŠETKY PRÁCE V ZMYSLE PLATNÝCH STN EN S DODRŽANÍM TECHNOLOGICKÝCH A BEZPEČNOSTNÝCH POSTUPOV. ĎALEJ JE POVINNÝ REŠPEKTOVAŤ USTANOVENIA STN 730421 O PRÍSLUŠNÝCH ROZMEROVÝCH ODCHÝLKACH REALIZOVANÝCH KONŠTRUKCIÍ PROTI PROJEKTOVANÉMU STAVU. KAŽDÚ ODCHÝLKU OD PROJEKTU JE POTREBNÉ PREROKOVAŤ S GP.
- ±0,000 SA VZŤAHUJE K ÚROVNI FINÁLNEJ ÚPRAVY PODLAHY
- VÝBER VYKUROVACÍCH TELIES PODĽA INVESTORA

TABUĽKA REVÍZIÍ

ČÍSLO REVÍZIE	DÁTUM	POPIS ZMENY	VYPRACOVAL

0,000=256,300 m n. m.

AUTOR PROJEKTU:	Ing. arch. Ivor Mečiar, ArtD.
H.I.P.:	Ing. arch. Ivor Mečiar, ArtD.
ZODP. PROJEKTANT:	Ing. arch. Ivor Mečiar, ArtD.
VYPRACOVAL:	Bc. Viktor Labovský

GENERÁLNY PROJEKTANT:
Alla s.r.o.
Riazanská 70/683
831 02 Bratislava
tel.: +421 907 693 679
email: ateliar@alla.sk

INVESTOR: Haverčáková Viera r. Miznerová, Novohradská 1283/1, Bratislava

NÁZOV PROJEKTU: ZAHRADNA CHATKA ZLATÁ HORA

MIESTO STAVBY: Zlatá hora B, Stupava, p.č 5329/11

OBSAH VÝKRESU: **ÚK - Pôdorys 1. NP**

STAVEBNÝ OBJEKT: REKREAČNÁ ZÁHRADNÁ STAVBA

ID STAVBY:	STUPEŇ PD:	URČENIE STAVBY:	IDENTIFIK. : KÓD	ČLENENIE DOK.:	PROFESIE:	ČÍSLO VÝKRESU:	NÁZOV VÝKRESU:	REVÍZIA:

NÁZOV VÝKRESU V ELEKTRONICKEJ PODOBE:

PEČIATKA:

PARÉ:

ČÍSLO VÝKRESU: 2

DÁTUM: 05/2026

FORMÁT: 420 x 297mm

KÓD AKCIE:

MIERKA: 1:50